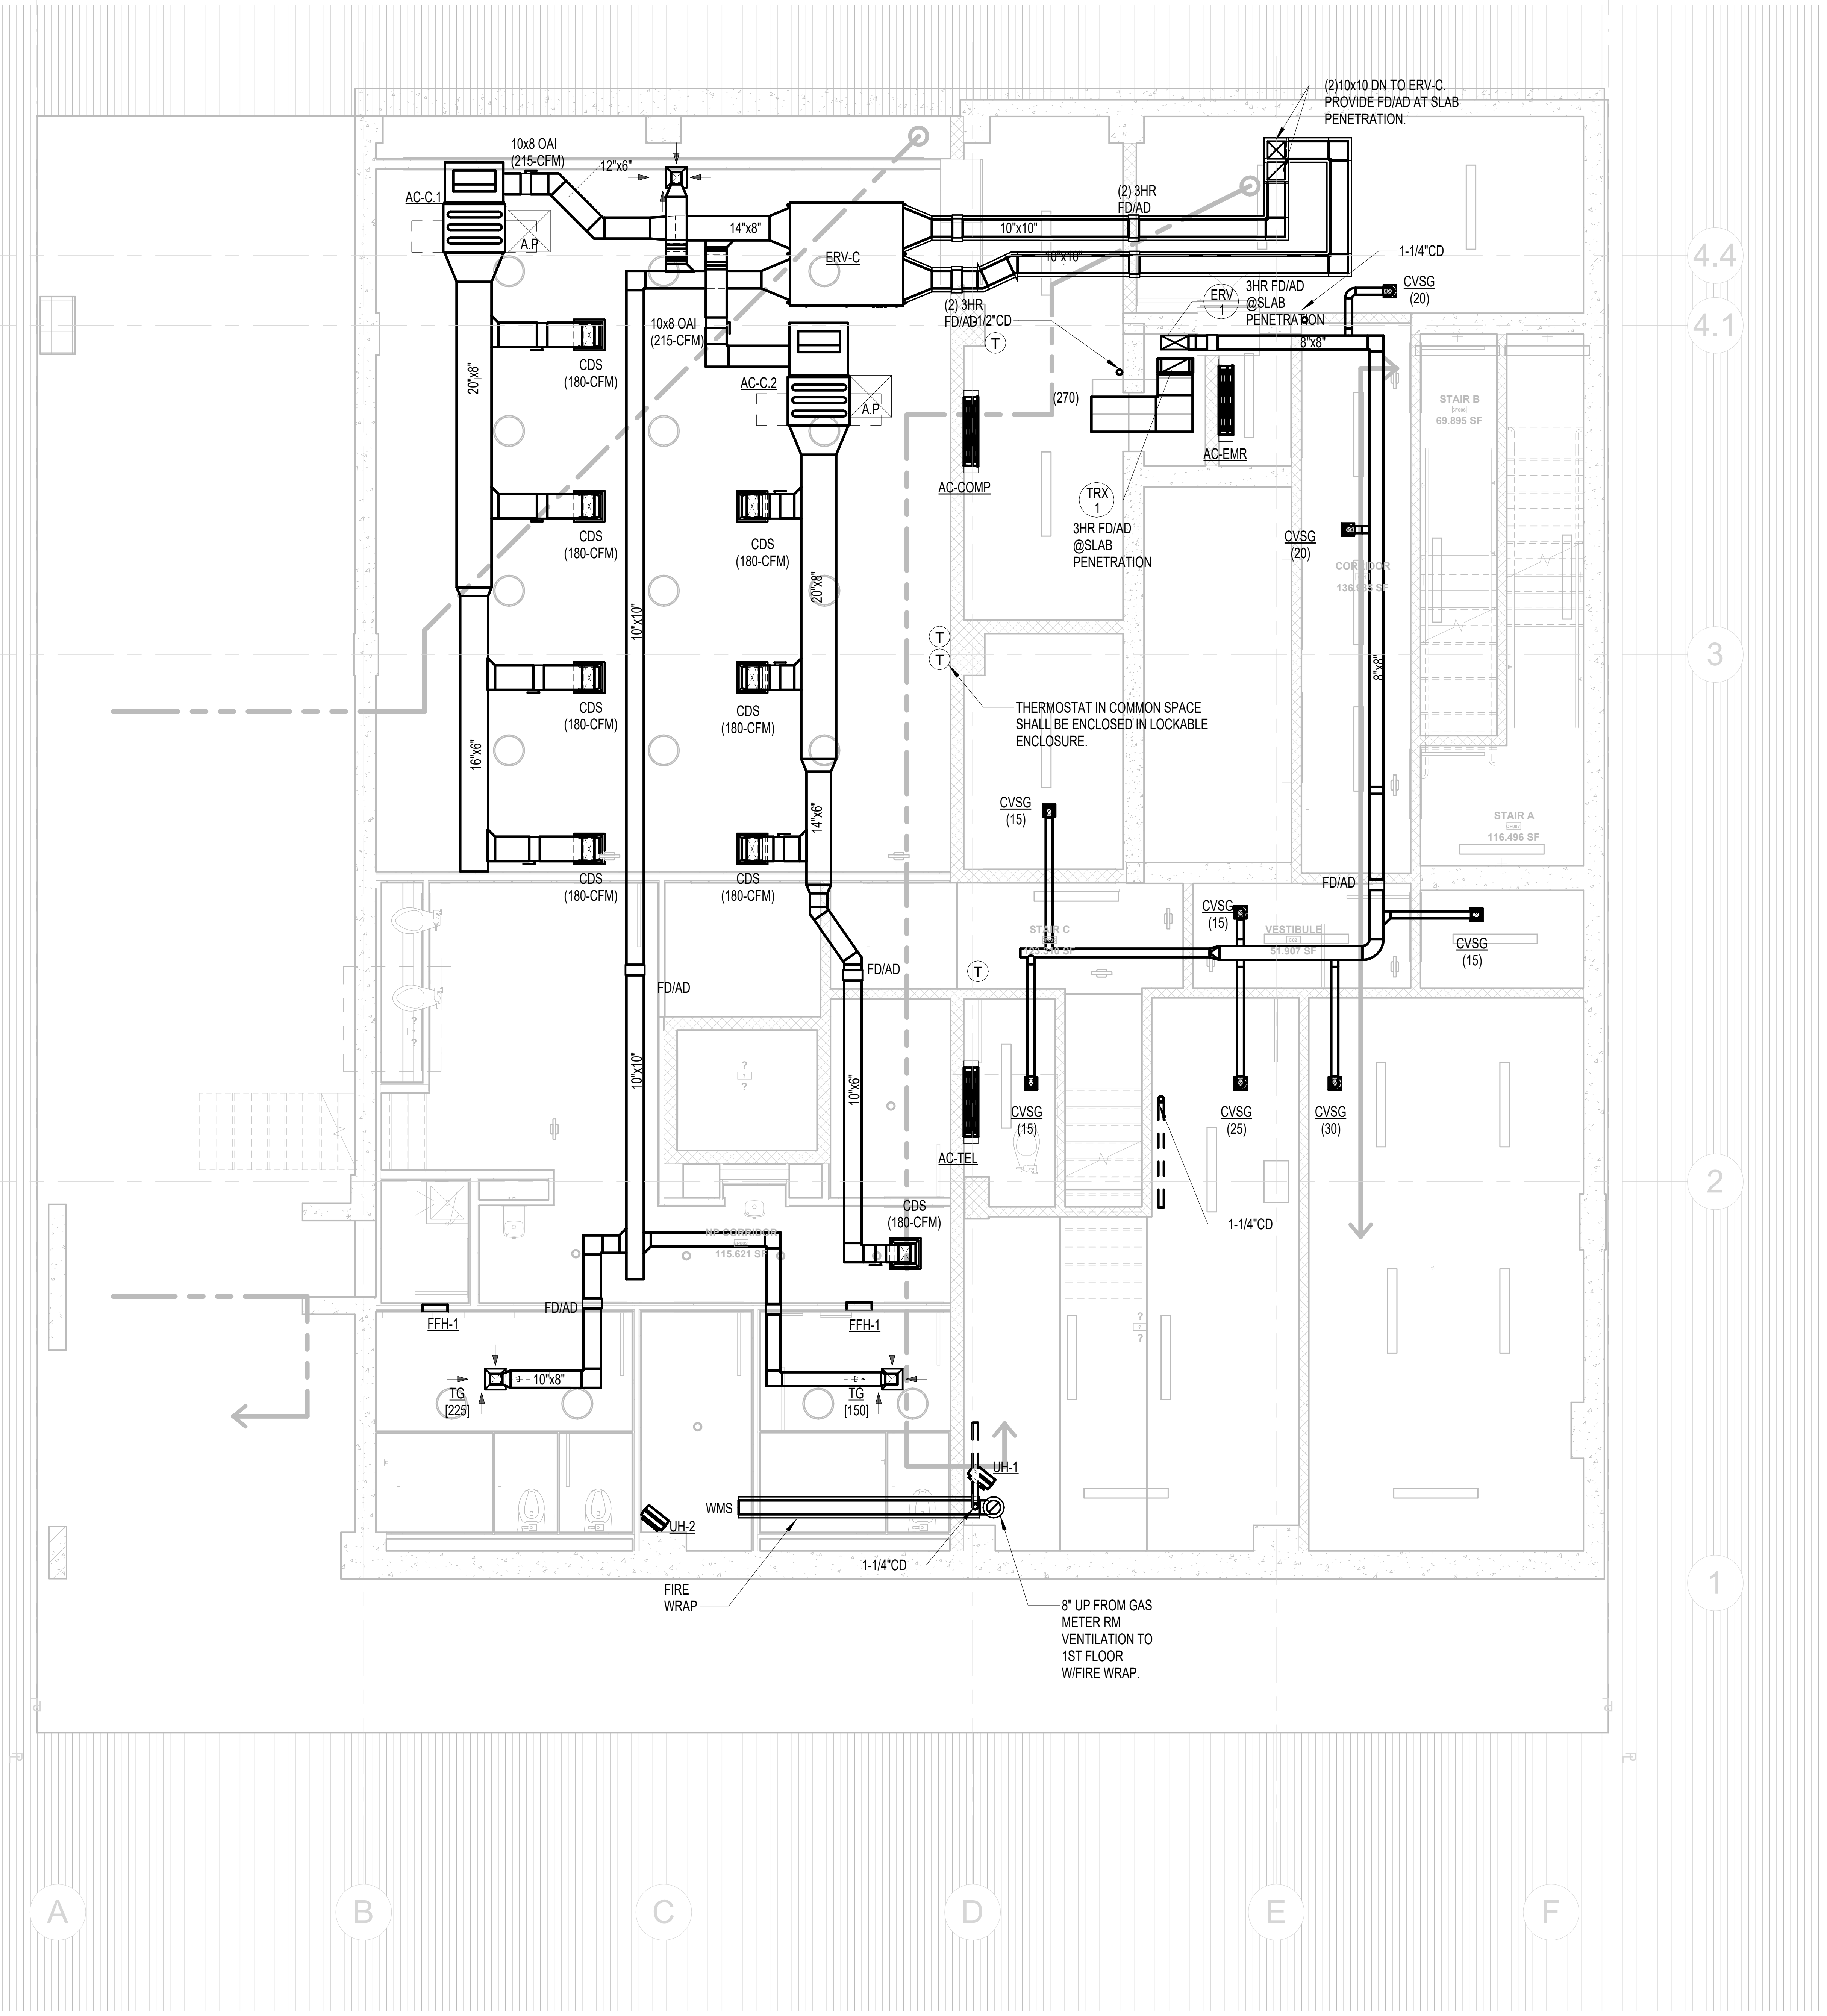

1

CELLAR LEVEL

SCALE: 3/16" = 1'-0"

DOB Application
number: #Q01372263-S4

INDIA HOME
A CENTER FOR SENIOR CARE

SITE 1 89TH AVE.

RKTB
Architects, P.C.
226 W 26th Street, 6th Flr.
New York, NY 10001
212.807.9500

FULCRUM
dream think build
226 W 26th Street, 6th Fl.
New York, NY
212.645.2317
www.fulcrumprop.com

India Home Procida Fulcro 178-36 Wexford Terrace Suite 2C Queens Village, NY 11432	Property Owner 917.288.7600 www.indiahome.org
McNamara Salvia Engineering 45 W 45th St. New York, NY 10036	Structural Engineer 212.246.9800 www.mcsal.com
Altera Engineering 1460 Broadway New York, NY 10036	Mechanical Engineer 212.330.7634 www.alteraeng.io
Pillori Associates, P.A. 71 Route 35 Laurence Harbor, NJ 08879	Geotechnical Engineer 732.335.0059 www.pilloriassociates.com
??? Landscape Architects ### Avenue Ave. City, ST #####	Landscape Architect ### ### #### www.????.com
??? Expeditor ### Avenue Ave. City, ST #####	Code Consultant ### ### #### www.????.com

Date	No.	Description
07/31/2026	3	PRICING SET
05/18/2026	2	ISSUED FOR DD
03/30/2026	1	ISSUED FOR DOB FILING

NOT FOR CONSTRUCTION

Approval:

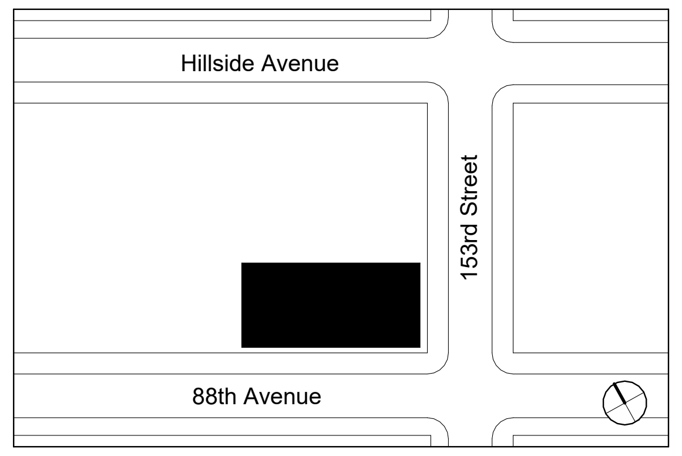

KEY PLAN

Project Address:

170-11 89th Avenue
Jamaica, Queens

Drawing Title:

MECHANICAL CELLAR
FLOOR

Borough:	Block Number:
Zoning Map:	Lot Number:
Zoning District:	BIN Number:
Drawn By: DM	Checked By: DM
Signature & Seal: STATE OF NEW YORK DMITRIY MOROZOV 086597 LICENSED PROFESSIONAL ENGINEER	Project Number: 2516
	Date:
	Scale: 3/16" = 1'-0"
	Drawing Number: M-100.00
	Drawing:

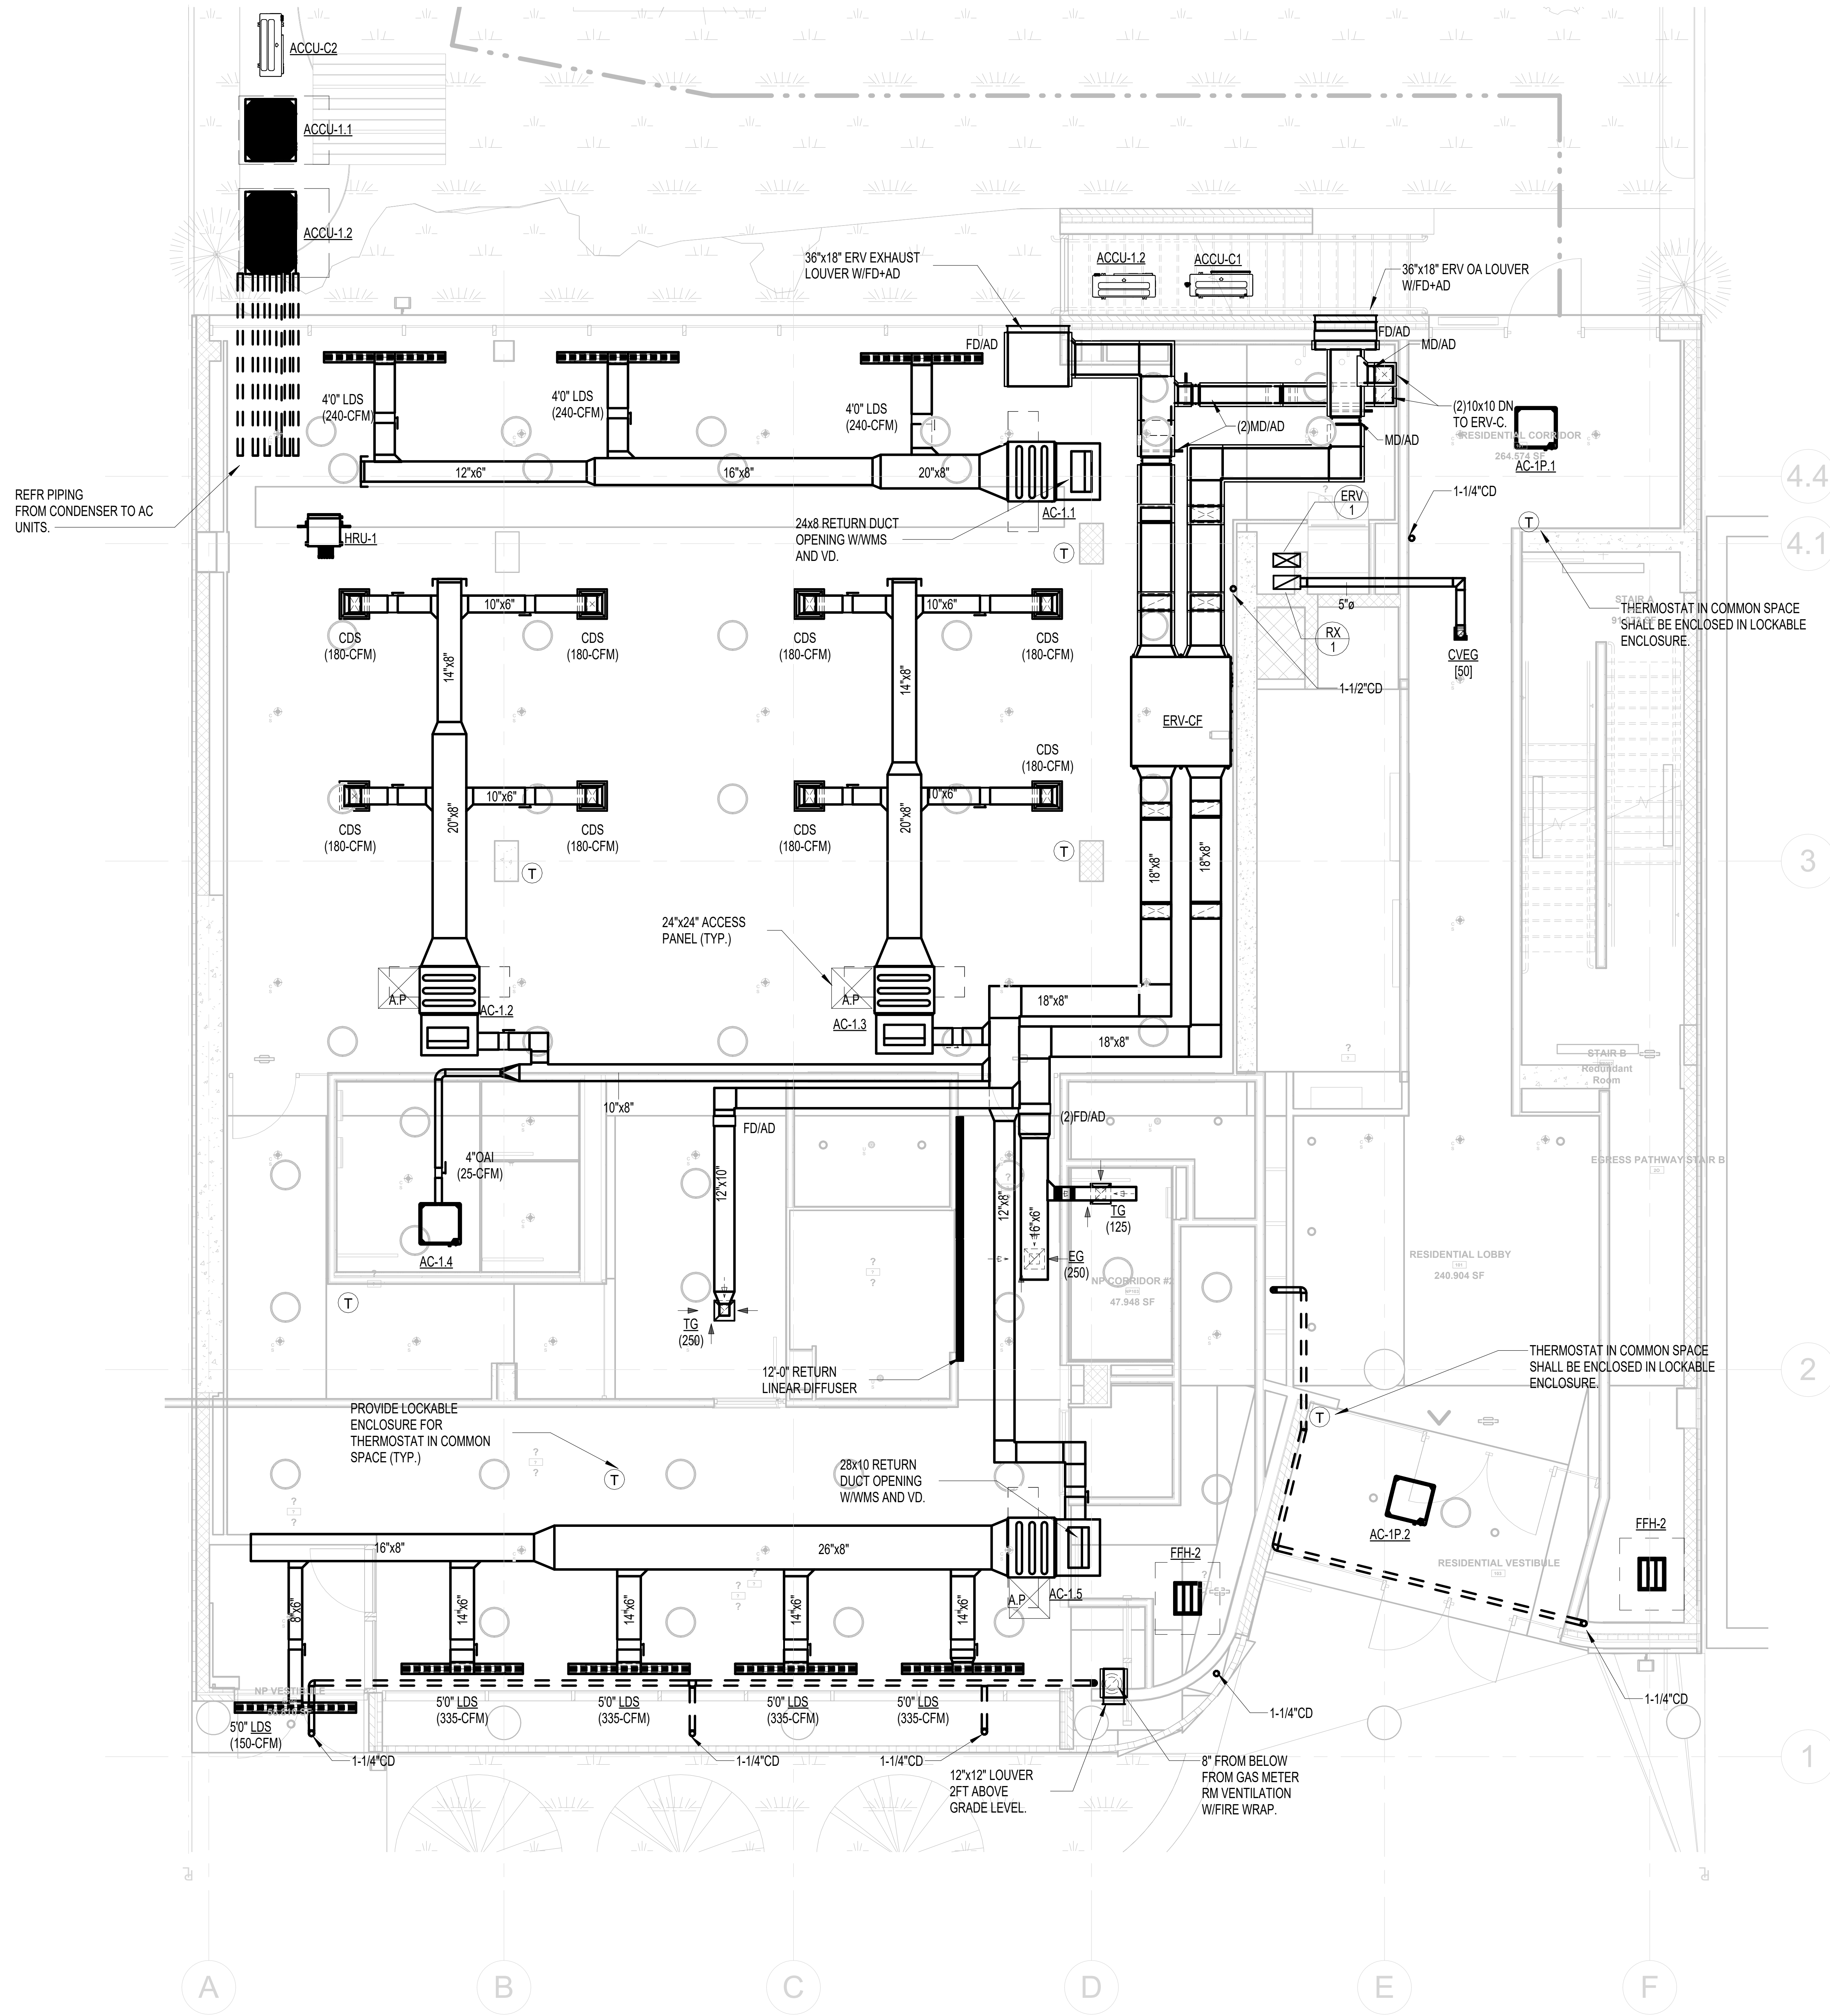

1 1ST FLOOR PLAN

SCALE: 3/16" = 1'-0"

DOB Application
number: #Q01372263-S4

INDIA HOME
A CENTER FOR SENIOR CARE

SITE 1 89TH AVE.

RKTB
Architects, P.C.

226 W 26th Street, 6th Flr.
New York, NY 10001
212.807.9500

FULCRUM
dream think build

226 W 26th Street, 6th Fl.
New York, NY
212.645.2317
www.fulcrumprop.com

India Home Procida Fulcro 178-36 Wexford Terrace Suite 2C Queens Village, NY 11432	Property Owner 917.288.7600 www.indiahome.org
McNamara Salvia Engineering 45 W 45th St. New York, NY 10036	Structural Engineer 212.246.9800 www.mcsal.com
Altera Engineering 1460 Broadway New York, NY 10036	Mechanical Engineer 212.330.7634 www.alteraeng.io
Pillori Associates, P.A. 71 Route 35 Laurence Harbor, NJ 08879	Geotechnical Engineer 732.335.0059 www.pilloriassociates.com
??? Landscape Architects ### Avenue Ave. City, ST #####	Landscape Architect ### ### #### www.????.com
??? Expeditor ### Avenue Ave. City, ST #####	Code Consultant ### ### #### www.????.com

Date	No.	Description
07/31/2026	3	PRICING SET
05/18/2026	2	ISSUED FOR DD
03/30/2026	1	ISSUED FOR DOB FILING

NOT FOR CONSTRUCTION

Approval:

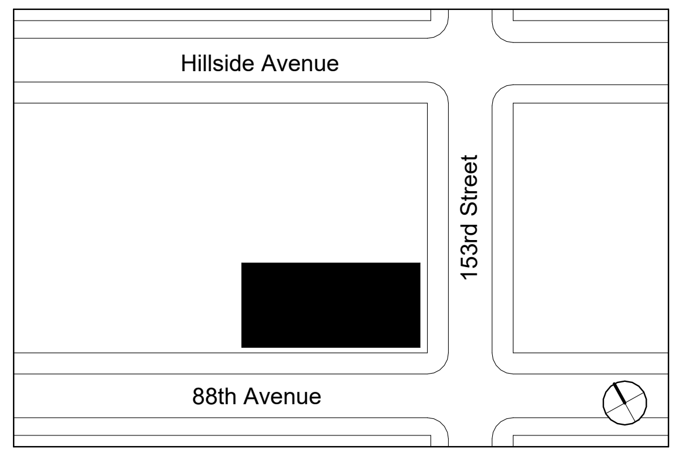

KEY PLAN

Project Address:

170-11 89th Avenue
Jamaica, Queens

Drawing Title:

MECHANICAL 1ST
FLOOR PLAN

Borough:	Block Number:
Zoning Map:	Lot Number:
Zoning District:	BIN Number:
Drawn By: DM	Checked By: DM
Signature & Seal: STATE OF NEW YORK · DMITRIY MOROZOV · 086597 · LICENSED PROFESSIONAL ENGINEER	Project Number: 2516
	Date:
	Scale: 3/16" = 1'-0"
	Drawing Number: M-101.00
	Drawing:

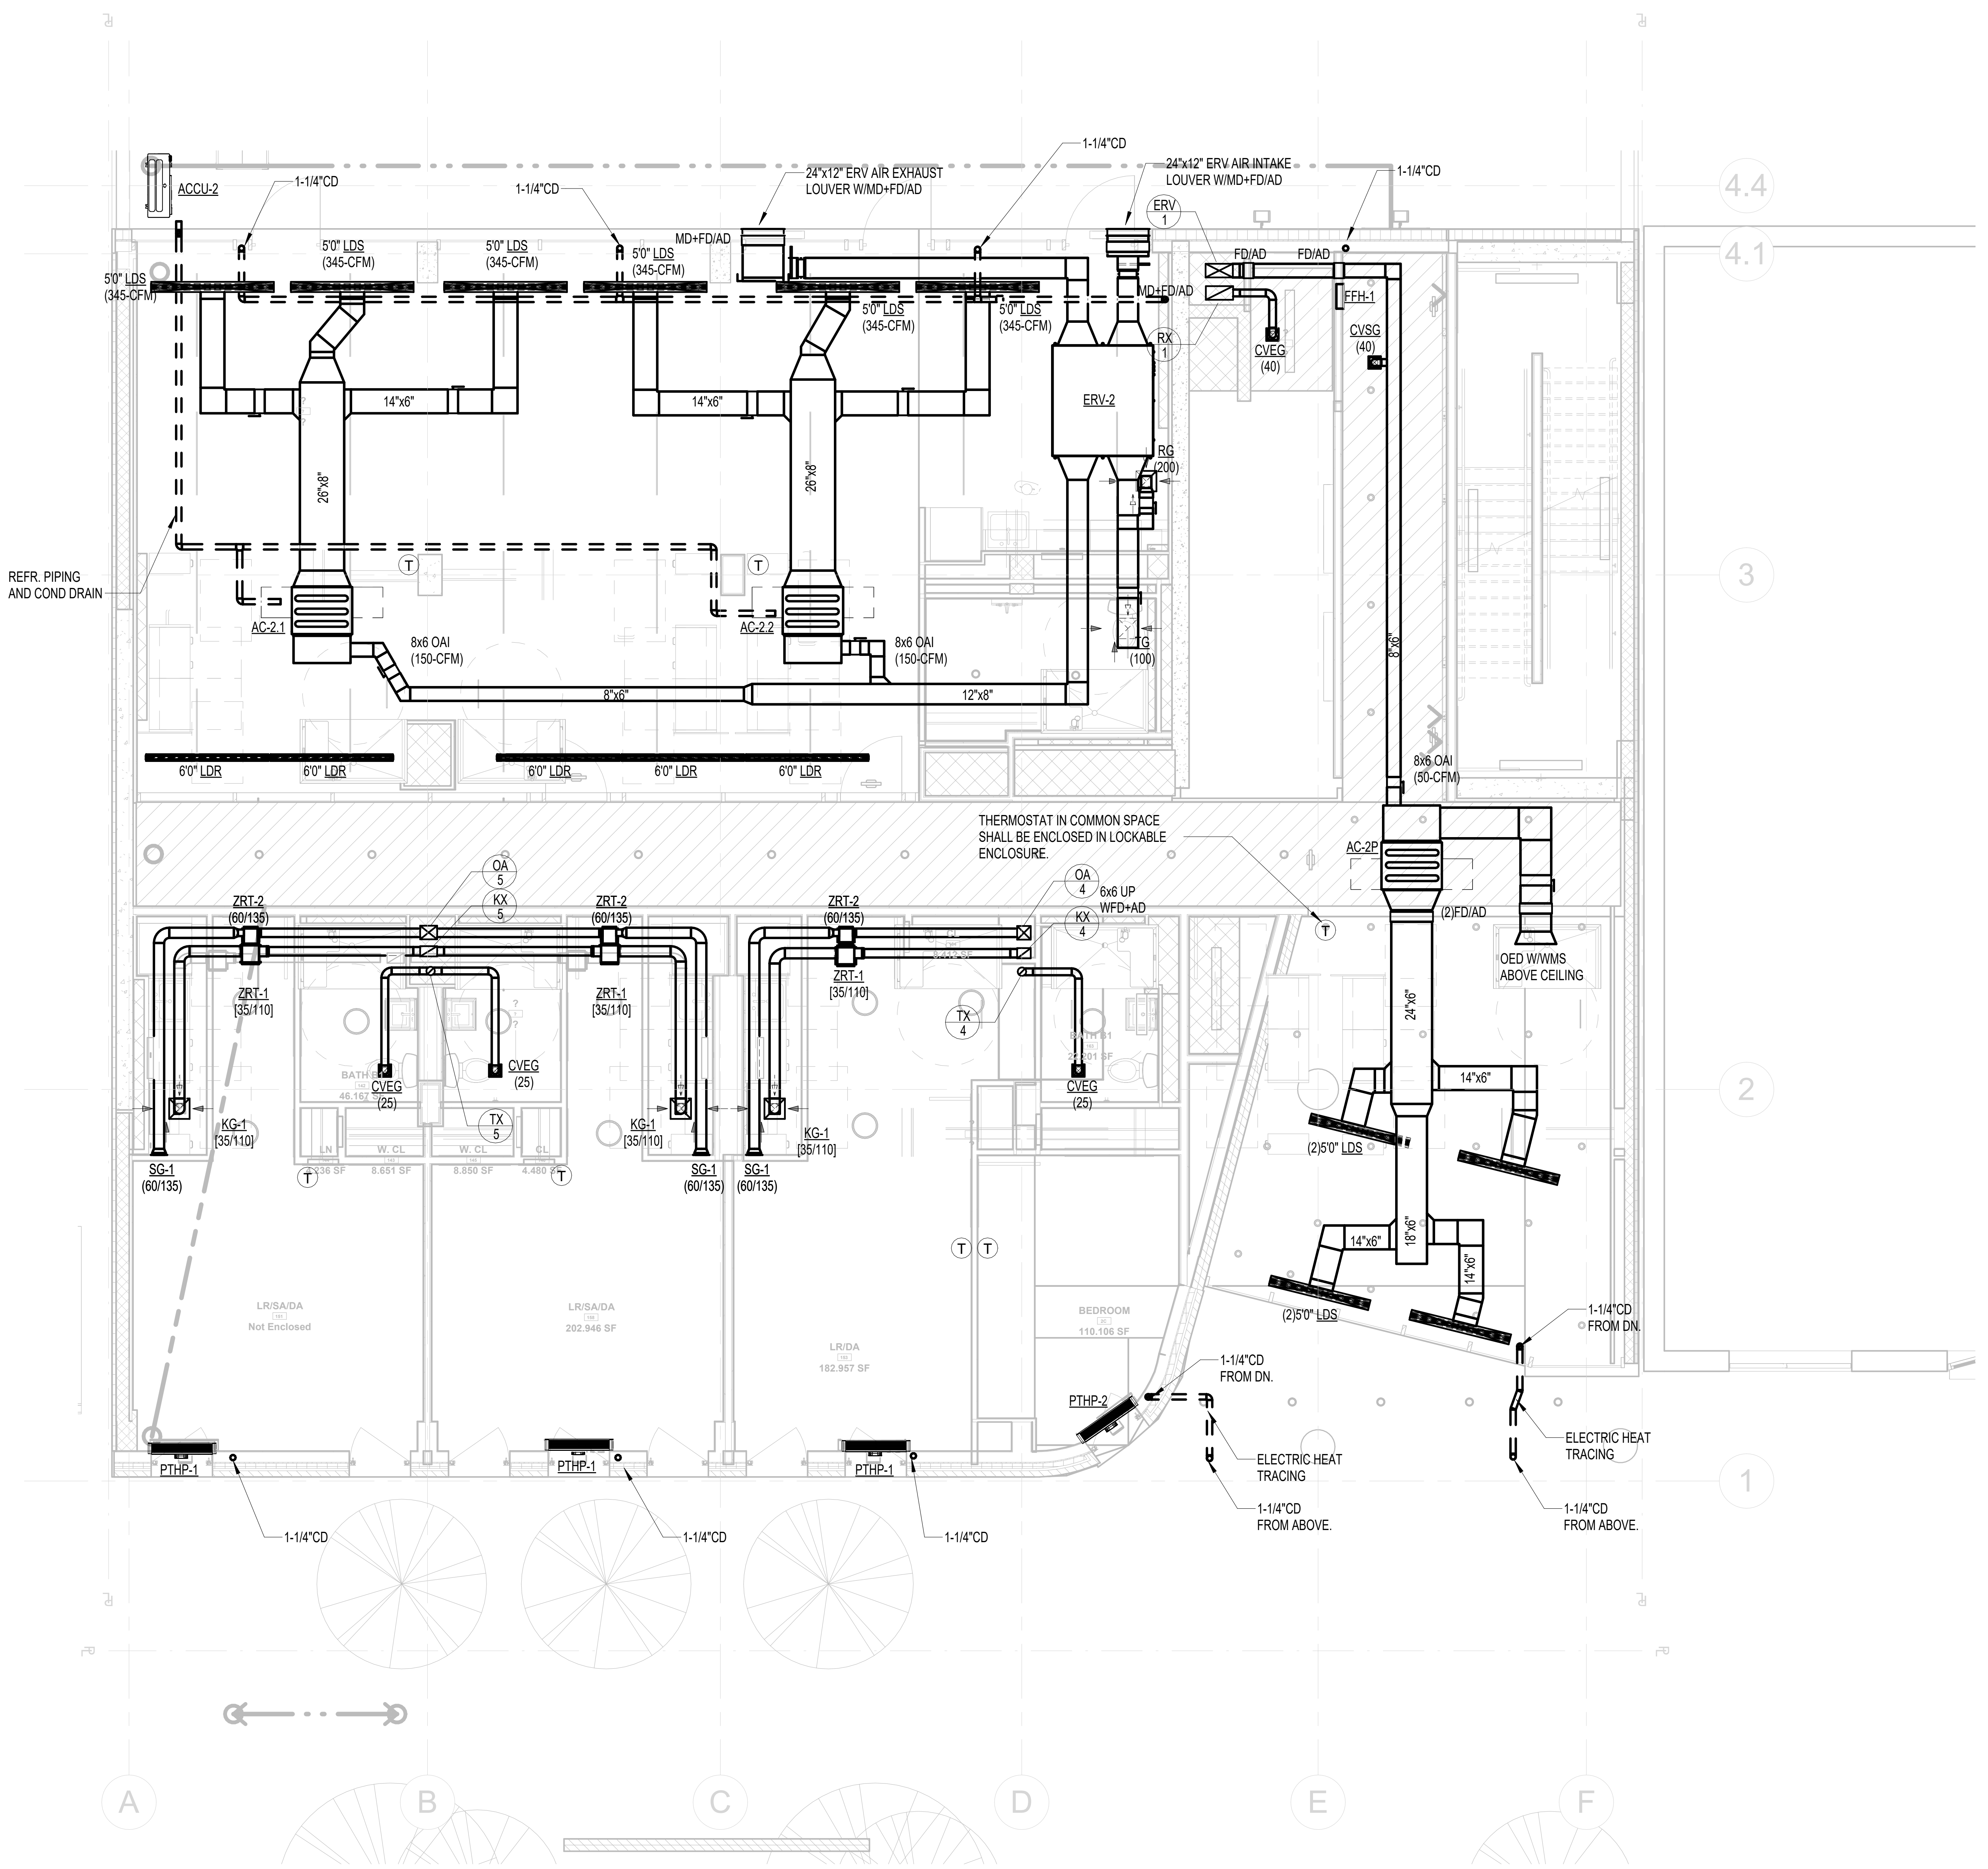

1 2ND FLOOR PLAN

SCALE: 3/16" = 1'-0"

DOB Application
number: #Q01372263-S4

INDIA HOME
A CENTER FOR SENIOR CARE

SITE 1 89TH AVE.

RKTB
Architects, P.C.
226 W 26th Street, 6th Flr.
New York, NY 10001
212.807.9500

FULCRUM
dream think build
226 W 26th Street, 6th Fl.
New York, NY
212.645.2317
www.fulcrumprop.com

India Home Procida Fulcro 178-36 Wexford Terrace Suite 2C Queens Village, NY 11432	Property Owner 917.288.7600 www.indiahome.org
McNamara Salvia Engineering 45 W 45th St. New York, NY 10036	Structural Engineer 212.246.9800 www.mcsal.com
Altera Engineering 1460 Broadway New York, NY 10036	Mechanical Engineer 212.330.7634 www.alteraeng.io
Pillori Associates, P.A. 71 Route 35 Laurence Harbor, NJ 08879	Geotechnical Engineer 732.335.0059 www.pilloriassociates.com
??? Landscape Architects ### Avenue Ave. City, ST #####	Landscape Architect ### ### #### www.????.com
??? Expeditor ### Avenue Ave. City, ST #####	Code Consultant ### ### #### www.????.com

Date	No.	Description
07/31/2026	3	PRICING SET
05/18/2026	2	ISSUED FOR DD
03/30/2026	1	ISSUED FOR DOB FILING

NOT FOR CONSTRUCTION

Approval:

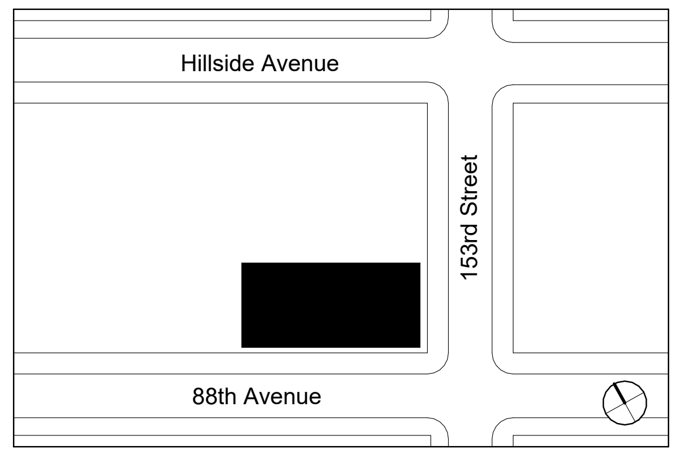

KEY PLAN

Project Address:

170-11 89th Avenue
Jamaica, Queens

Drawing Title:

MECHANICAL 2ND FLOOR PLAN

Borough:	Block Number:
Zoning Map:	Lot Number:
Zoning District:	BIN Number:
Drawn By: DM	Checked By: DM
Signature & Seal: DMITRIY MOROZOV 086597	Project Number: 2516
	Date:
	Scale: 3/16" = 1'-0"
	Drawing Number: M-102.00
	Drawing:

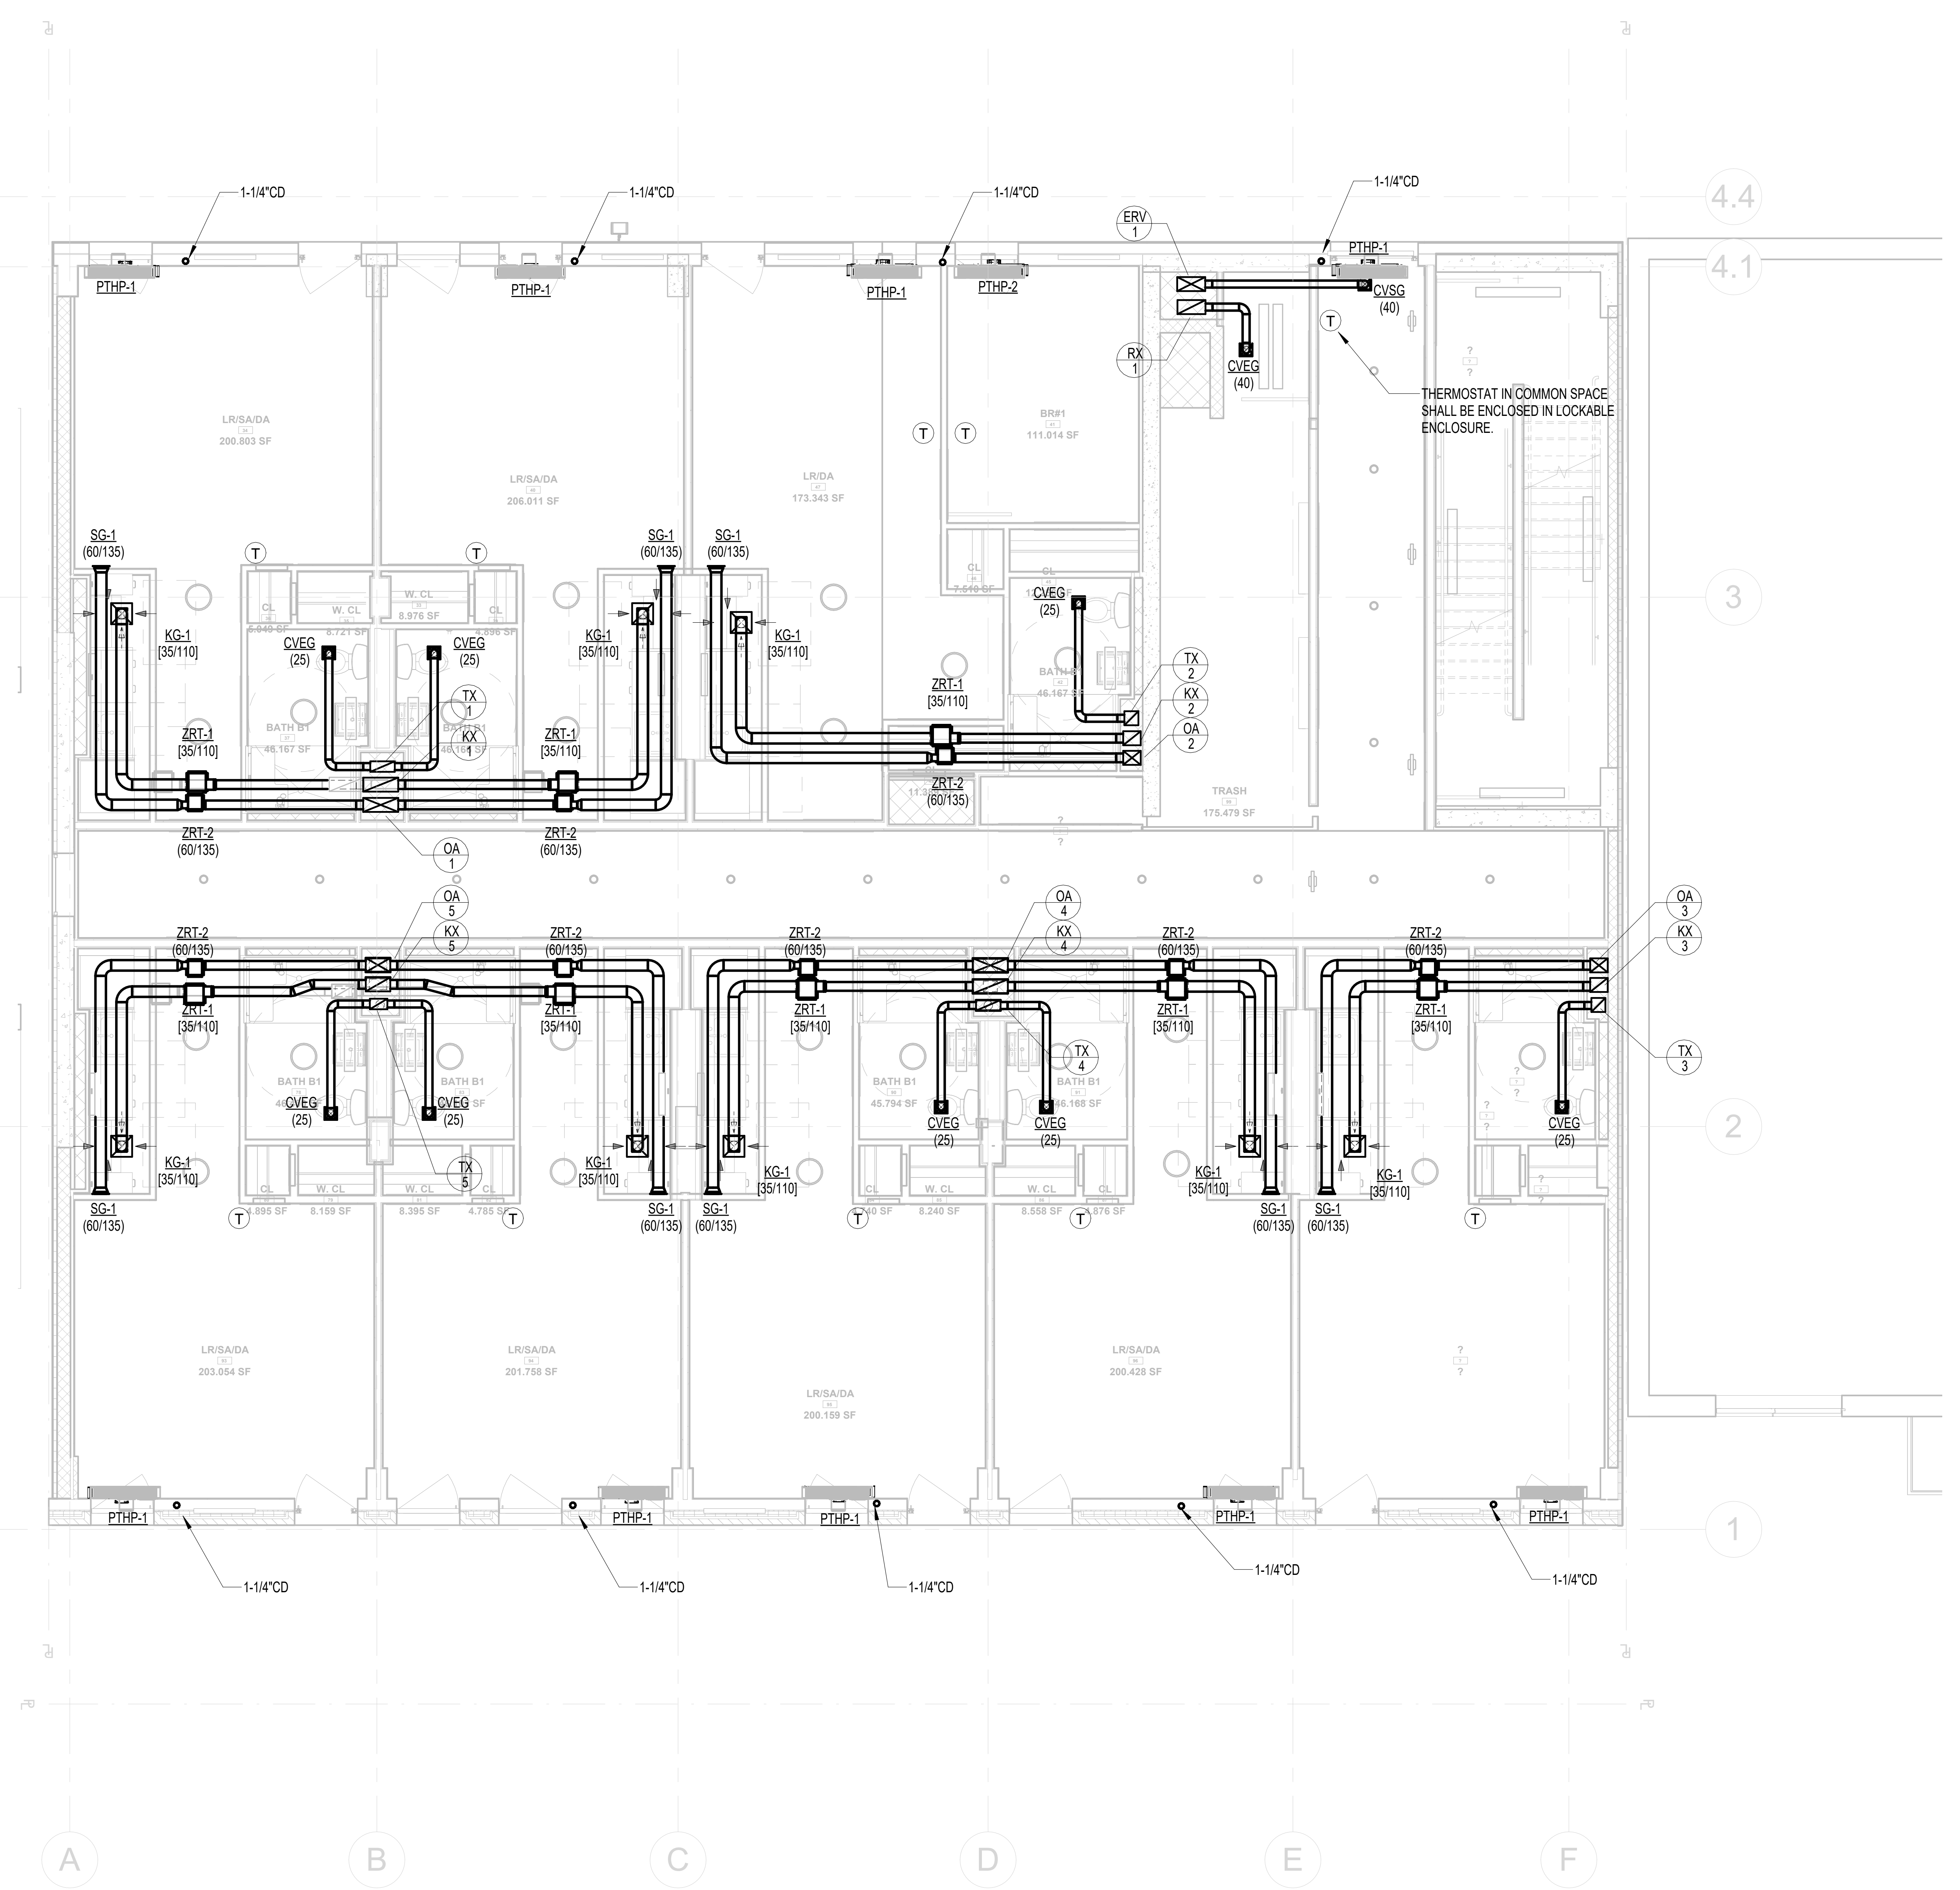

THERMOSTAT IN COMMON SPACE SHALL BE ENCLOSED IN LOCKABLE ENCLOSURE.

1 **3RD THRU 5TH FLOOR PLAN**
SCALE: 3/16" = 1'-0"

DOB Application
number: #Q01372263-S4

INDIA HOME
A CENTER FOR SENIOR CARE

SITE 1 89TH AVE.

RKTB
Architects, P.C.
226 W 26th Street, 6th Flr.
New York, NY 10001
212.807.9500

FULCRUM
dream think build
226 W 26th Street, 6th Fl.
New York, NY
212.645.2317
www.fulcrumprop.com

India Home Procida Fulcro 178-36 Wexford Terrace Suite 2C Queens Village, NY 11432	Property Owner 917.288.7600 www.indiahome.org
McNamara Salvia Engineering 45 W 45th St. New York, NY 10036	Structural Engineer 212.246.9800 www.mcsal.com
Altera Engineering 1460 Broadway New York, NY 10036	Mechanical Engineer 212.330.7634 www.alteraeng.io
Pillori Associates, P.A. 71 Route 35 Laurence Harbor, NJ 08879	Geotechnical Engineer 732.335.0059 www.pilloriassociates.com
??? Landscape Architects ### Avenue Ave. City, ST #####	Landscape Architect ### ### #### www.????.com
??? Expeditor ### Avenue Ave. City, ST #####	Code Consultant ### ### #### www.????.com

Date	No.	Description
07/31/2026	3	PRICING SET
05/18/2026	2	ISSUED FOR DD
03/30/2026	1	ISSUED FOR DOB FILING

NOT FOR CONSTRUCTION

Approval:

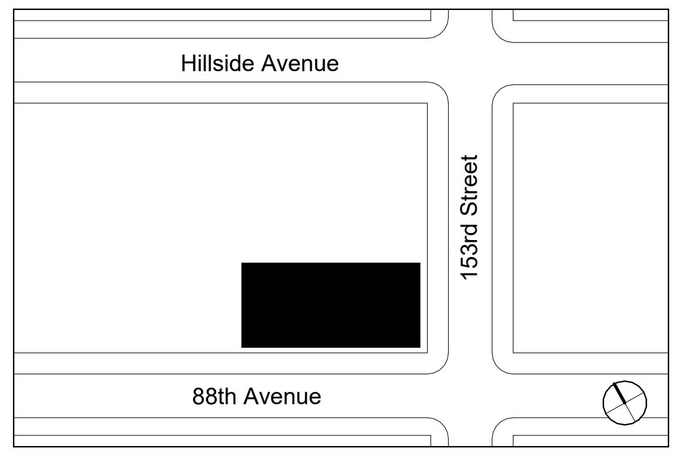

KEY PLAN

Project Address:

170-11 89th Avenue
Jamaica, Queens

Drawing Title:

MECHANICAL 3RD
THRU 5TH FLOOR
PLAN

Borough:	Block Number:
Zoning Map:	Lot Number:
Zoning District:	BIN Number:
Drawn By: DM	Checked By: DM
Signature & Seal: DMITRIY MOROZOV 086597	Project Number: 2516
	Date:
	Scale: 3/16" = 1'-0"
	Drawing Number: M-103.00
	Drawing:

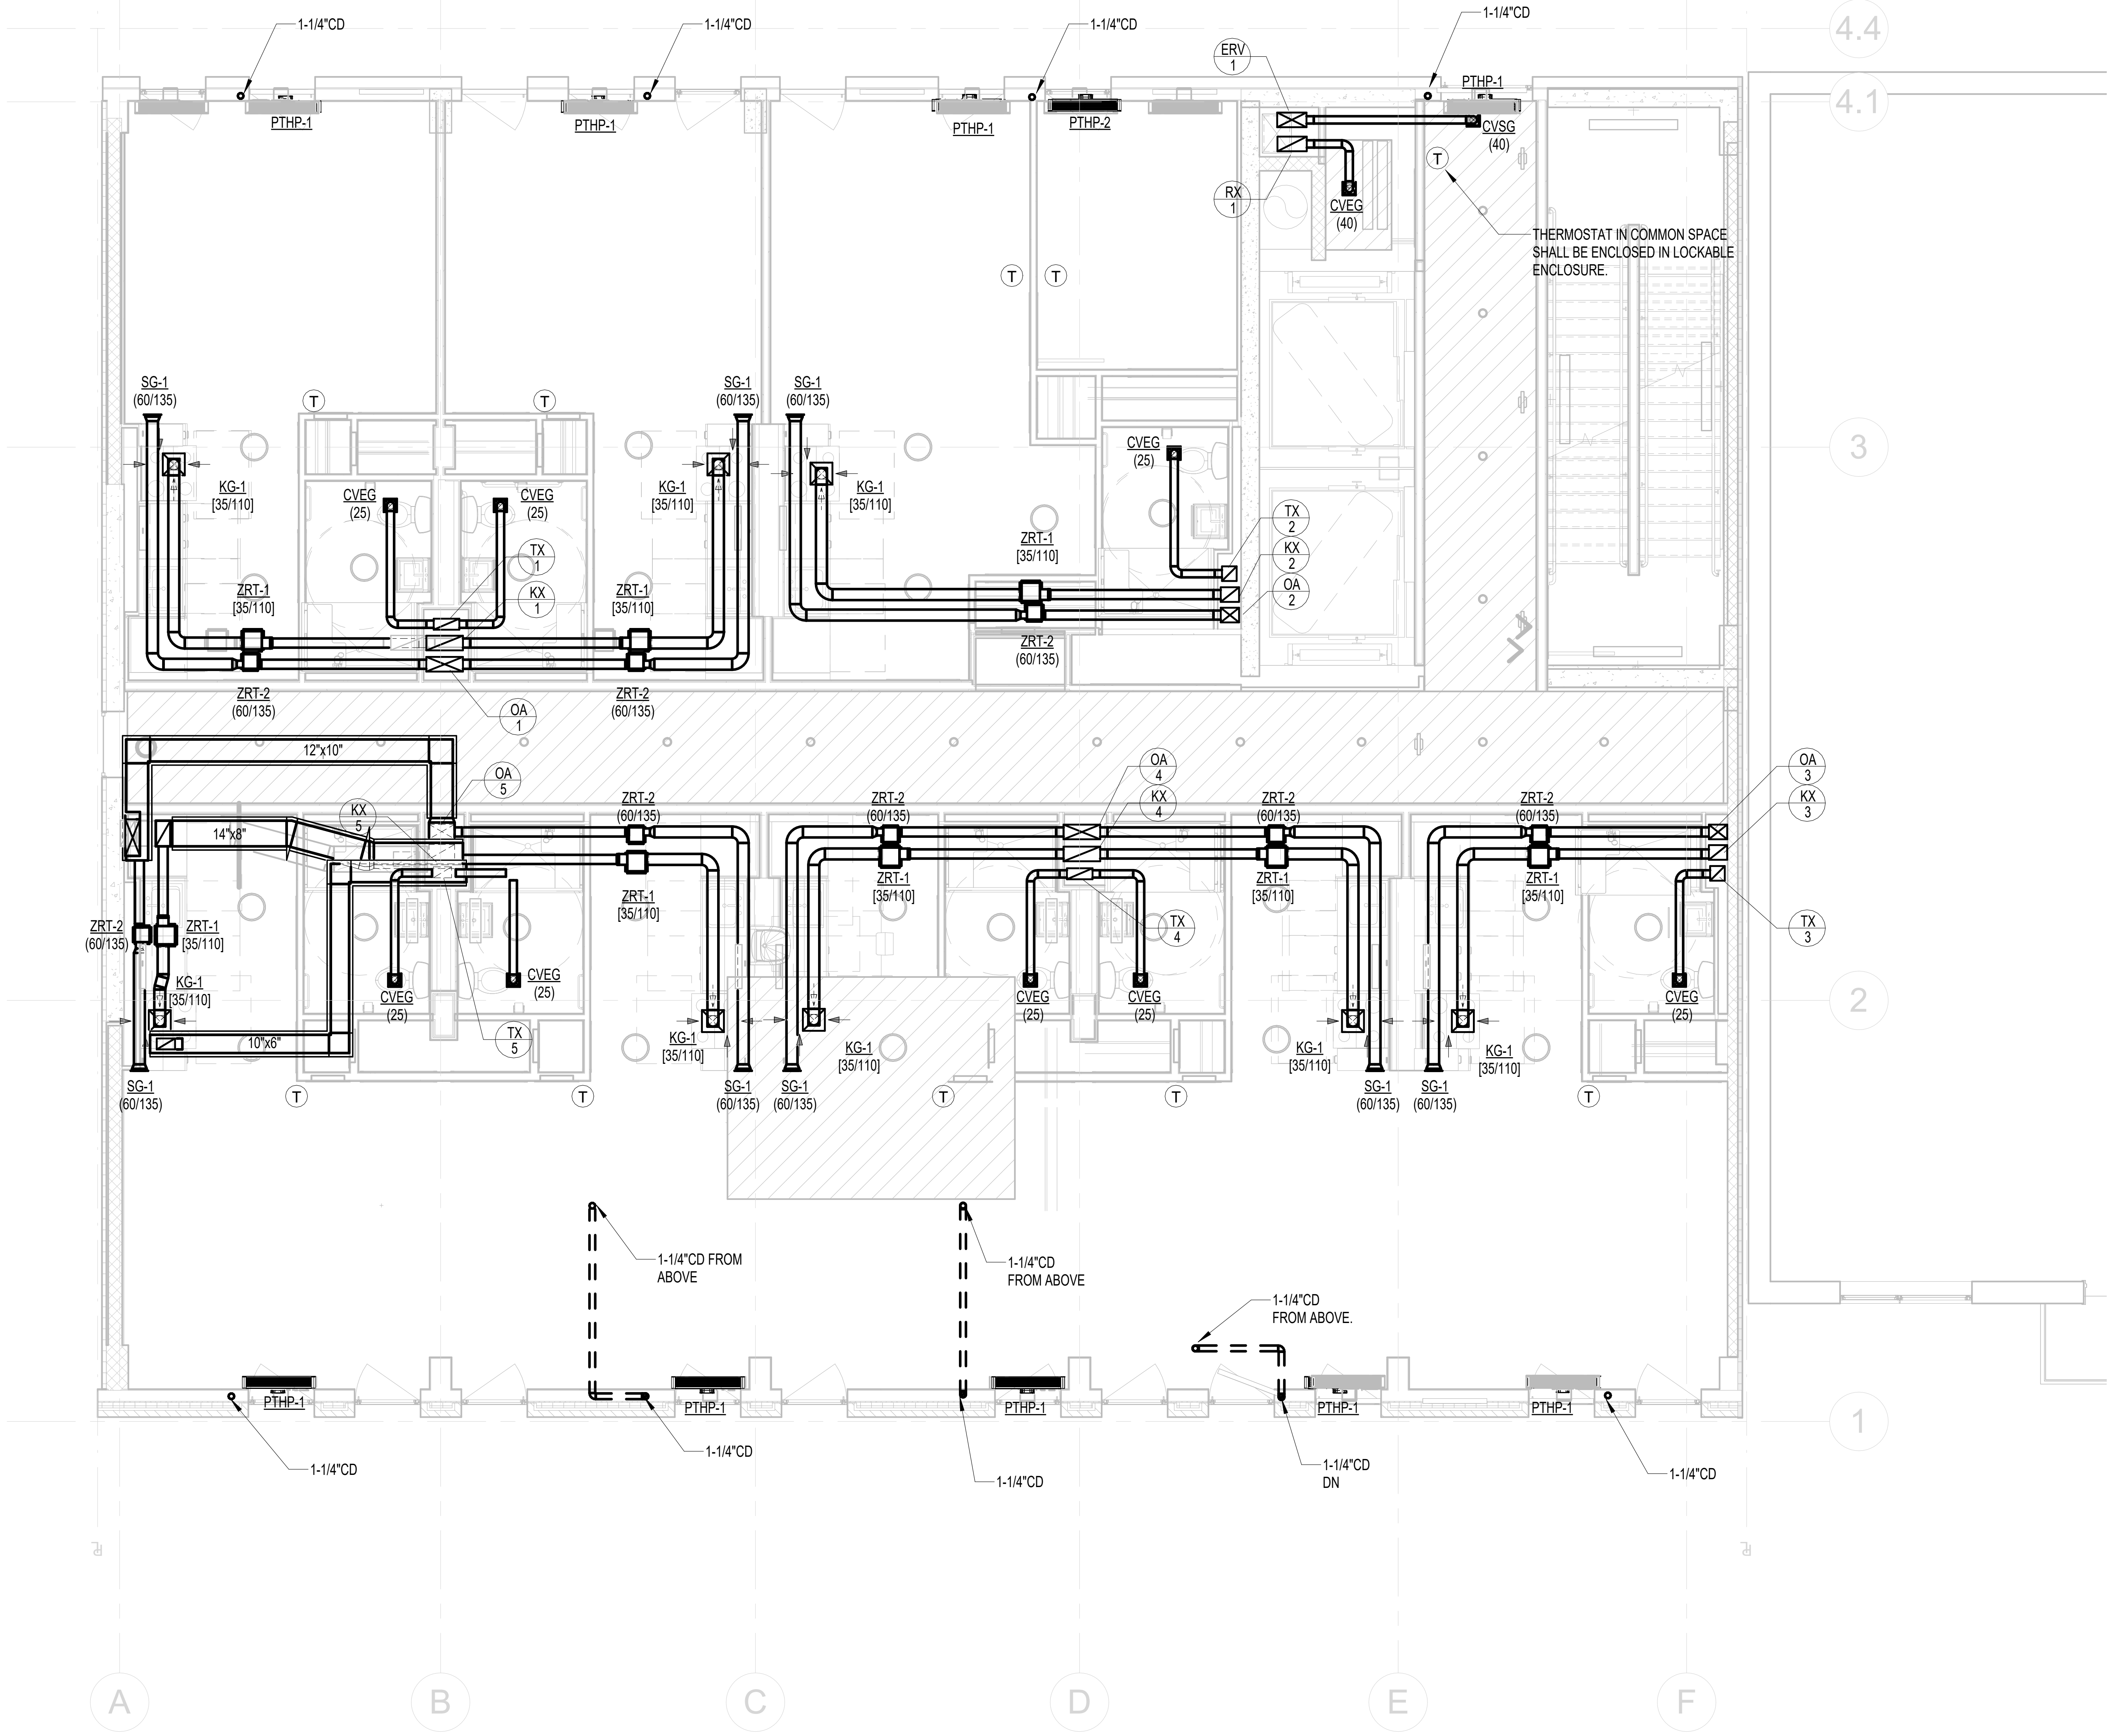

1 **6TH FLOOR PLAN**

SCALE: 3/16" = 1'-0"

DOB Application
number: #Q01372263-S4

31-Jul-26 7:49:30 PM

INDIA HOME
A CENTER FOR SENIOR CARE

SITE 1 89TH AVE.

RKTB
Architects, P.C.

226 W 26th Street, 6th Flr.
New York, NY 10001
212.807.9500

FULCRUM
dream think build

226 W 26th Street, 6th Fl.
New York, NY
212.645.2317
www.fulcrumprop.com

India Home Procida Fulcro 178-36 Wexford Terrace Suite 2C Queens Village, NY 11432	Property Owner 917.288.7600 www.indiahome.org
McNamara Salvia Engineering 45 W 45th St. New York, NY 10036	Structural Engineer 212.246.9800 www.mcsal.com
Altera Engineering 1460 Broadway New York, NY 10036	Mechanical Engineer 212.330.7634 www.alteraeng.io
Pillori Associates, P.A. 71 Route 35 Laurence Harbor, NJ 08879	Geotechnical Engineer 732.335.0059 www.pilloriassociates.com
??? Landscape Architects ### Avenue Ave. City, ST #####	Landscape Architect ### ### #### www.????.com
??? Expeditor ### Avenue Ave. City, ST #####	Code Consultant ### ### #### www.????.com

Date	No.	Description
07/31/2026	3	PRICING SET
05/18/2026	2	ISSUED FOR DD
03/30/2026	1	ISSUED FOR DOB FILING

NOT FOR CONSTRUCTION

Approval:

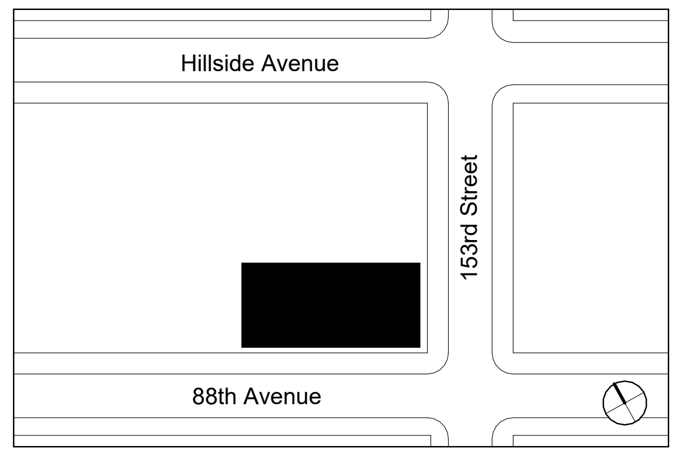

KEY PLAN

Project Address:

170-11 89th Avenue
Jamaica, Queens

Drawing Title:

MECHANICAL 6TH
FLOOR PLAN

Borough:	Block Number:
Zoning Map:	Lot Number:
Zoning District:	BIN Number:
Drawn By: DM	Checked By: DM
Signature & Seal: DMITRIY MOROZOV 086597	Project Number: 2516
	Date:
	Scale: 3/16" = 1'-0"
	Drawing Number: M-104.00
	Drawing:

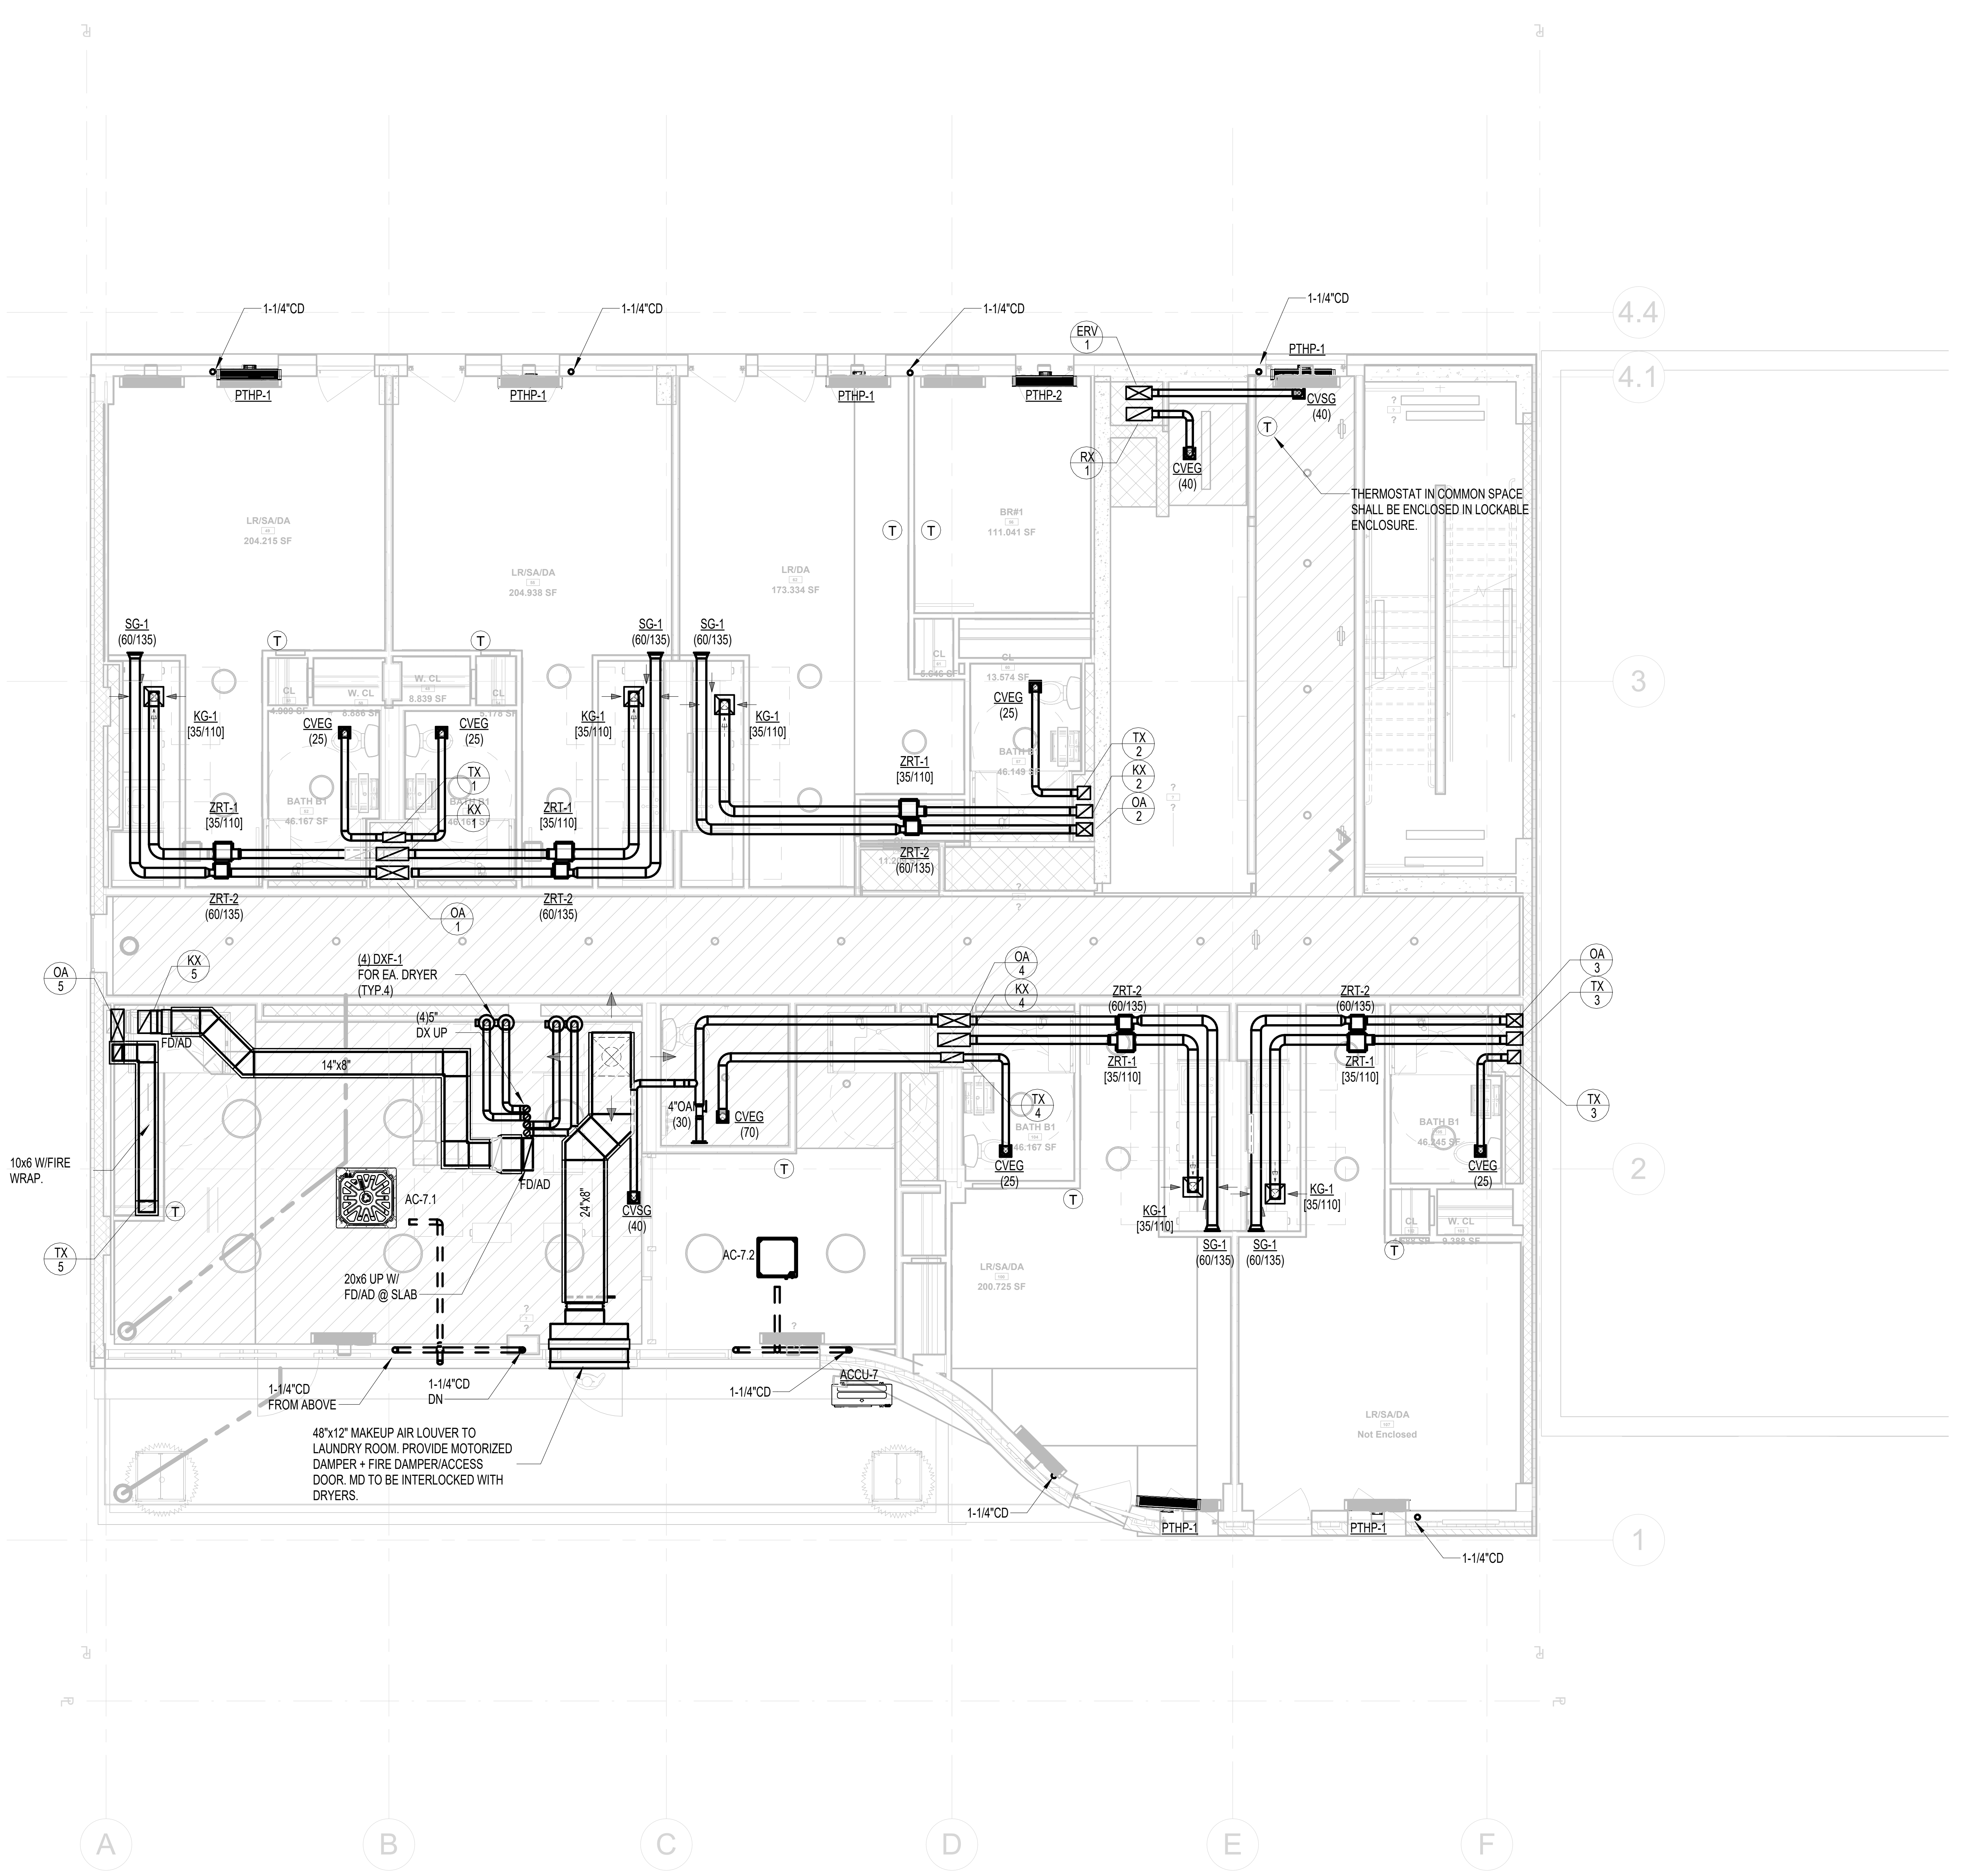

1 **7TH FLOOR PLAN**
SCALE: 3/16" = 1'-0"

DOB Application
number: #Q01372263-S4

INDIA HOME
A CENTER FOR SENIOR CARE

SITE 1 89TH AVE.

RKTB
Architects, P.C.

226 W 26th Street, 6th Flr.
New York, NY 10001
212.807.9500

FULCRUM
dream think build

226 W 26th Street, 6th Fl.
New York, NY
212.645.2317
www.fulcrumprop.com

India Home Procida Fulcro 178-36 Wexford Terrace Suite 2C Queens Village, NY 11432	Property Owner 917.288.7600 www.indiahome.org
McNamara Salvia Engineering 45 W 45th St. New York, NY 10036	Structural Engineer 212.246.9800 www.mcsal.com
Altera Engineering 1460 Broadway New York, NY 10036	Mechanical Engineer 212.330.7634 www.alteraeng.io
Pillori Associates, P.A. 71 Route 35 Laurence Harbor, NJ 08879	Geotechnical Engineer 732.335.0059 www.pilloriassociates.com
??? Landscape Architects ### Avenue Ave. City, ST #####	Landscape Architect ### ### #### www.????.com
??? Expeditor ### Avenue Ave. City, ST #####	Code Consultant ### ### #### www.????.com

Date	No.	Description
07/31/2026	3	PRICING SET
05/18/2026	2	ISSUED FOR DD
03/30/2026	1	ISSUED FOR DOB FILING

NOT FOR CONSTRUCTION

Approval:

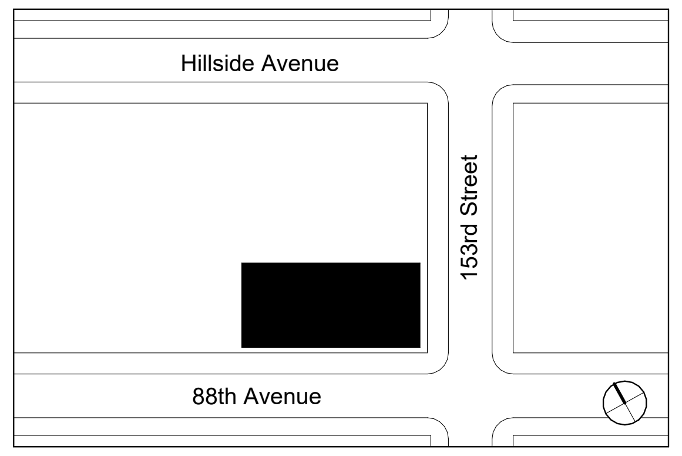

KEY PLAN

Project Address:
170-11 89th Avenue
Jamaica, Queens

Drawing Title:
MECHANICAL 7TH
FLOOR PLAN

Borough:	Block Number:
Zoning Map:	Lot Number:
Zoning District:	BIN Number:
Drawn By: DM	Checked By: DM
Signature & Seal: STATE OF NEW YORK DMITRIY MOROZOV 086597 LICENSED PROFESSIONAL ENGINEER	Project Number: 2516
	Date:
	Scale: 3/16" = 1'-0"
	Drawing Number: M-105.00
	Drawing:

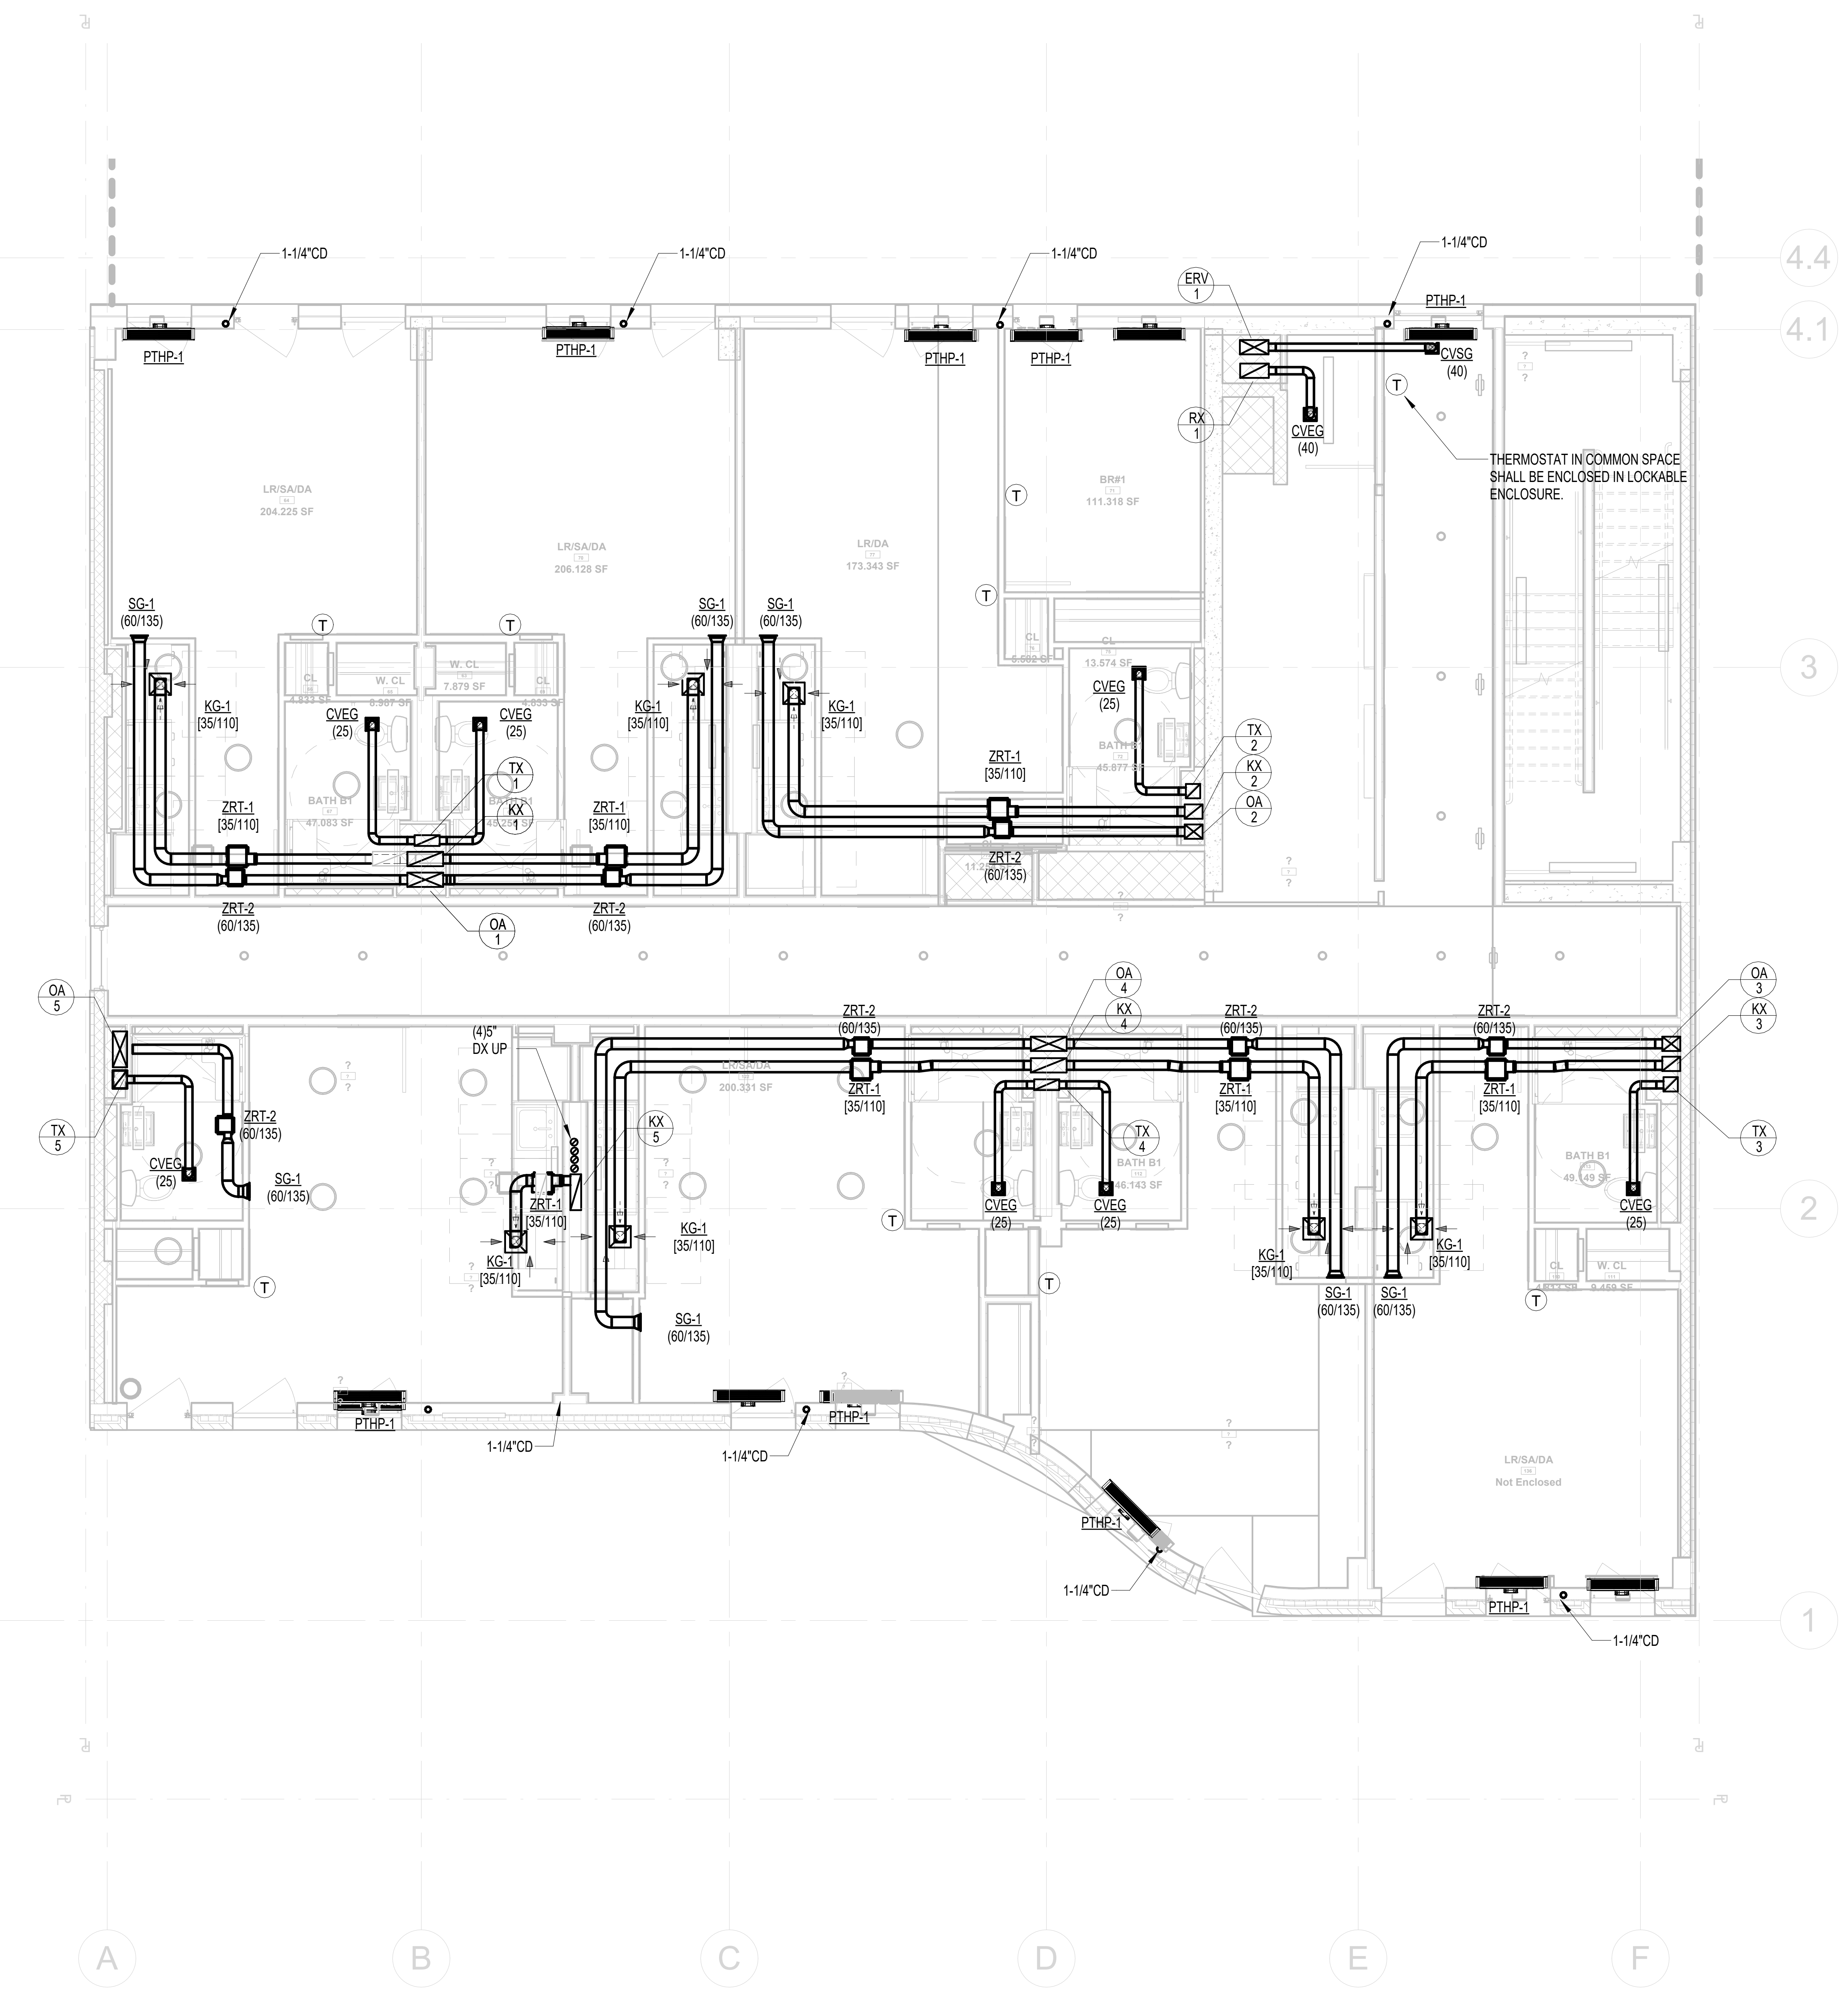

① 8TH FLOOR PLAN

SCALE: 3/16" = 1'-0"

DOB Application
number: #Q01372263-S4

INDIA HOME
A CENTER FOR SENIOR CARE

SITE 1 89TH AVE.

RKTB
Architects, P.C.

226 W 26th Street, 6th Flr.
New York, NY 10001
212.807.9500

FULCRUM
dream think build

226 W 26th Street, 6th Fl.
New York, NY
212.645.2317
www.fulcrumprop.com

India Home Procida Fulcro 178-36 Wexford Terrace Suite 2C Queens Village, NY 11432	Property Owner 917.288.7600 www.indiahome.org
McNamara Salvia Engineering 45 W 45th St. New York, NY 10036	Structural Engineer 212.246.9800 www.mcsal.com
Altera Engineering 1460 Broadway New York, NY 10036	Mechanical Engineer 212.330.7634 www.alteraeng.io
Pillori Associates, P.A. 71 Route 35 Laurence Harbor, NJ 08879	Geotechnical Engineer 732.335.0059 www.pilloriassociates.com
??? Landscape Architects ### Avenue Ave. City, ST #####	Landscape Architect ### ### #### www.????.com
??? Expeditor ### Avenue Ave. City, ST #####	Code Consultant ### ### #### www.????.com

Date	No.	Description
07/31/2026	3	PRICING SET
05/18/2026	2	ISSUED FOR DD
03/30/2026	1	ISSUED FOR DOB FILING

NOT FOR CONSTRUCTION

Approval:

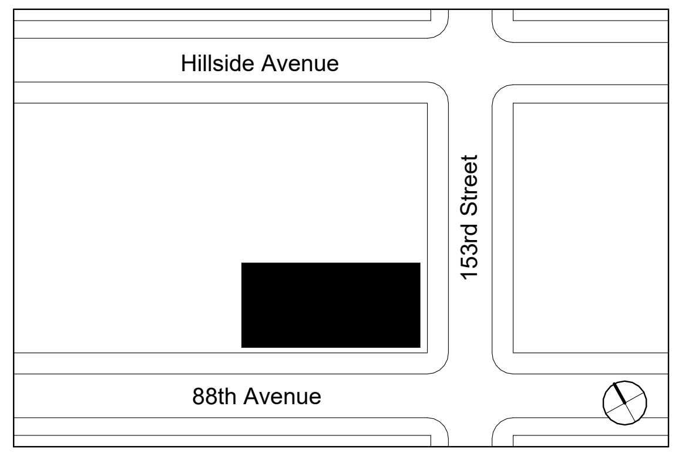

KEY PLAN

Project Address:

170-11 89th Avenue
Jamaica, Queens

Drawing Title:

MECHANICAL 8TH
FLOOR PLAN

Borough:	Block Number:
Zoning Map:	Lot Number:
Zoning District:	BIN Number:
Drawn By: DM	Checked By: DM
Signature & Seal: DMITRIY MOROZOV 086597	Project Number: 2516
	Date:
	Scale: 3/16" = 1'-0"
	Drawing Number: M-106.00
	Drawing:

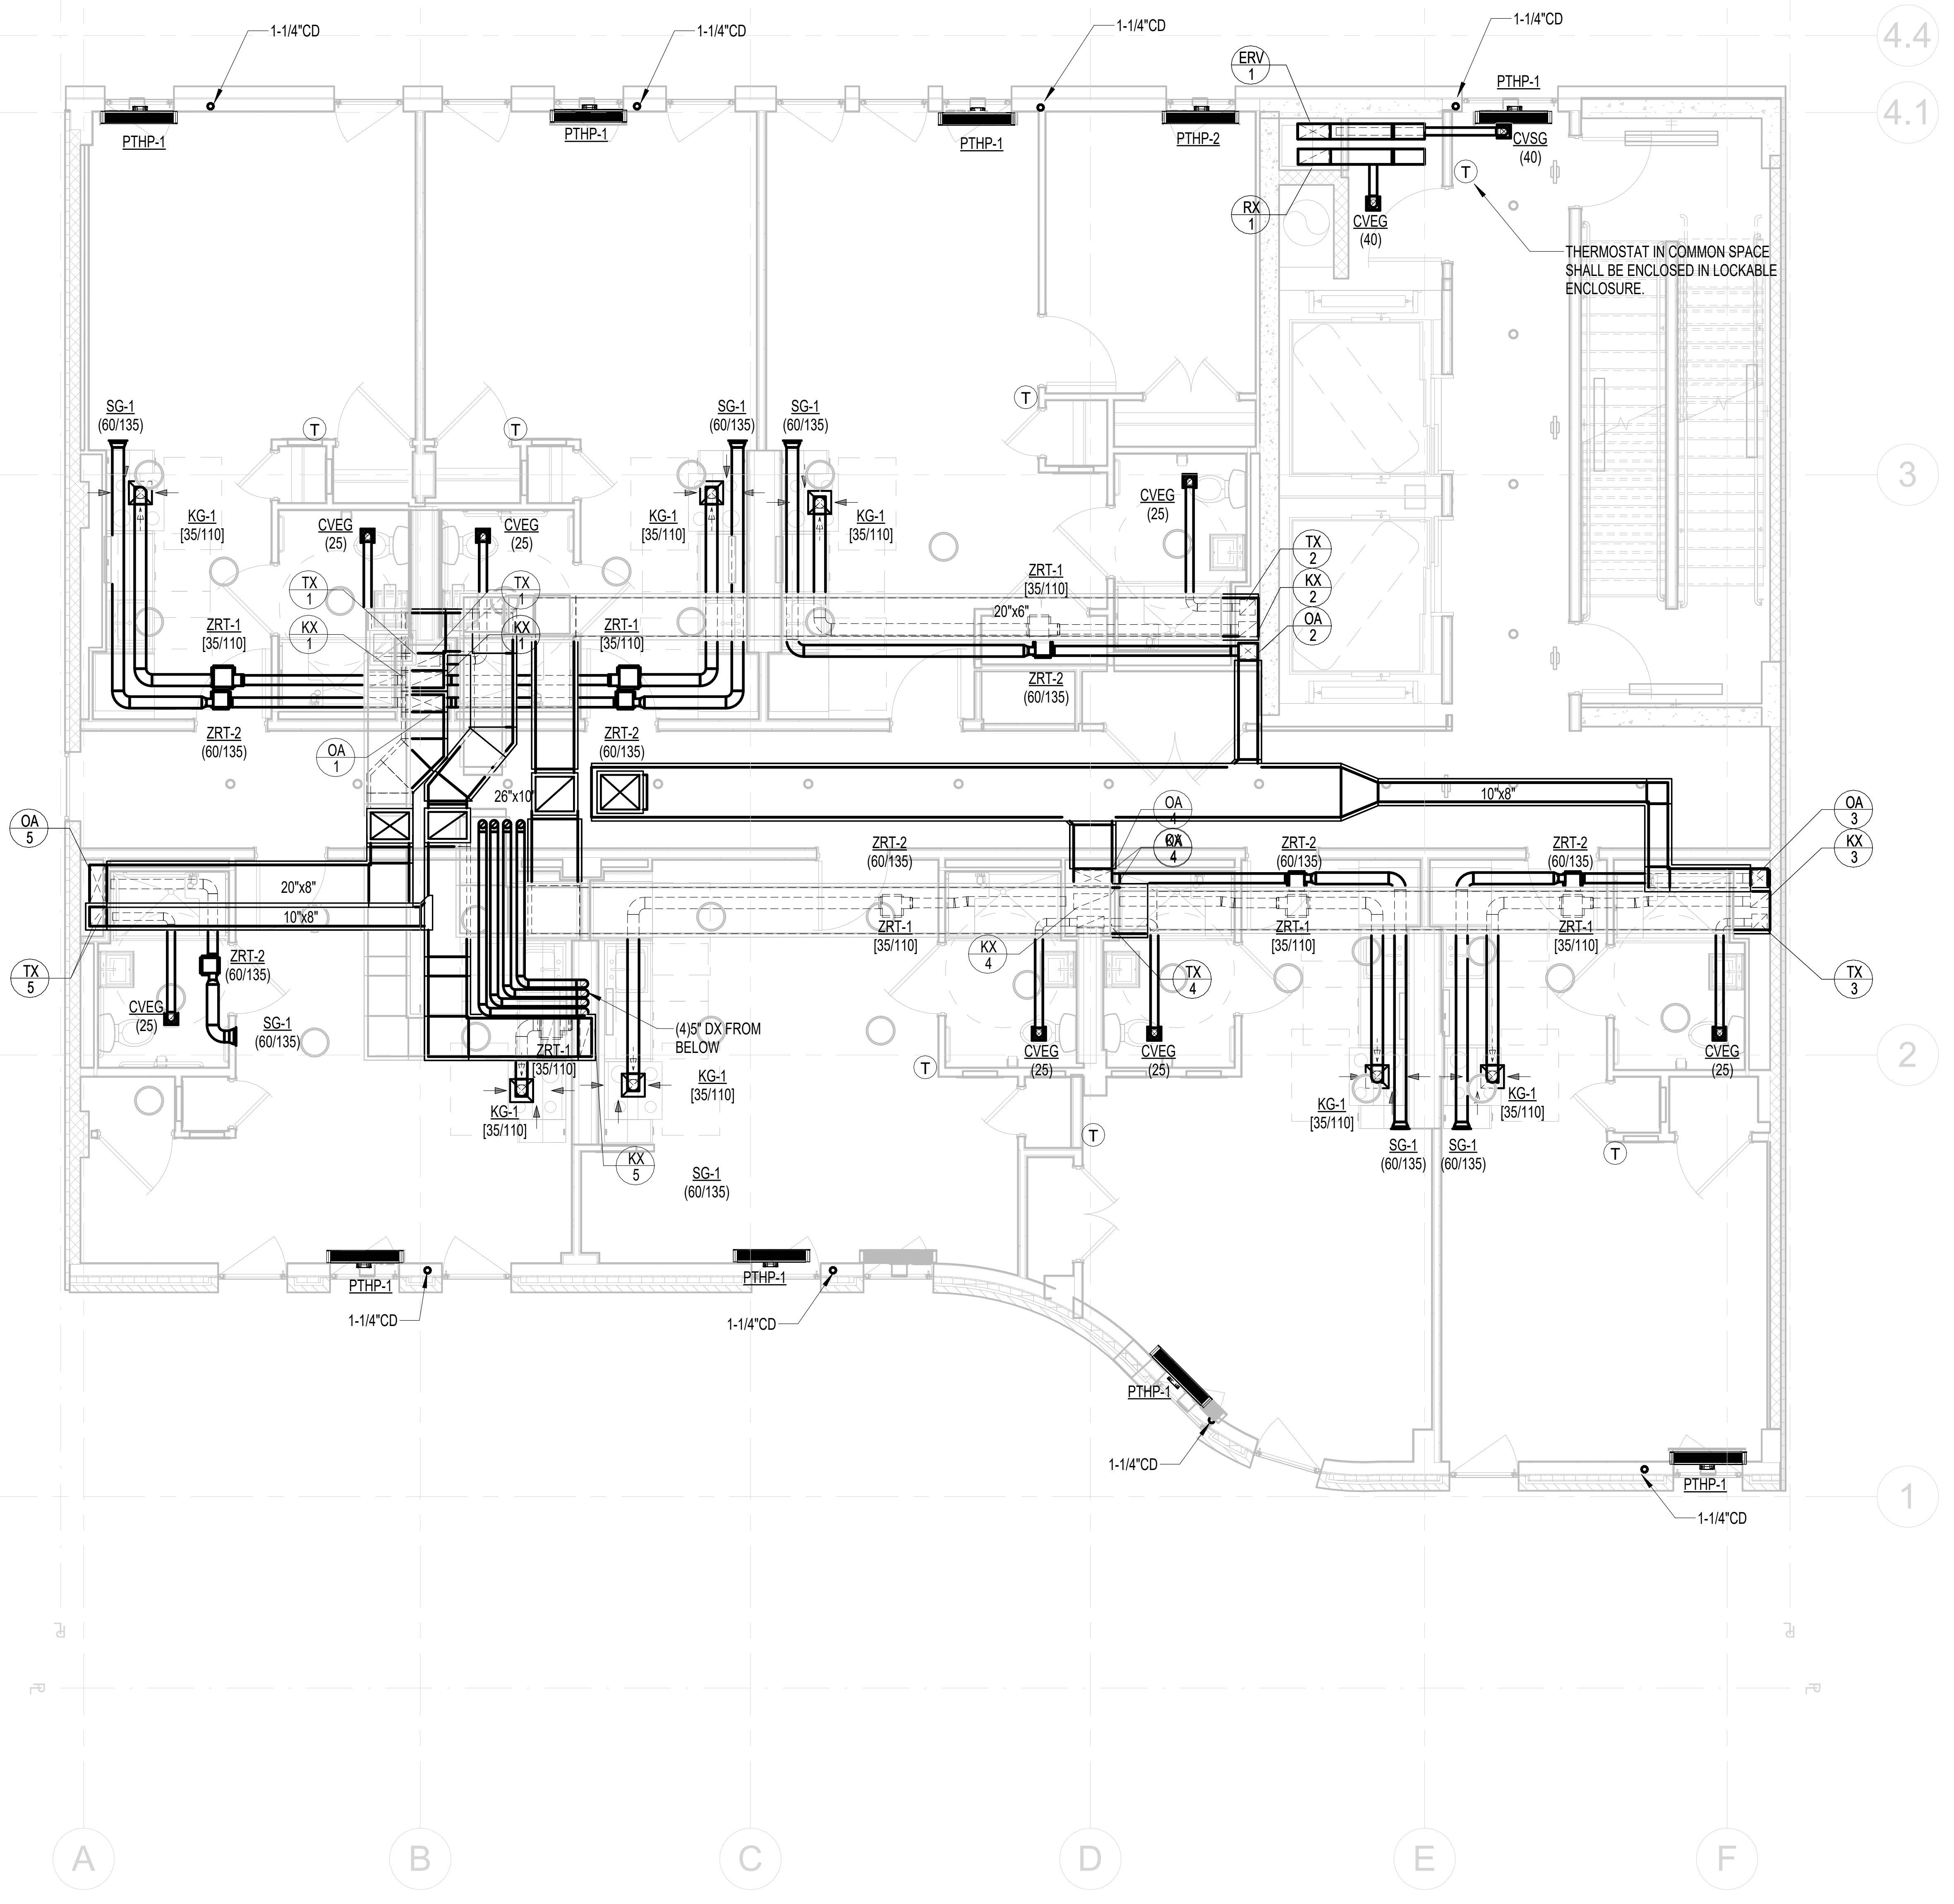

DOB Application
number: #Q01372263-S4

INDIA HOME
A CENTER FOR SENIOR CARE

SITE 1 89TH AVE.

RKTB
Architects, P.C.

226 W 26th Street, 6th Flr.
New York, NY 10001
212.807.9500

FULCRUM
dream think build

226 W 26th Street, 6th Fl.
New York, NY
212.645.2317
www.fulcrumprop.com

India Home Procida Fulcro 178-36 Wexford Terrace Suite 2C Queens Village, NY 11432	Property Owner 917.288.7600 www.indiahome.org
McNamara Salvia Engineering 45 W 45th St. New York, NY 10036	Structural Engineer 212.246.9800 www.mcsal.com
Altera Engineering 1460 Broadway New York, NY 10036	Mechanical Engineer 212.330.7634 www.alteraeng.io
Pillori Associates, P.A. 71 Route 35 Laurence Harbor, NJ 08879	Geotechnical Engineer 732.335.0059 www.pilloriassociates.com
??? Landscape Architects ### Avenue Ave. City, ST #####	Landscape Architect ### ### #### www.????.com
??? Expeditor ### Avenue Ave. City, ST #####	Code Consultant ### ### #### www.????.com

Date	No.	Description
07/31/2026	3	PRICING SET
05/18/2026	2	ISSUED FOR DD
03/30/2026	1	ISSUED FOR DOB FILING

NOT FOR CONSTRUCTION

Approval:

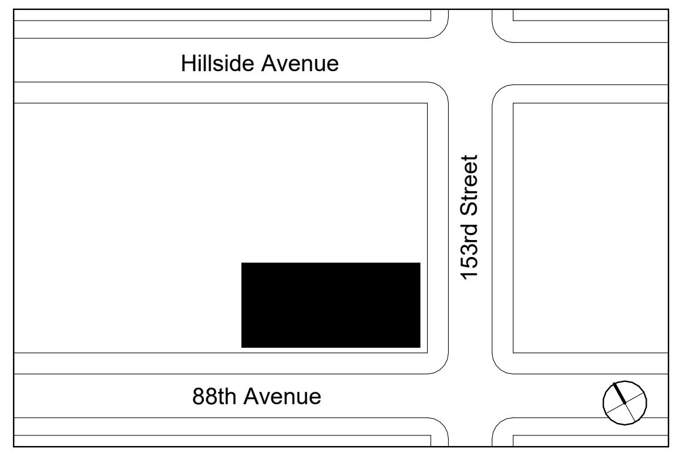

KEY PLAN

Project Address:

170-11 89th Avenue
Jamaica, Queens

Drawing Title:

MECHANICAL 9TH FLOOR PLAN

Borough:	Block Number:
Zoning Map:	Lot Number:
Zoning District:	BIN Number:
Drawn By: DM	Checked By: DM
Signature & Seal: DMITRIY MOROZOV 086597	Project Number: 2516
	Date:
	Scale: 3/16" = 1'-0"
	Drawing Number: M-107.00
	Drawing:

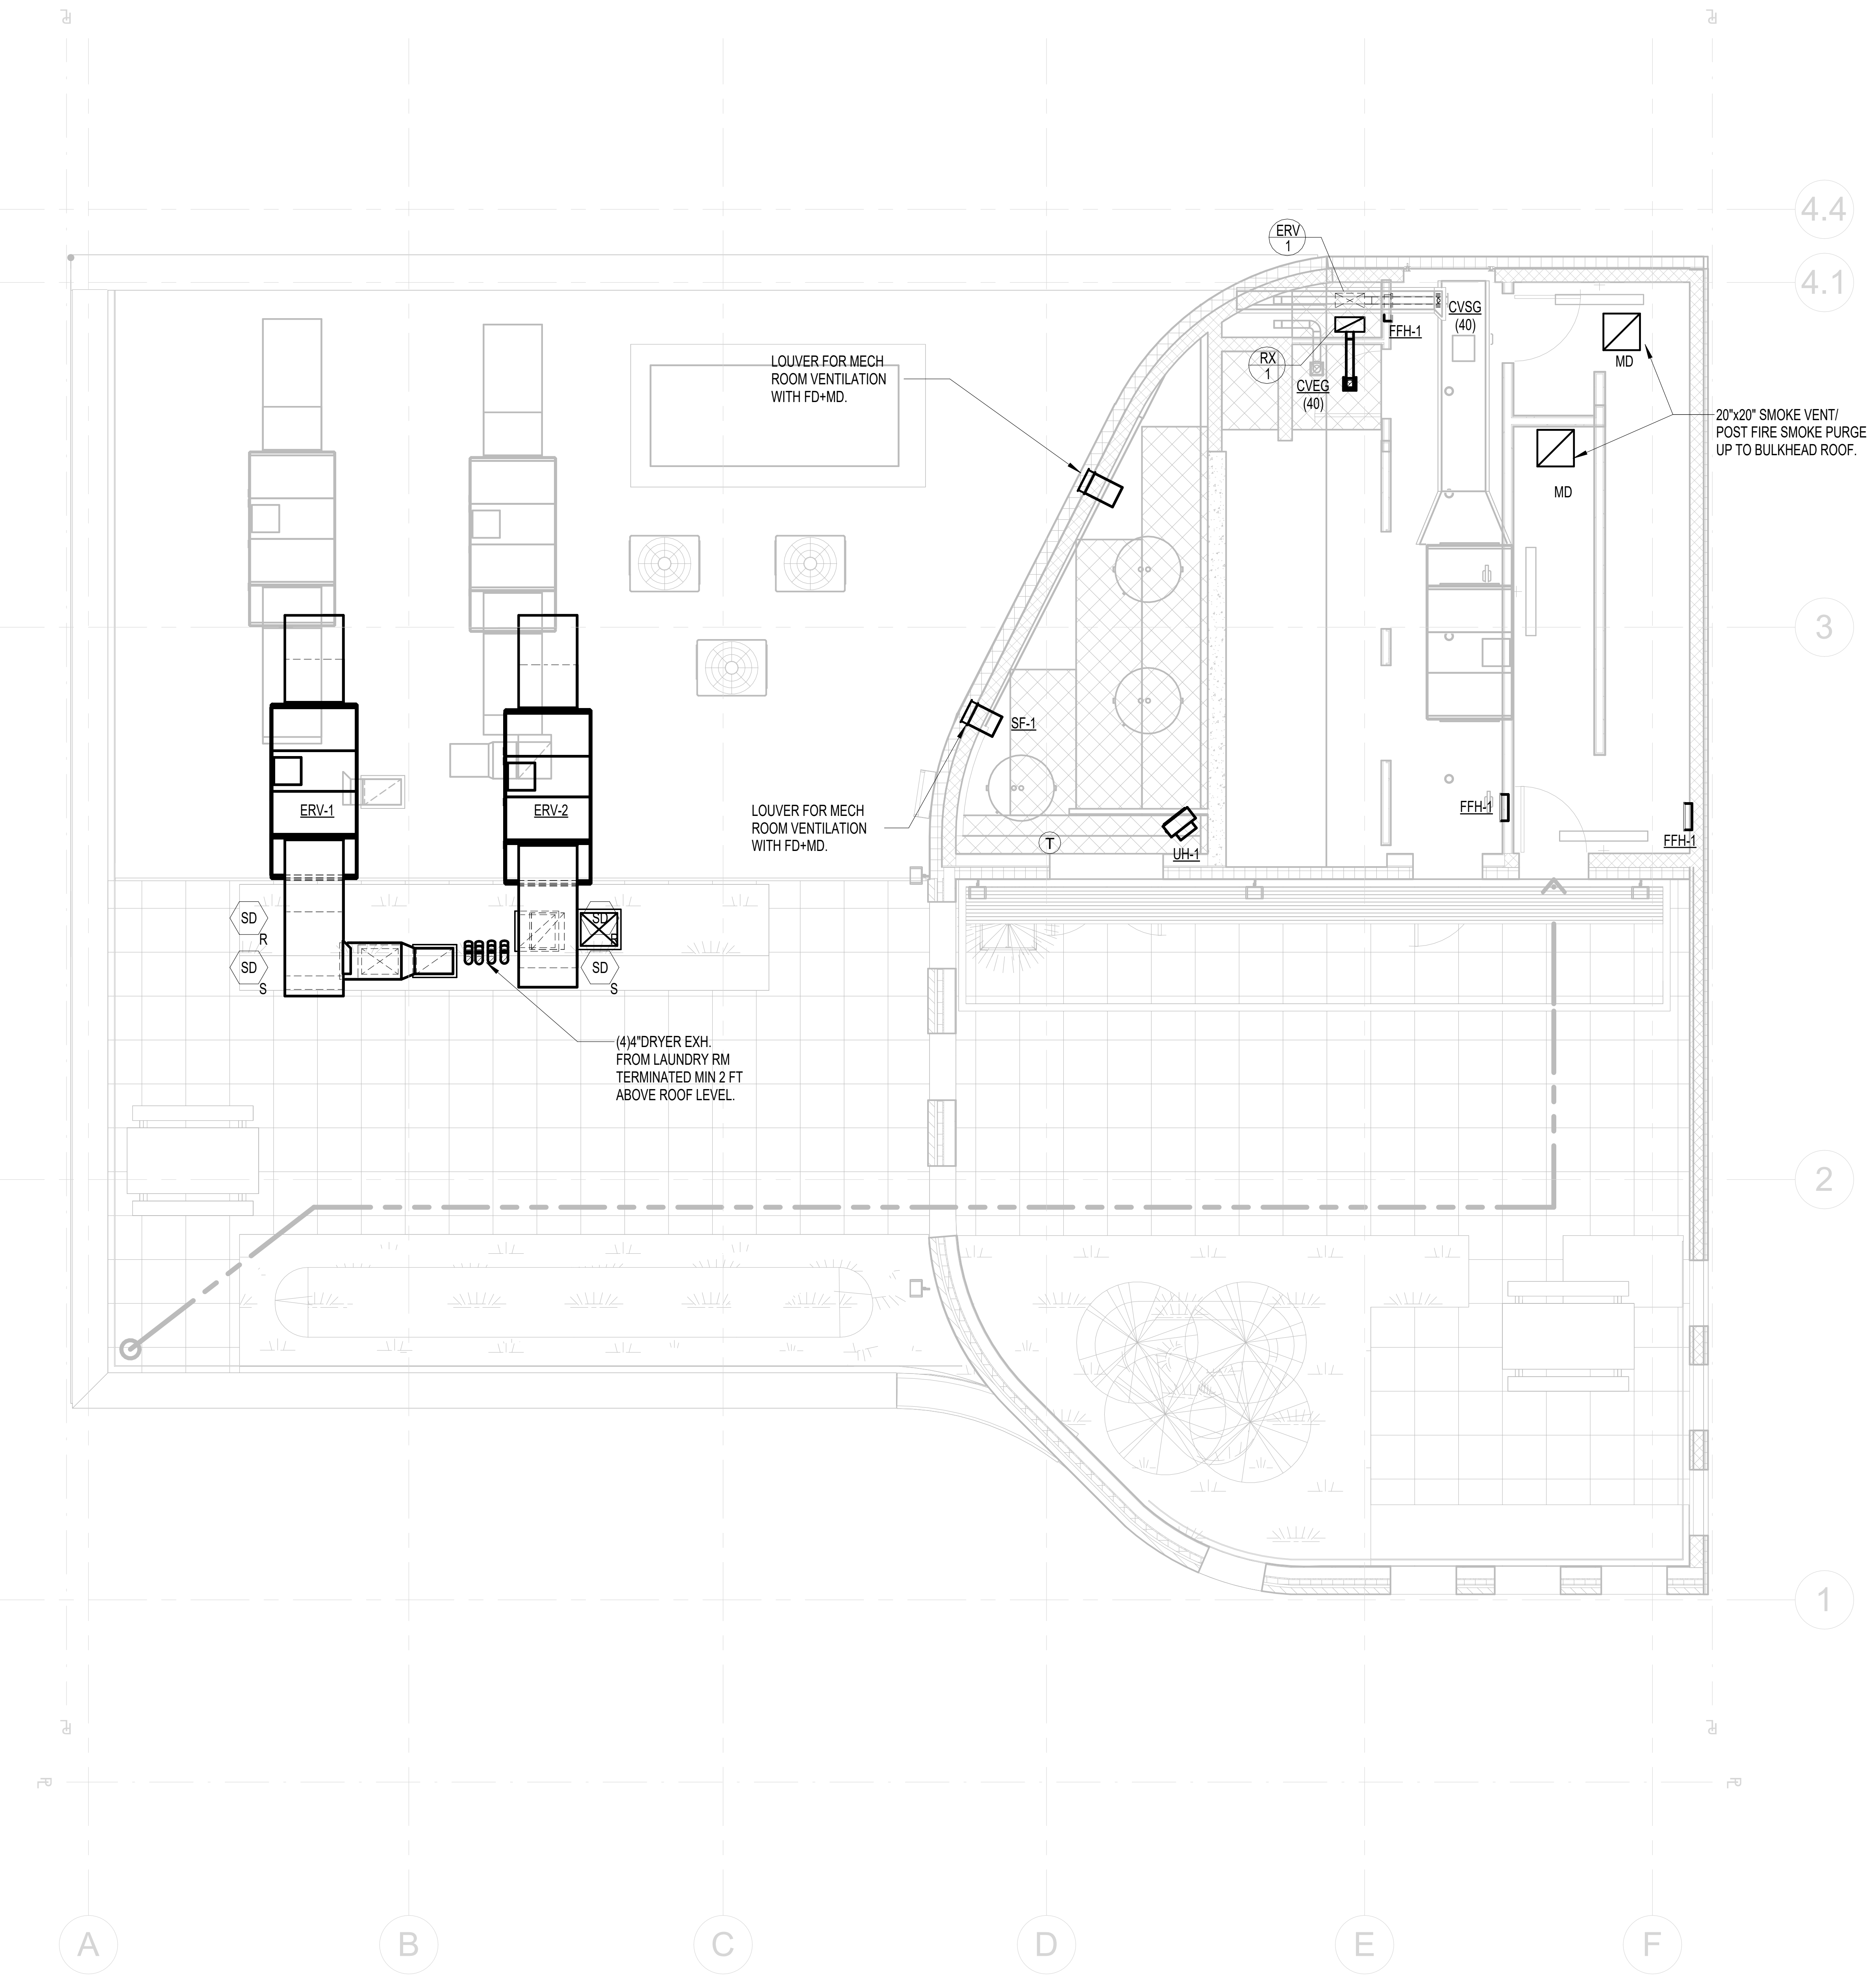

1 **ROOF**
SCALE: 3/16" = 1'-0"

31-Jul-26 7:50:00 PM

DOB Application
number: #Q01372263-S4

INDIA HOME
A CENTER FOR SENIOR CARE

SITE 1 89TH AVE.

RKTB
Architects, P.C.
226 W 26th Street, 6th Flr.
New York, NY 10001
212.807.9500

FULCRUM
dream think build
226 W 26th Street, 6th Fl.
New York, NY
212.645.2317
www.fulcrumprop.com

India Home Procida Fulcro 178-36 Wexford Terrace Suite 2C Queens Village, NY 11432	Property Owner 917.288.7600 www.indiahome.org
McNamara Salvia Engineering 45 W 45th St. New York, NY 10036	Structural Engineer 212.246.9800 www.mcsal.com
Altera Engineering 1460 Broadway New York, NY 10036	Mechanical Engineer 212.330.7634 www.alteraeng.io
Pillori Associates, P.A. 71 Route 35 Laurence Harbor, NJ 08879	Geotechnical Engineer 732.335.0059 www.pilloriassociates.com
??? Landscape Architects ### Avenue Ave. City, ST #####	Landscape Architect ### ### #### www.????.com
??? Expeditor ### Avenue Ave. City, ST #####	Code Consultant ### ### #### www.????.com

Date	No.	Description
07/31/2026	3	PRICING SET
05/18/2026	2	ISSUED FOR DD
03/30/2026	1	ISSUED FOR DOB FILING

NOT FOR CONSTRUCTION

Approval:

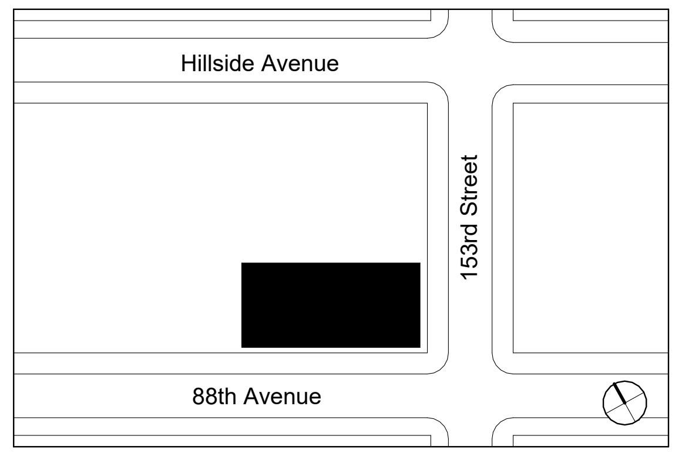

KEY PLAN

Project Address:

170-11 89th Avenue
Jamaica, Queens

Drawing Title:

MECHANICAL ROOF
PLAN 1

Borough:	Block Number:
Zoning Map:	Lot Number:
Zoning District:	BIN Number:
Drawn By: DM	Checked By: DM
Signature & Seal:	Project Number: 2516
	Date:
	Scale: 3/16" = 1'-0"
	Drawing Number: M-108.00
	Drawing:

DMITRIY MOROZOV
086597

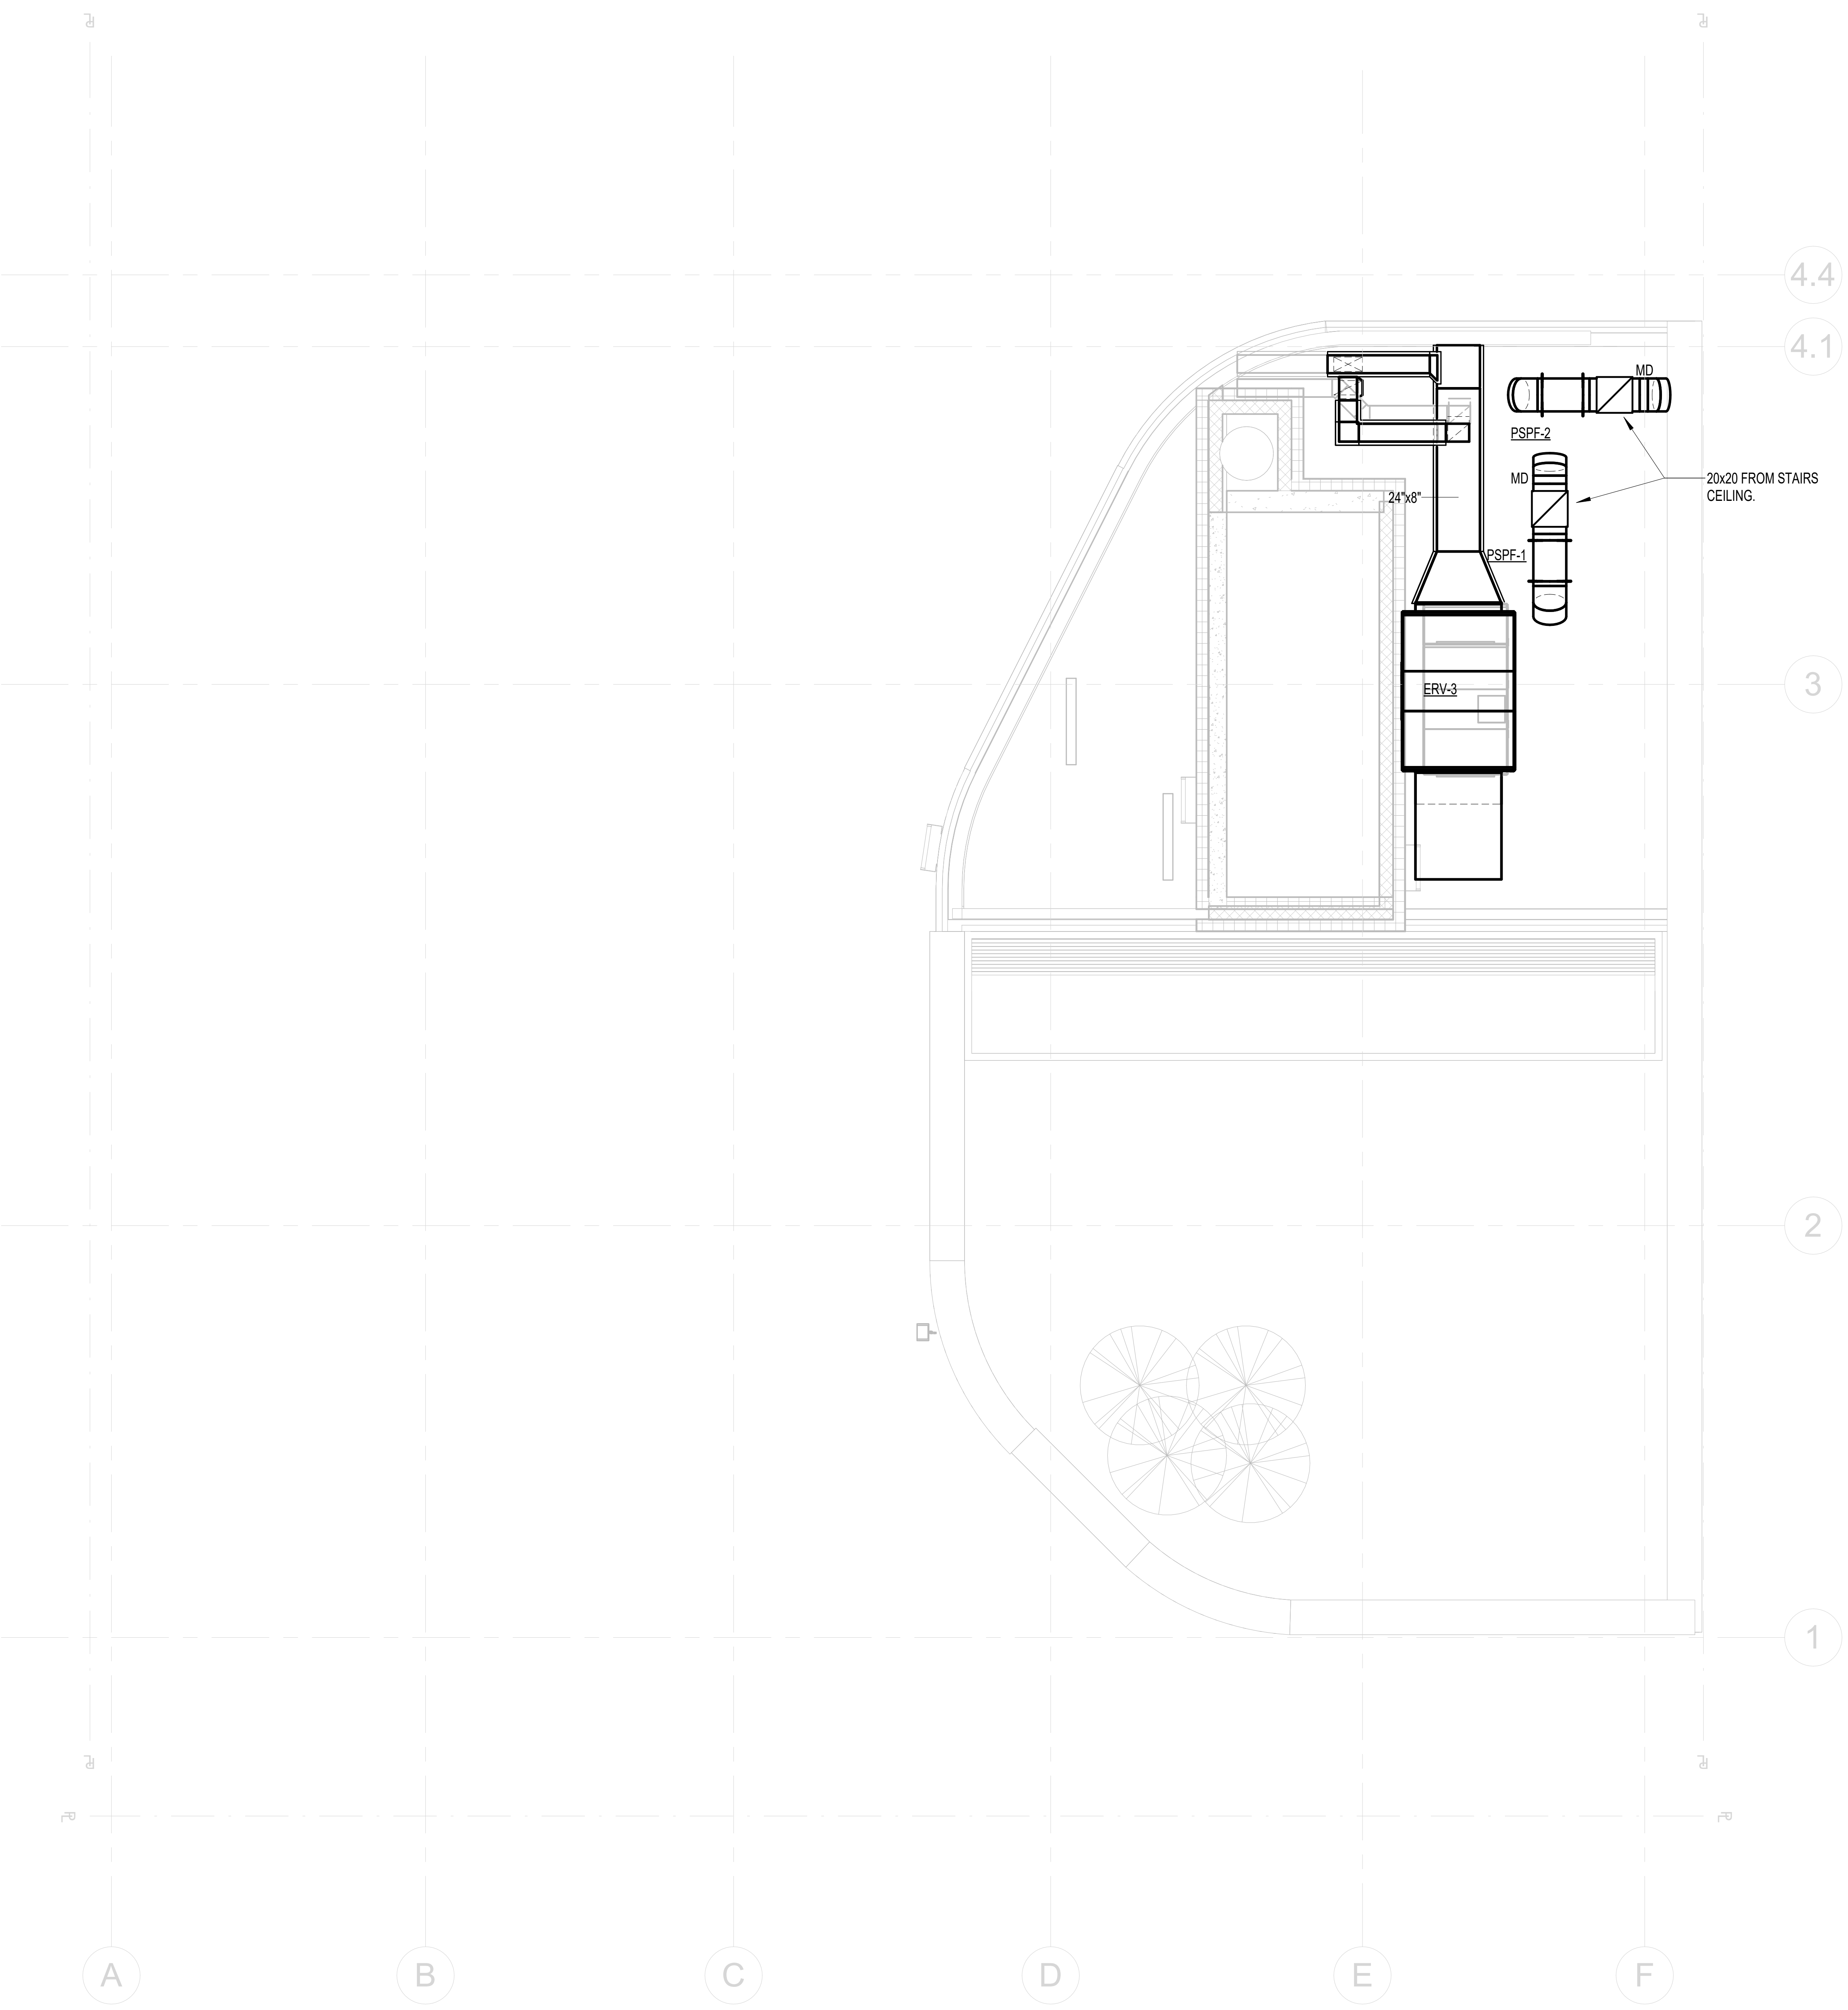

1 MECH ROOF
SCALE: 3/16" = 1'-0"

DOB Application
number: #Q01372263-S4

31-Jul-26 7:50:00 PM

INDIA HOME
A CENTER FOR SENIOR CARE

SITE 1 89TH AVE.

RKTB
Architects, P.C.

226 W 26th Street, 6th Flr.
New York, NY 10001
212.807.9500

FULCRUM
dream think build

226 W 26th Street, 6th Fl.
New York, NY
212.645.2317
www.fulcrumprop.com

India Home Procida Fulcro 178-36 Wexford Terrace Suite 2C Queens Village, NY 11432	Property Owner 917.288.7600 www.indiahome.org
McNamara Salvia Engineering 45 W 45th St. New York, NY 10036	Structural Engineer 212.246.9800 www.mcsal.com
Altera Engineering 1460 Broadway New York, NY 10036	Mechanical Engineer 212.330.7634 www.alteraeng.io
Pillori Associates, P.A. 71 Route 35 Laurence Harbor, NJ 08879	Geotechnical Engineer 732.335.0059 www.pilloriassociates.com
??? Landscape Architects ### Avenue Ave. City, ST #####	Landscape Architect ### ### #### www.????.com
??? Expeditor ### Avenue Ave. City, ST #####	Code Consultant ### ### #### www.????.com

Date	No.	Description
07/31/2026	3	PRICING SET
05/18/2026	2	ISSUED FOR DD
03/30/2026	1	ISSUED FOR DOB FILING

NOT FOR CONSTRUCTION

Approval:

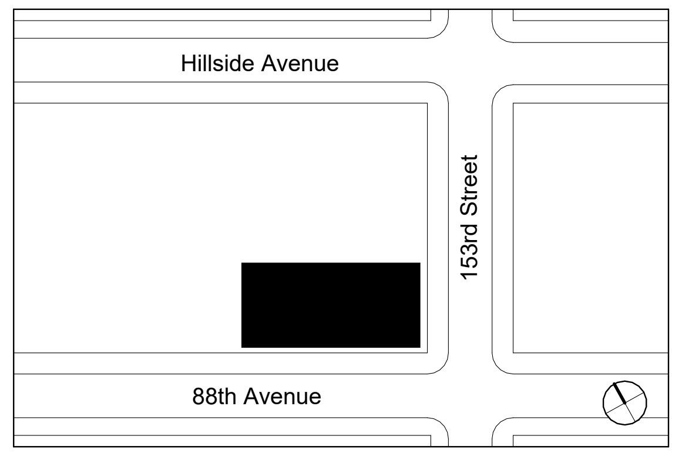

KEY PLAN

Project Address:

170-11 89th Avenue
Jamaica, Queens

Drawing Title:

MECHANICAL ROOF
PLAN 2

Borough:	Block Number:
Zoning Map:	Lot Number:
Zoning District:	BIN Number:
Drawn By: FD	Checked By: DM
Signature & Seal: DMITRIY MOROZOV 086597	Project Number: 2516
	Date:
	Scale: 3/16" = 1'-0"
	Drawing Number: M-109.00
	Drawing: