



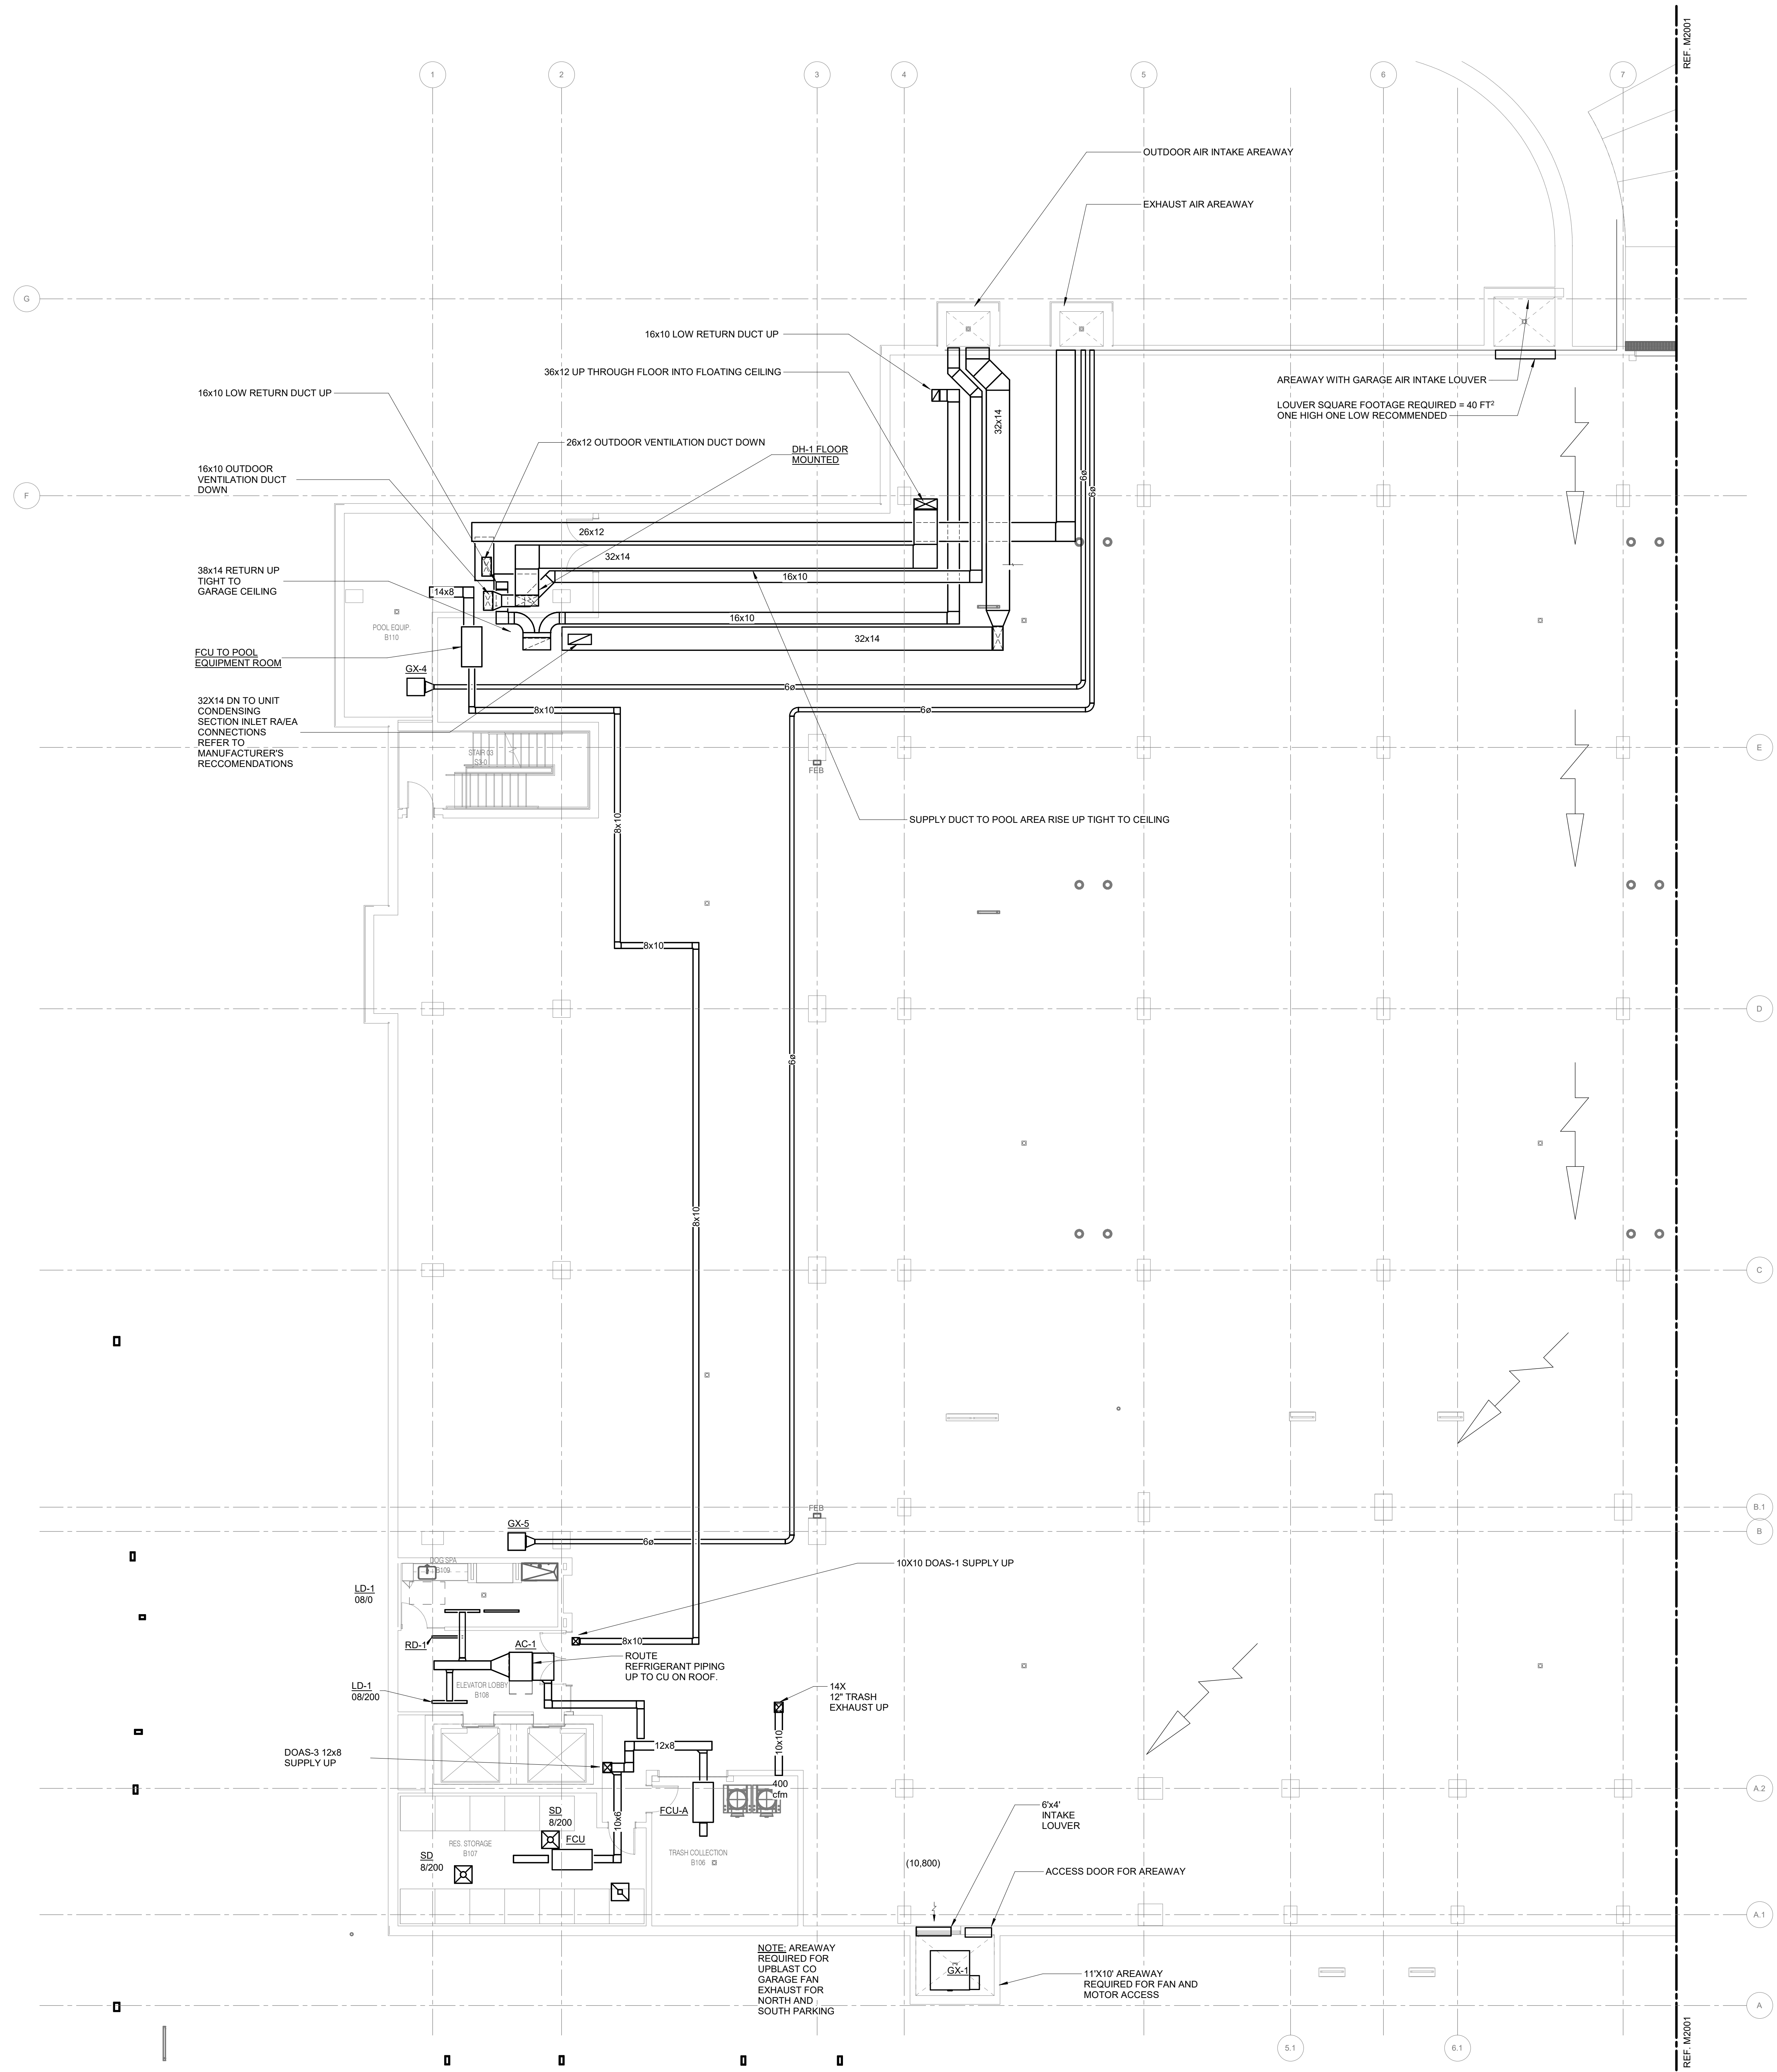

1 INDEPENDENT LIVING BASEMENT PLAN - MECHANICAL

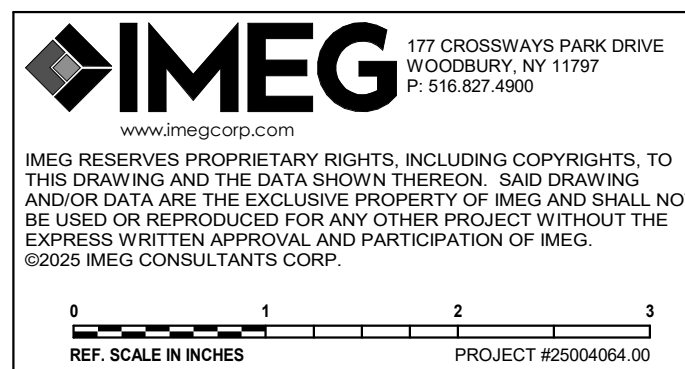

HKS

ARCHITECT
HKS ARCHITECTS, P.C.
30 WEST 28th STREET, 12th FLOOR
NEW YORK, NY 10010

STRUCTURAL

IMEG
1411 BROADWAY, SUITE 600
NEW YORK, NY 10018

MEP ENGINEER

IMEG
177 CROSSWAYS PARK DRIVE
WOODBURY, NY 11797

LV ENGINEER

TAZERGY
7653 HICKORY FLAT HWY, SUITE 200
WOODSTOCK, GA 30188


LANDSCAPE ARCHITECT

MPFP
120 BROADWAY, 20TH FLOOR
NEW YORK, NY 10271

POOL DESIGNER
COUNSILMAN-HUNSAKER & ASSOCIATES, INC.

12851 MANCHESTER ROAD, SUITE 120
ST. LOUIS, MO 63131


FOOD SERVICE
CLARK
2551 HORSESHOE RD
LANCASTER, PA 17601

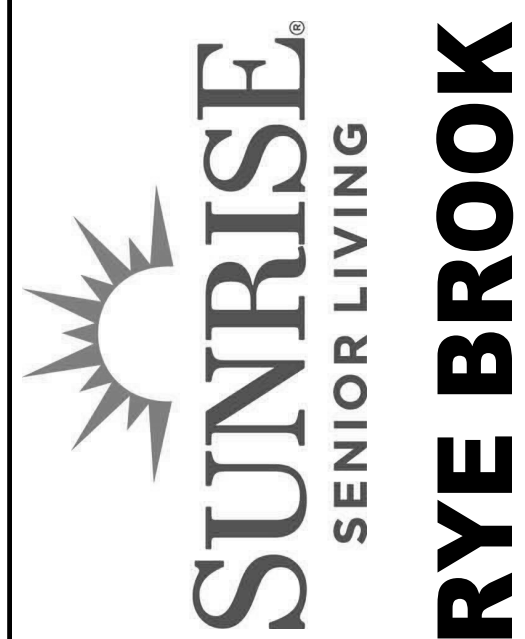

DOB BSCAN | DOB STAMP & SIGNATURES

SEAL & SIGNATURE_____

CON NO.: 111AAA
KEY PLAN_____

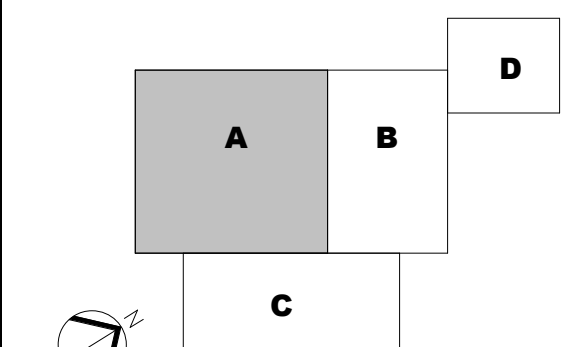

REVISION		
NO.	DESCRIPTION	DATE
1	DD Progress Print	08/28/2
2	DESIGN DEVELOPMENT	11/25/2
3	EXTERIOR BUILDING PERMIT	12/23/2
4	100% DESIGN DEVELOPMENT	01/30/2
5	ISSUED FOR PERMIT	06/05/2

HKS PROJECT NUMBER

25004064.00

DATE
07/15/26

ISSUE


ISSUED FOR GMP

SHEET TITLE
**INDEPENDENT LIVING
BASEMENT PLAN -
MECHANICAL**



SHEET NO.

M2000

DOB FILE #: DOB PAGE #

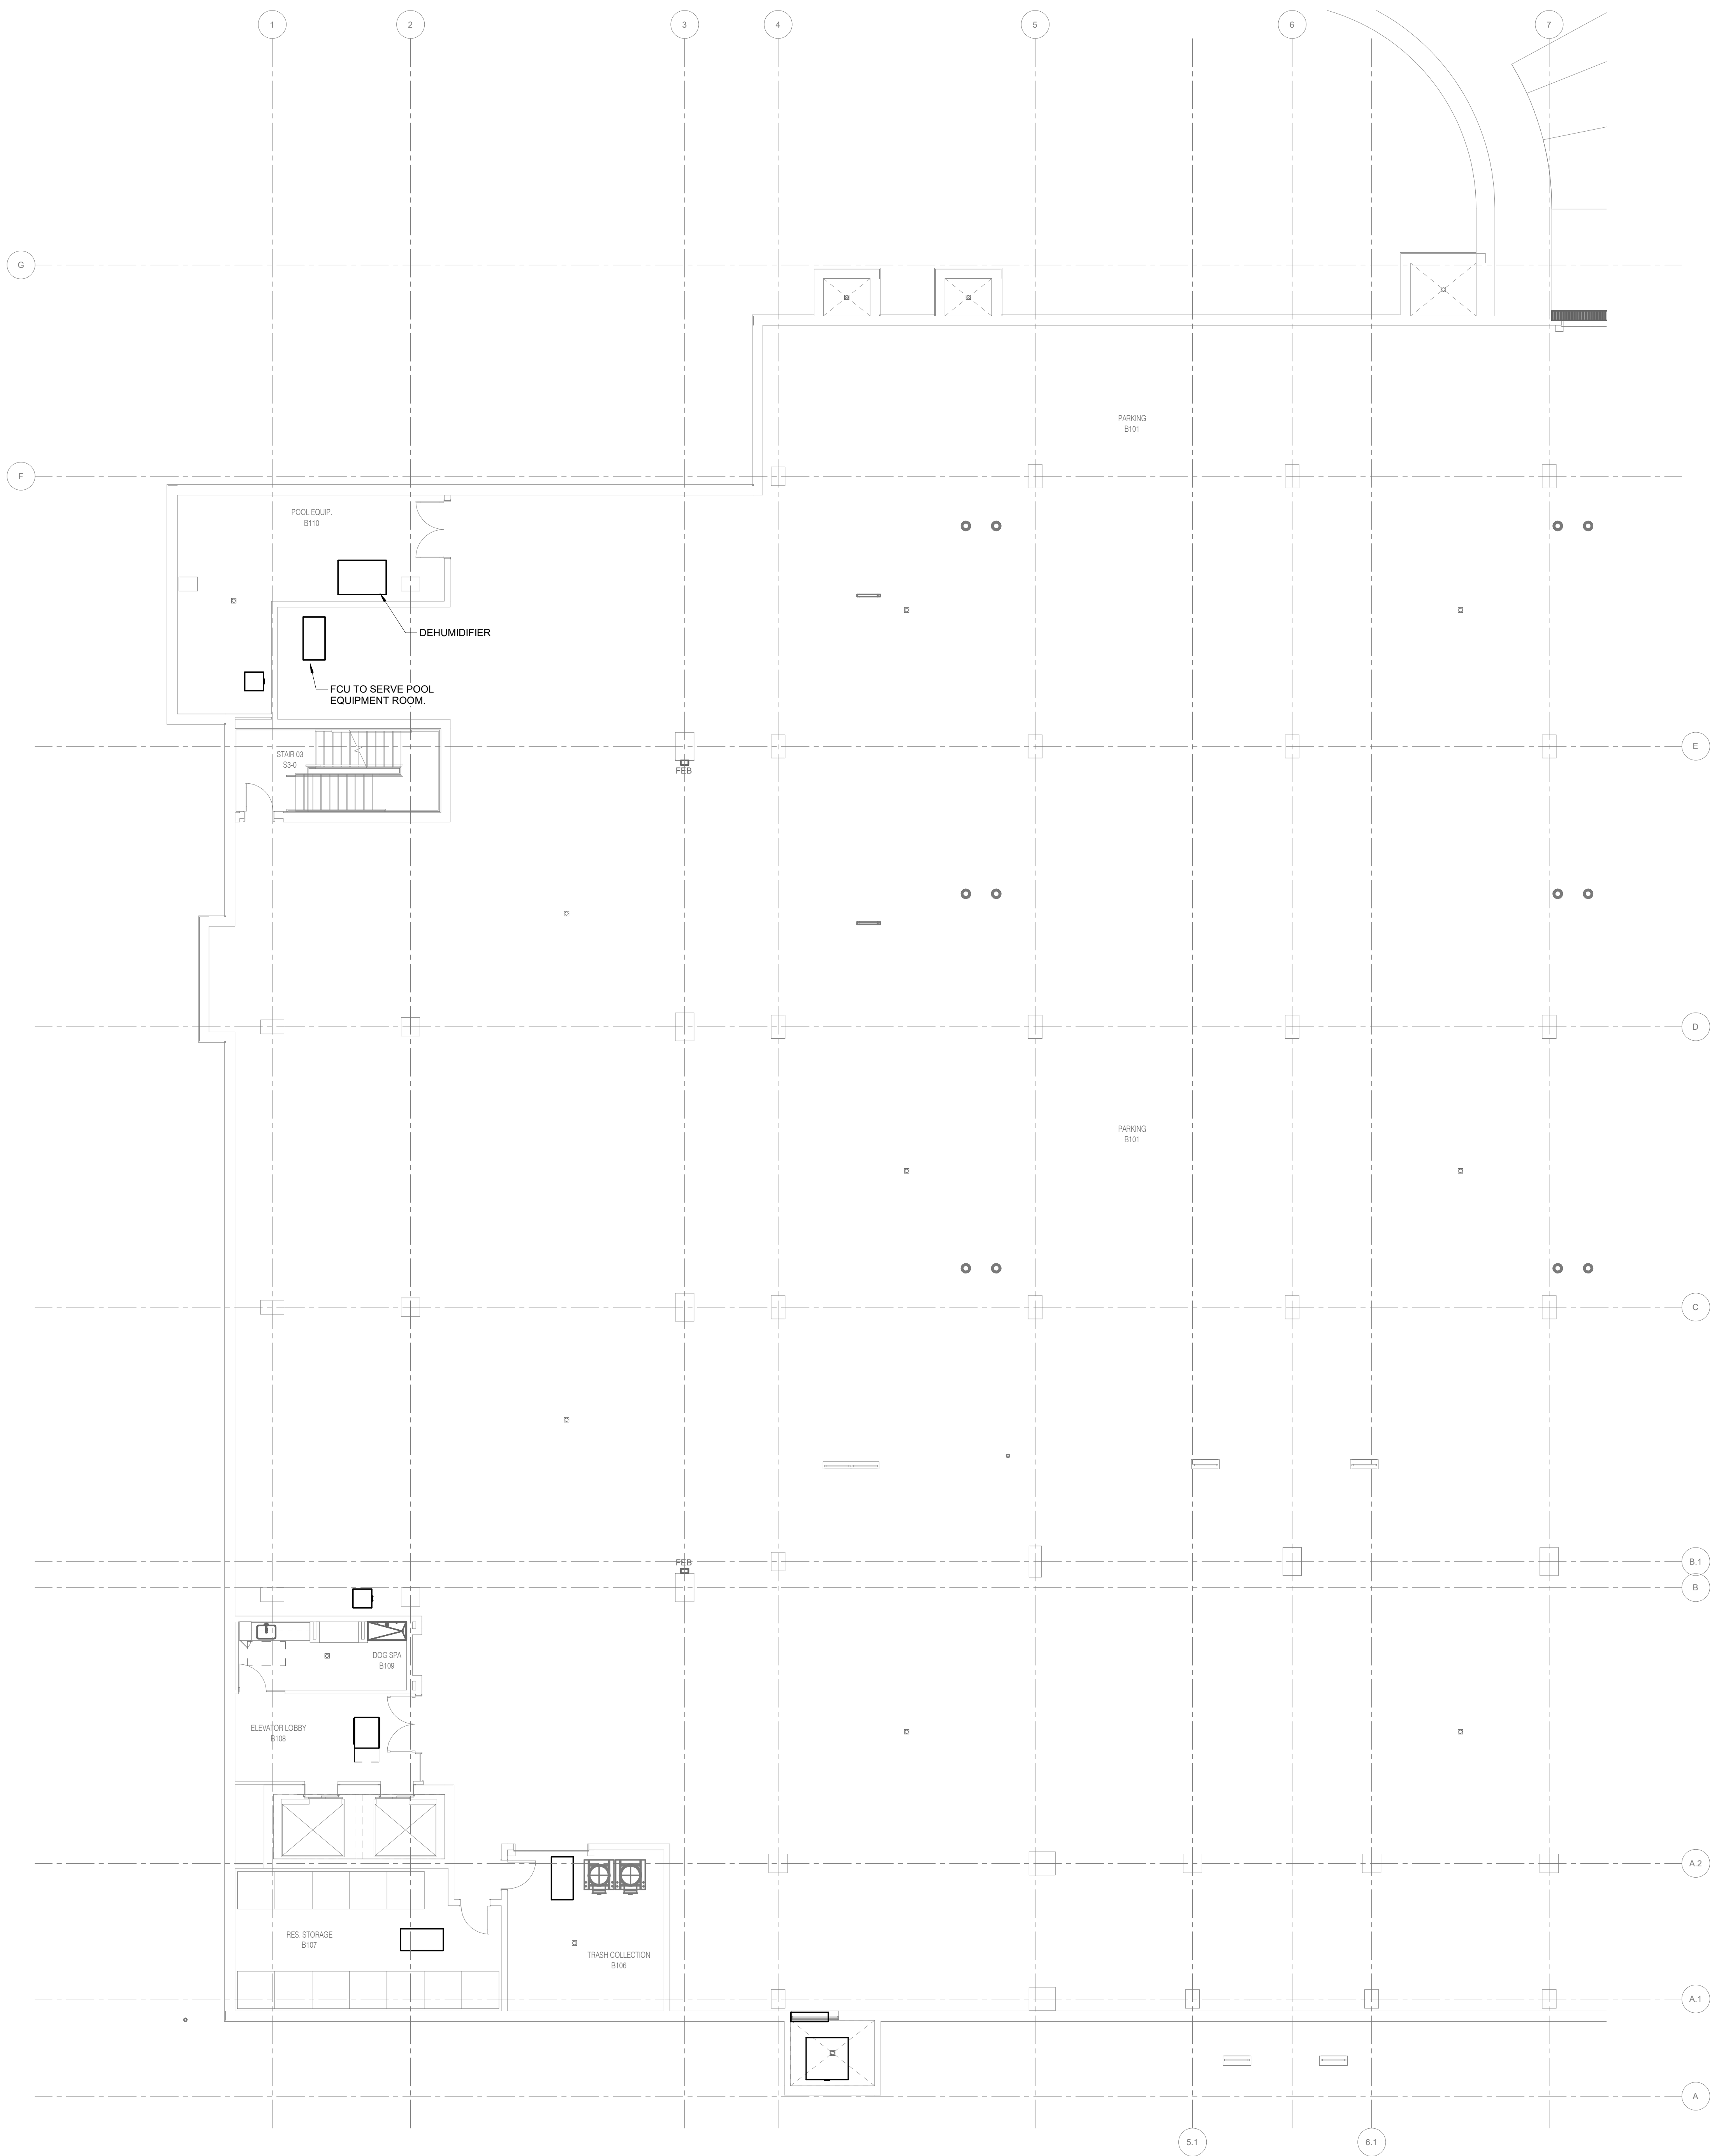**1 INDEPENDENT LIVING BASEMENT PLAN - MECHANICAL PIPING**

1/8" = 1'-0"

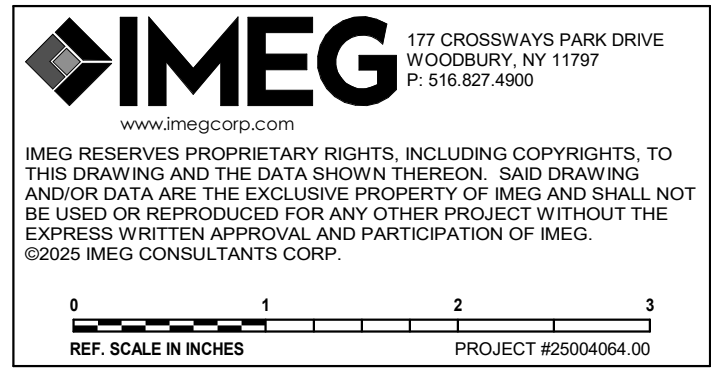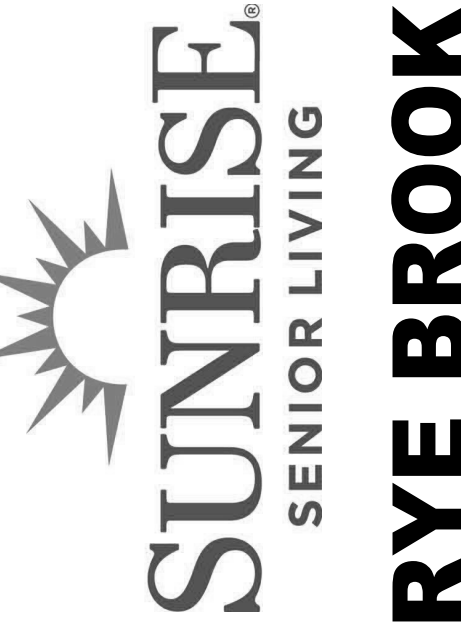
**HKS****ARCHITECT**
HKS ARCHITECTS, P.C.
30 WEST 26th STREET, 12th FLOOR
NEW YORK, NY 10010**STRUCTURAL**
IMEG
1411 BROADWAY, SUITE 600
NEW YORK, NY 10018**MEP ENGINEER**
IMEG
177 CROSWAYS PARK DRIVE
WOODBURY, NY 11797**LV ENGINEER**
TIZERGY
7853 HICKORY FLAT HWY, SUITE 200
WOODSTOCK, GA 30188**LANDSCAPE ARCHITECT**
MPFP
120 BROADWAY, 20TH FLOOR
NEW YORK, NY 10271**POOL DESIGNER**
COUNSLMANHUNSAKER & ASSOCIATES, INC.
12851 MANCHESTER ROAD, SUITE 120
ST. LOUIS, MO 63131**FOOD SERVICE & LAUNDRY**
CLARK
2551 HORSESHOE RD.
LANCASTER, PA 17601

DOB BSCAN | DOB STAMP & SIGNATURES

SEAL & SIGNATURE

CON NO.: 111AAA

KEY PLAN

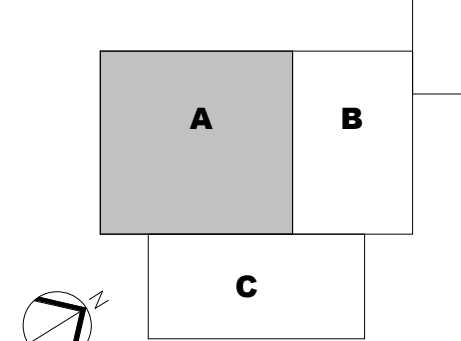

REVISION		
NO.	DESCRIPTION	DATE
1	DD Progress Print	08/26/25
2	DESIGN DEVELOPMENT	11/25/25
3	EXTERIOR BUILDING PERMIT	12/23/25
4	100% DESIGN DEVELOPMENT	01/30/26
5	ISSUED FOR PERMIT	06/05/26

HKS PROJECT NUMBER
25004064.00

DATE

07/15/26

ISSUE


ISSUED FOR GMPSHEET TITLE
**INDEPENDENT LIVING
BASEMENT PLAN -
MECHANICAL PIPING**

SHEET NO.

M2001

DOB FILE # DOB PAGE #

TITLE BLOCK VERSION: 20160301
PROJECT: 25004064.00 - ASSISTED LIVING BASEMENT PLAN - MECHANICAL
PROJECT ADDRESS: 300 Kings Rye Brook, NY 10573
CON NO.: 111AAA
KEY PLAN:
REVISION:
NO. 1
DESCRIPTION
DATE
1. 00 Program Phase 08/26/25
2. DESIGN DEVELOPMENT 11/25/25
3. EXTERIOR BUILDING PERMIT 12/23/25
4. 100% DESIGN DEVELOPMENT 01/28/26
5. ISSUED FOR PERMIT 06/26/26
HKS PROJECT NUMBER
25004064.00
DATE
07/15/26
ISSUE
ISSUED FOR GMP
SHEET TITLE
ASSISTED LIVING
BASEMENT PLAN - MECHANICAL
SHEET NO.
M2002
DOB FILE #
DOB PAGE #

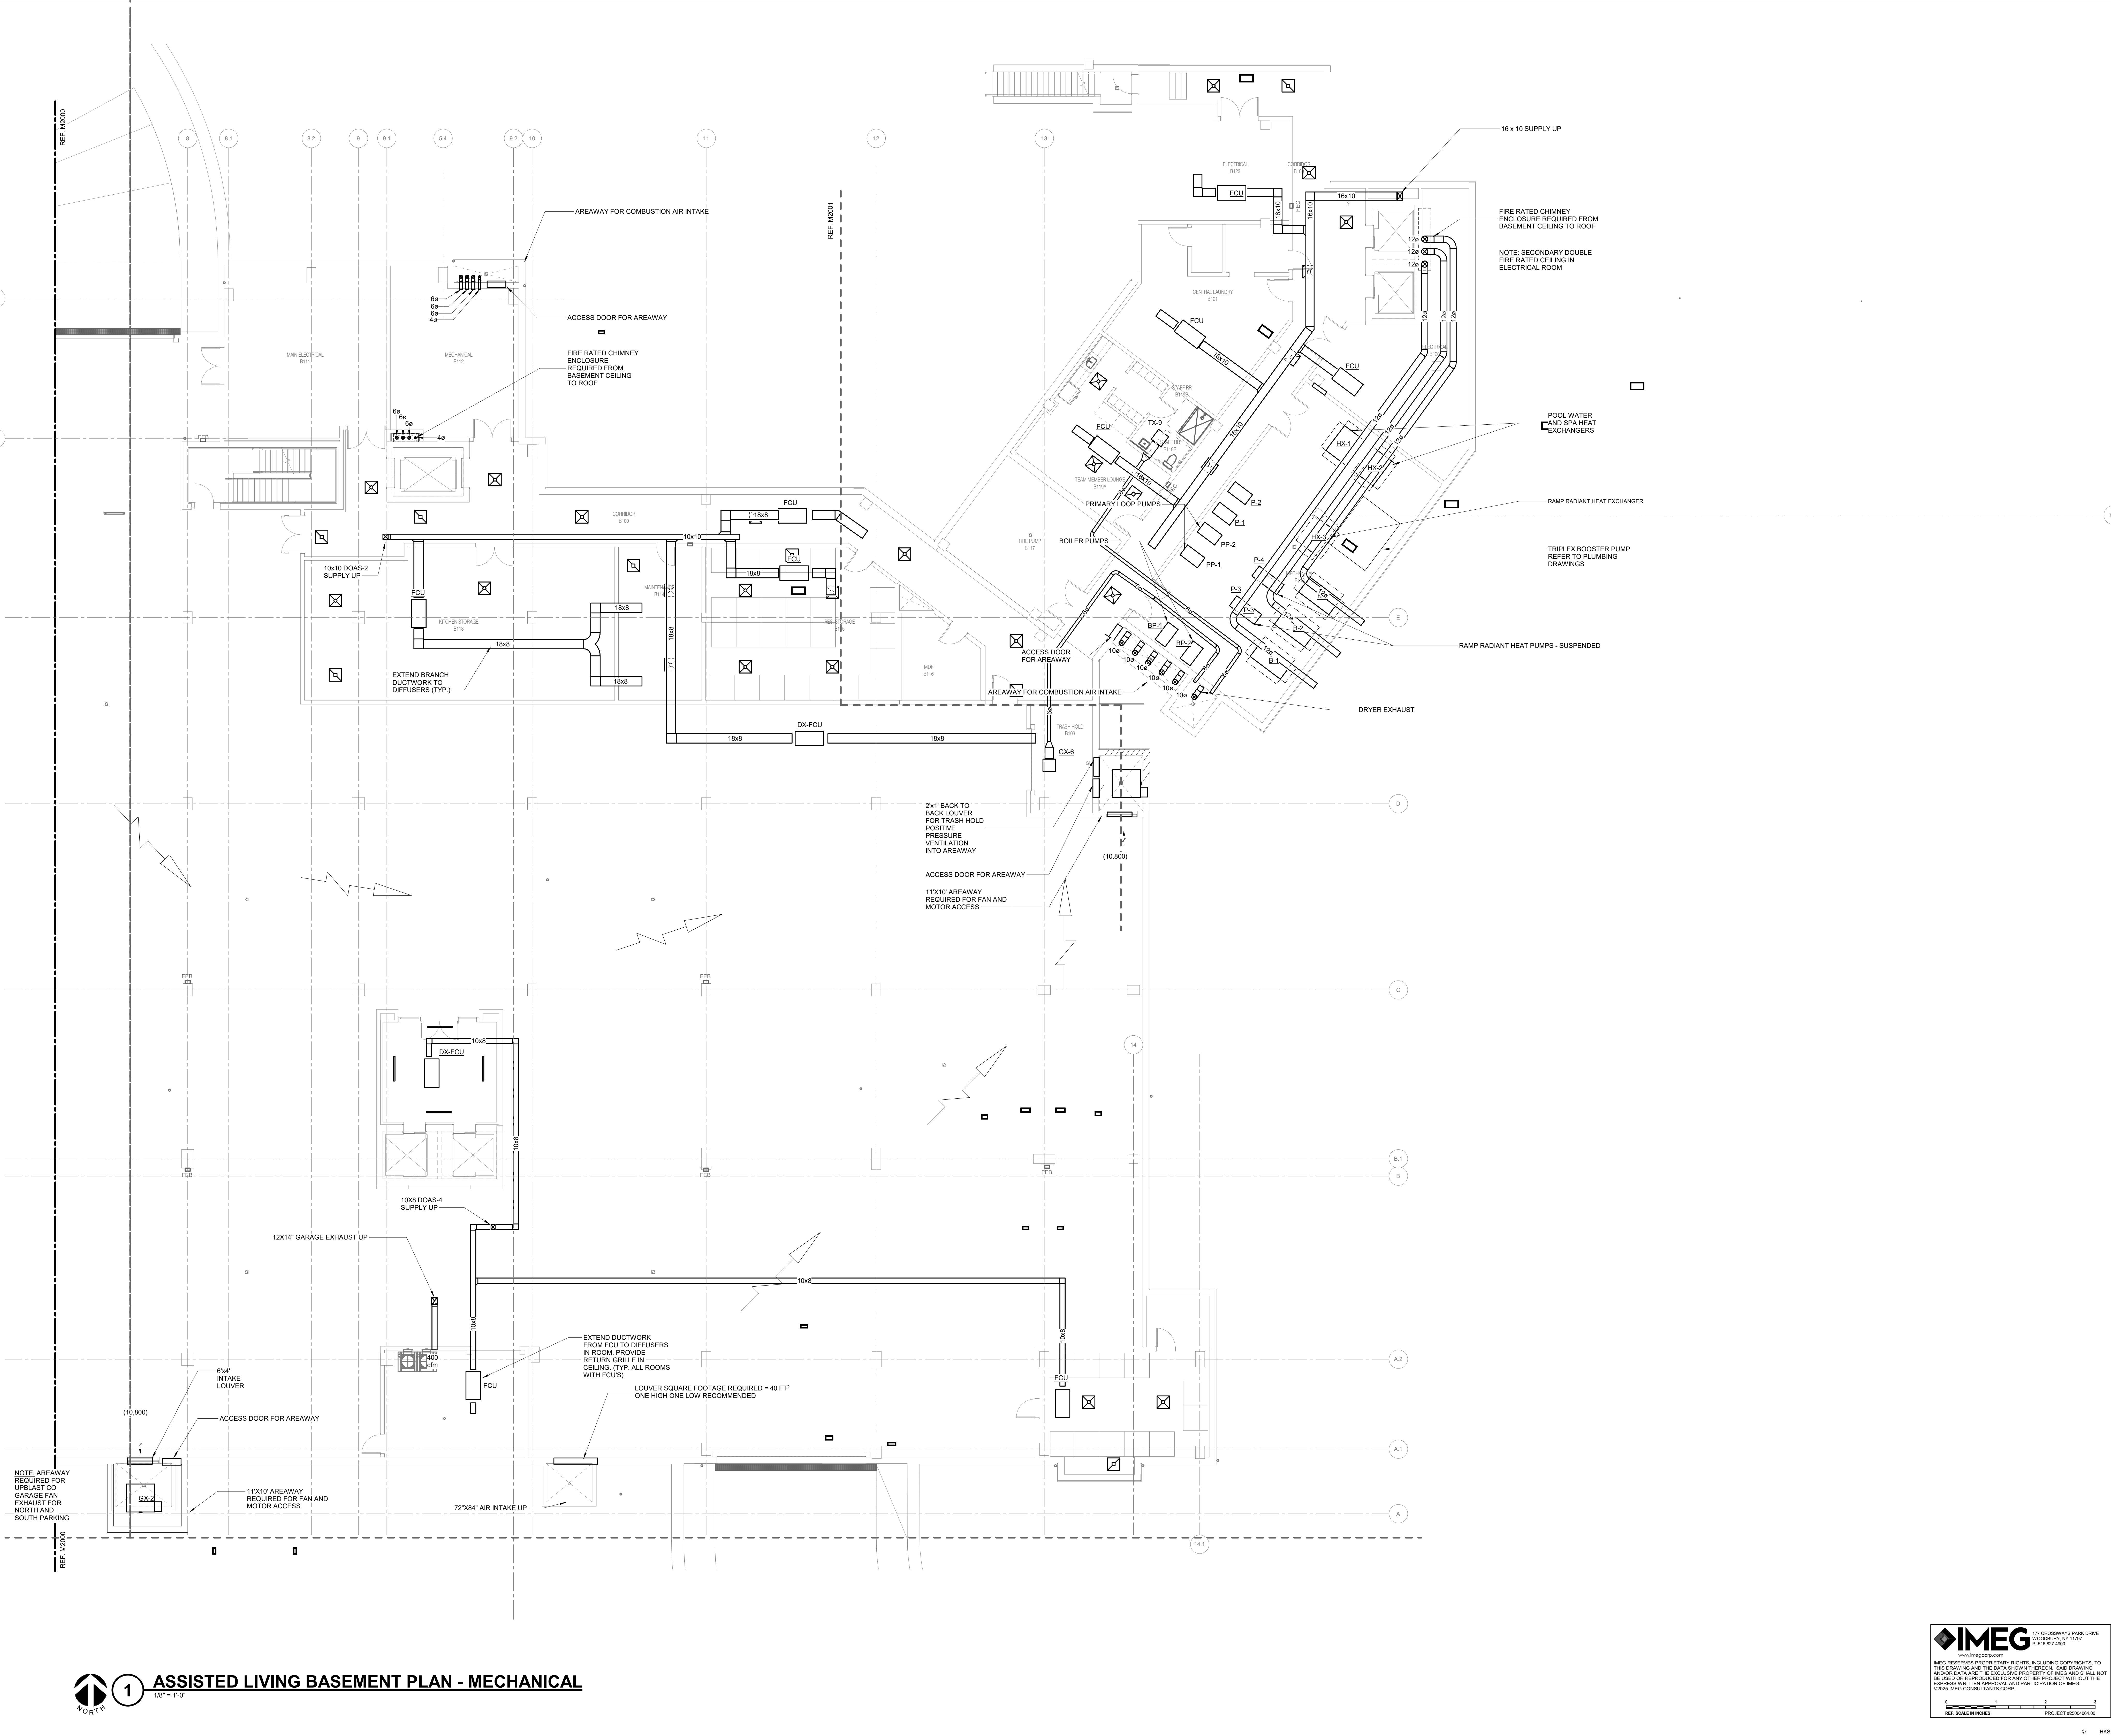

HKS

ARCHITECT
HKS ARCHITECTS, P.C.
30 WEST 26th STREET, 12th FLOOR
NEW YORK, NY 10010

STRUCTURAL
IMEG
1411 BROADWAY, SUITE 600
NEW YORK, NY 10018

MEP ENGINEER
IMEG
177 CROSWAYS PARK DRIVE
WOODBURY, NY 11797

LV ENGINEER
TATEROY
785 HICKORY FLAT HWY, SUITE 200
WOODSTOCK, GA 30188

LANDSCAPE ARCHITECT
MFP
120 BROADWAY, 20TH FLOOR
NEW YORK, NY 10271

POOL DESIGNER
COUNSLMANHUNSAKER & ASSOCIATES, INC.
12851 MANCHESTER ROAD, SUITE 120
ST. LOUIS, MO 63131


FOOD SERVICE & LAUNDRY
CLARK
2551 HORSESHOE RD.
LANCASTER, PA 17601

SUNRISE
SENIOR LIVING
RYE BROOK

DOB BSCAN | DOB STAMP & SIGNATURES

SEAL & SIGNATURE

CON NO.: 111AAA
KEY PLAN


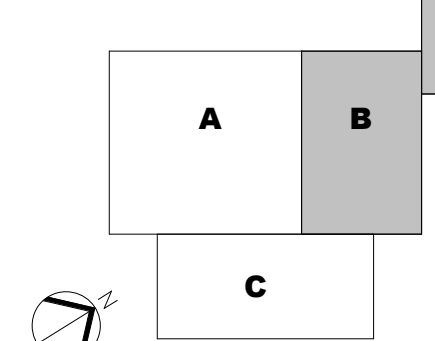


REVISION	
NO.	DESCRIPTION
1	DD Progress Print
2	DESIGN DEVELOPMENT
3	EXTERIOR BUILDING PERMIT
4	100% DESIGN DEVELOPMENT
5	ISSUED FOR PERMIT

IMEG
177 CROSWAYS PARK DRIVE
WOODBURY, NY 11797
P: 516-927-6900

IMEG RESERVES PROPRIETARY RIGHTS, INCLUDING COPYRIGHTS, TO THIS DRAWING AND THE DATA SHOWN THEREON. NO PART OF THIS DRAWING OR DATA ARE THE EXCLUSIVE PROPERTY OF IMEG AND SHALL NOT BE USED OR REPRODUCED FOR ANY OTHER PROJECT WITHOUT THE EXPRESS WRITTEN APPROVAL AND PARTICIPATION OF IMEG. ©2026 IMEG CONSULTANTS CORP.

REF. SCALE IN INCHES
PROJECT #25004064.00

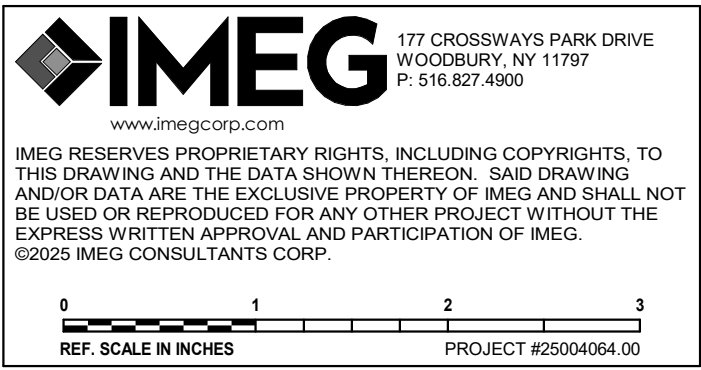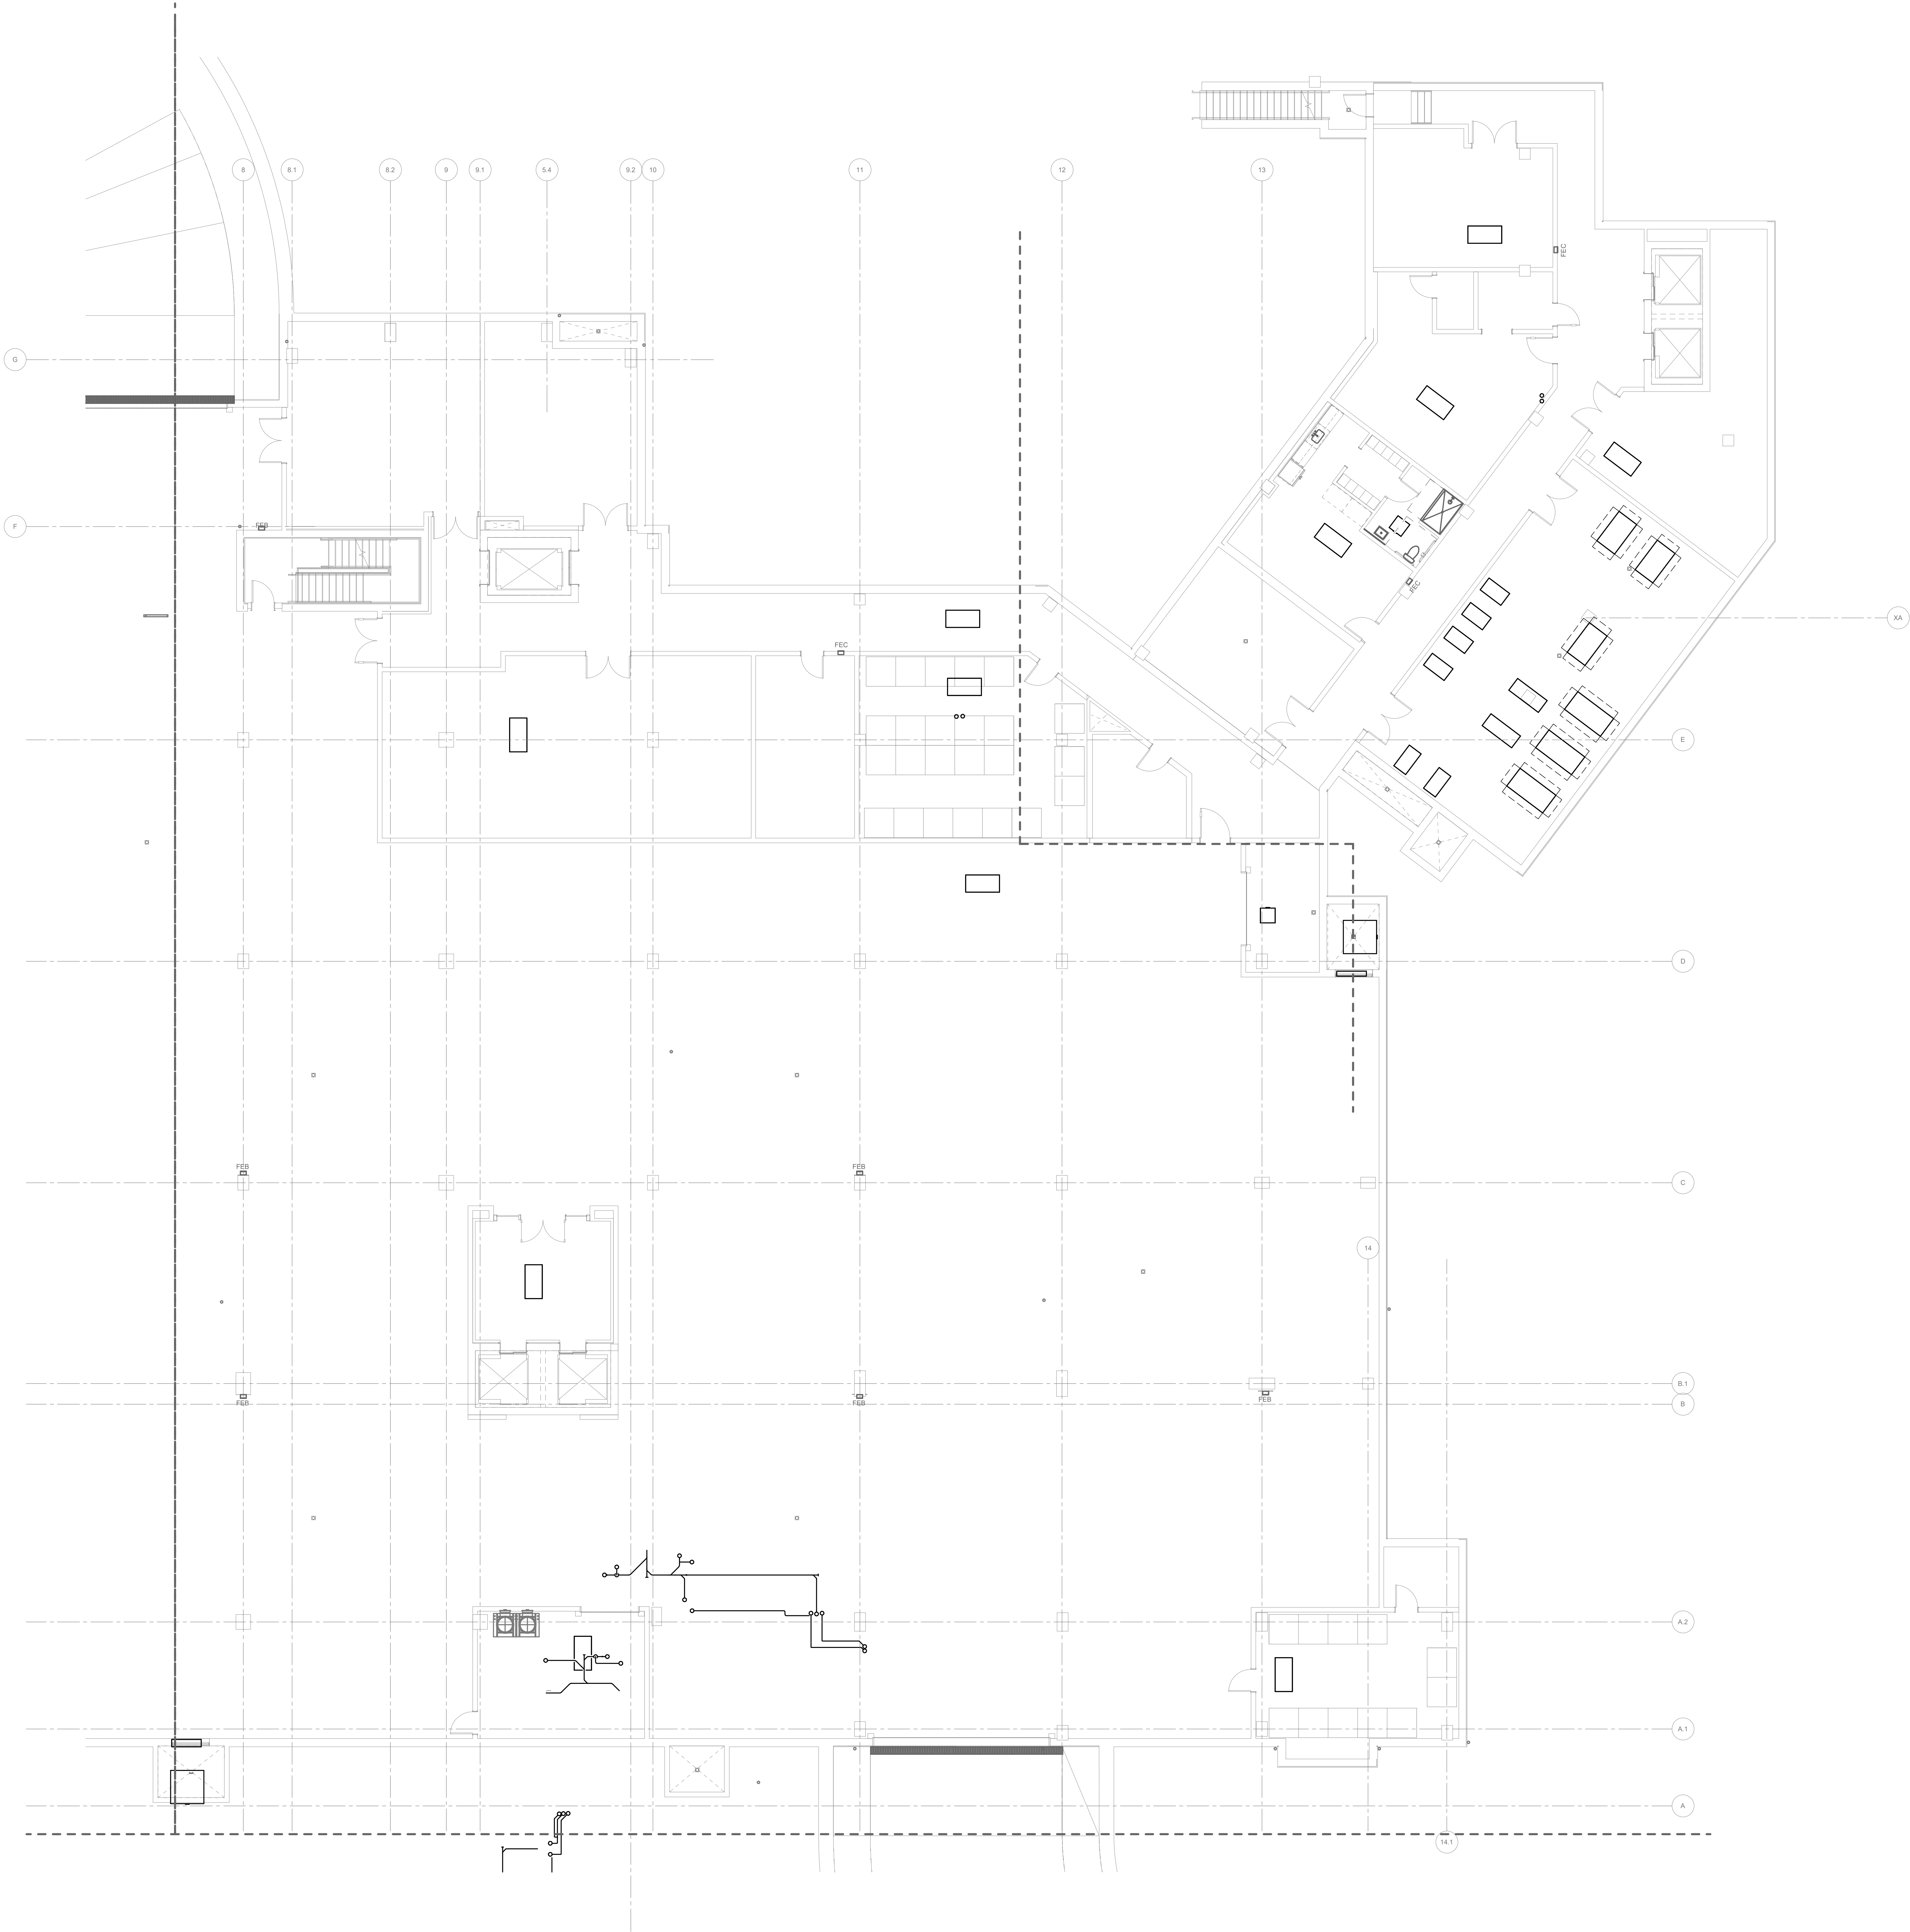

HKS

ARCHITECT
HKS ARCHITECTS, P.C.
30 WEST 26th STREET, 12th FLOOR
NEW YORK, NY 10010

STRUCTURAL
IMEG
1411 BROADWAY, SUITE 600
NEW YORK, NY 10018

MEP ENGINEER
IMEG
177 CROSWAYS PARK DRIVE
WOODBURY, NY 11797

LV ENGINEER
TASERCO
7855 HICKORY FLAT HWY, SUITE 200
WOODSTOCK, GA 30188

LANDSCAPE ARCHITECT
MPFP
120 BROADWAY, 20TH FLOOR
NEW YORK, NY 10021

POOL DESIGNER
COUNSLMAN HUNSAKER & ASSOCIATES, INC.
12851 MANCHESTER ROAD, SUITE 120
ST. LOUIS, MO 63131


FOOD SERVICE & LAUNDRY
CLARK
2551 HORSESHOE RD.
LANCASTER, PA 17601



DOB BSCAN / DOB STAMP & SIGNATURES _____

SEAL & SIGNATURE _____

CON NO.: 111AAA
KEY PLAN _____

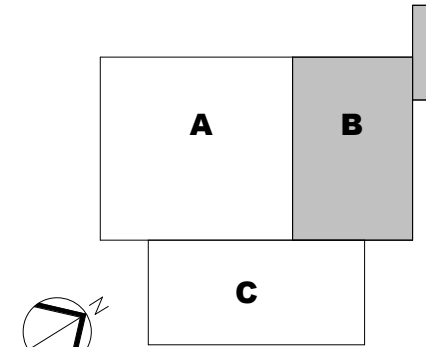


REVISION	
NO.	DESCRIPTION
1	DD Progress Print
2	DESIGN DEVELOPMENT
3	EXTERIOR BUILDING PERMIT
4	100% DESIGN DEVELOPMENT
5	ISSUED FOR PERMIT

HKS PROJECT NUMBER
25004064.00
DATE
07/15/26
ISSUE
ISSUED FOR GMP

SHEET TITLE
**ASSISTED LIVING
BASEMENT PLAN -
MECHANICAL PIPING**
SHEET NO.

M2003
DOB FILE # _____ DOB PAGE # _____

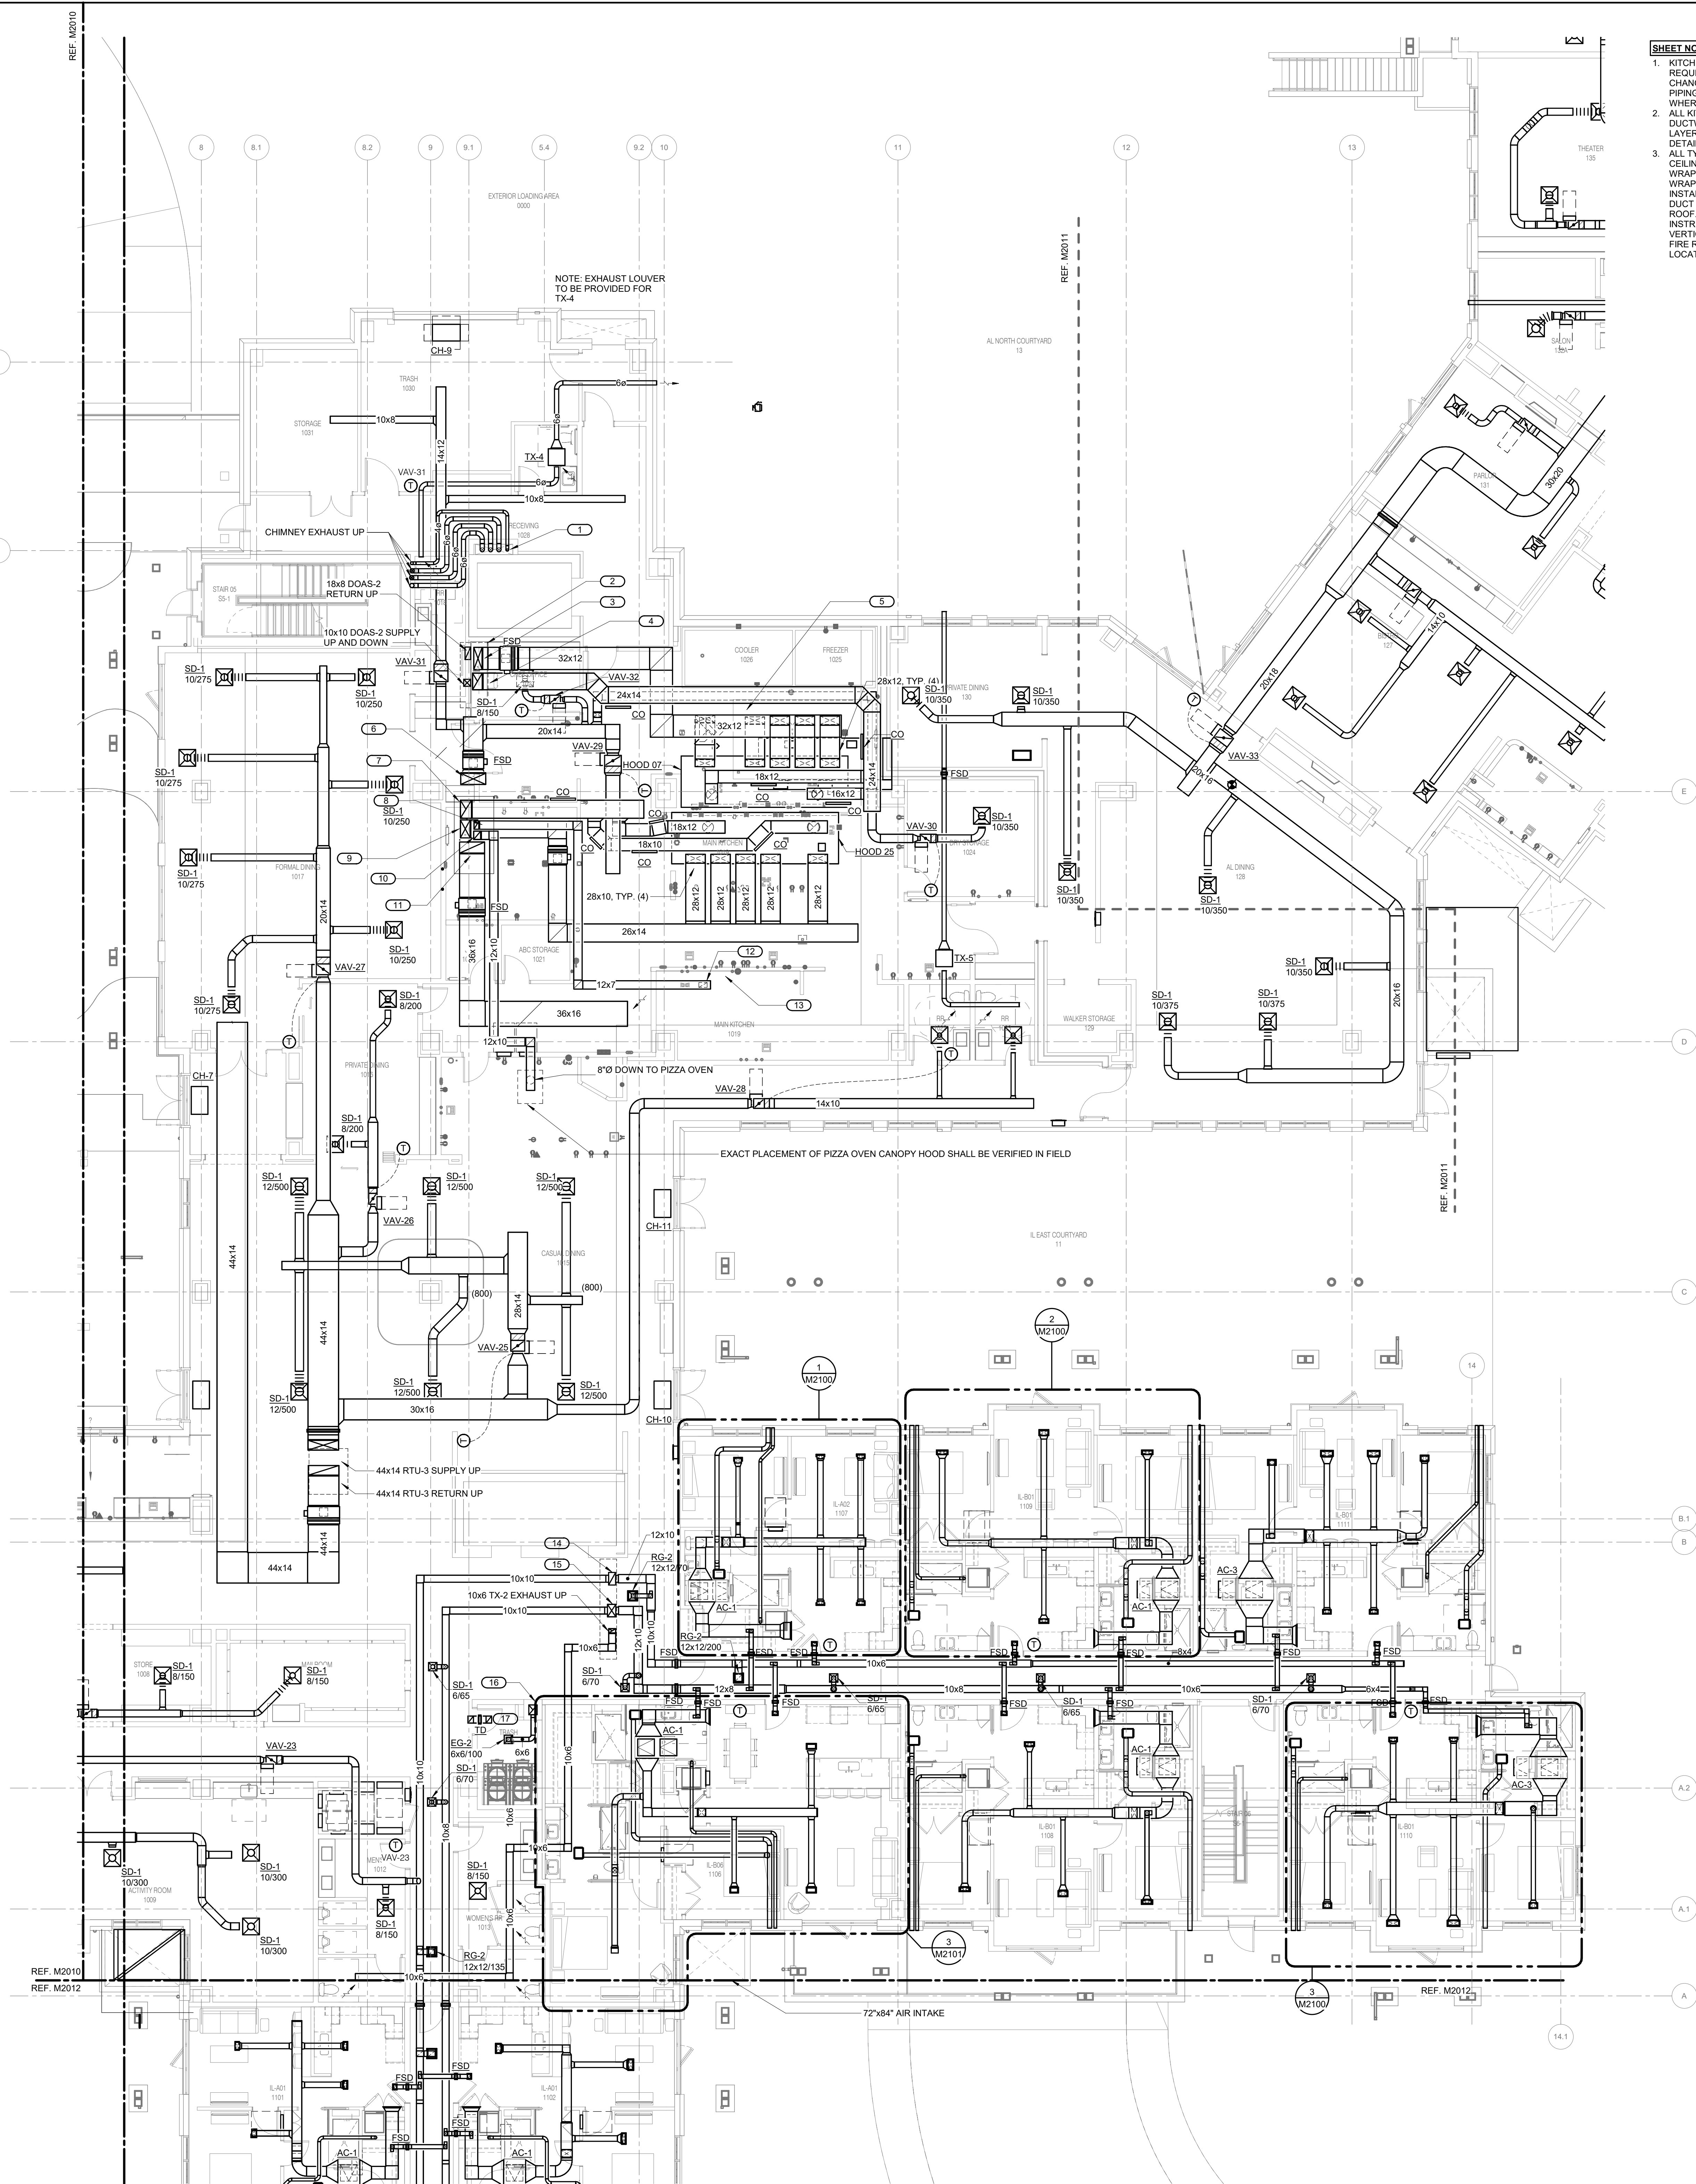

- | SEEK NOTES: |
|---|
| 1. KITCHEN HOOD GREASE EXHAUST DUCTS REQUIRE CLEAN OUT ACCESS DOORS AT EVERY CHANGE IN DIRECTION. THERE SHALL BE NO APPLICABLE CODES OR REGULATIONS THAT REQUIRE ACCESS DOORS BE PLACED. |
| 2. ALL KITCHEN HOOD GREASE EXHAUST DUCTWORK SHALL BE WRAPPED WITH (2) LAYERS OF MORGAN FAST WRAP, REFER TO DETAILS AND SPECIFICATIONS. |
| 3. ALL TYPE I GREASE EXHAUST DUCTWORK IN CEILING AND IN DUCT SHAFT SHALL BE WRAPPED WITH (2) LAYERS OF MORGAN FAST WRAP. FOLLOW MANUFACTURER'S INSTALLATION RECOMMENDATIONS ON GREASE EXHAUST DUCTWORK. ALL EXHAUST DUCTWORK INSIDE OF ROOF. FOLLOW MANUFACTURER'S INSTRUCTIONS FOR ACCESS DOORS IN VERTICAL DUCT SHAFTS. GC TO COORDINATE FIRE RATED ACCESS DOORS IN CORRIDOR LOCATIONS. |

- KEYNOTES:**
- 1. FIRE RATED CHIMNEY ENCLOSEURE REQUIRED FOR EXHAUST FROM KITCHEN DUCT INTO AIR IN CHASE TO DASH-4.
 - 2. OUTLINE OF DUCT SHIRT ABOVE.
 - 3. 32x12 SUPPLY AIR DUCT UP AND DOWN THROUGH CHASE TO DASH-4 CHASE TO DASH-4 PROVIDE FSD WHERE DUCT LEAVES CHASE.
 - 4. 24x14 PROVIDE FSD UP AND DOWN (SERVING DASH-4) THROUGH CHASE TO DASH-4 PROVIDE FSD WHERE DUCT LEAVES CHASE.
 - 5. 18" CLEAR FOR CO ACCESS FOR A PERSON ON LOADER BELOW
 - 6. 36x14 SUPPLY AIR UP IN SHIRT
 - 7. 26x18 KITCHEN HOOD 25" AIR DUCT UP IN CHASE TO DASH-4
 - 8. 12x7 DISHWASHER EXHAUST UP IN SHIRT
 - 9. 12x10 SUPPLY AIR DUCT UP AND DOWN THROUGH CHASE TO DASH-4 PROVIDE FSD WHERE DUCT LEAVES CHASE
 - 10. 12x10 PIZZA OVEN EXHAUST UP IN SHIRT
 - 11. 12x10 SUPPLY AIR DUCT UP AND DOWN THROUGH CHASE TO RTU-4.
 - 12. 12x10 SUPPLY AIR DUCT UP AND DOWN THROUGH CHASE TO DASH-4 PROVIDE FSD WHERE DUCT LEAVES CHASE
 - 13. 12x14 TRANSFER AIR DUCT UP IN SHIRT
 - 14. TRANSFER P/W TRANSFER AIR DUCT THROUGH CHASE TO RTU-4 FROM FIREZONE DAMPER AS REQUIRED

HKS

ARCHITECT
HKS ARCHITECTS, P.C.
30 WEST 26th STREET, 12th FLOOR
NEW YORK, NY 10010

STRUCTURAL
IMEG
1411 BROADWAY, SUITE 800
NEW YORK, NY 10018

MEP ENGINEER
IMEG
177 CROSSWAYS PARK DRIVE
WOODBURY, NY 11797

LV ENGINEER
TAZERGY
7653 HICKORY FLAT HWY, SUITE 200
WOODSTOCK, GA 30188

LANDSCAPE ARCHITECT
MPFP
120 BROADWAY, 20TH FLOOR
NEW YORK, NY 10271

POOL DESIGNER
COUNSILMAN-HUNSAKER & ASSOCIATES
12851 MANCHESTER ROAD, SUITE 120
ST. LOUIS, MO 63131


FOOD SERVICE & LAUNDRY
CLARK
2551 HORSESHOE RD.
LANCASTER, PA 17601



DOB BSCAN | DOB STAMP & SIGNATURE

SEAL & SIGNATURE _____

CON NO.: 111AAA
KEY PLAN _____

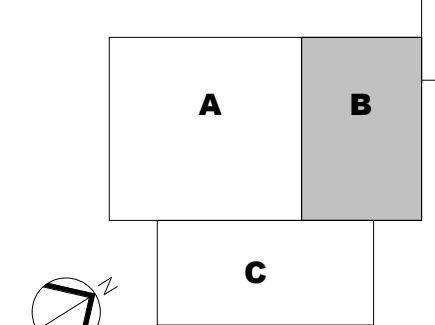

REVISION	
NO.	DESCRIPTION
1	DD Progress Print
2	DESIGN DEVELOPMENT
3	EXTERIOR BUILDING PERMIT
4	100% DESIGN DEVELOPMENT
5	ISSUED FOR PERMIT


HKS PROJECT NUMBER
25004064.00


DATE
07/15/26

ISSUE
ISSUED FOR GMP

SHEET TITLE
**INDEPENDENT LIV
FIRST FLOOR PLA
MECHANICAL IL A**


M2011

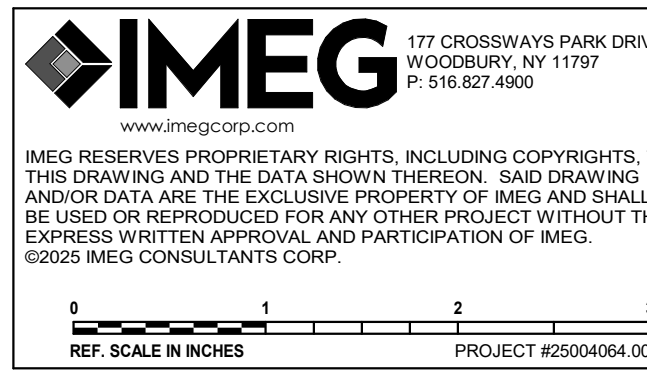

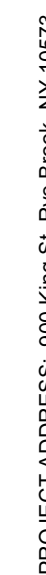 $1/8" = 1'-0"$ 

SEAL & SIGNATURE _____

CON NO.: 111AAA
KEY PLAN

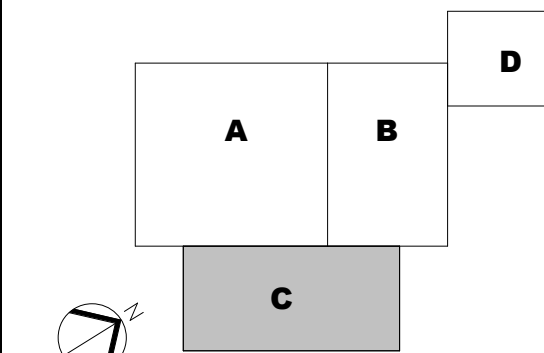


REVISION		
NO.	DESCRIPTION	DATE
1	DD Progress Print	08/26/25
2	DESIGN DEVELOPMENT	11/25/25
3	EXTERIOR BUILDING PERMIT	12/23/25
4	100% DESIGN DEVELOPMENT	01/30/26
5	ISSUED FOR PERMIT	06/05/26

INDEX

**FIRST FLOOR PLAN -
MECHANICAL AREA**

MECH
CHEET NO.

M3013

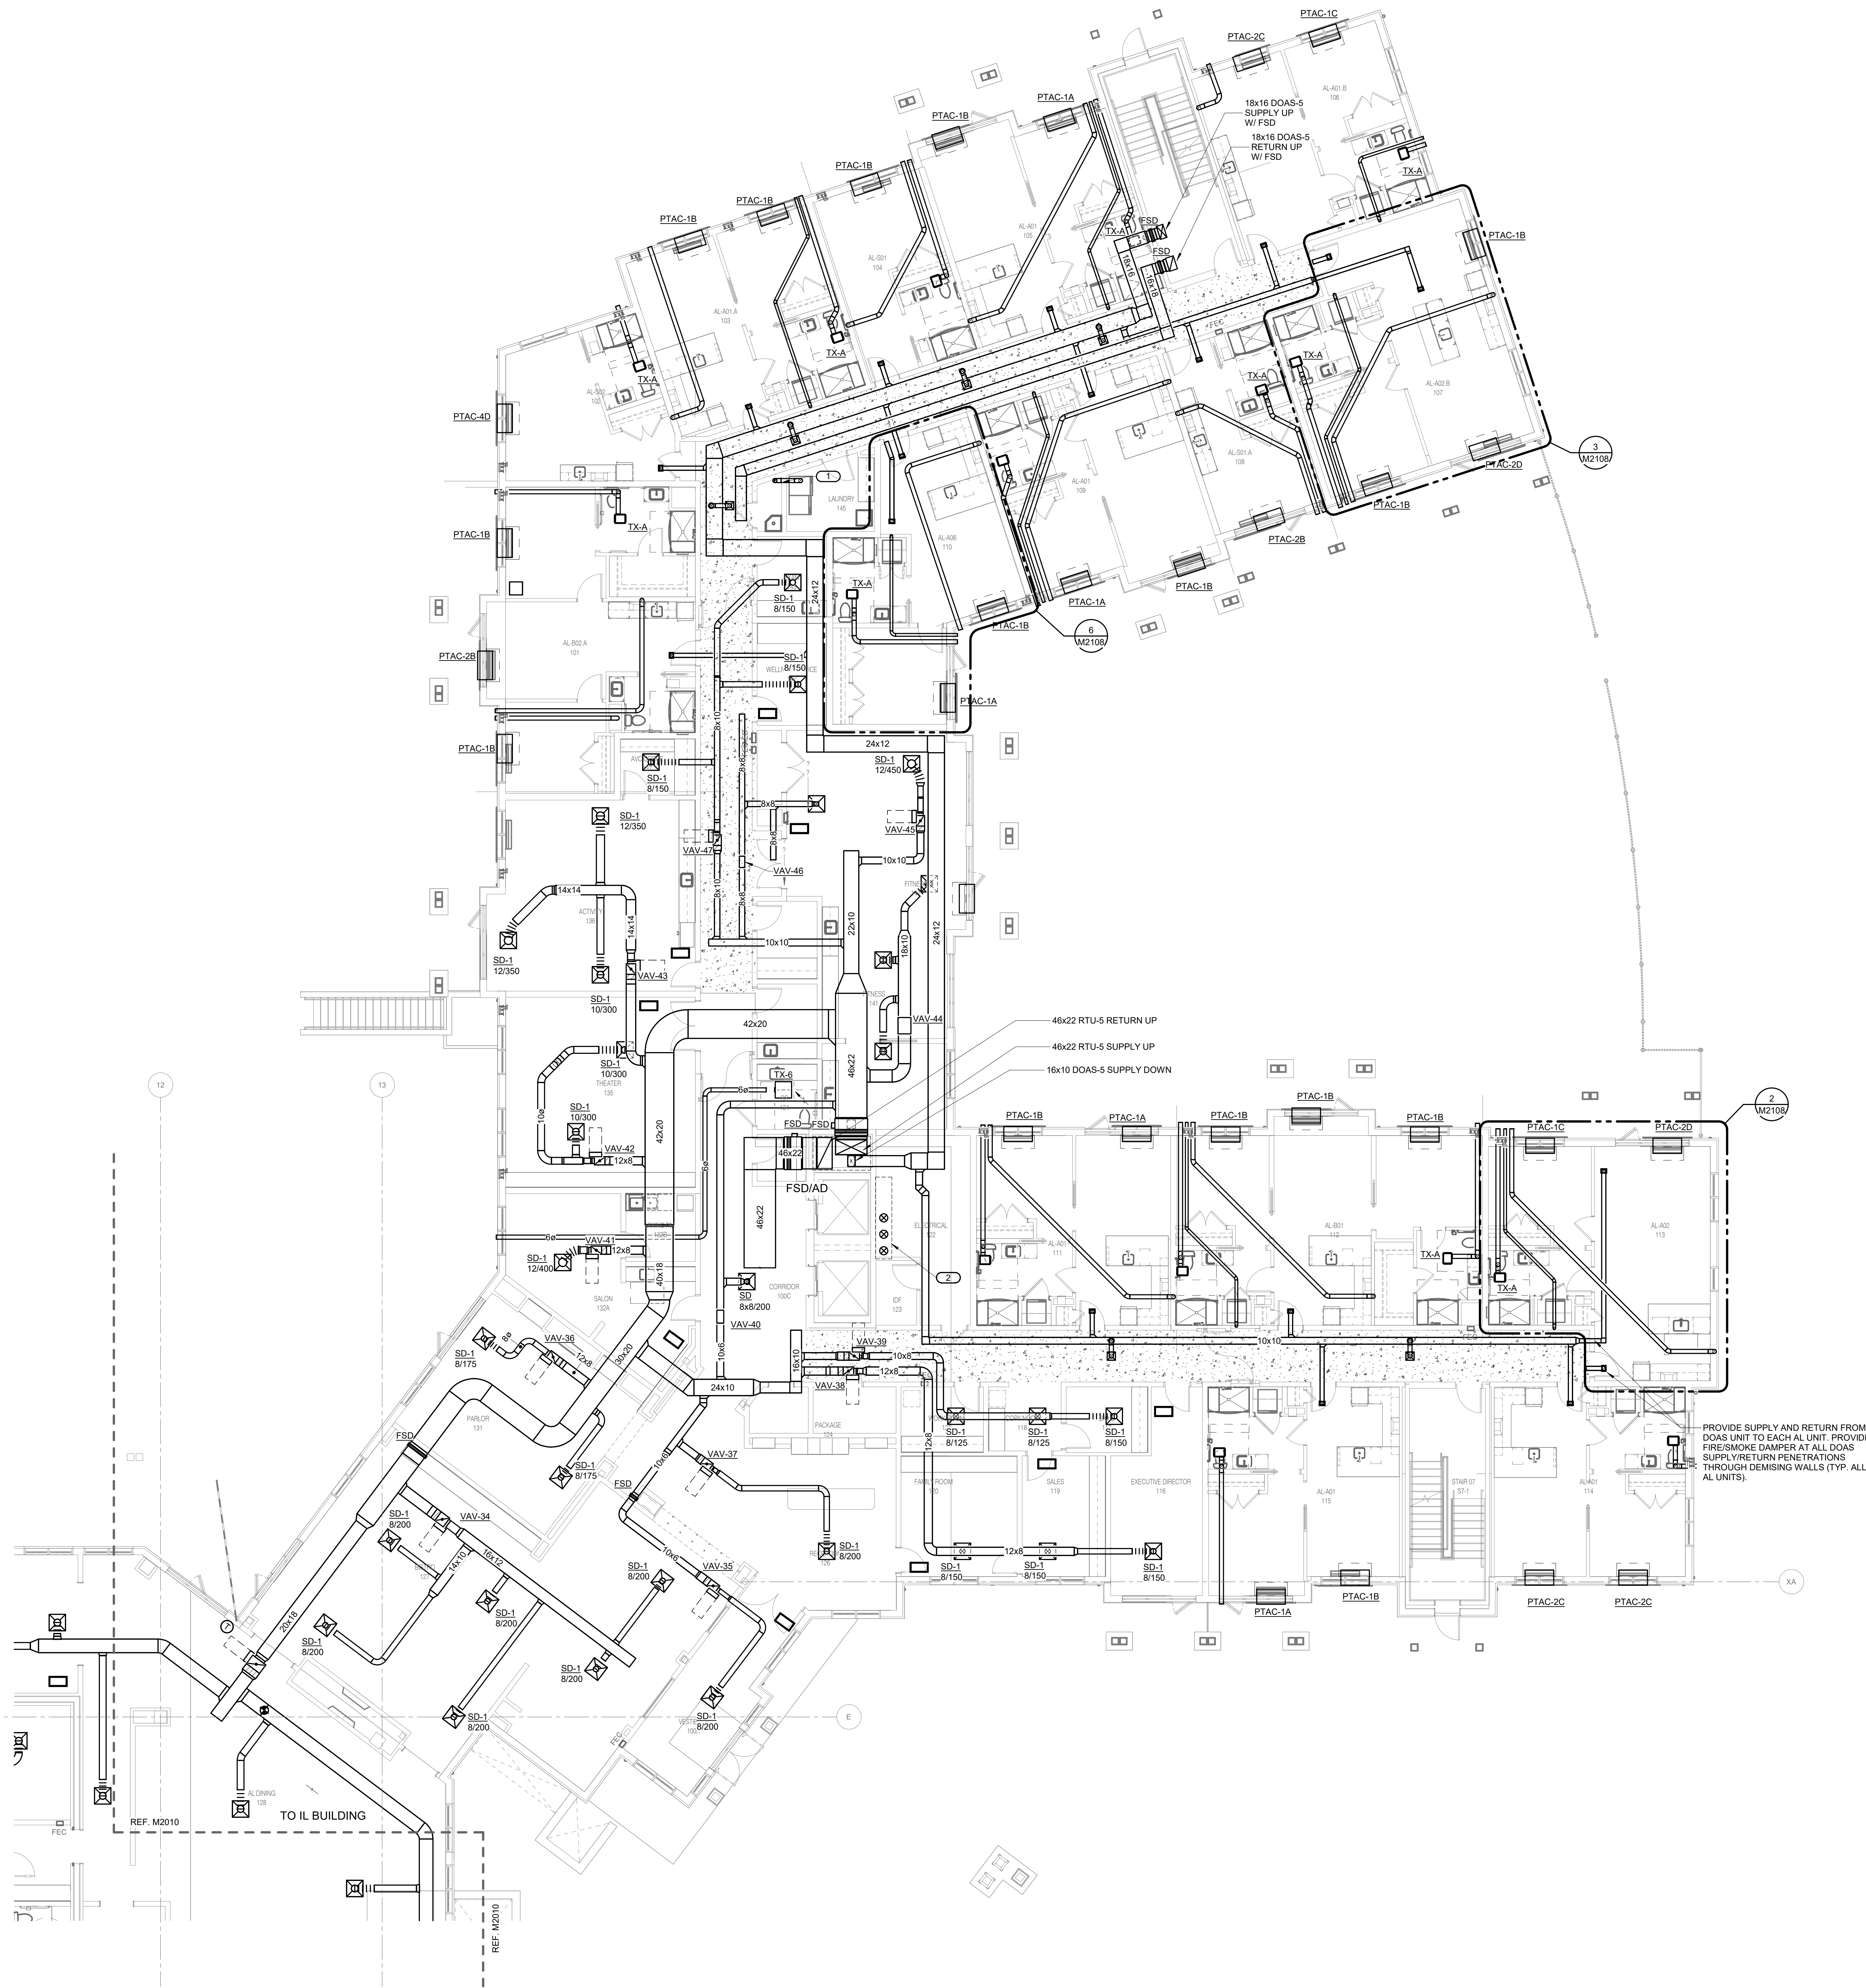


**1 INDEPENDENT LIVING FIRST FLOOR PLAN - MECHANICAL PIPING IL AREA A**

1/8" = 1'-0"

177 CROSWAYS PARK DRIVE
WOODBURY, NY 11797
P: 516-927-6900

IMEG RESERVES PROPRIETARY RIGHTS, INCLUDING COPYRIGHTS, TO THIS DRAWING AND THE DATA HEREIN THEREON. NO REPRODUCTION AND/OR DATA ARE THE EXCLUSIVE PROPERTY OF IMEG AND SHALL NOT BE USED OR REPRODUCED FOR ANY OTHER PROJECT WITHOUT THE EXPRESS WRITTEN APPROVAL AND PARTICIPATION OF IMEG. ©2016 IMEG CONSULTANTS CORP.

REF. SCALE IN INCHES PROJECT #20060406.00

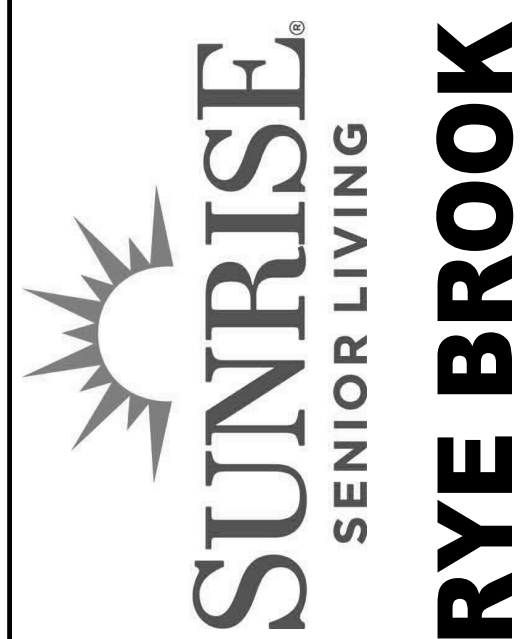HKS**ARCHITECT**
HKS ARCHITECTS, P.C.
30 WEST 26th STREET, 12th FLOOR
NEW YORK, NY 10010**STRUCTURAL**
IMEG
1411 BROADWAY, SUITE 600
NEW YORK, NY 10018**MEP ENGINEER**
IMEG
177 CROSWAYS PARK DRIVE
WOODBURY, NY 11797**LV ENGINEER**
TASERCO
7853 HICKORY FLAT HWY, SUITE 200
WOODSTOCK, GA 30188**LANDSCAPE ARCHITECT**
MPFP
120 BROADWAY, 20TH FLOOR
NEW YORK, NY 10021**POOL DESIGNER**
COUNSLMANHUNSAKER & ASSOCIATES, INC.
12851 MANCHESTER ROAD, SUITE 120
ST. LOUIS, MO 63131**FOOD SERVICE & LAUNDRY**
CLARK
2551 HORSESHOE RD.
LANCASTER, PA 17601


PROJECT ADDRESS: 300 Kings Rye Brook, NY 10573

DOB BSCAN | DOB STAMP & SIGNATURES

SEAL & SIGNATURE

CON NO.: 111AAA

KEY PLAN


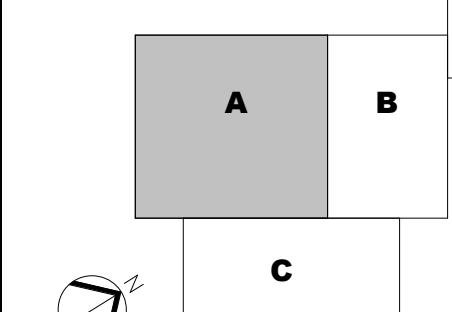


REVISION		
NO.	DESCRIPTION	DATE
1	DD Progress Print	08/26/25
2	DESIGN DEVELOPMENT	11/25/25
3	EXTERIOR BUILDING PERMIT	12/23/25
4	100% DESIGN DEVELOPMENT	01/30/26
5	ISSUED FOR PERMIT	06/05/26

HKS PROJECT NUMBER
25004064.00DATE
07/15/26ISSUE
ISSUED FOR GMPSHEET TITLE
**INDEPENDENT LIVING
FIRST FLOOR PLAN -
MECHANICAL PIPING IL
AREA A****M2014**

DOB FILE #

DOB PAGE #

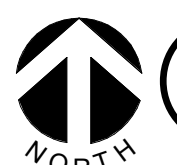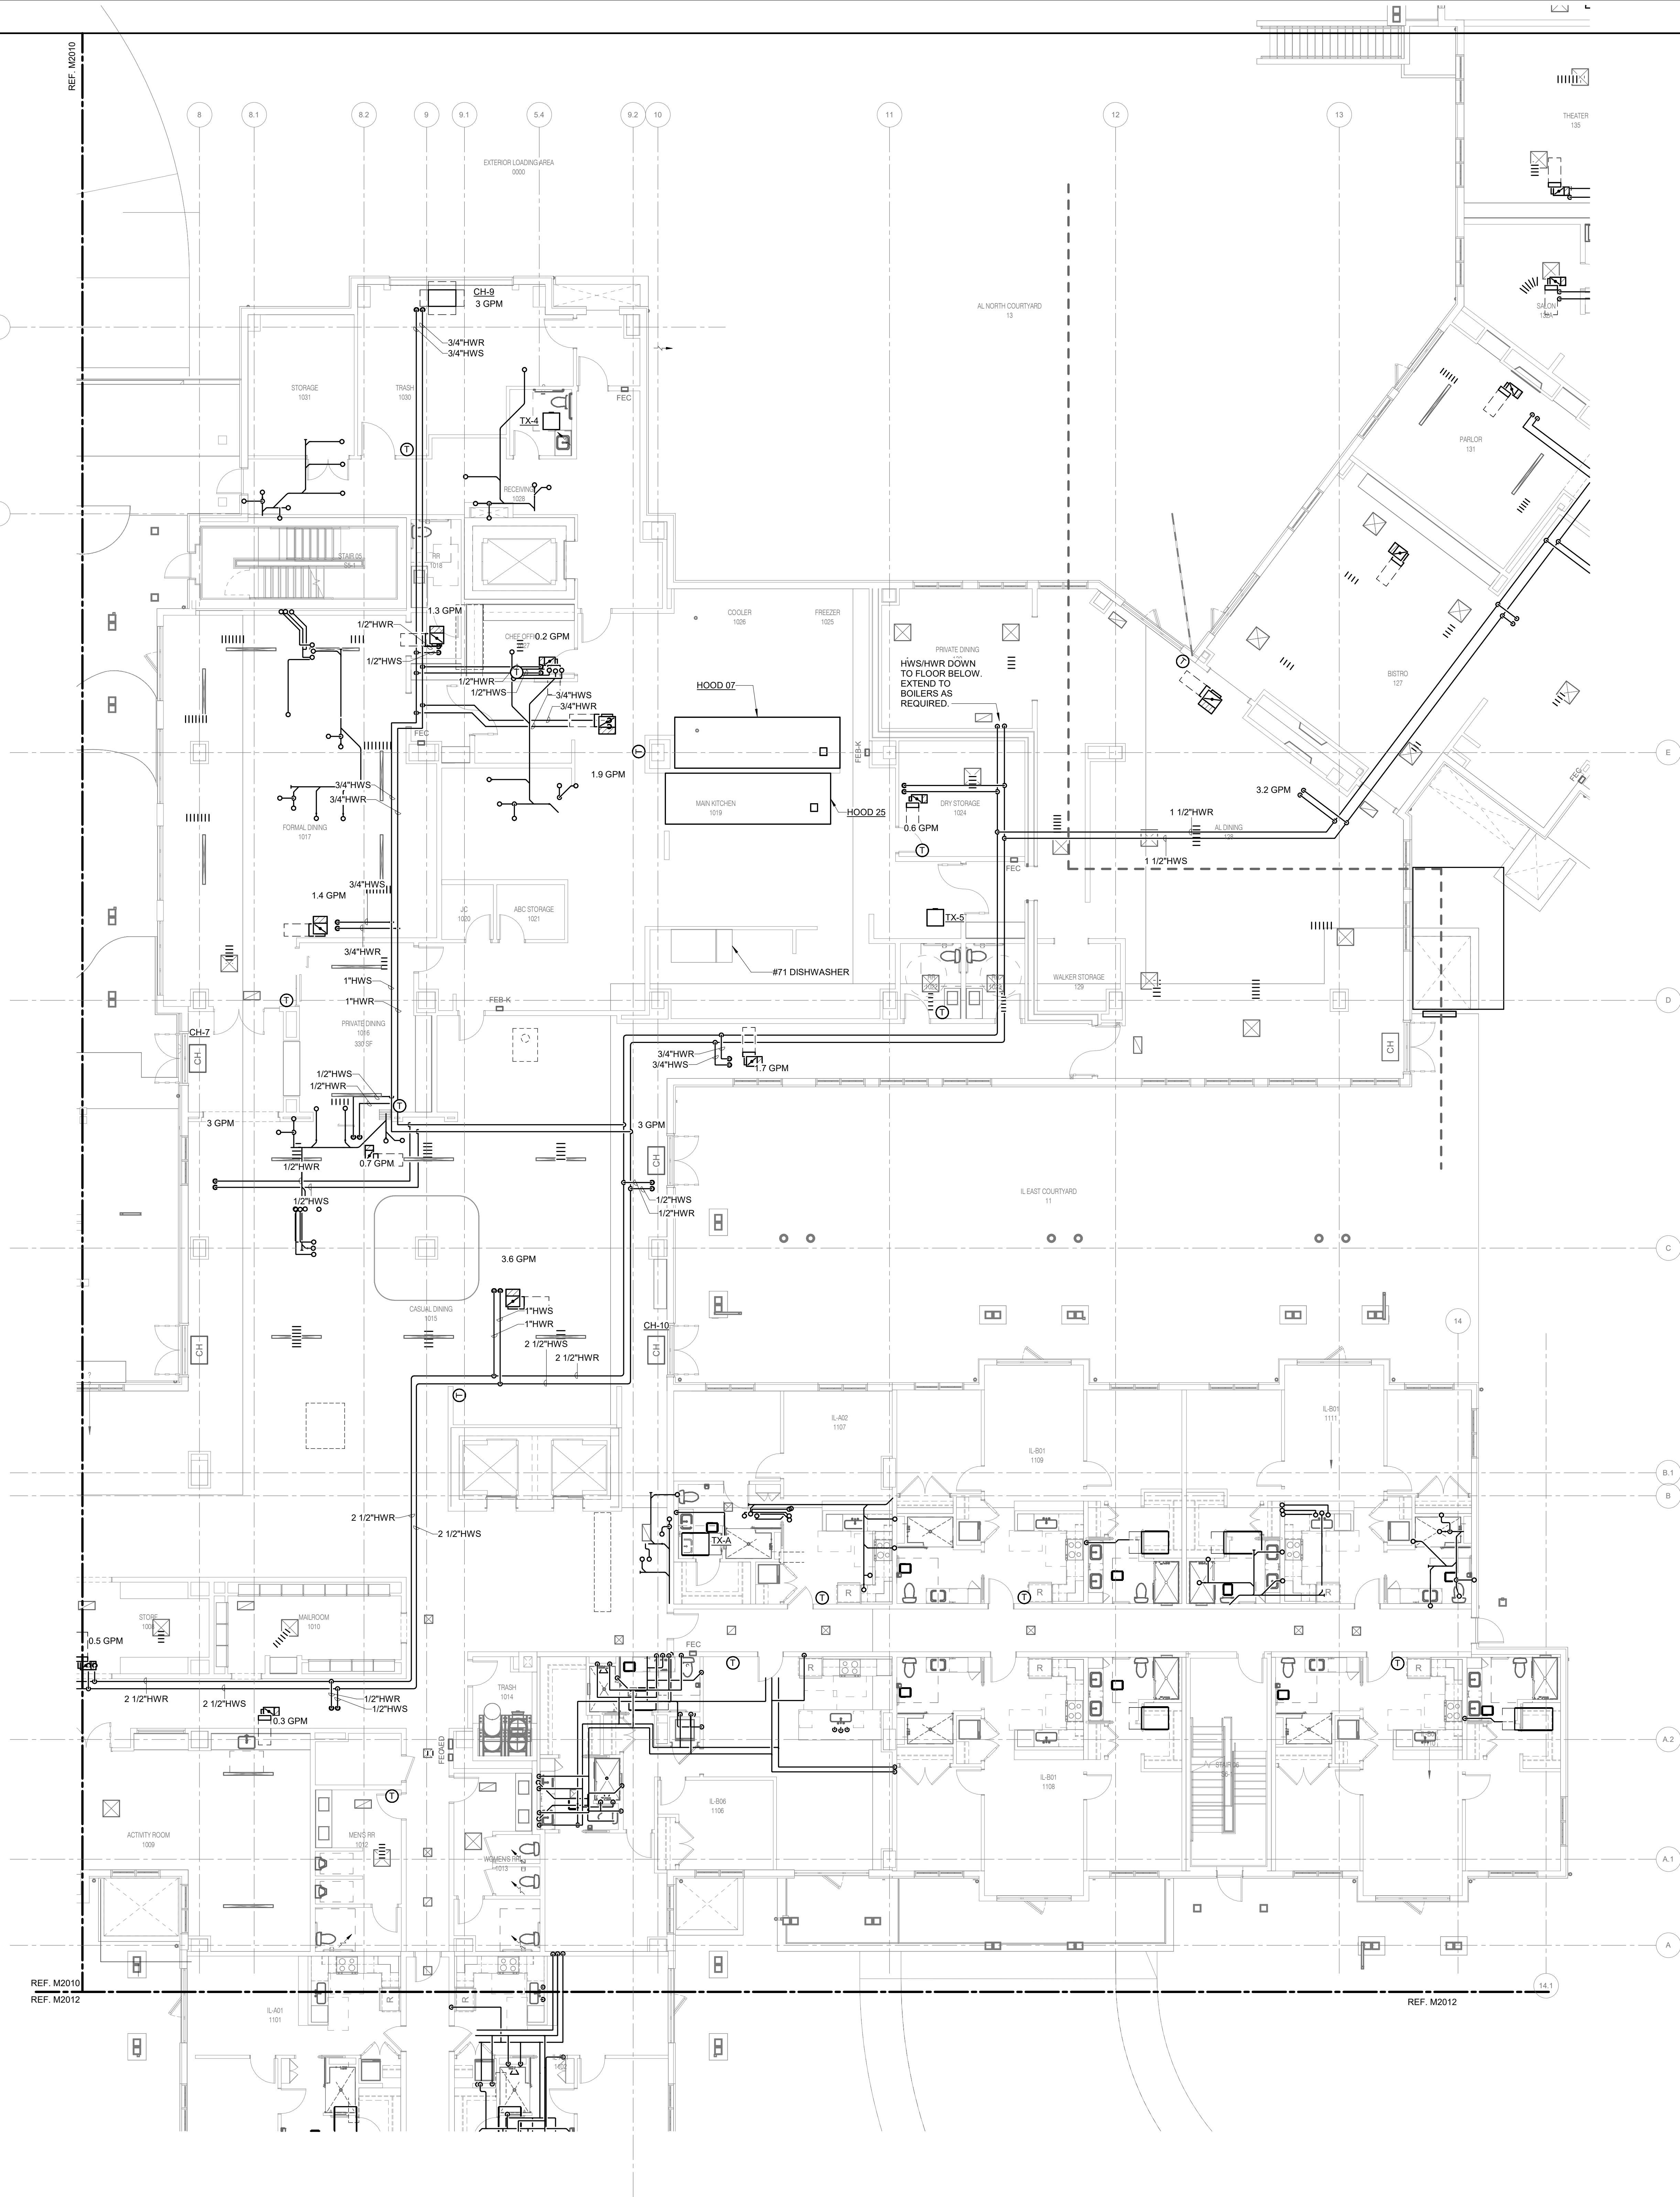

1

INDEPENDENT LIVING FIRST FLOOR PLAN - MECHANICAL PIPING IL AREA B

1/8" = 1'-0"



IMEG RESERVES PROPRIETARY RIGHTS, INCLUDING COPYRIGHTS, TO THE DRAWING AND THE DATA SHOWN HEREON. NO PART OF THIS DRAWING OR DATA AND THE EXCLUSIVE PROPERTY OF IMEG AND SHALL NOT BE USED OR REPRODUCED FOR ANY OTHER PROJECT WITHOUT THE EXPRESS WRITTEN APPROVAL AND PARTICIPATION OF IMEG. ©2020 IMEG CONSULTANTS CORP.

177 CROSSWAYS PARK DRIVE
WOODBURY, NY 11797
P: 516-827-4900

HKS

ARCHITECT
HKS ARCHITECTS, P.C.
30 WEST 26th STREET, 12th FLOOR
NEW YORK, NY 10010

STRUCTURAL
IMEG
1411 BROADWAY, SUITE 600
NEW YORK, NY 10018

MEP ENGINEER
IMEG
177 CROSSWAYS PARK DRIVE
WOODBURY, NY 11797

LV ENGINEER
TASERCO
785 HICKORY FLAT HWY, SUITE 200
WOODSTOCK, GA 30188

LANDSCAPE ARCHITECT
MFPF
120 BROADWAY, 20TH FLOOR
NEW YORK, NY 10071

POOL DESIGNER
COUNSLMAN-HUNSAKER & ASSOCIATES, INC.
12851 MANCHESTER ROAD, SUITE 120
ST. LOUIS, MO 63131

FOOD SERVICE & LAUNDRY
CLARK
2551 HORSESHOE RD.
LANCASTER, PA 17601

SUNRISE
SENIOR LIVING
RYE BROOK



RYE BROOK


PROJECT ADDRESS: 800 King St., Rye Brook, NY 10573

DOB.BSCAN | DOB STAMP & SIGNATURES

SEAL & SIGNATURE

CON NO.: 111AAA

KEY PLAN

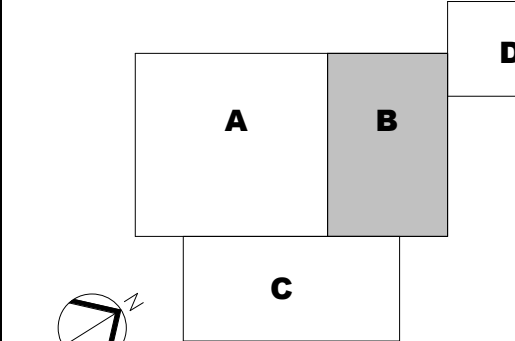


REVISION	
NO.	DESCRIPTION
1	DD Progress Print
2	DESIGN DEVELOPMENT
3	EXTERIOR BUILDING PERMIT
4	100% DESIGN DEVELOPMENT
5	ISSUED FOR PERMIT

HKS PROJECT NUMBER
25004064.00
DATE
07/15/26
ISSUE
ISSUED FOR GMP



SHEET TITLE
**INDEPENDENT LIVING
FIRST FLOOR PLAN -
MECHANICAL PIPING IL
AREA B**

M2015

DOB FILE # DOB PAGE #

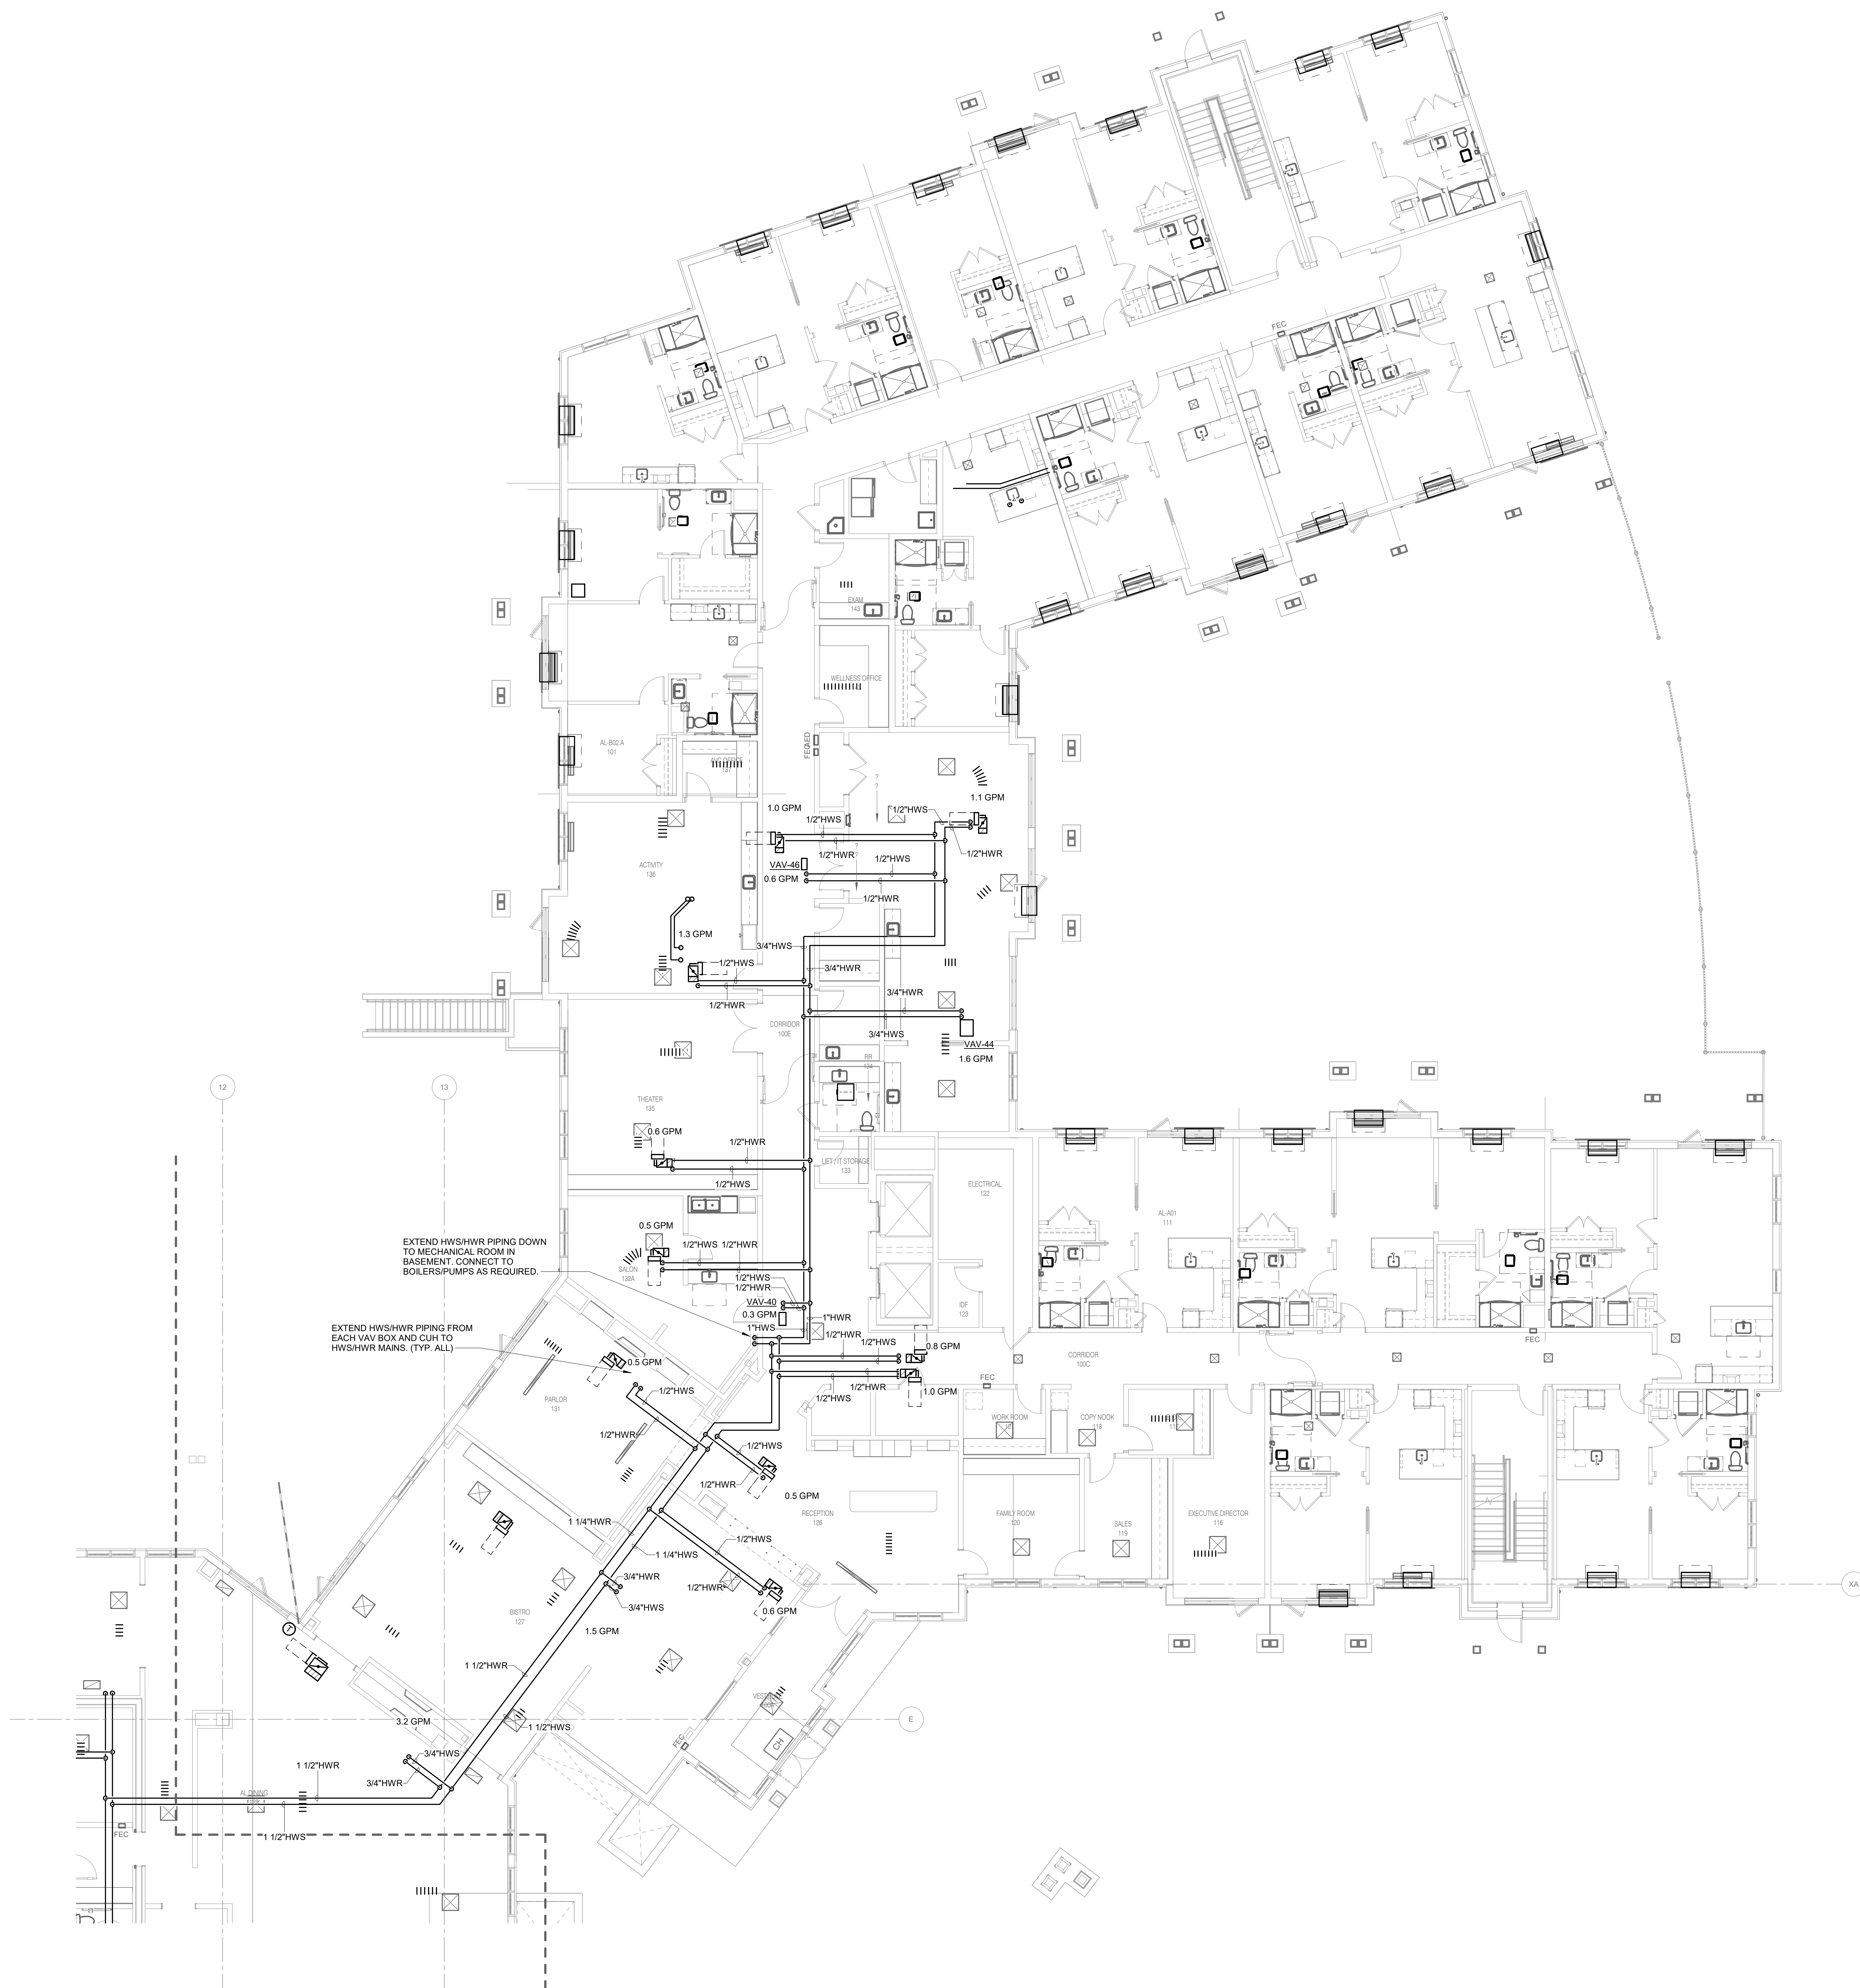


 **1** **ASSISTED LIVING FIRST FLOOR PLAN - MECHANICAL AL AREA D Copy 2**
1/8" = 1'-0"

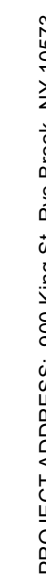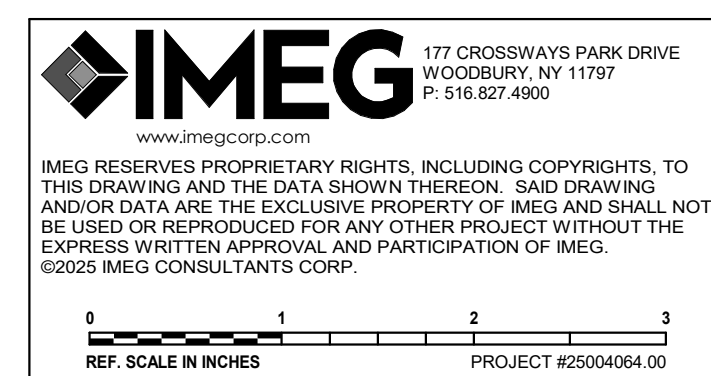

DOB BSCAN DCB STAMP & SIGNATURES

SEAL & SIGNATURE

CON NO.: 111AAA
KEY PLAN_____

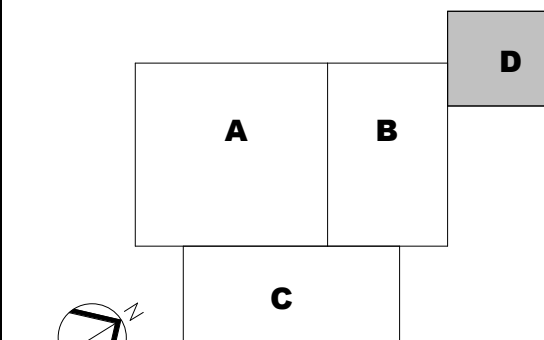

REVISION		
NO.	DESCRIPTION	DATE
1	DD Progress Print	08/26/25
2	DESIGN DEVELOPMENT	11/25/25
3	EXTERIOR BUILDING PERMIT	12/23/25
4	100% DESIGN DEVELOPMENT	01/30/26
5	ISSUED FOR PERMIT	06/05/26

HKS PROJECT NUMBER
25004064.00

DATE
07/15/26

ISSUE

ISS


SHEET TITLE

ASSIS

FIRST FLOOR PLAN - MECHANICAL RIDING

MECHANICAL AREA D

M2016

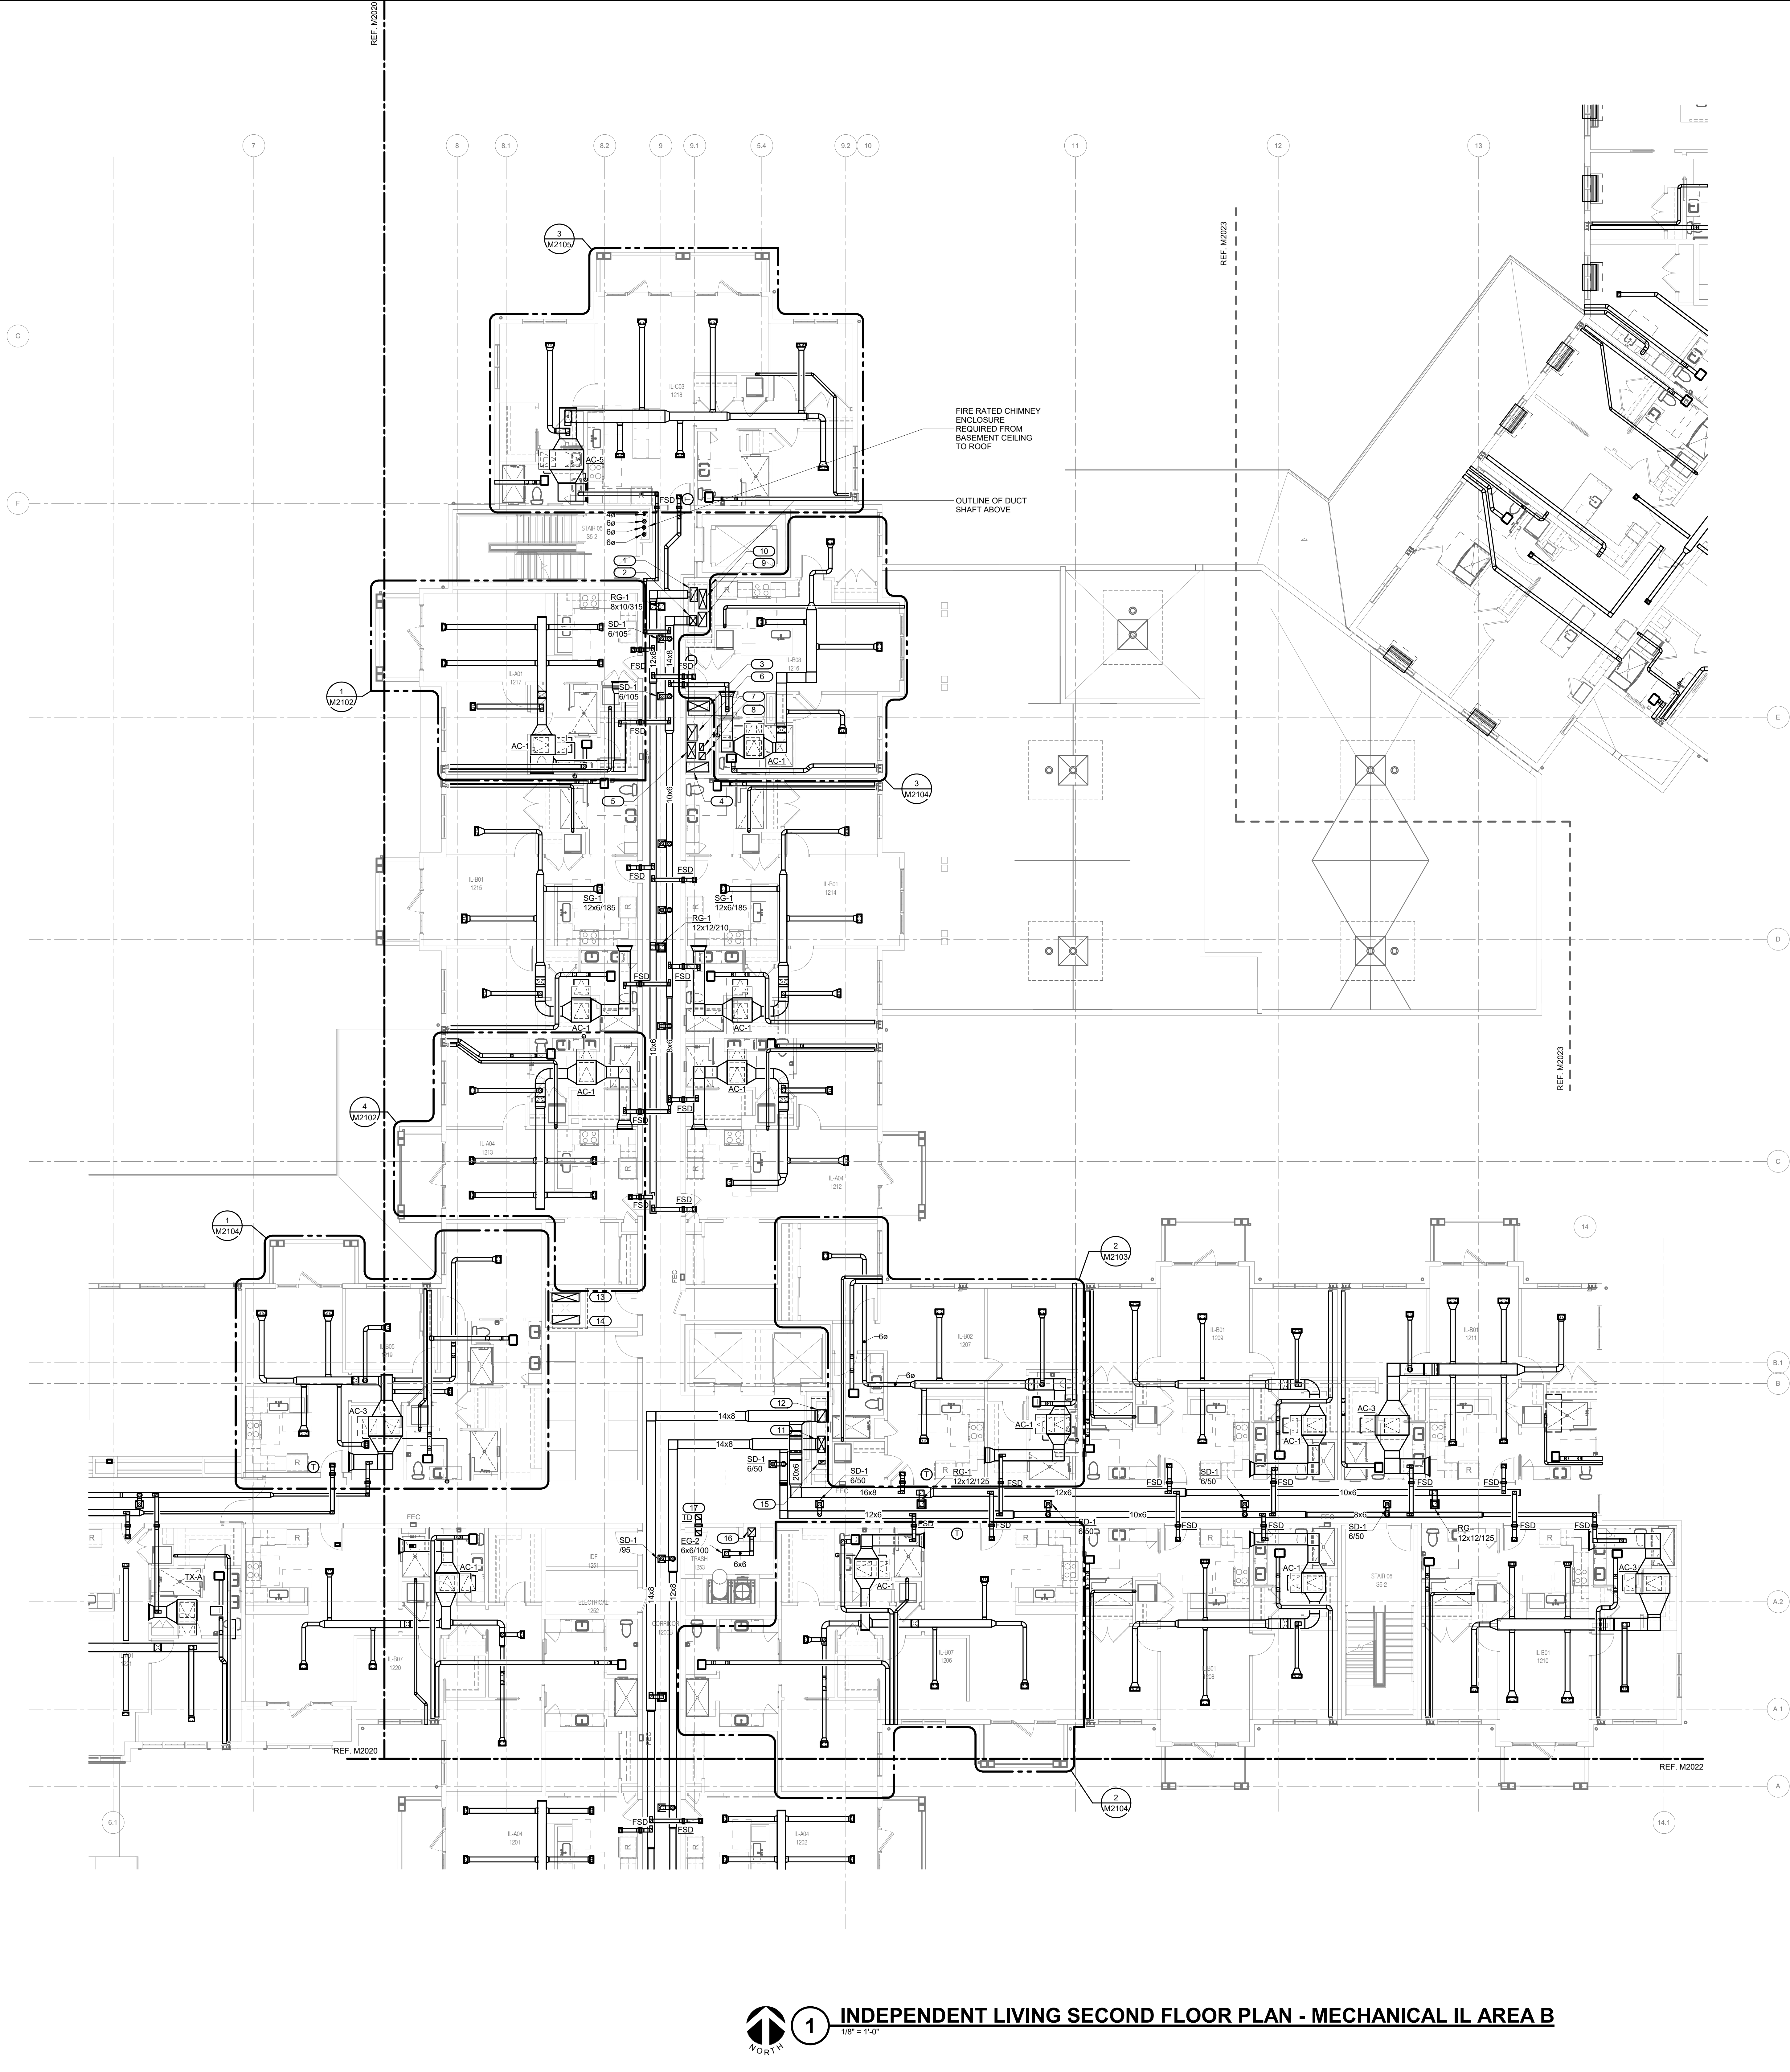

- KEYNOTES:**
- 18x12 SUPPLY AIR DUCT UP AND DOWN THROUGH CHASE TO DOAS-2.
 - 22x12 RETURN AIR DUCT UP AND DOWN THROUGH CHASE TO DOAS-2.
 - 36x16 SUPPLY AIR DUCT UP AND DOWN THROUGH CHASE TO RTU-4.
 - 36x16 RETURN AIR DUCT UP AND DOWN THROUGH CHASE TO RTU-4.
 - 26x14 SUPPLY AIR DUCT UP AND DOWN (SERVING KITCHEN HOOD) THROUGH CHASE TO DOAS-6. PROVIDE FSD WHERE DUCT LEAVES CHASE.
 - 26x16 GREASE DUCT UP AND DOWN (SERVING KITCHEN HOOD 25) IN CHASE.
 - 12x8 DISH WASHER EXHAUST AIR DUCT UP AND DOWN IN CHASE.
 - 12x10 PIZZA OVEN EXHAUST AIR DUCT UP AND DOWN IN CHASE.
 - 24x14 GREASE DUCT UP AND DOWN (SERVING KITCHEN HOOD 07) IN CHASE.
 - 32x12 SUPPLY AIR DUCT UP AND DOWN (SERVING KITCHEN HOOD) THROUGH CHASE TO DOAS-6. PROVIDE FSD AND ACCESS DOOR WHERE DUCT LEAVES CHASE.
 - 26x12 SUPPLY AIR DUCT UP AND DOWN THROUGH CHASE TO DOAS-4. PROVIDE FSD WHERE DUCT LEAVES CHASE.
 - 20x14 RETURN AIR DUCT UP AND DOWN THROUGH CHASE TO DOAS-4. PROVIDE FSD WHERE DUCT LEAVES CHASE.
 - 44x14 SUPPLY AIR DUCT UP AND DOWN THROUGH CHASE TO RTU-3.
 - 44x14 RETURN AIR DUCT UP AND DOWN THROUGH CHASE TO RTU-3.
 - 10x6 12x2 EXHAUST DUCT UP AND DOWN.
 - 12x14 TRASH EXHAUST UP AND DOWN IN SHAFT.
 - PROVIDE 6"x6" TRANSFER AIR DUCT THROUGH WALL WITH FIRE/SMOKE DAMPER AS REQUIRED.

HKS

ARCHITECT
HKS ARCHITECTS, P.C.
1411 BROADWAY, SUITE 600
NEW YORK, NY 10018

STRUCTURAL
IMEG
177 CROSSWAYS PARK DRIVE
WOODBURY, NY 11797

MEP ENGINEER
IMEG

LV ENGINEER
TATEROY
7853 HICKORY FLAT HWY, SUITE 200
WOODSTOCK, GA 30188

LANDSCAPE ARCHITECT
MPP
120 BROADWAY, 20TH FLOOR
NEW YORK, NY 10271

POOL DESIGNER
CONSELMAN HUNSAKER & ASSOCIATES, INC.
12851 MANCHESTER ROAD, SUITE 120
ST. LOUIS, MO 63131


FOOD SERVICE & LAUNDRY
CLARK
255 HORSESHOE RD.
LANCASTER, PA 17601

SUNRISE
SENIOR LIVING
RYE BROOK

DOB BSCAN L DOB STAMP & SIGNATURES

SEAL & SIGNATURE

CDN NO.: 111AAA
KEY PLAN

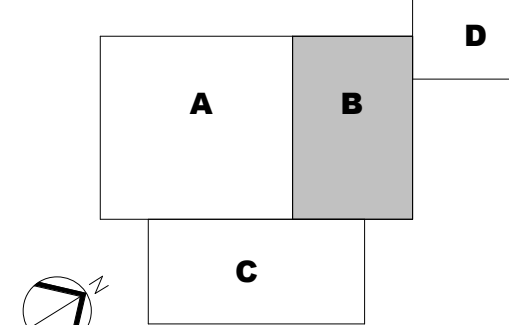

REVISION		
NO.	DESCRIPTION	DATE
1	DD Progress Print	09/26/25
2	DESIGN DEVELOPMENT	11/25/25
3	EXTERIOR BUILDING PERMIT	12/25/25
4	100% DESIGN DEVELOPMENT	01/30/26
5	ISSUED FOR PERMIT	06/05/26


HKS PROJECT NUMBER
25004064.00

DATE
07/15/26


ISSUE
ISSUED FOR GMP

SHEET TITLE
**INDEPENDENT LIVING
SECOND FLOOR PLAN -
MECHANICAL IL AREA**

SHEET NO.
M2021

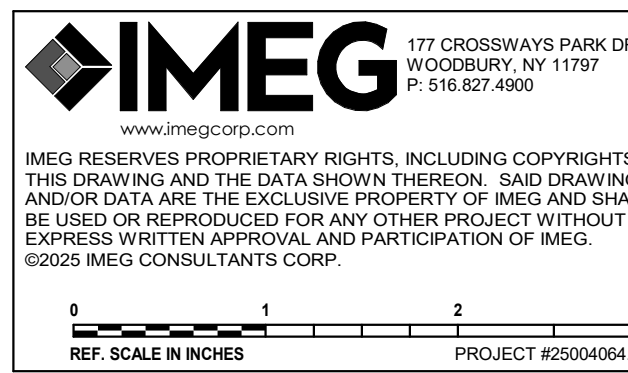


1 INDEPENDENT LIVING SECOND FLOOR PLAN - MECHANICAL IL AREA B

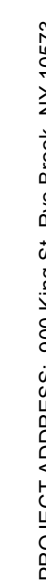

SEAL & SIGNATURE _____


CON NO.: 111AAA
KEY PLAN_____

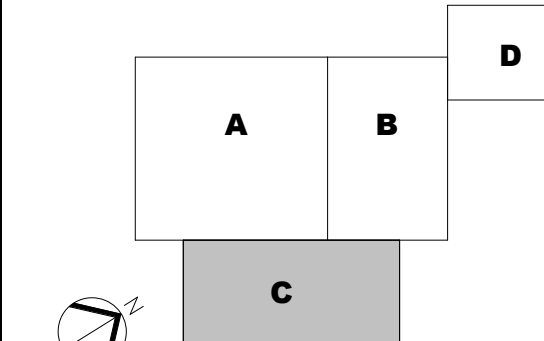

REVISION		
NO.	DESCRIPTION	DATE
1	DD Progress Print	08/26/25
2	DESIGN DEVELOPMENT	11/25/25
3	EXTERIOR BUILDING PERMIT	12/23/25
4	100% DESIGN DEVELOPMENT	01/30/26
5	ISSUED FOR PERMIT	06/05/26

MECH
C EET NO.

DOB FILE #: DOB PAGE #:

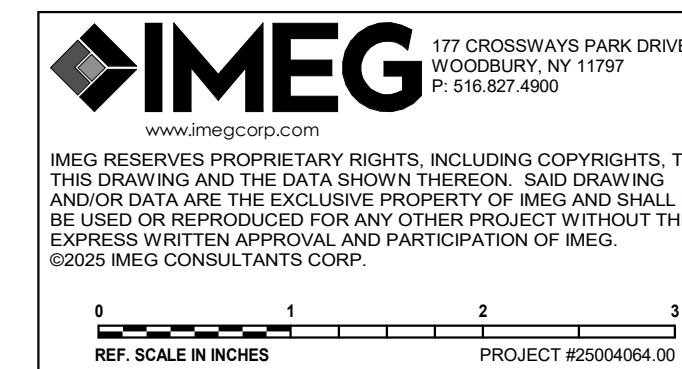



STRUCTURAL
IMEG
1411 BROADWAY, SUITE 600
NEW YORK, NY 10018

MEP ENGINEER
IMEG
177 CROSWAYS PARK DRIVE
WOODBURY, NY 11797

LV ENGINEER
TIZERGY
7653 HICKORY FAL HWY, SUITE 200
WOODSTOCK, GA 30188

LANDSCAPE ARCHITECT
MPPF
120 BROADWAY, 20TH FLOOR
NEW YORK, NY 10021


POOL DESIGNER
CONSULTEMAN HUNSEKER & ASSOCIATES
12651 MANCHESTER ROAD, SUITE 120
ST. LOUIS, MO 63131

CLAY SERVICE & LAUNDRY
CLARYK
2551 HORSESHOE RD.
LANCASTER, PA 17601

DOB BSCAN | DOB STAMP & SIGNATURES

SEAL & SIGNATURE

CON NO.: 111AAA
KEY PLAN _____

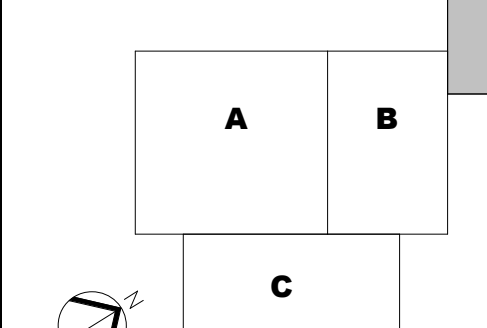

REVISION	
NO.	DESCRIPTION
1	DD Progress Print
2	DESIGN DEVELOPMENT
3	EXTERIOR BUILDING PERMIT
4	100% DESIGN DEVELOPMENT
5	ISSUED FOR PERMIT


HKS PROJECT NUMBER
25004064.00

DATE
07/15/26


ISSUE
ISSUED FOR GMP


SHEET TITLE
**ASSISTED LIVING
SECOND FLOOR PL.
MECHANICAL AL AL**
SHEET NO.

M2023

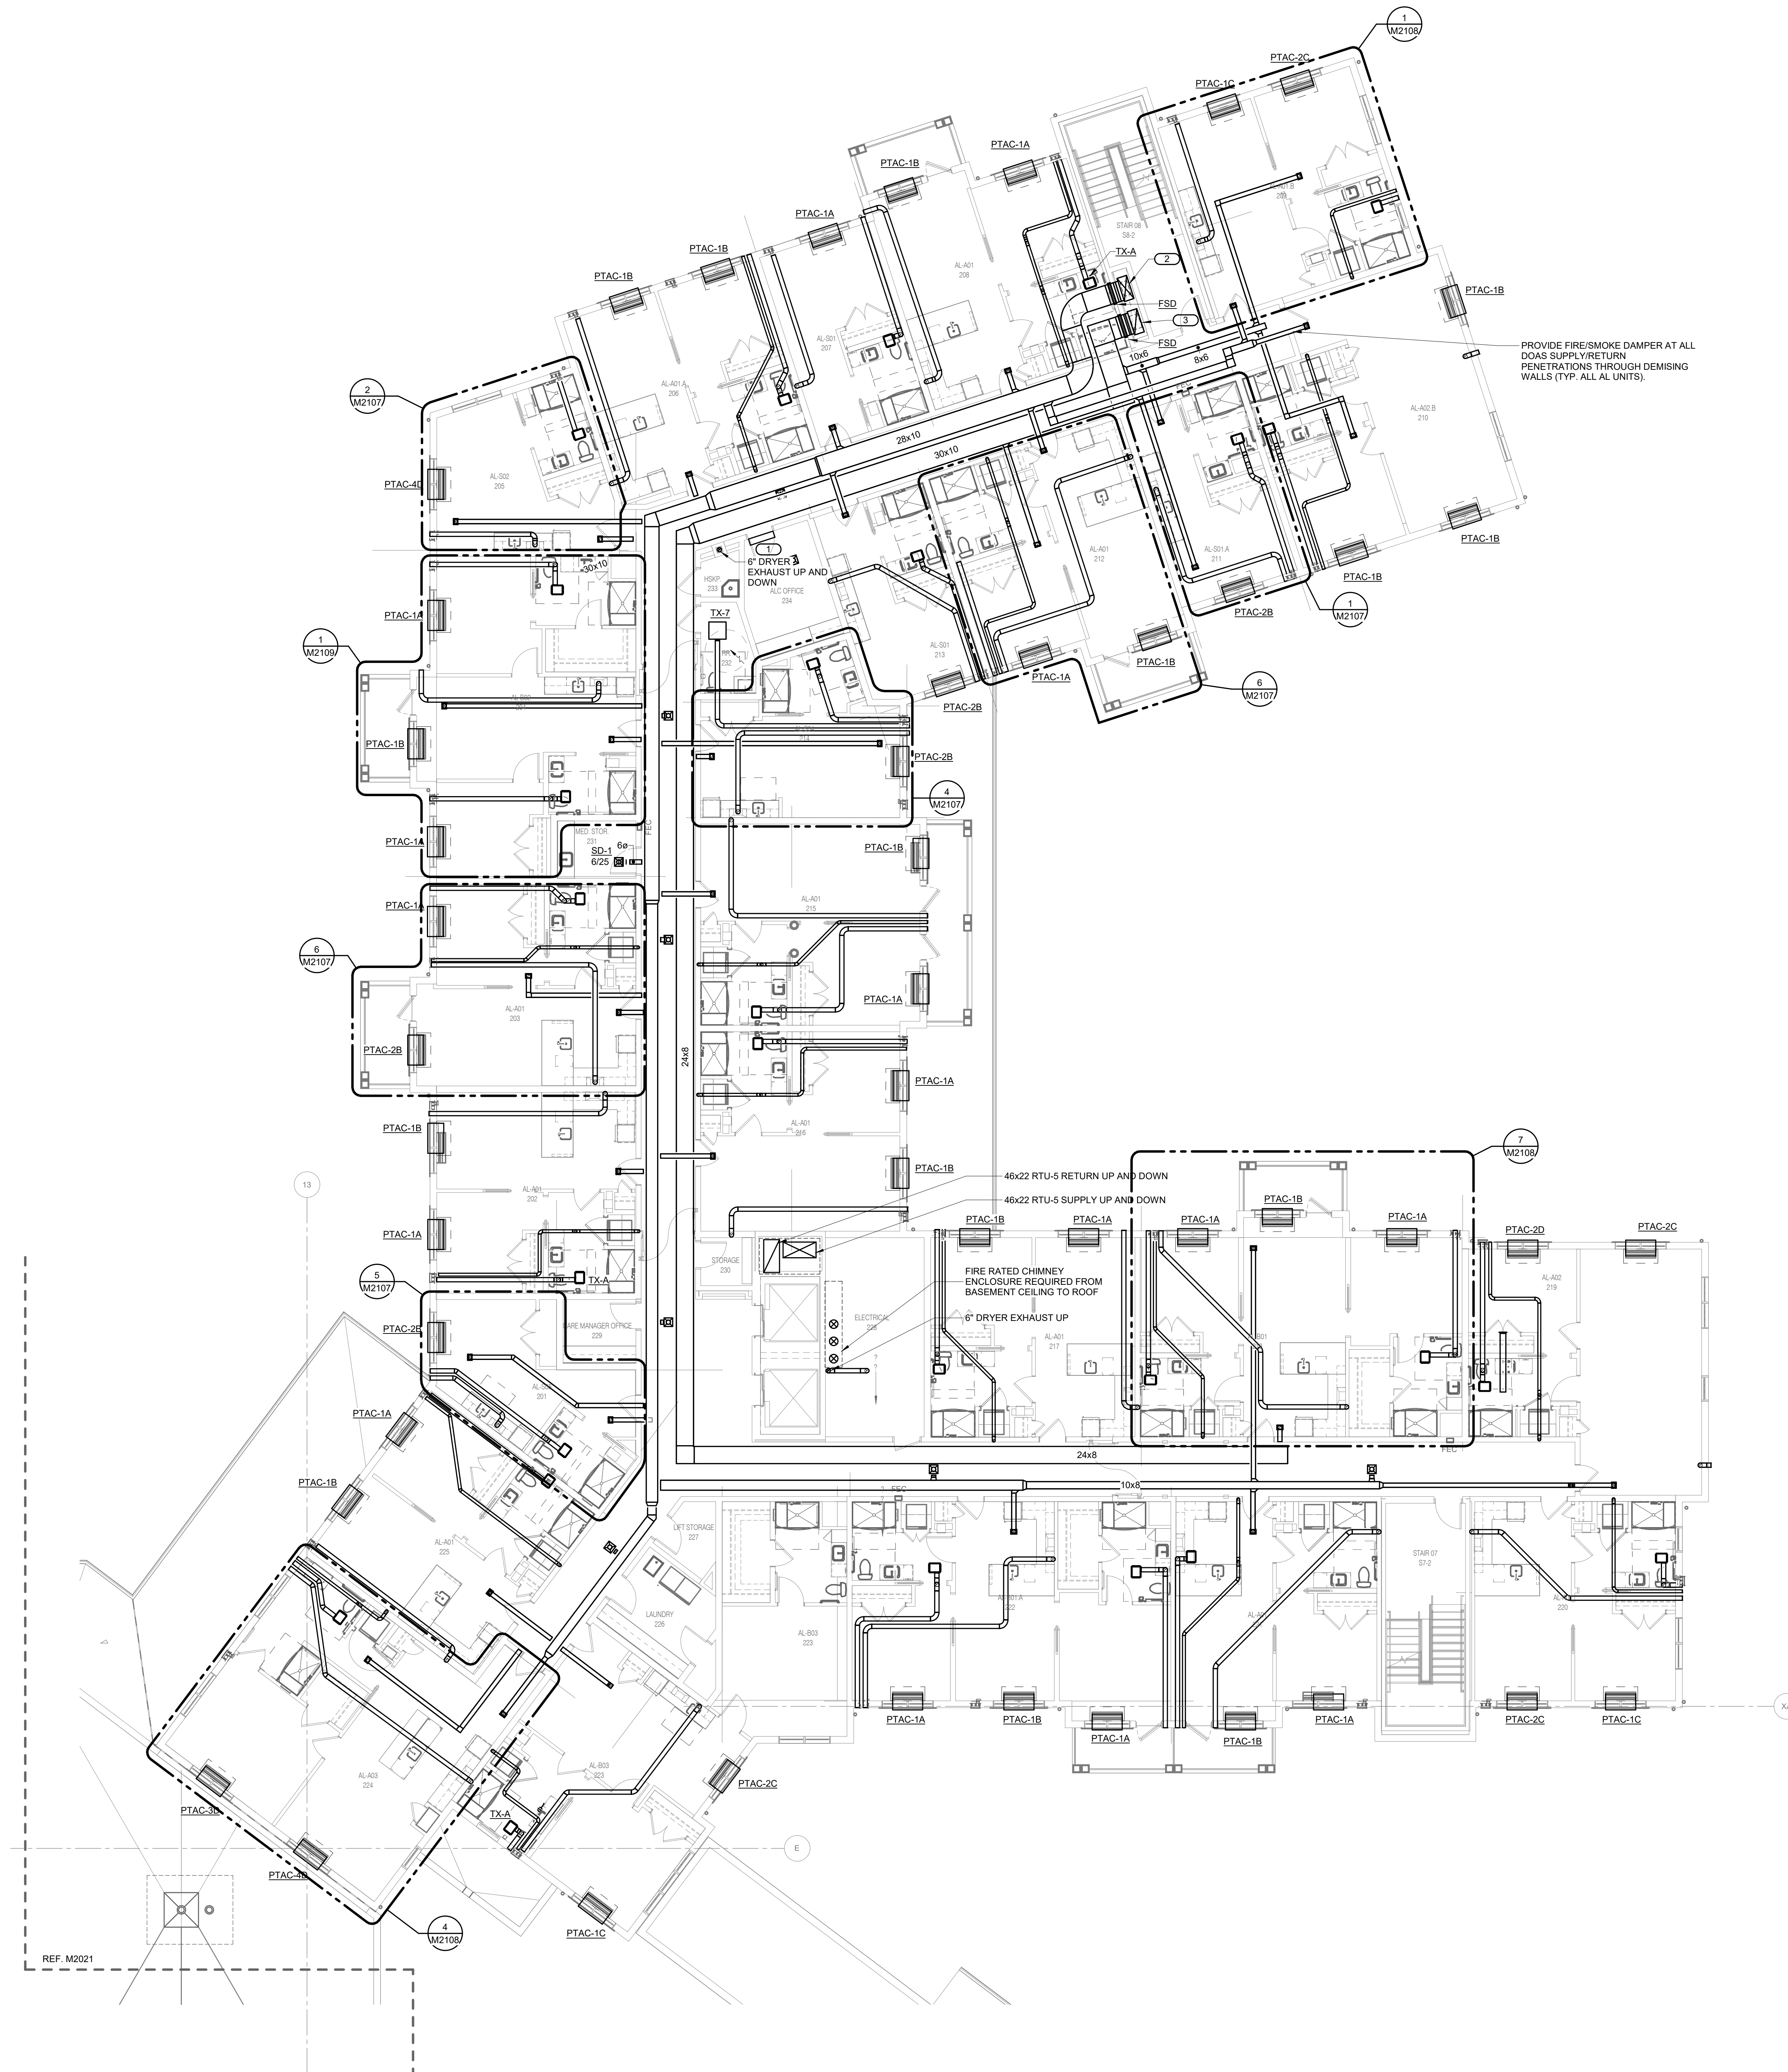

 1 **ASSISTED LIVING SECOND FLOOR PLAN - MECHANICAL AL AREA D**
1/8" = 1'-0"

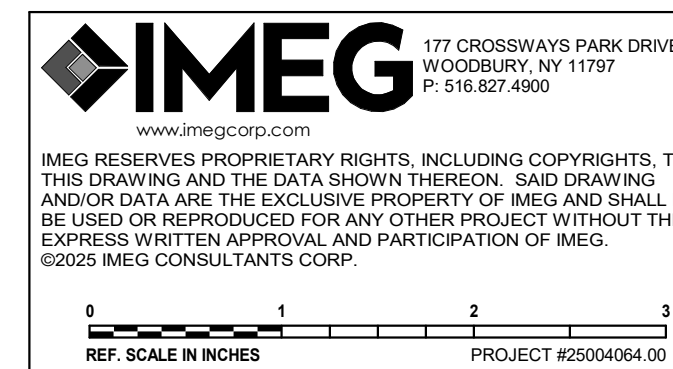

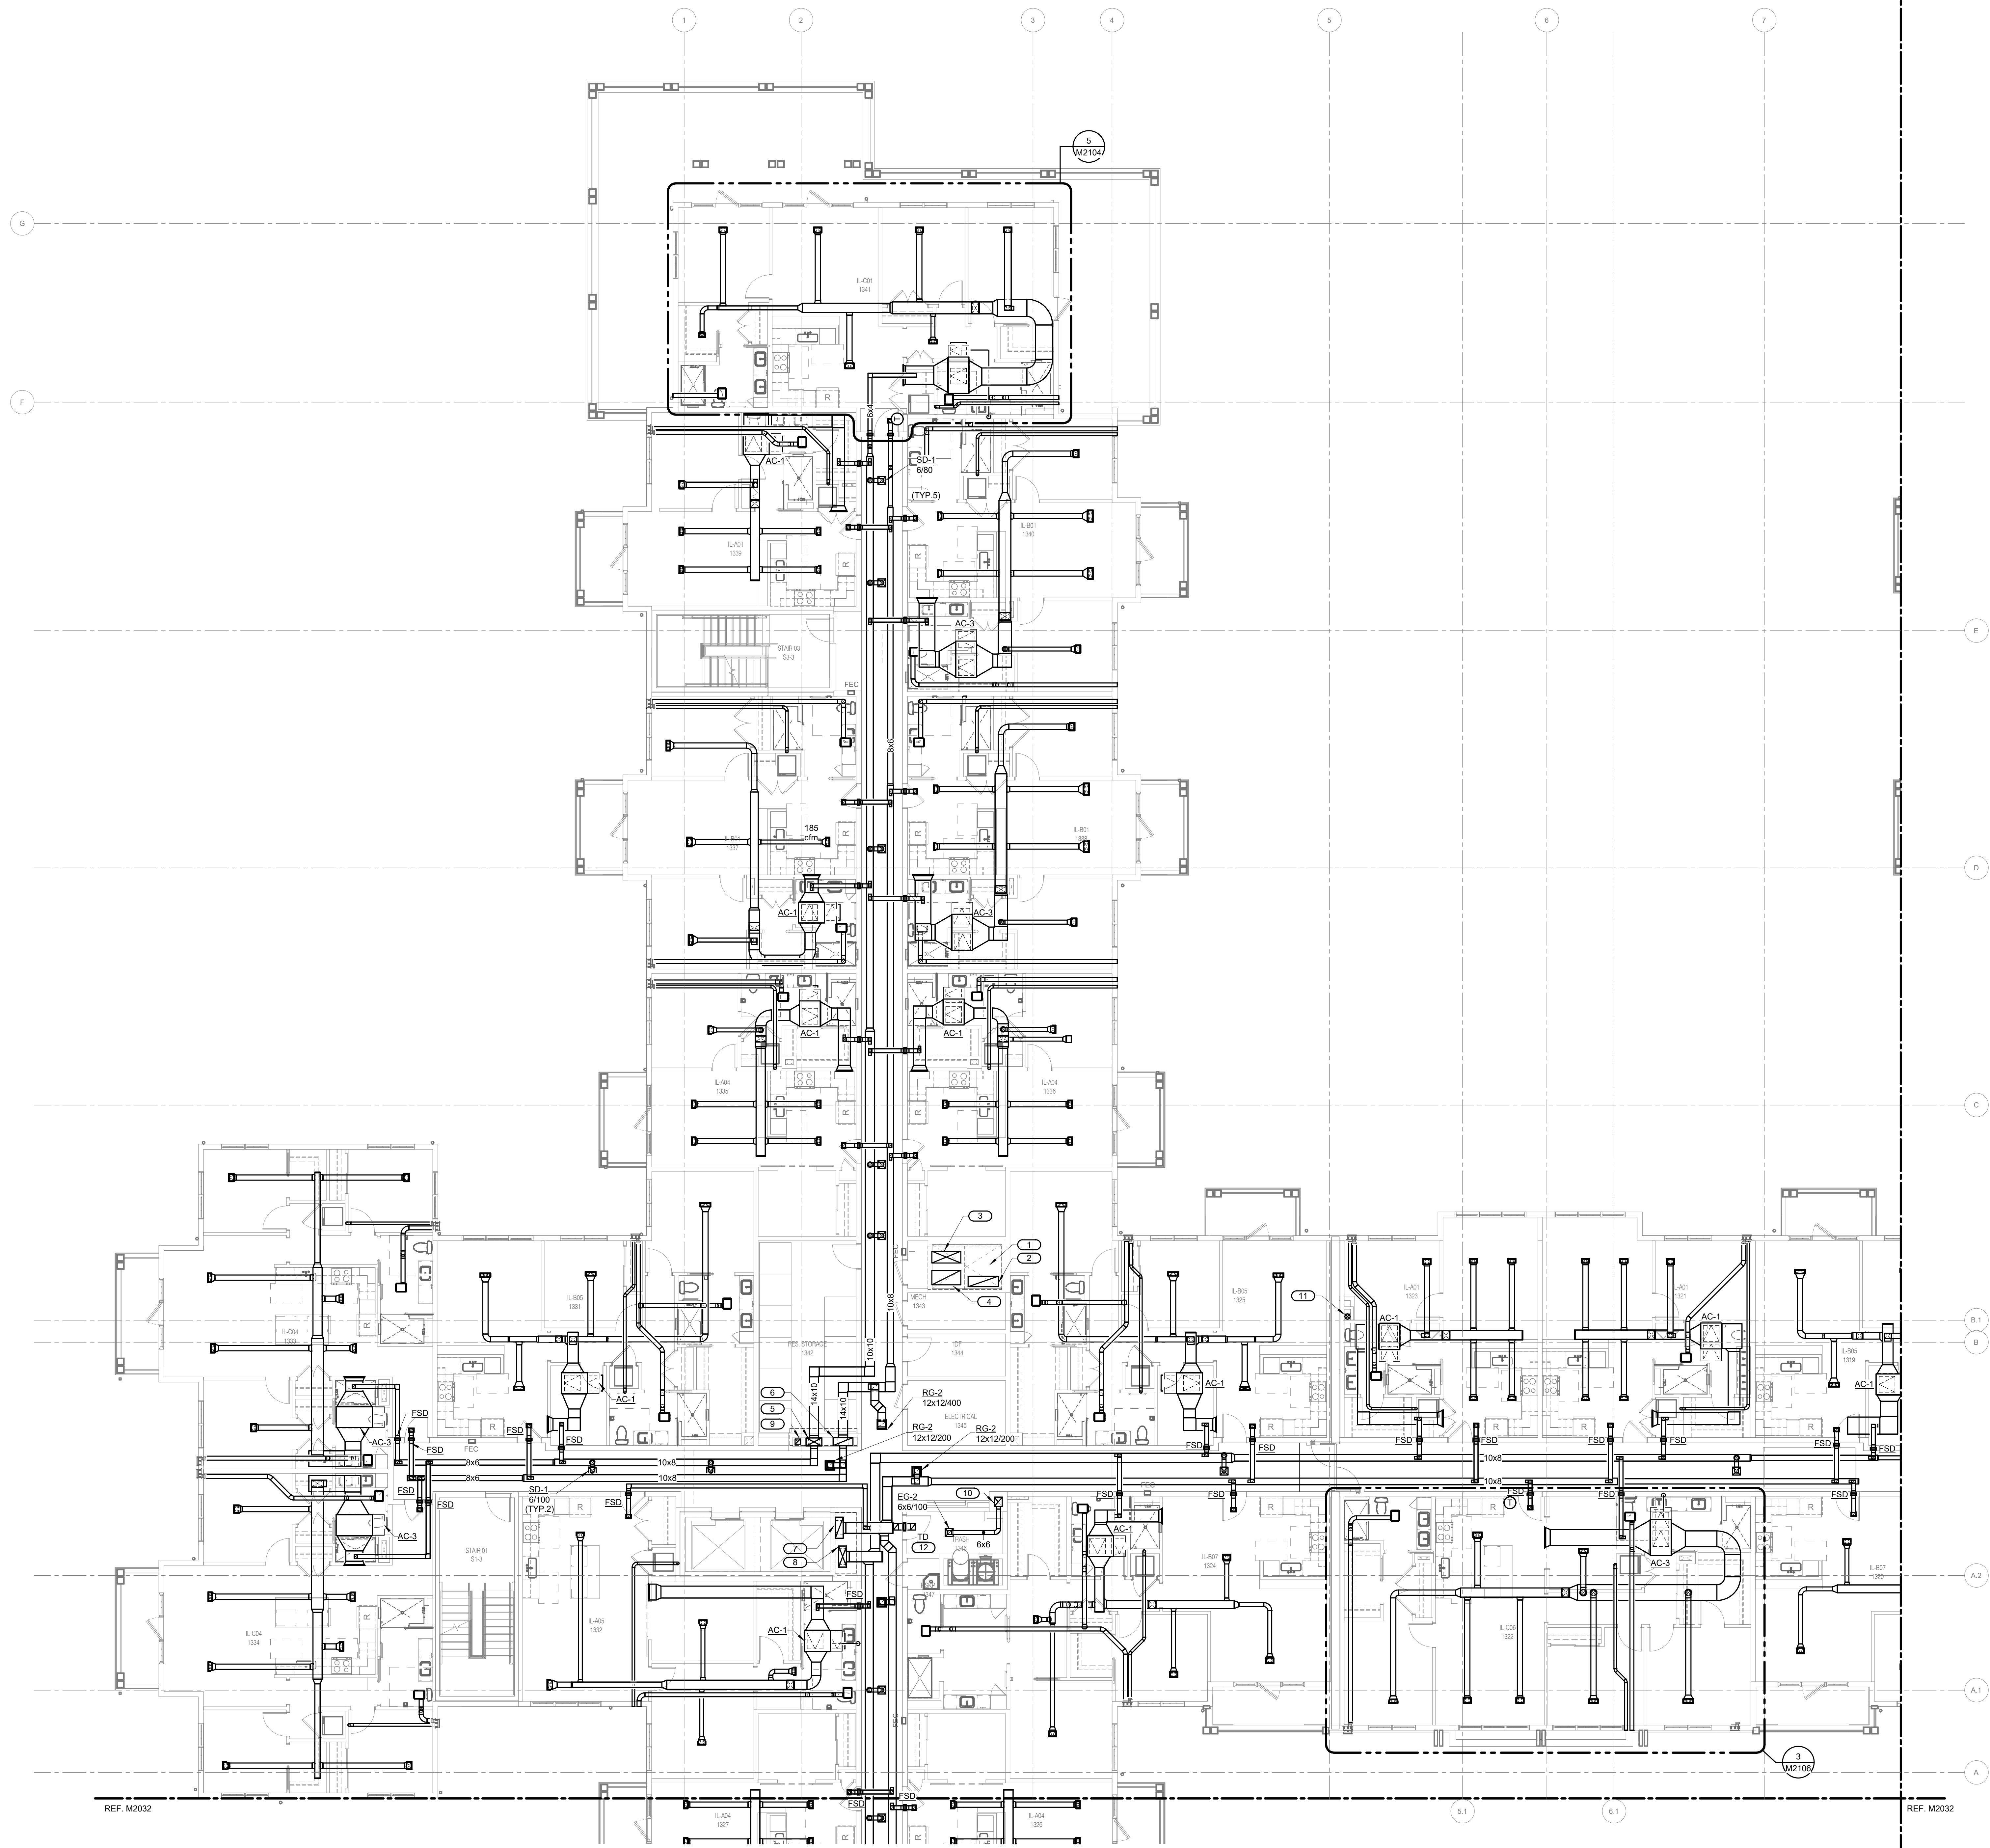

1 INDEX
1/8" = 1'-0"

INDEPENDENT LIVING THIRD FLOOR PLAN - MECHANICAL IL AREA A

ACTUATORS:

- 1. 38x1 SUPPLY AIR DUCT UP AND DOWN THROUGH CHASE TO RTU2.
- 46x16 RETURN AIR DUCT UP AND DOWN THROUGH CHASE TO RTU2.
- 44x24 SUPPLY AIR DUCT UP AND DOWN THROUGH CHASE TO RTU1.
- 46x16 RETURN AIR DUCT UP AND DOWN THROUGH CHASE TO RTU1.
- 24x12 SUPPLY AIR DUCT UP AND DOWN THROUGH CHASE TO DOAS-1. PROVIDE FSD WHERE DUCT LEAVES CHASE.
- 24x12 RETURN AIR DUCT UP AND DOWN THROUGH CHASE TO DOAS-1. PROVIDE FSD WHERE DUCT LEAVES CHASE.
- 24x12 SUPPLY AIR DUCT UP AND DOWN THROUGH CHASE TO DOAS-3.
- 24x12 RETURN AIR DUCT UP AND DOWN THROUGH CHASE TO DOAS-3.
- 16x12 TRASH EXHAUST DUCT UP AND DOWN THROUGH CHASE TO DOAS-1.
- 16x8 EXHAUST AIR DUCT UP AND DOWN.
- 16x8 EXHAUST DUCT ROUTED VERTICALLY UP AND DOWN FROM FIRE PLACE CHIMNEY.
- 24x12 TRASH EXHAUST DUCT DOWN THROUGH WALL WITH FIRESCOPE DAMPER AS REQUIRED.

HKS

HKS ARCHITECTS, P.C.
30 WEST 25th STREET, 12th FLOOR
NEW YORK, NY 10010

IMEG
1411 BROADWAY, SUITE 600
NEW YORK, NY 10018


IMEG
177 CROSSWAYS PARK DRIVE
WOODBURY, NY 11797

TAZERGY
7853 HICKORY FLAT HWY, SUITE 200
WOODSTOCK, GA 30188

MPFP
120 BROADWAY, 20TH FLOOR
NEW YORK, NY 10271

COUNSLMAN-HUNSAKER & ASSOCIATES, INC
12851 MANCHESTER ROAD, SUITE 120
ST. LOUIS, MO 63131


CLARK
2551 HORSESHOE RD.
LANCASTER, PA 17601

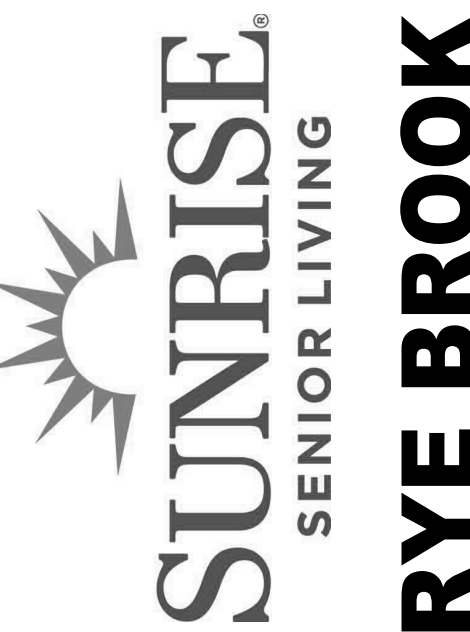

DOB BSCAN | DOB STAMP & SIGNATURES

SEAL & SIGNATURE

CON NO.: 111AAA
KEY PLAN _____

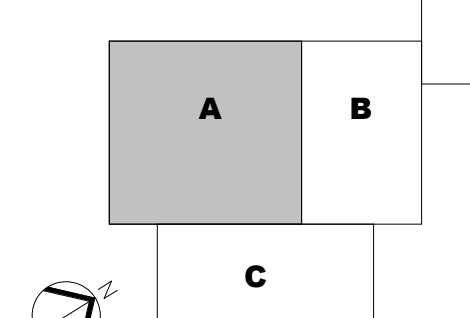

REVISION		
NO.	DESCRIPTION	DATE
1	DD Progress Print	08/28/2
2	DESIGN DEVELOPMENT	11/25/2
3	EXTERIOR BUILDING PERMIT	12/23/2
4	100% DESIGN DEVELOPMENT	01/30/2
5	ISSUED FOR PERMIT	06/05/2

25004064.00

DATE _____

07/15/26

ISSUE

ISSUED FOR CMI

SHEET TITLE

INDEPENDENT LIVING

THIRD FLOOR PLAN -

MECH

AEET NO.
M2030




www.megcorp.com

MEG RESERVES PROPRIETARY RIGHTS, INCLUDING COPYRIGHTS, TO THE DRAWING AND THE DATA SHOWN THEREON. SAID DRAWING AND/OR DATA ARE THE EXCLUSIVE PROPERTY OF MEG AND SHALL NOT BE USED OR REPRODUCED FOR ANY OTHER PROJECT WITHOUT THE EXPRESS WRITTEN APPROVAL AND PARTICIPATION OF MEG.

©2015 MEG CONSULTANTS CORP.

0 1 2 3
REF. SCALE IN INCHES PROJECT #25004(064.00)

© HKS INC.

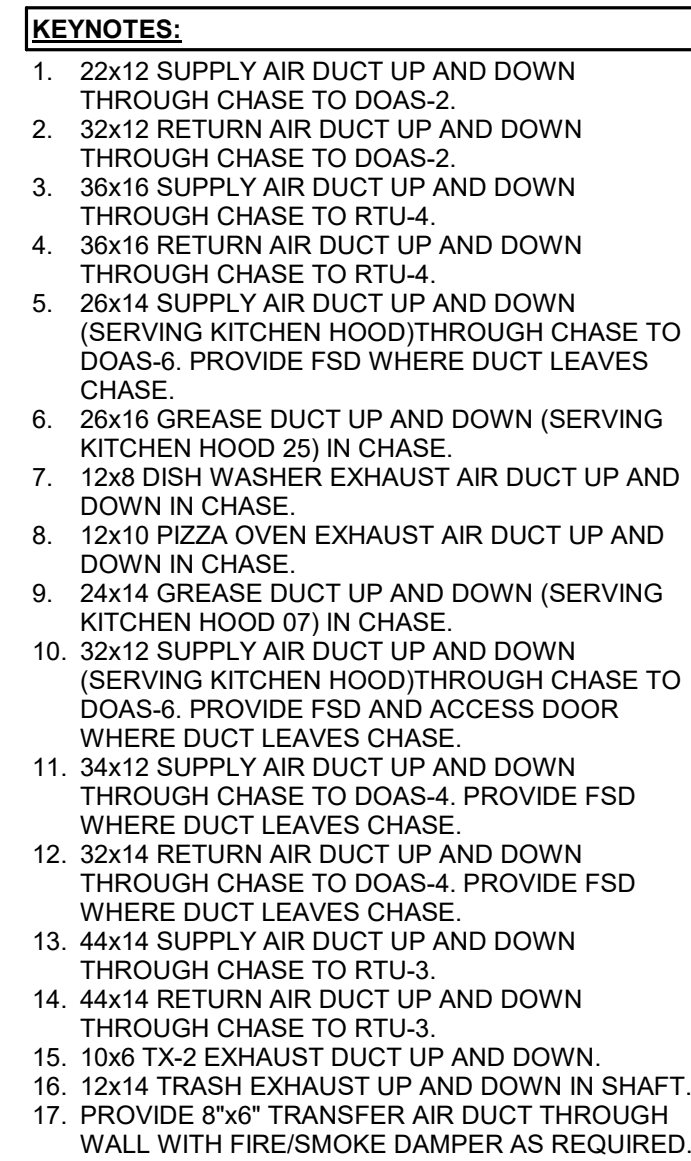

ARCHITECT
HKS ARCHITECTS, P.C.
30 WEST 28TH STREET, 12TH FLOOR
NEW YORK, NY 10010

STRUCTURAL
INEG
1411 BROADWAY, SUITE 600
NEW YORK, NY 10016


MEP ENGINEER
INEG
177 CROSSWAYS PARK DRIVE
WOODBURY, NY 11797

LV ENGINEER
TAZERDY
7863 HICKORY FLAT HWY., SUITE 200
WOODSTOCK, GA 30188

LANDSCAPE ARCHITECT
MPPF
1200 BROADWAY, 20TH FLOOR
NEW YORK, NY 10021


POOL DESIGNER
COUNSMAN HUNSEKER & ASSOCIATES, INC
12851 MANCHESTER ROAD, SUITE 120
ST. LOUIS, MO 63131

FOOD SERVICE & LAUNDRY
CLARK
255 HORSESHOE RD.
LANCASTER, PA 17601

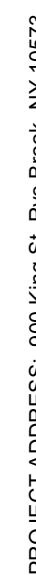

DOB BSCAN | DOB STAMP & SIGNATURES

SEAL & SIGNATURE

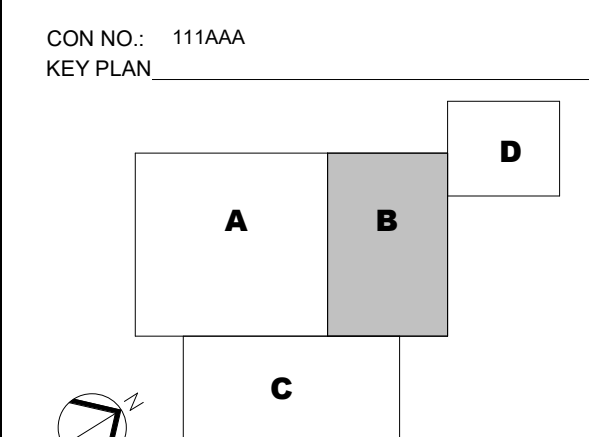


REVISION		
NO.	DESCRIPTION	DATE
1	DD Progress Print	08/26/25
2	DESIGN DEVELOPMENT	11/25/25
3	EXTERIOR BUILDING PERMIT	12/23/25
4	100% DESIGN DEVELOPMENT	01/30/26
5	ISSUED FOR PERMIT	06/05/26

HKS PROJECT NUMBER
25004064.00
DATE
07/15/26
ISSUE
ISSUED FOR GMP


SHEET TITLE
**INDEPENDENT LIVING
THIRD FLOOR PLAN -
MECHANICAL IL AREA**
SHEET NO.

M2031

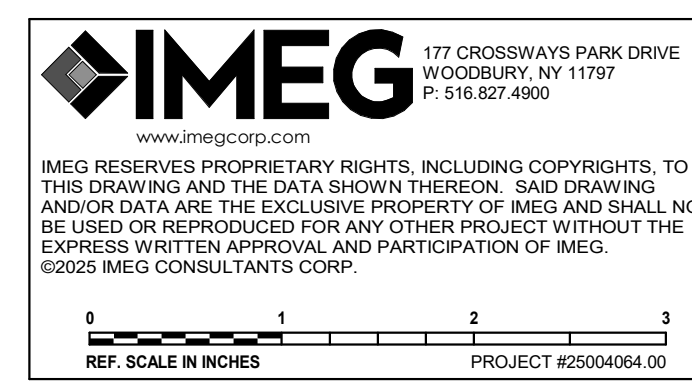

1 INDEPENDENT LIVING THIRD FLOOR PLAN - MECHANICAL IL AREA B

$$1/8'' = 1'-0''$$

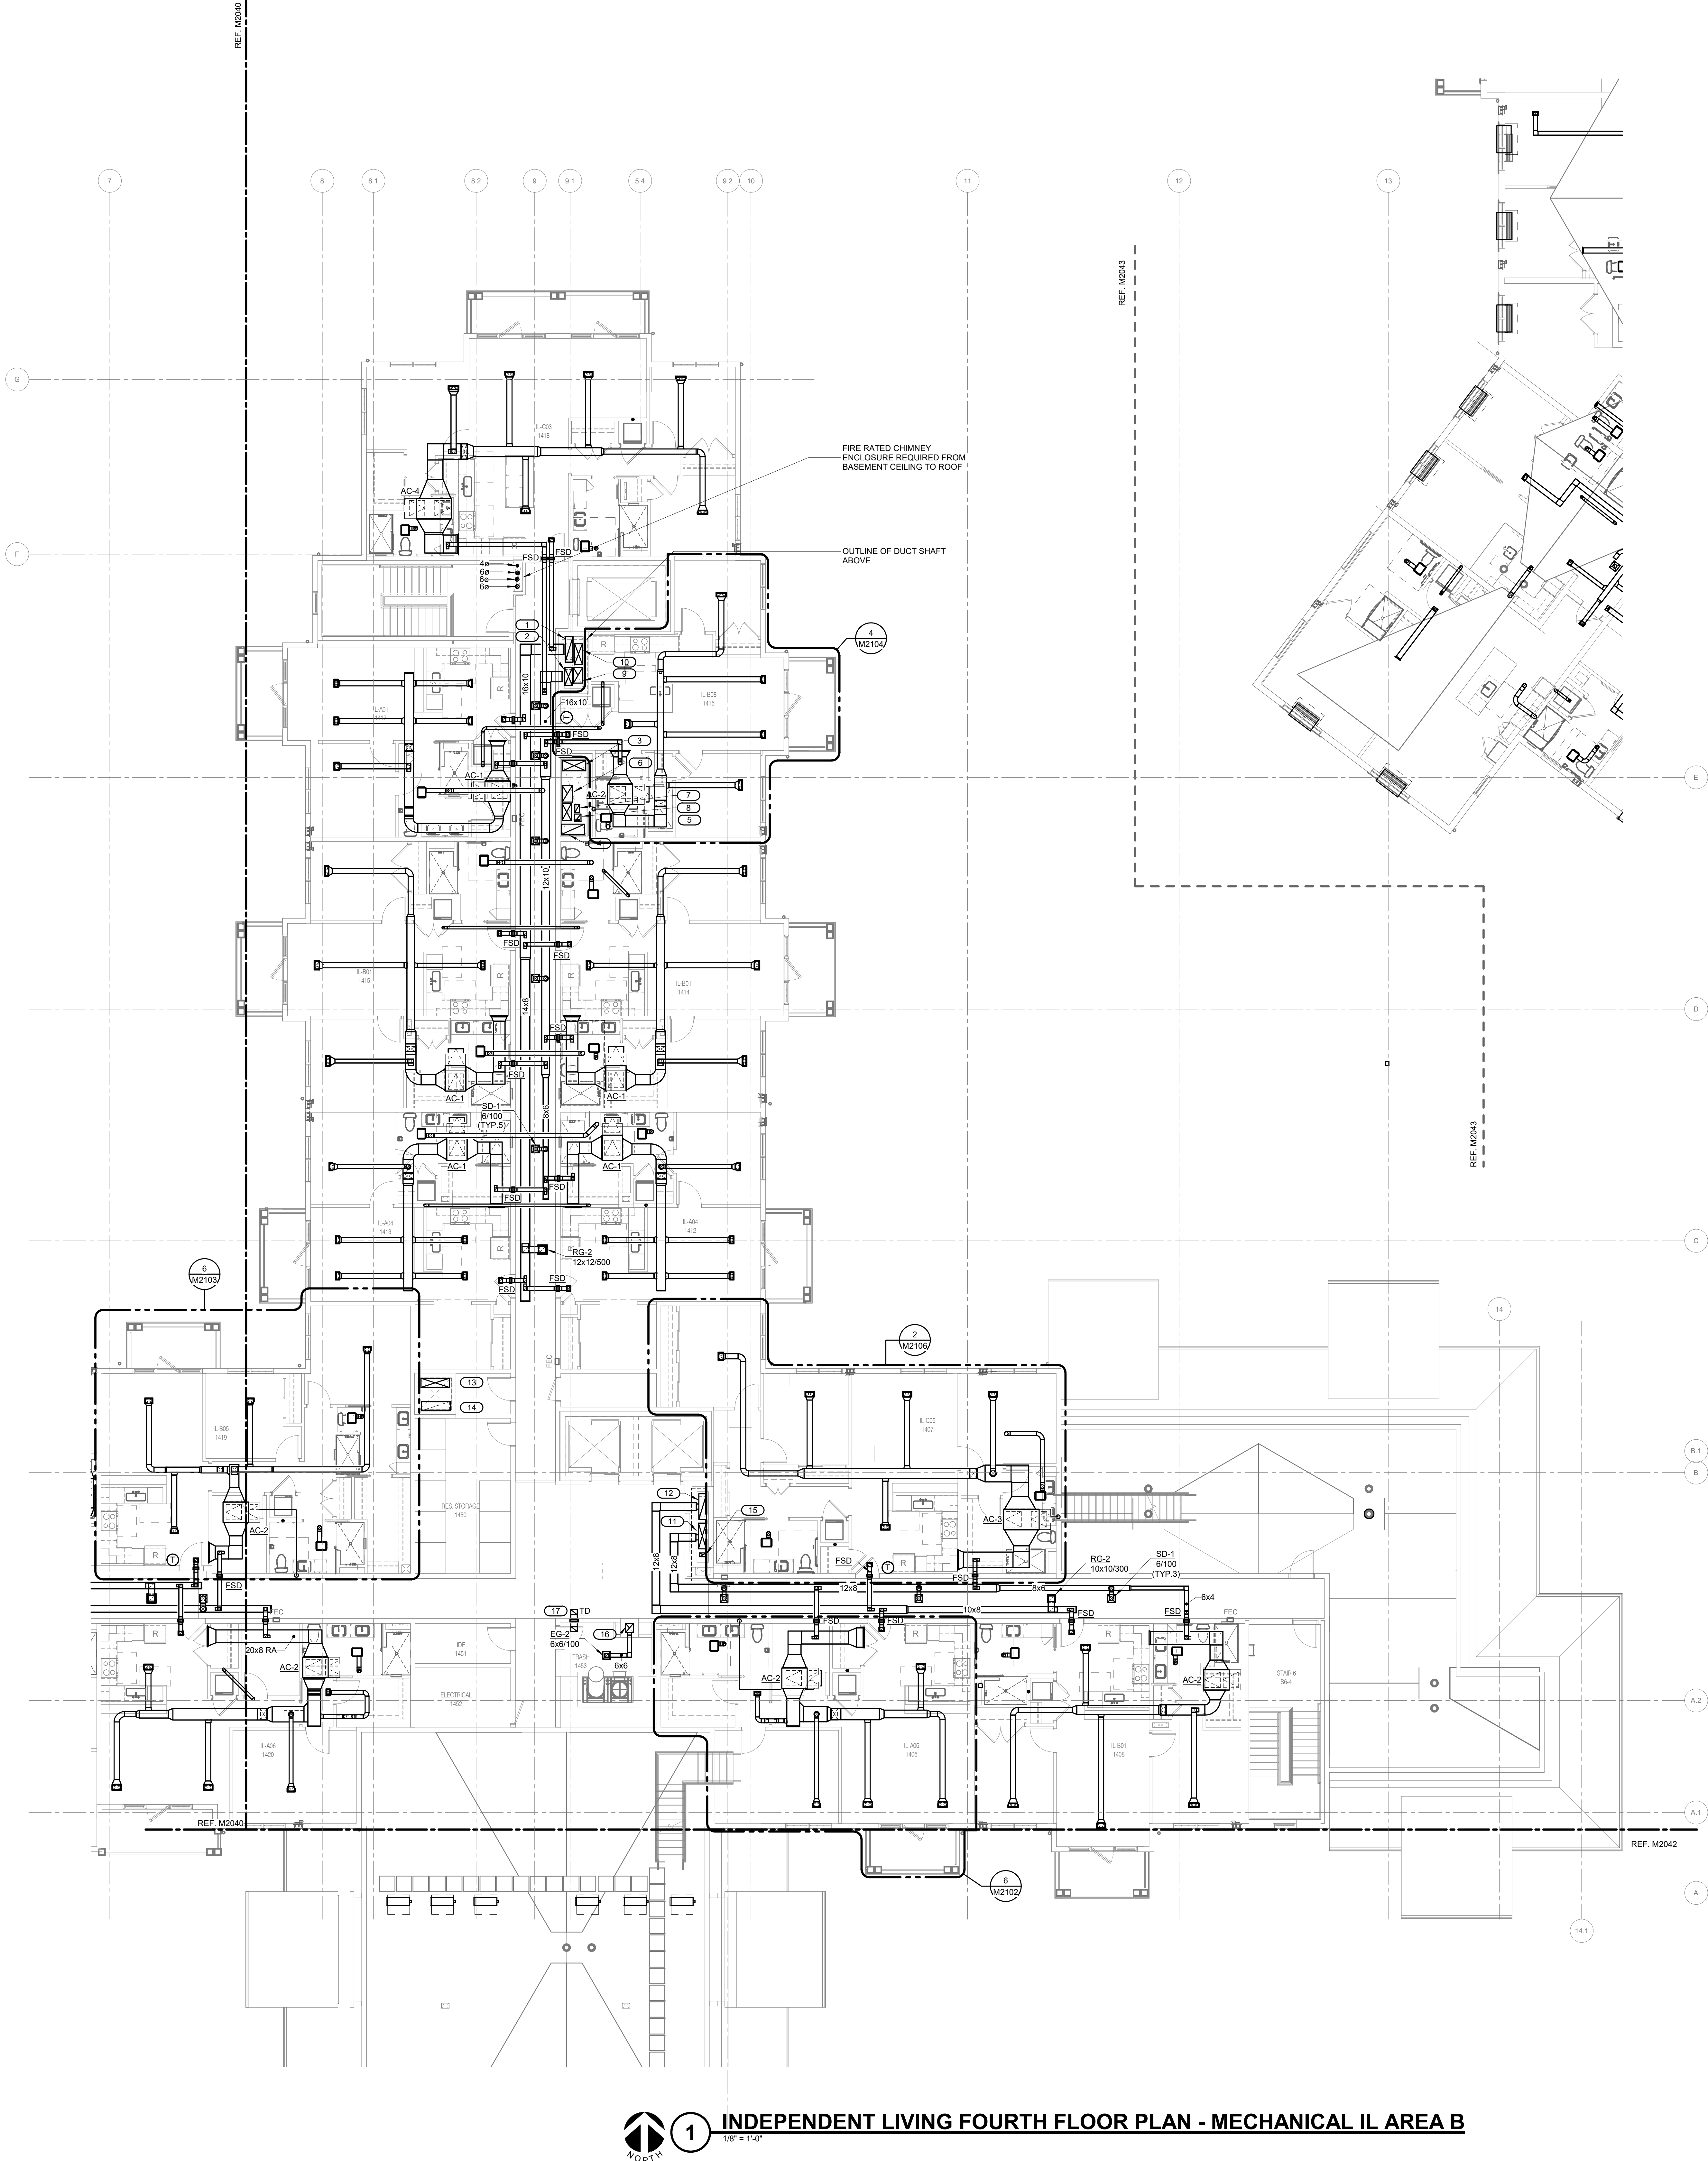

- KEYNOTES:**
- 26x12 SUPPLY AIR DUCT UP AND DOWN THROUGH CHASE TO DOAS-2
 - 40x12 RETURN AIR DUCT UP AND DOWN THROUGH CHASE TO DOAS-2
 - 36x16 SUPPLY AIR DUCT UP AND DOWN THROUGH CHASE TO RTU-4
 - 36x16 RETURN AIR DUCT UP AND DOWN THROUGH CHASE TO RTU-4
 - 26x14 SUPPLY AIR DUCT UP AND DOWN (SERVING KITCHEN HOOD) THROUGH CHASE TO DOAS-4. PROVIDE FSD WHERE DUCT LEAVES CHASE.
 - 26x16 GREASE DUCT UP AND DOWN (SERVING KITCHEN HOOD 25) IN CHASE.
 - 12x8 DISH WASHER EXHAUST AIR DUCT UP AND DOWN IN CHASE.
 - 12x10 PIZZA OVEN EXHAUST AIR DUCT UP AND DOWN IN CHASE.
 - 24x14 GREASE DUCT UP AND DOWN (SERVING KITCHEN HOOD 07) IN CHASE.
 - 32x12 SUPPLY AIR DUCT UP AND DOWN (SERVING KITCHEN HOOD) THROUGH CHASE TO DOAS-6. PROVIDE FSD AND ACCESS DOOR WHERE DUCT LEAVES CHASE.
 - 40x12 SUPPLY AIR DUCT UP AND DOWN THROUGH CHASE TO DOAS-4. PROVIDE FSD WHERE DUCT LEAVES CHASE.
 - 40x14 RETURN AIR DUCT UP AND DOWN THROUGH CHASE TO DOAS-4. PROVIDE FSD WHERE DUCT LEAVES CHASE.
 - 44x14 SUPPLY AIR DUCT UP AND DOWN THROUGH CHASE TO RTU-3.
 - 44x14 RETURN AIR DUCT UP AND DOWN THROUGH CHASE TO RTU-3.
 - 10x6 TX-2 EXHAUST DUCT UP AND DOWN.
 - 12x14 TRASH EXHAUST UP AND DOWN IN SHAFT.
 - PROVIDE 8"x6" TRANSFER AIR DUCT THROUGH WALL WITH FIRE/SMOKE DAMPER AS REQUIRED.

HKS

ARCHITECT
HKS ARCHITECTS, P.C.
30 WEST 26th STREET, 12th FLOOR
NEW YORK, NY 10010

STRUCTURAL
IMEG
1411 BROADWAY, SUITE 600
NEW YORK, NY 10018

MEP ENGINEER
IMEG
177 CROSSWAYS PARK DRIVE
WOODBURY, NY 11797

LV ENGINEER
TASERCO
765 HICKORY FLAT HWY, SUITE 200
WOODSTOCK, GA 30188

LANDSCAPE ARCHITECT
MFP
120 BROADWAY, 20TH FLOOR
NEW YORK, NY 10271

POOL DESIGNER
COUNSLMAN HUNSAKER & ASSOCIATES, INC.
12851 MANCHESTER ROAD, SUITE 120
ST. LOUIS, MO 63131


FOOD SERVICE & LAUNDRY
CLARK
2551 HORSEHOE RD.
LANCASTER, PA 17601

SUNRISE SENIOR LIVING
RYE BROOK

DOB BSCAN | DOB STAMP & SIGNATURES

SEAL & SIGNATURE

CON NO.: 111AAA
KEY PLAN

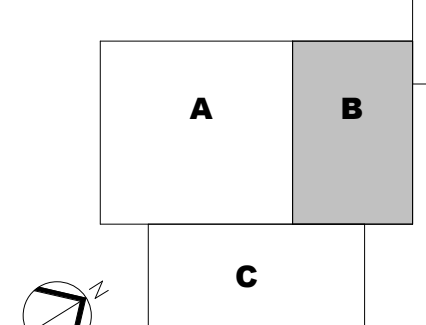



REVISION	
NO.	DESCRIPTION
1	DD Progress Print
2	DESIGN DEVELOPMENT
3	EXTERIOR BUILDING PERMIT
4	100% DESIGN DEVELOPMENT
5	ISSUED FOR PERMIT

HKS PROJECT NUMBER
25004064.00
DATE
07/15/26
ISSUE
ISSUED FOR GMP

SHEET TITLE
**INDEPENDENT LIVING
FOURTH FLOOR PLAN -
MECHANICAL IL AREA**
SHEET NO.
M2041

DOB FILE # DOB PAGE #


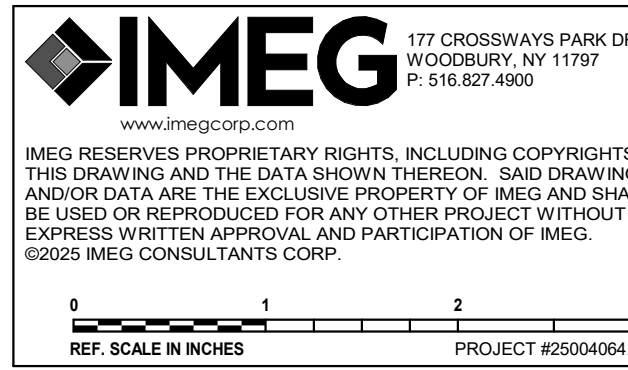


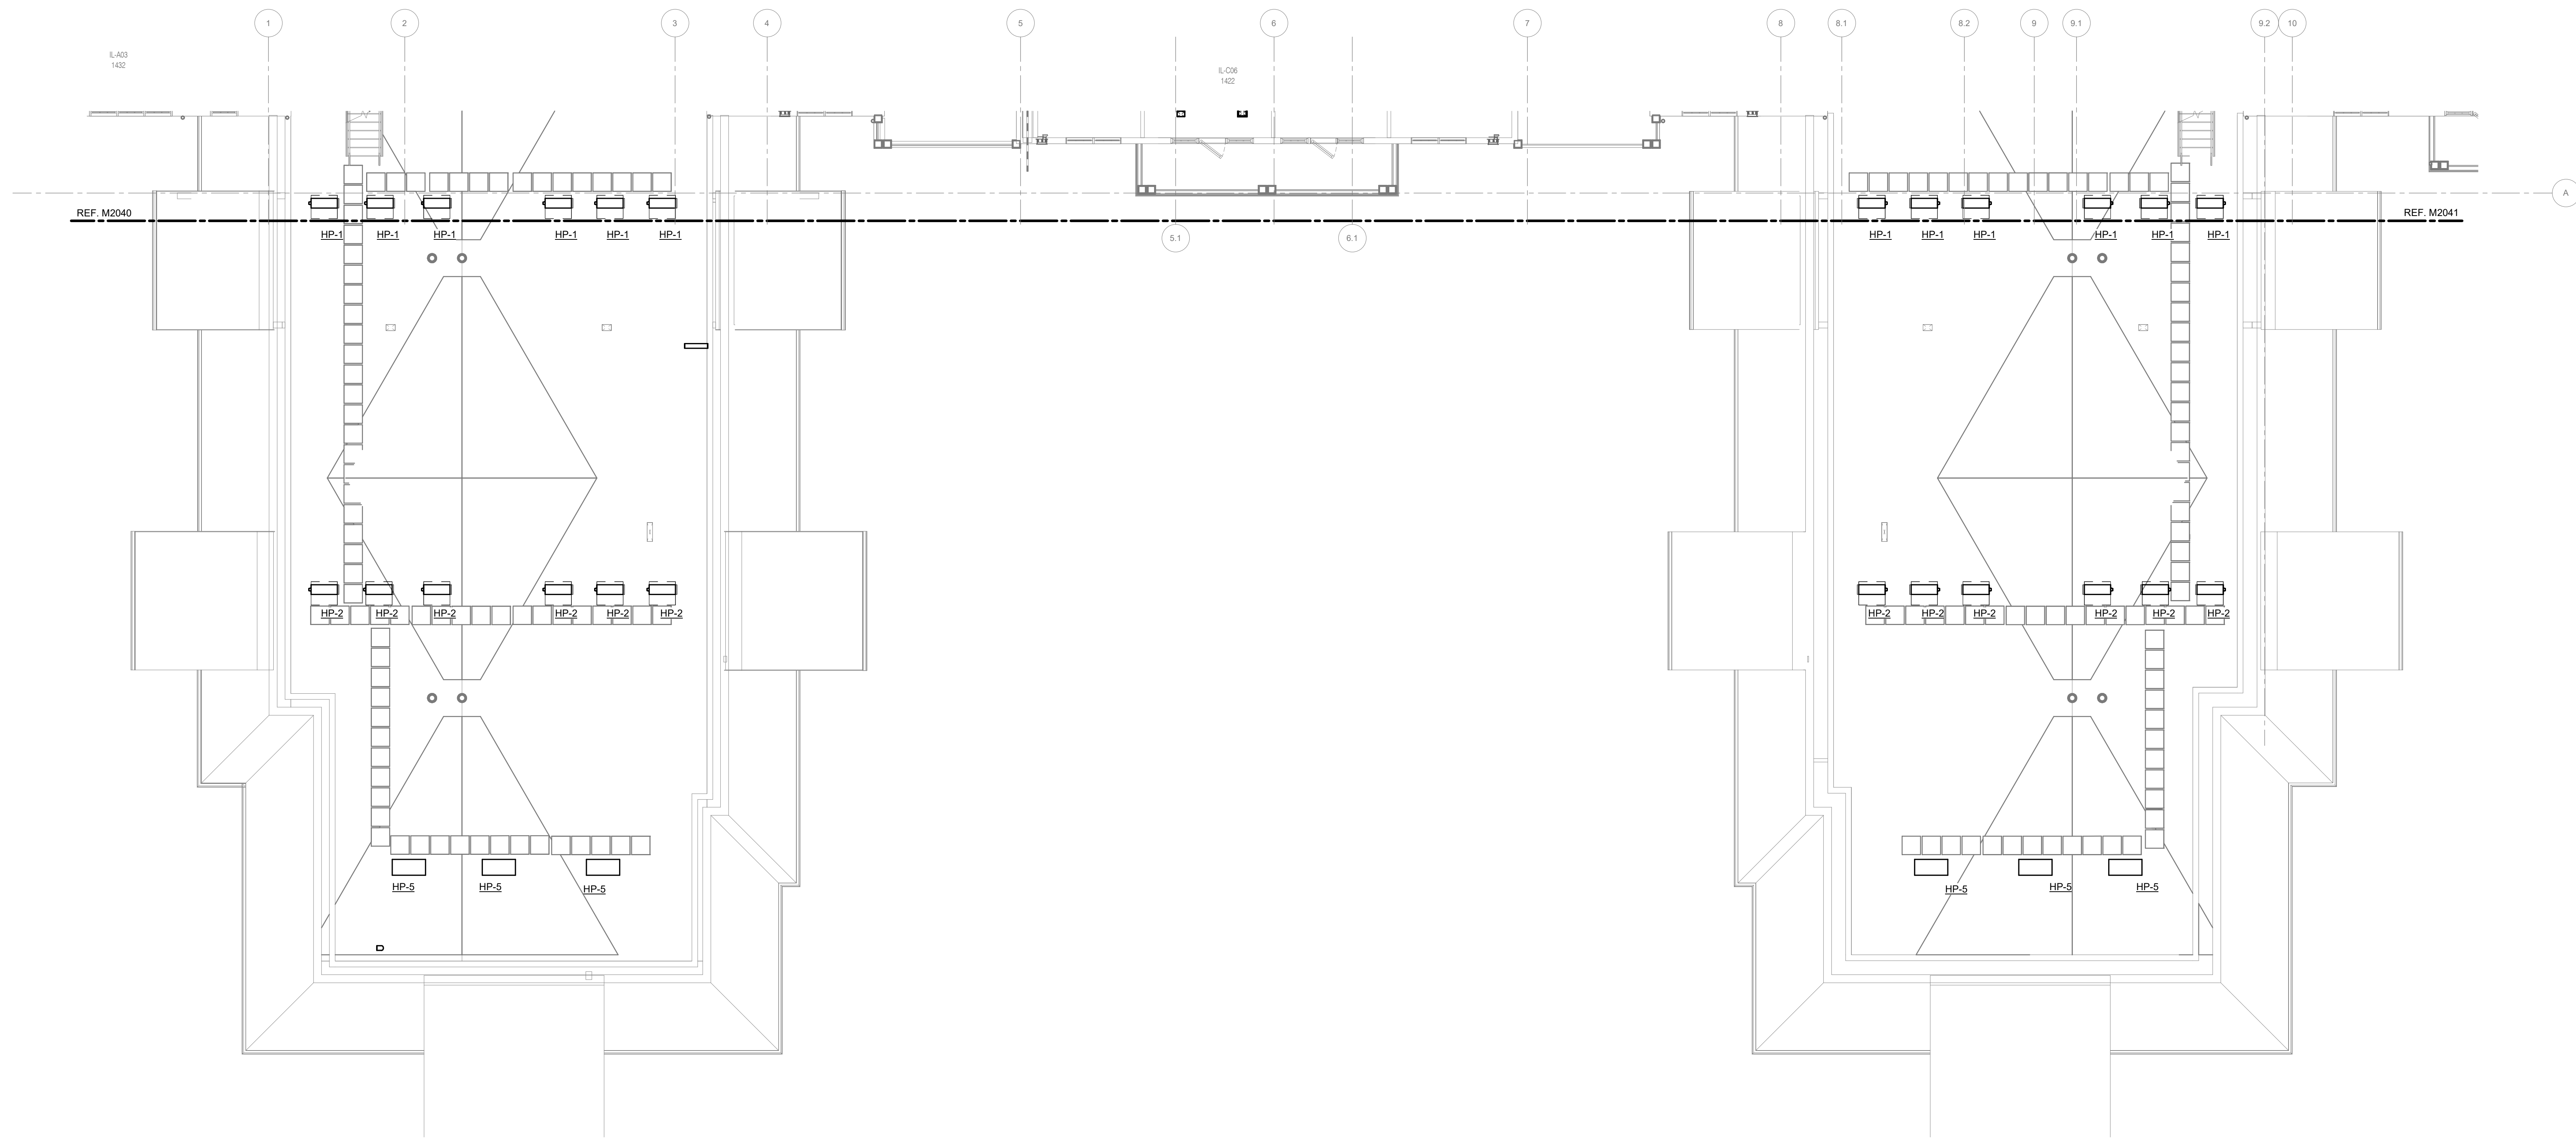

1

1/8" = 1'-0"

INDEPENDENT LIVING FOURTH FLOOR PLAN - MECHANICAL IL AREA C

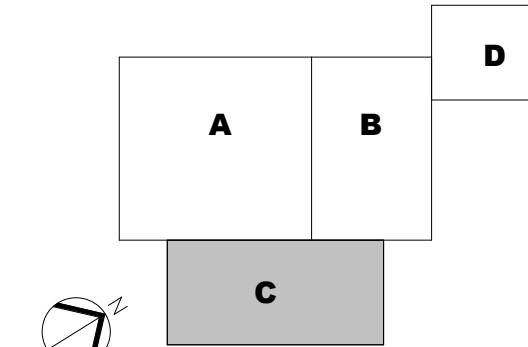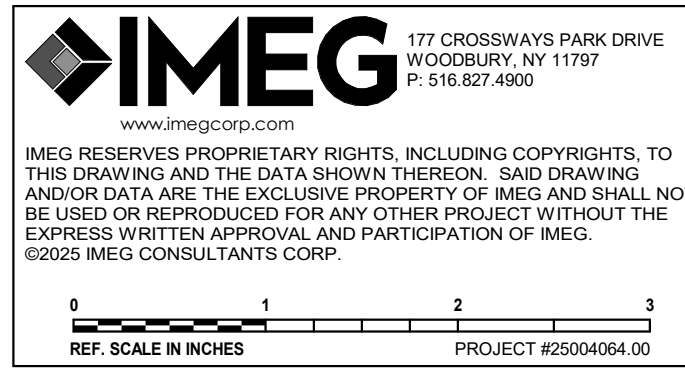

REVISION		
NO	DESCRIPTION	DATE
1	DD Progress Print	08/26/25
2	DESIGN DEVELOPMENT	11/25/25
3	EXTERIOR BUILDING PERMIT	12/23/25
4	100% DESIGN DEVELOPMENT	01/30/26
5	ISSUED FOR PERMIT	06/05/26



1

ASSISTED LIVING FOURTH FLOOR PLAN - MECHANICAL AL AREA D

1/8" = 1'-0"



IMEG RESERVES PROPRIETARY RIGHTS, INCLUDING COPYRIGHTS, TO THIS DRAWING AND THE DATA SHOWN THEREON. NO REPRODUCING AND/OR DATA ARE THE EXCLUSIVE PROPERTY OF IMEG AND SHALL NOT BE USED OR REPRODUCED FOR ANY OTHER PROJECT WITHOUT THE EXPRESS WRITTEN APPROVAL AND PARTICIPATION OF IMEG. ©2025 IMEG CONSULTANTS CORP.

177 CROSSWAYS PARK DRIVE
WOODBURY, NY 11797
P: 516-927-6900

PROJECT: 25004064.00

© HKS, INC.

HKS PROJECT NUMBER

25004064.00

DATE

07/15/26

ISSUE

ISSUED FOR GMP

SHEET TITLE

ASSISTED LIVING

FOURTH FLOOR PLAN -

MECHANICAL AL AREA

SHEET NO.

M2043

DOB FILE #

DOB PAGE #

HKS

ARCHITECT

HKS ARCHITECTS, P.C.
30 WEST 26th STREET, 12th FLOOR
NEW YORK, NY 10010

STRUCTURAL

MEG

1411 BROADWAY, SUITE 600
NEW YORK, NY 10018

MEP ENGINEER

MEG

177 CROSSWAYS PARK DRIVE
WOODBURY, NY 11797

LV ENGINEER

TAGERGY

765 HICKORY FLAT HWY, SUITE 200
WOODSTOCK, GA 30188

LANDSCAPE ARCHITECT

MFP

120 BROADWAY, 20TH FLOOR
NEW YORK, NY 10021


POOL DESIGNER

COUNSLMANHUNSAKER & ASSOCIATES, INC.

12851 MANCHESTER ROAD, SUITE 120
ST. LOUIS, MO 63131

FOOD SERVICE & LAUNDRY

CLARK

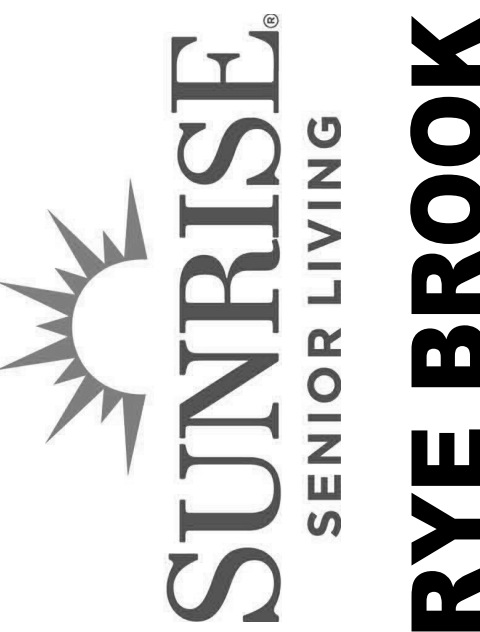
2551 HORSESHOE RD.
LANCASTER, PA 17601

DOB BSCAN | DOB STAMP & SIGNATURES

SEAL & SIGNATURE


CON NO.: 111AAA

KEY PLAN

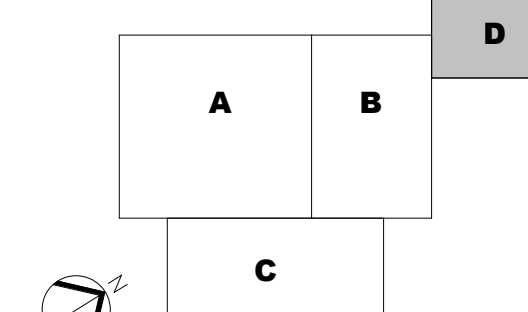

REVISION

NO.	DESCRIPTION	DATE
1	DD Program Print	08/26/25
2	DESIGN DEVELOPMENT	11/05/25
3	EXTERIOR BUILDING PERMIT	12/03/25
4	100% DESIGN DEVELOPMENT	01/08/26
5	ISSUED FOR PERMIT	06/05/26

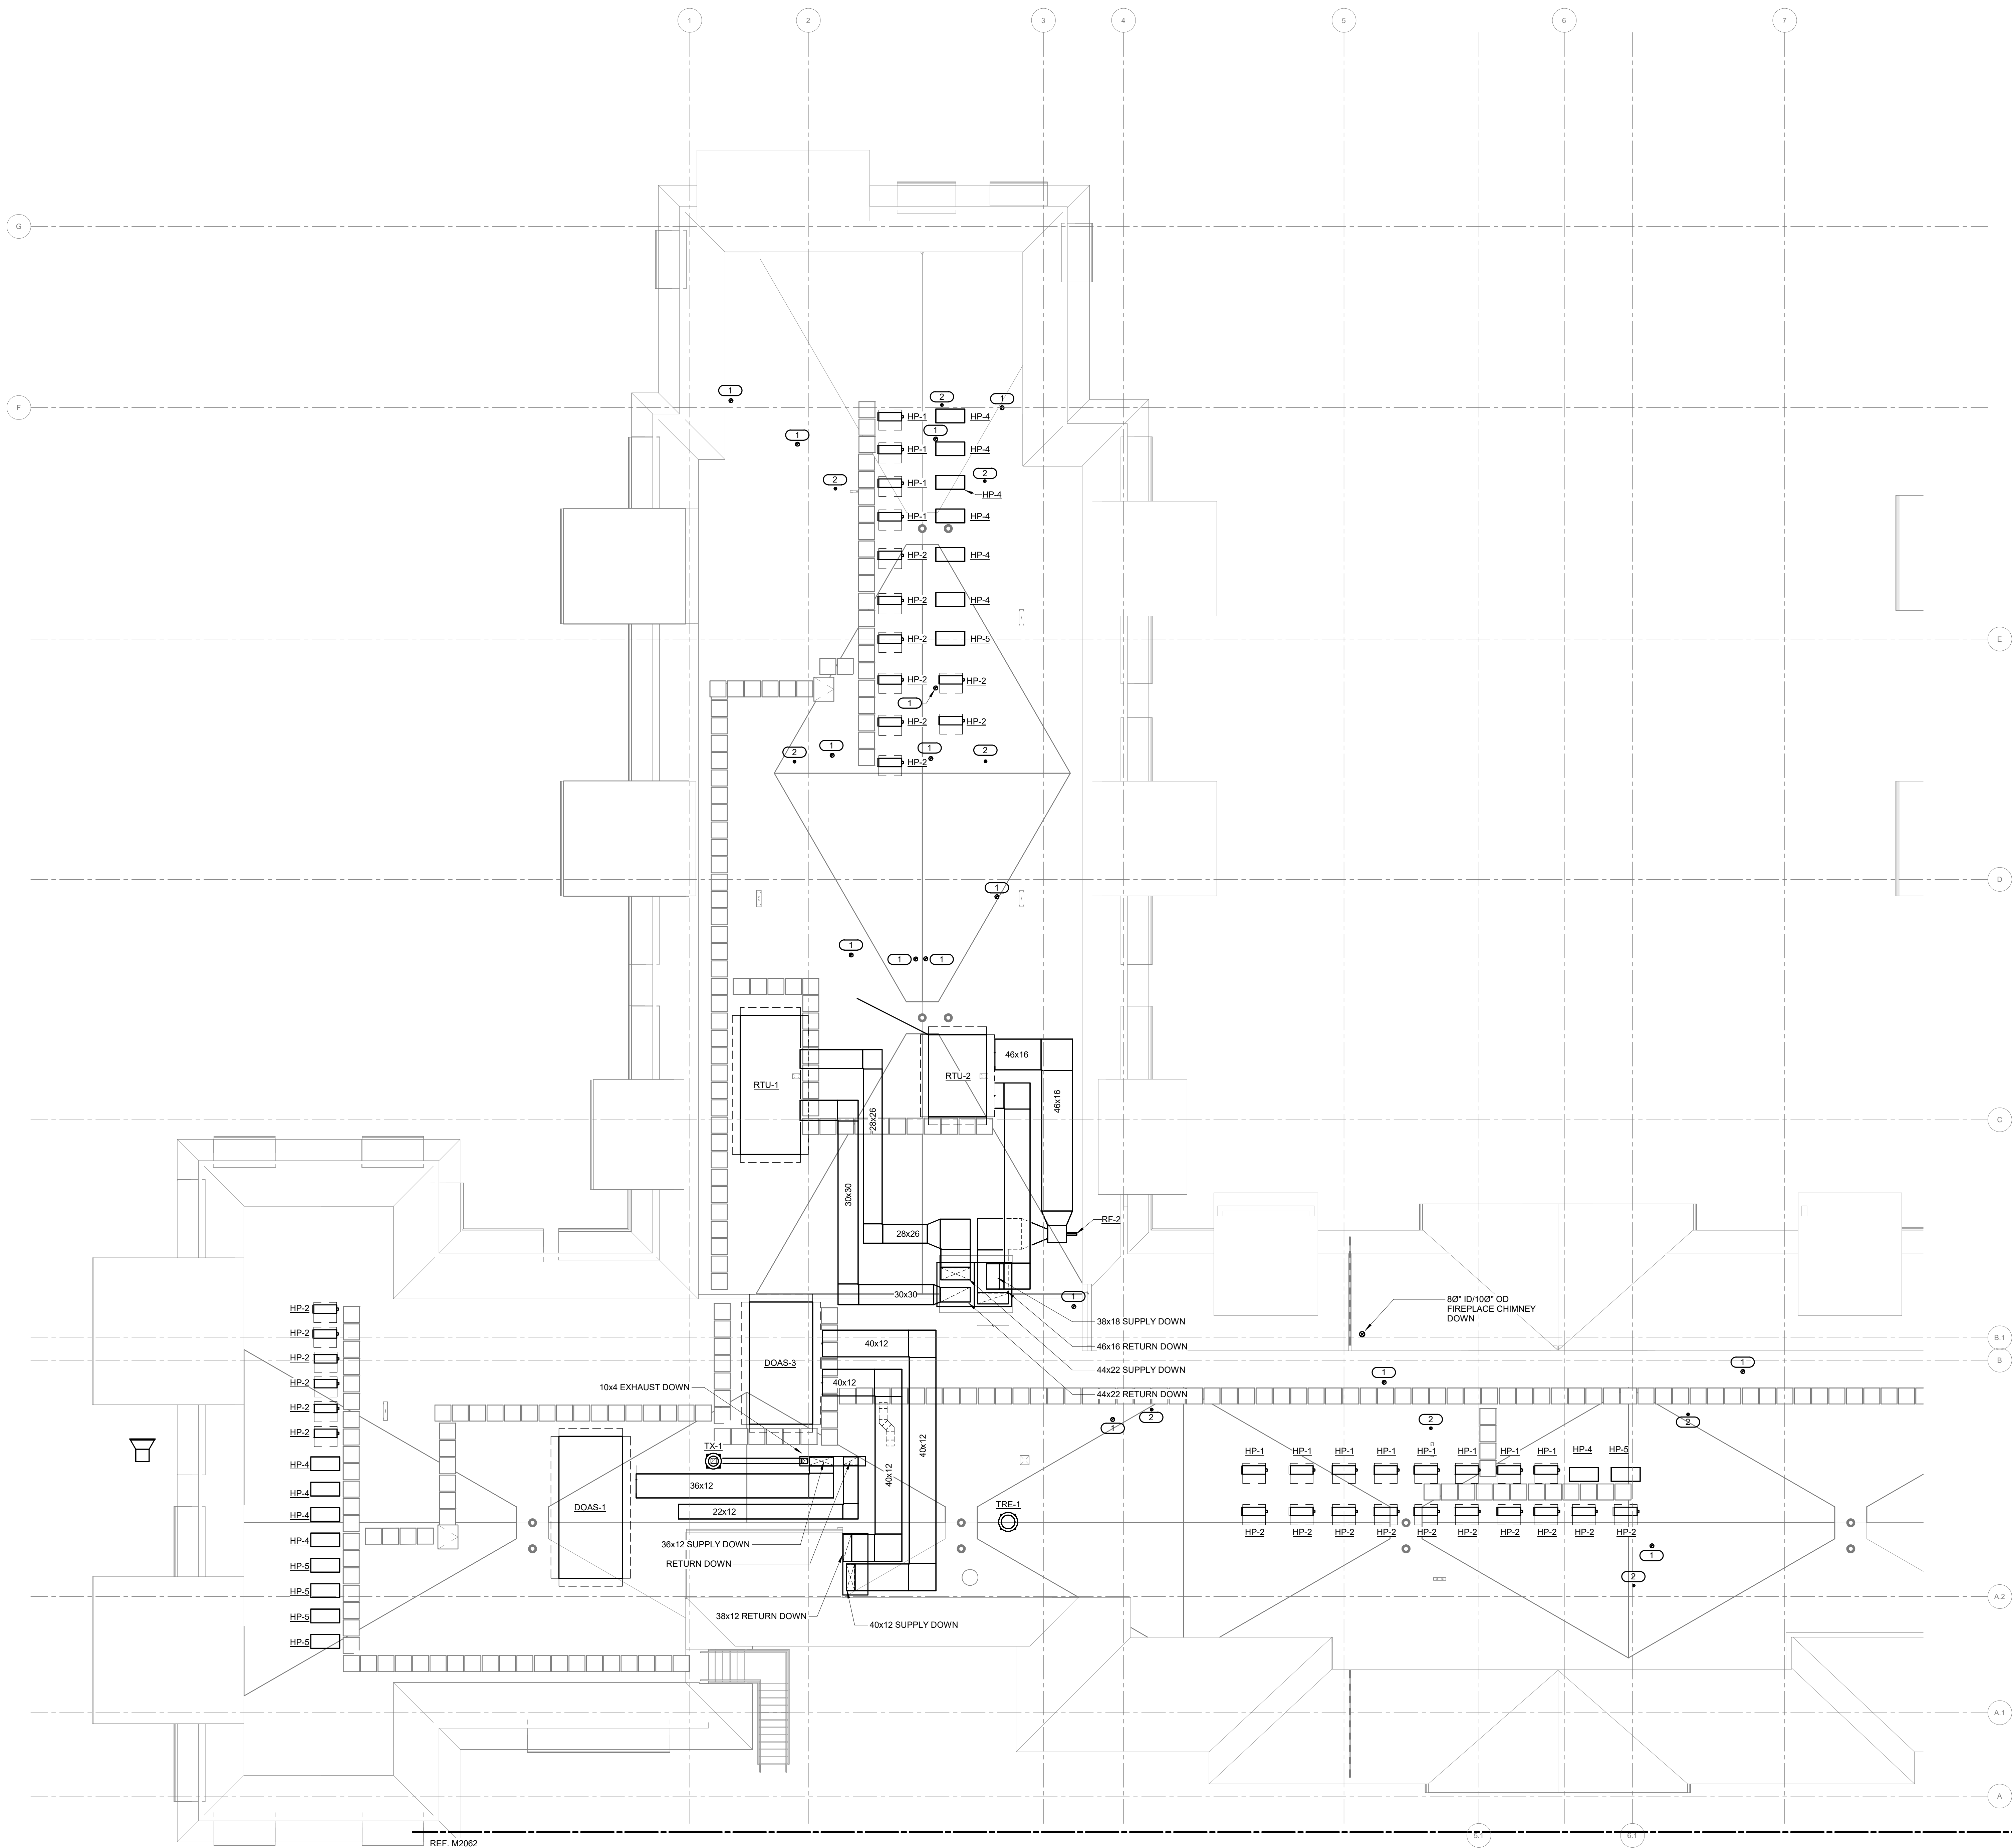

 1 **INDEPENDENT LIVING ROOF PLAN - MECHANICAL IL AREA A**
1/8" = 1'-0"

1. 6" TOILET EXHAUST DUCT TO PENETRATE THROUGH ROOF AND TERMINATE ABOVE ROOF WITH WEATHER CAP. MAINTAIN MINIMUM 10'-0" DISTANCE FROM ANY OUTDOOR AIR INTAKES.
2. 4" DRYER EXHAUST DUCT TO PENETRATE THROUGH ROOF AND TERMINATE ABOVE ROOF WITH WEATHER CAP.

ARCHITECT
HKS ARCHITECTS, P.C.
30 WEST 28th STREET, 12th FLOOR
NEW YORK, NY 10010

STRUCTURAL

IMEG
1411 BROADWAY, SUITE 600
NEW YORK, NY 10018

MEP ENGINEER

IMEG
177 CROSSWAYS PARK DRIVE
WOODBURY, NY 11797

LV ENGINEER

TAZERGY
7853 HICKORY FLAT HWY, SUITE 200
WOODSTOCK, GA 30188

LANDSCAPE ARCHITECT


MPFP
120 BROADWAY, 20TH FLOOR
NEW YORK, NY 10271

POOL DESIGNER

COUNSILMAN-HUNSAKER & ASSOCIATES, INC.
12851 MANCHESTER ROAD, SUITE 120
ST. LOUIS, MO 63131

FOOD SERVICE & LAUNDRY

CLARK
2551 HORSESHOE RD
LANCASTER, PA 1760

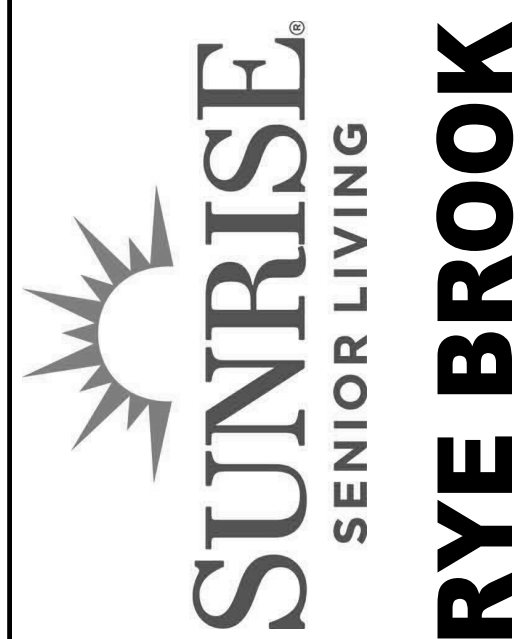


PROFESSOR AND DEAN, COLLEGE OF BUSINESS, UNIVERSITY OF ALABAMA

DOB BSCAN | DOB STAMP & SIGNATURES

SEAL & SIGNATURE

CON NO.: 111AAA

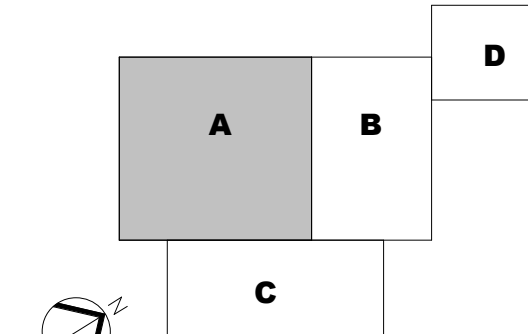

REVISION		
NO.	DESCRIPTION	DATE
1	DD Progress Print	09/26/25
2	DESIGN DEVELOPMENT	11/25/25
3	EXTERIOR BUILDING PERMIT	12/23/25
4	100% DESIGN DEVELOPMENT	01/30/26
5	ISSUED FOR PERMIT	08/05/26

HKS PROJECT NUMBER

25004064.00

DATE _____

07/15/26

ISSUE

ISSUED FOR GMP

SHEET TITLE


INDEPENDENT LIVING

ROOF PLAN -

MEC

MEET NO.
M2060

DOB FILE #: DOB PAGE #

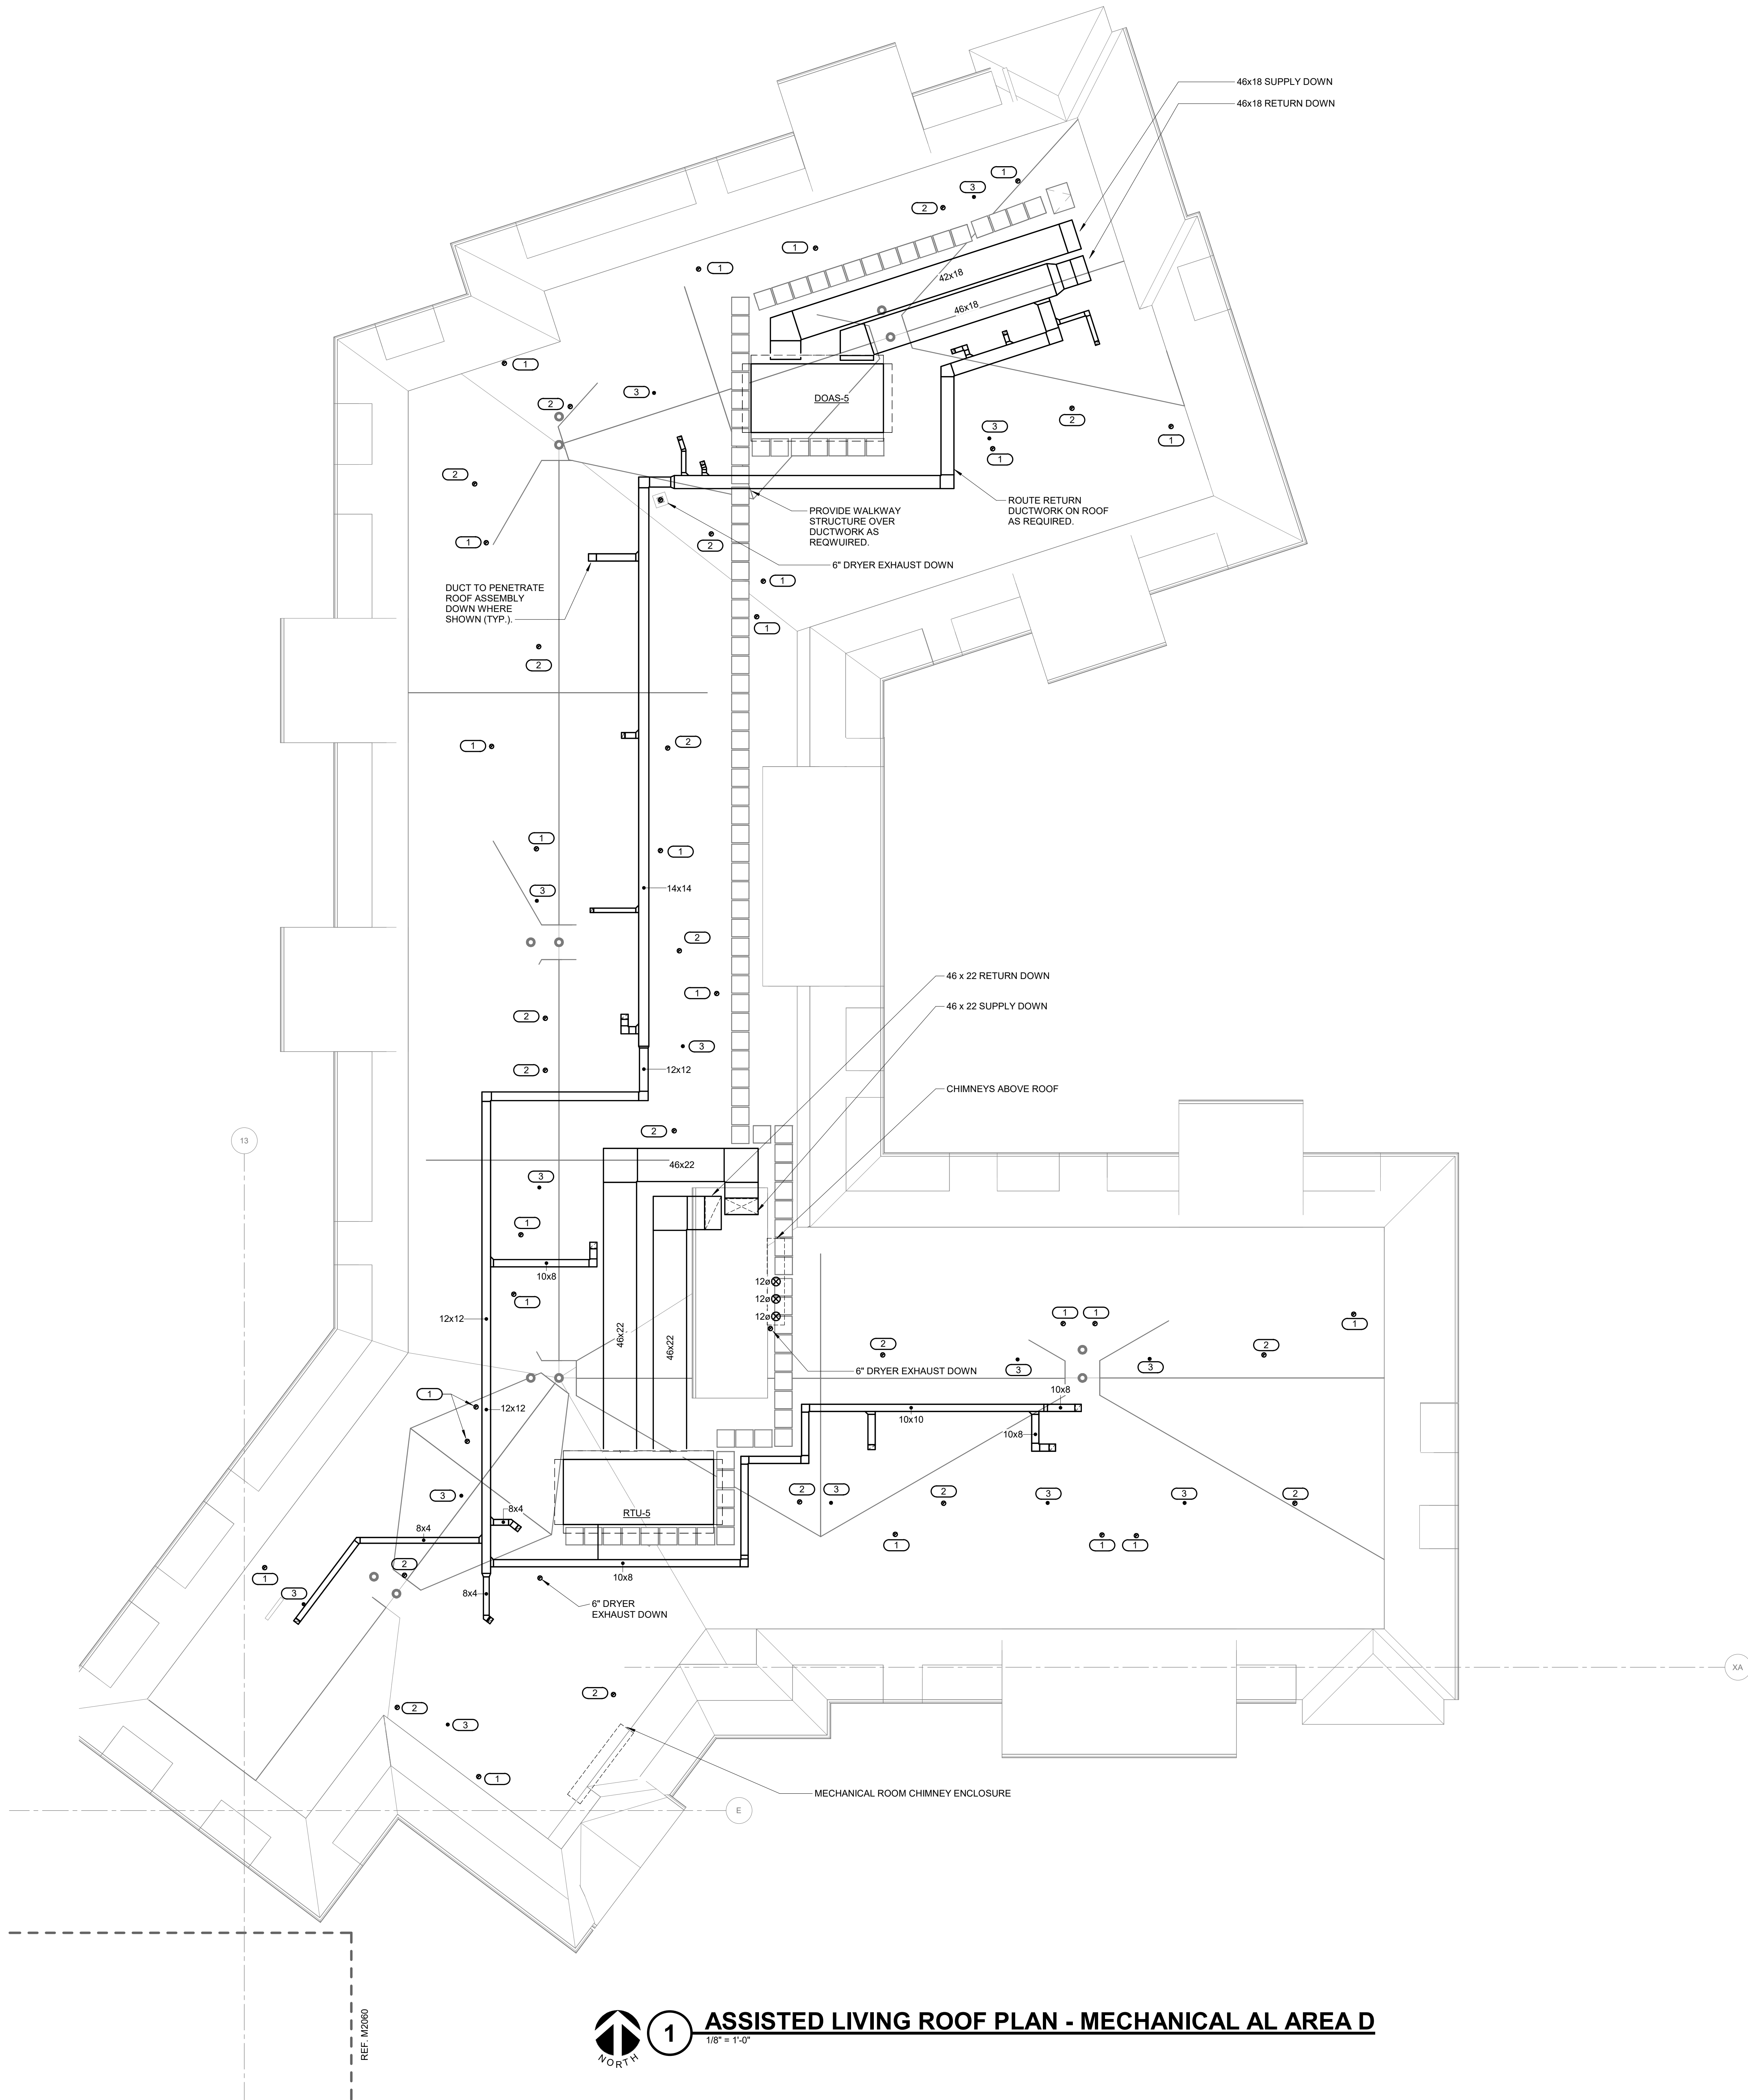

KEYNOTES:

1. 6\"/>

HKS

ARCHITECT

HKS ARCHITECTS, P.C.
30 WEST 26th STREET, 12th FLOOR
NEW YORK, NY 10010

STRUCTURAL

IMEG

1411 BROADWAY, SUITE 600
NEW YORK, NY 10018

MEP ENGINEER

IMEG

177 CROSWAYS PARK DRIVE
WOODBURY, NY 11797

LV ENGINEER

TASERCO

765 HICKORY FLAT HWY, SUITE 200
WOODSTOCK, GA 30188

LANDSCAPE ARCHITECT

MFPF

120 BROADWAY, 20TH FLOOR
NEW YORK, NY 10071


POOL DESIGNER

COUNSLMANHUNSAKER & ASSOCIATES, INC.

12851 MANCHESTER ROAD, SUITE 120
ST. LOUIS, MO 63131

FOOD SERVICE & LAUNDRY

CLARK

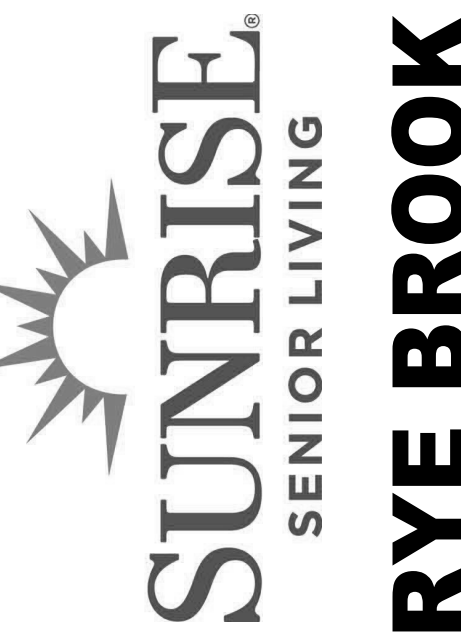
2551 HORSESHOE RD.
LANCASTER, PA 17601

DOB BSCAN | DOB STAMP & SIGNATURES

SEAL & SIGNATURE

CON NO.: 111AAA

KEY PLAN

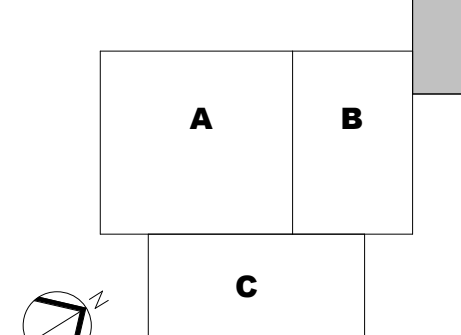

REVISION	NO.	DESCRIPTION	DATE
1	1	100% DESIGN DEVELOPMENT	08/05/2016
2	2	90% DESIGN DEVELOPMENT	11/05/2016
3	3	EXTERIOR BUILDING PERMIT	12/03/2016
4	4	100% DESIGN DEVELOPMENT	01/05/2017
5	5	ISSUED FOR PERMIT	06/05/2016

HKS PROJECT NUMBER

25004064.00

DATE

07/15/26

ISSUE

ISSUED FOR GMP

SHEET TITLE


ASSISTED LIVING ROOF
PLAN - MECHANICAL AL
AREA D


SHEET NO.

M2063


DOB FILE #

DOB PAGE #

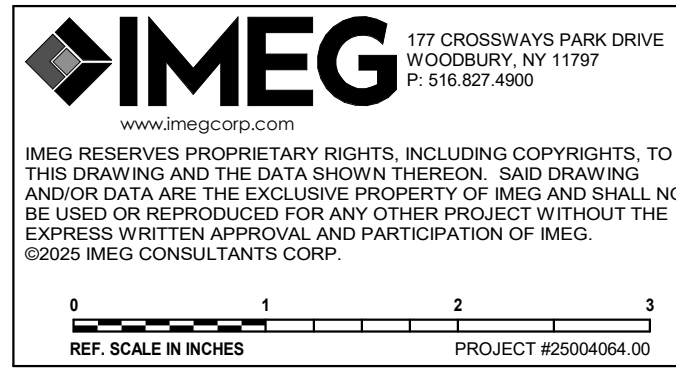


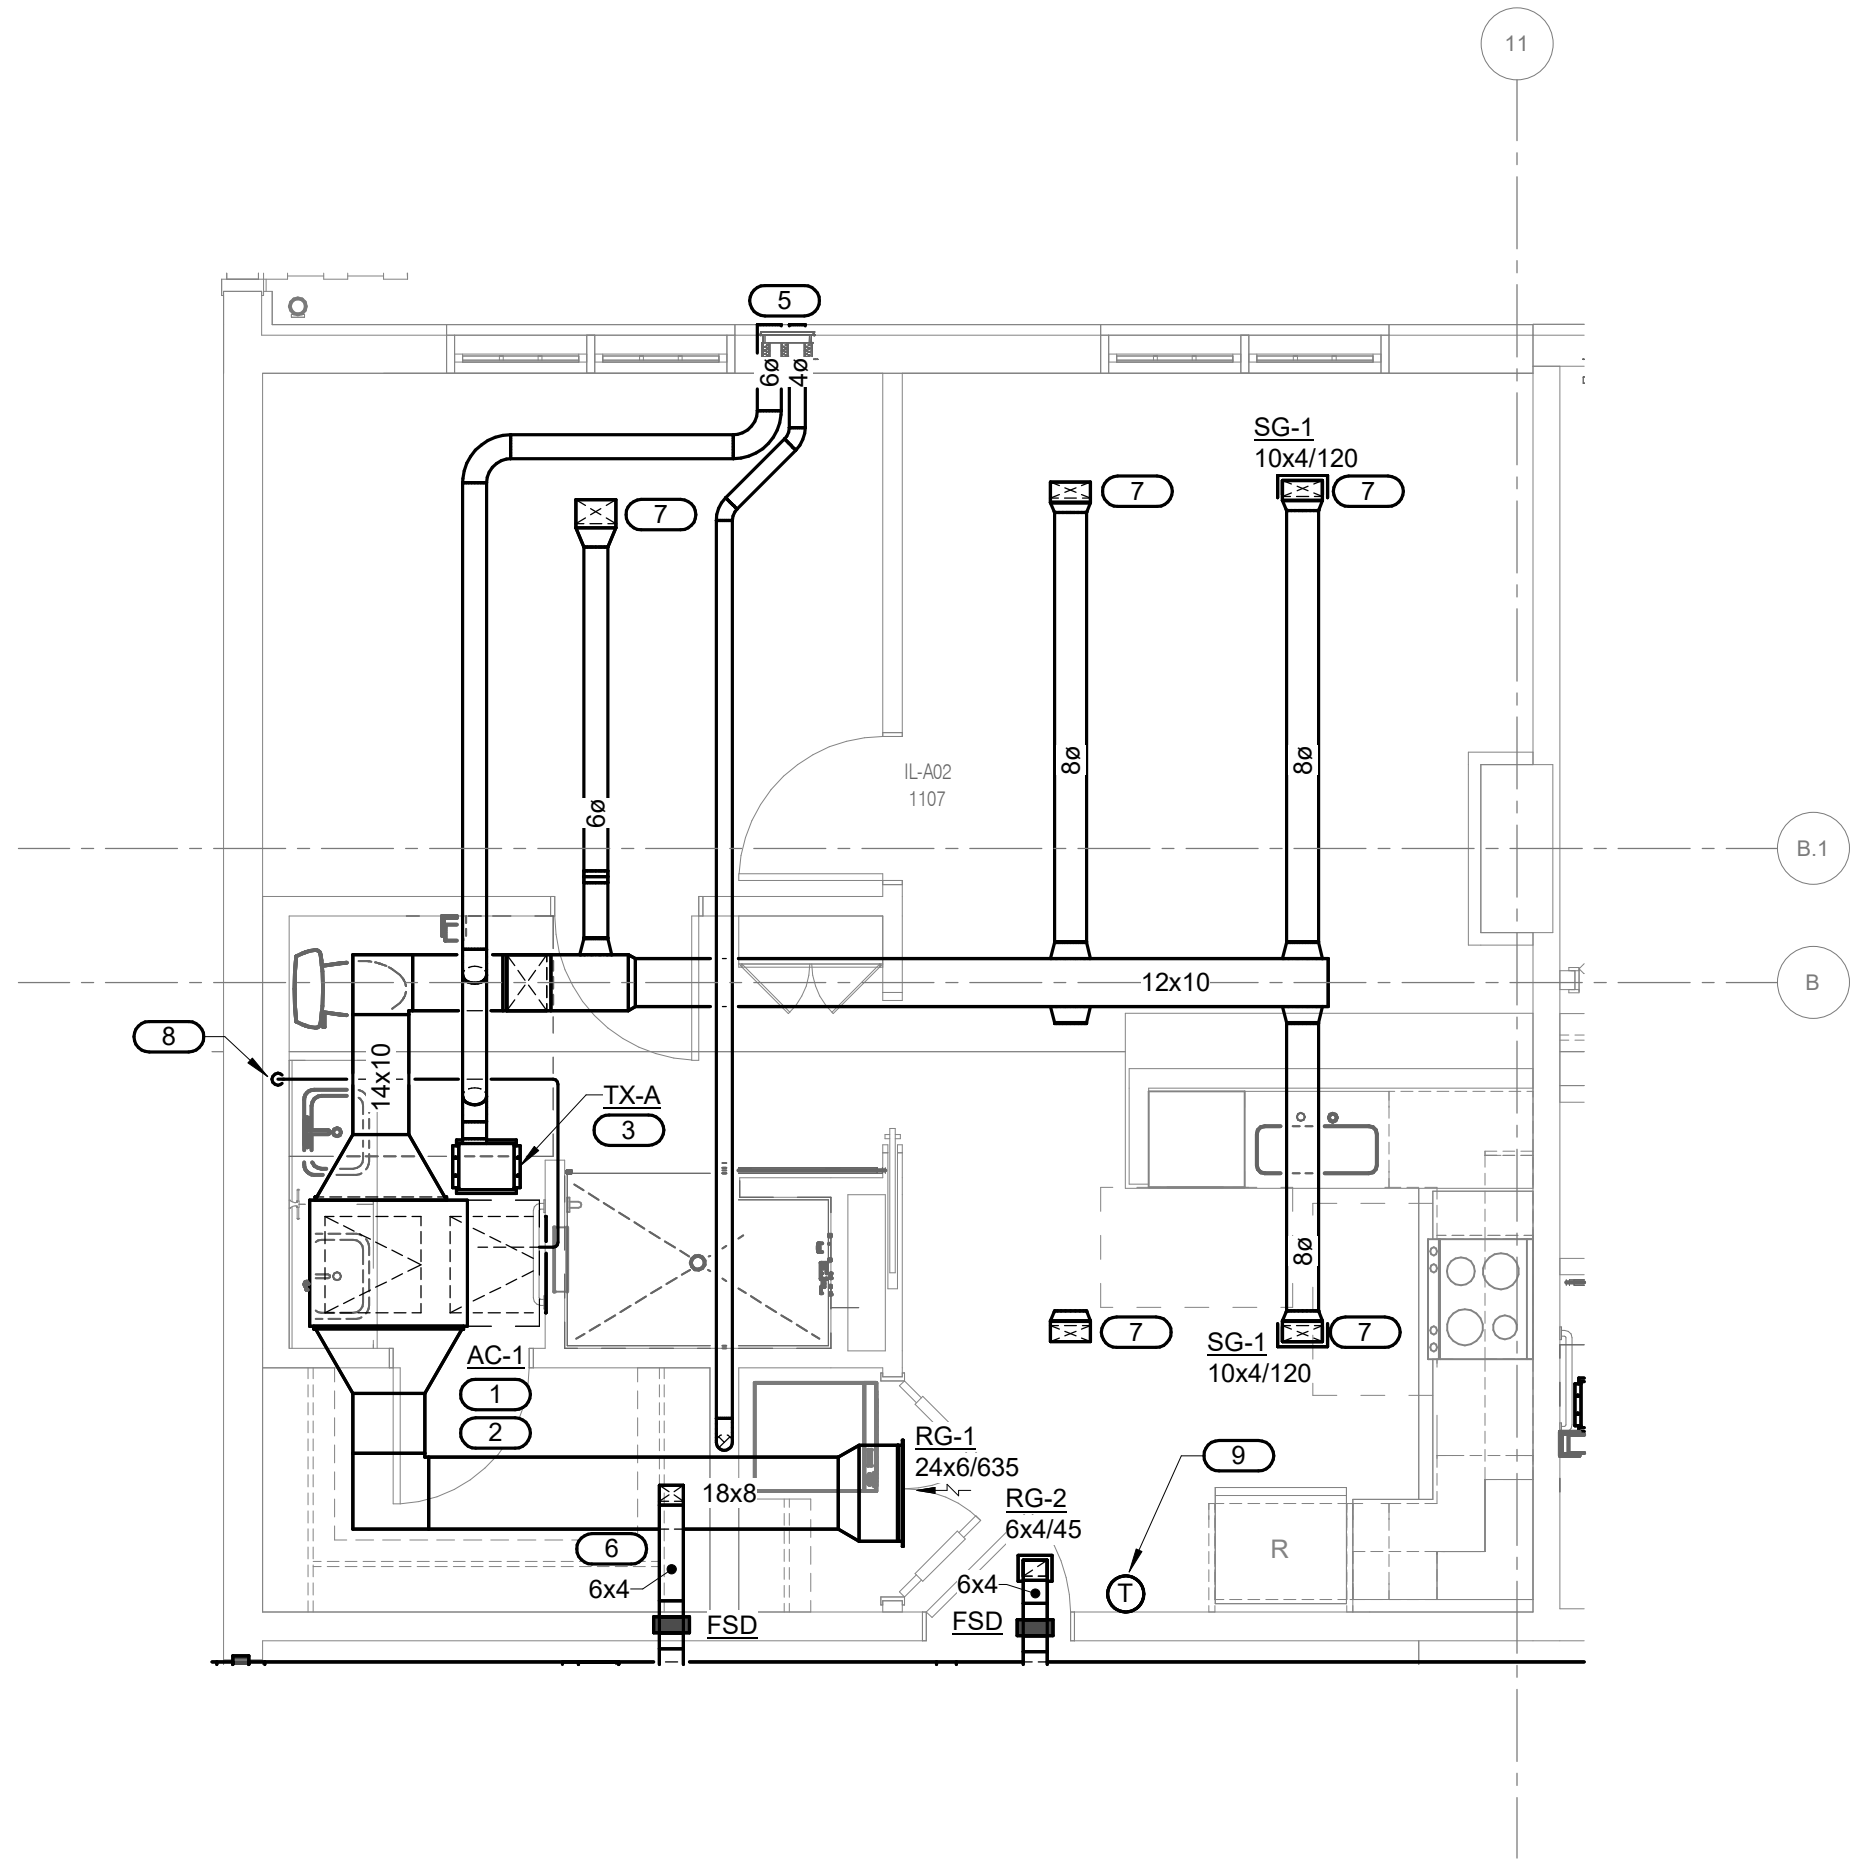


1 MECH. UNIT A02 -1 BED 1 BATH - PLAN - AC- 1 - FIRST FLOOR
1/4" = 1'-0"

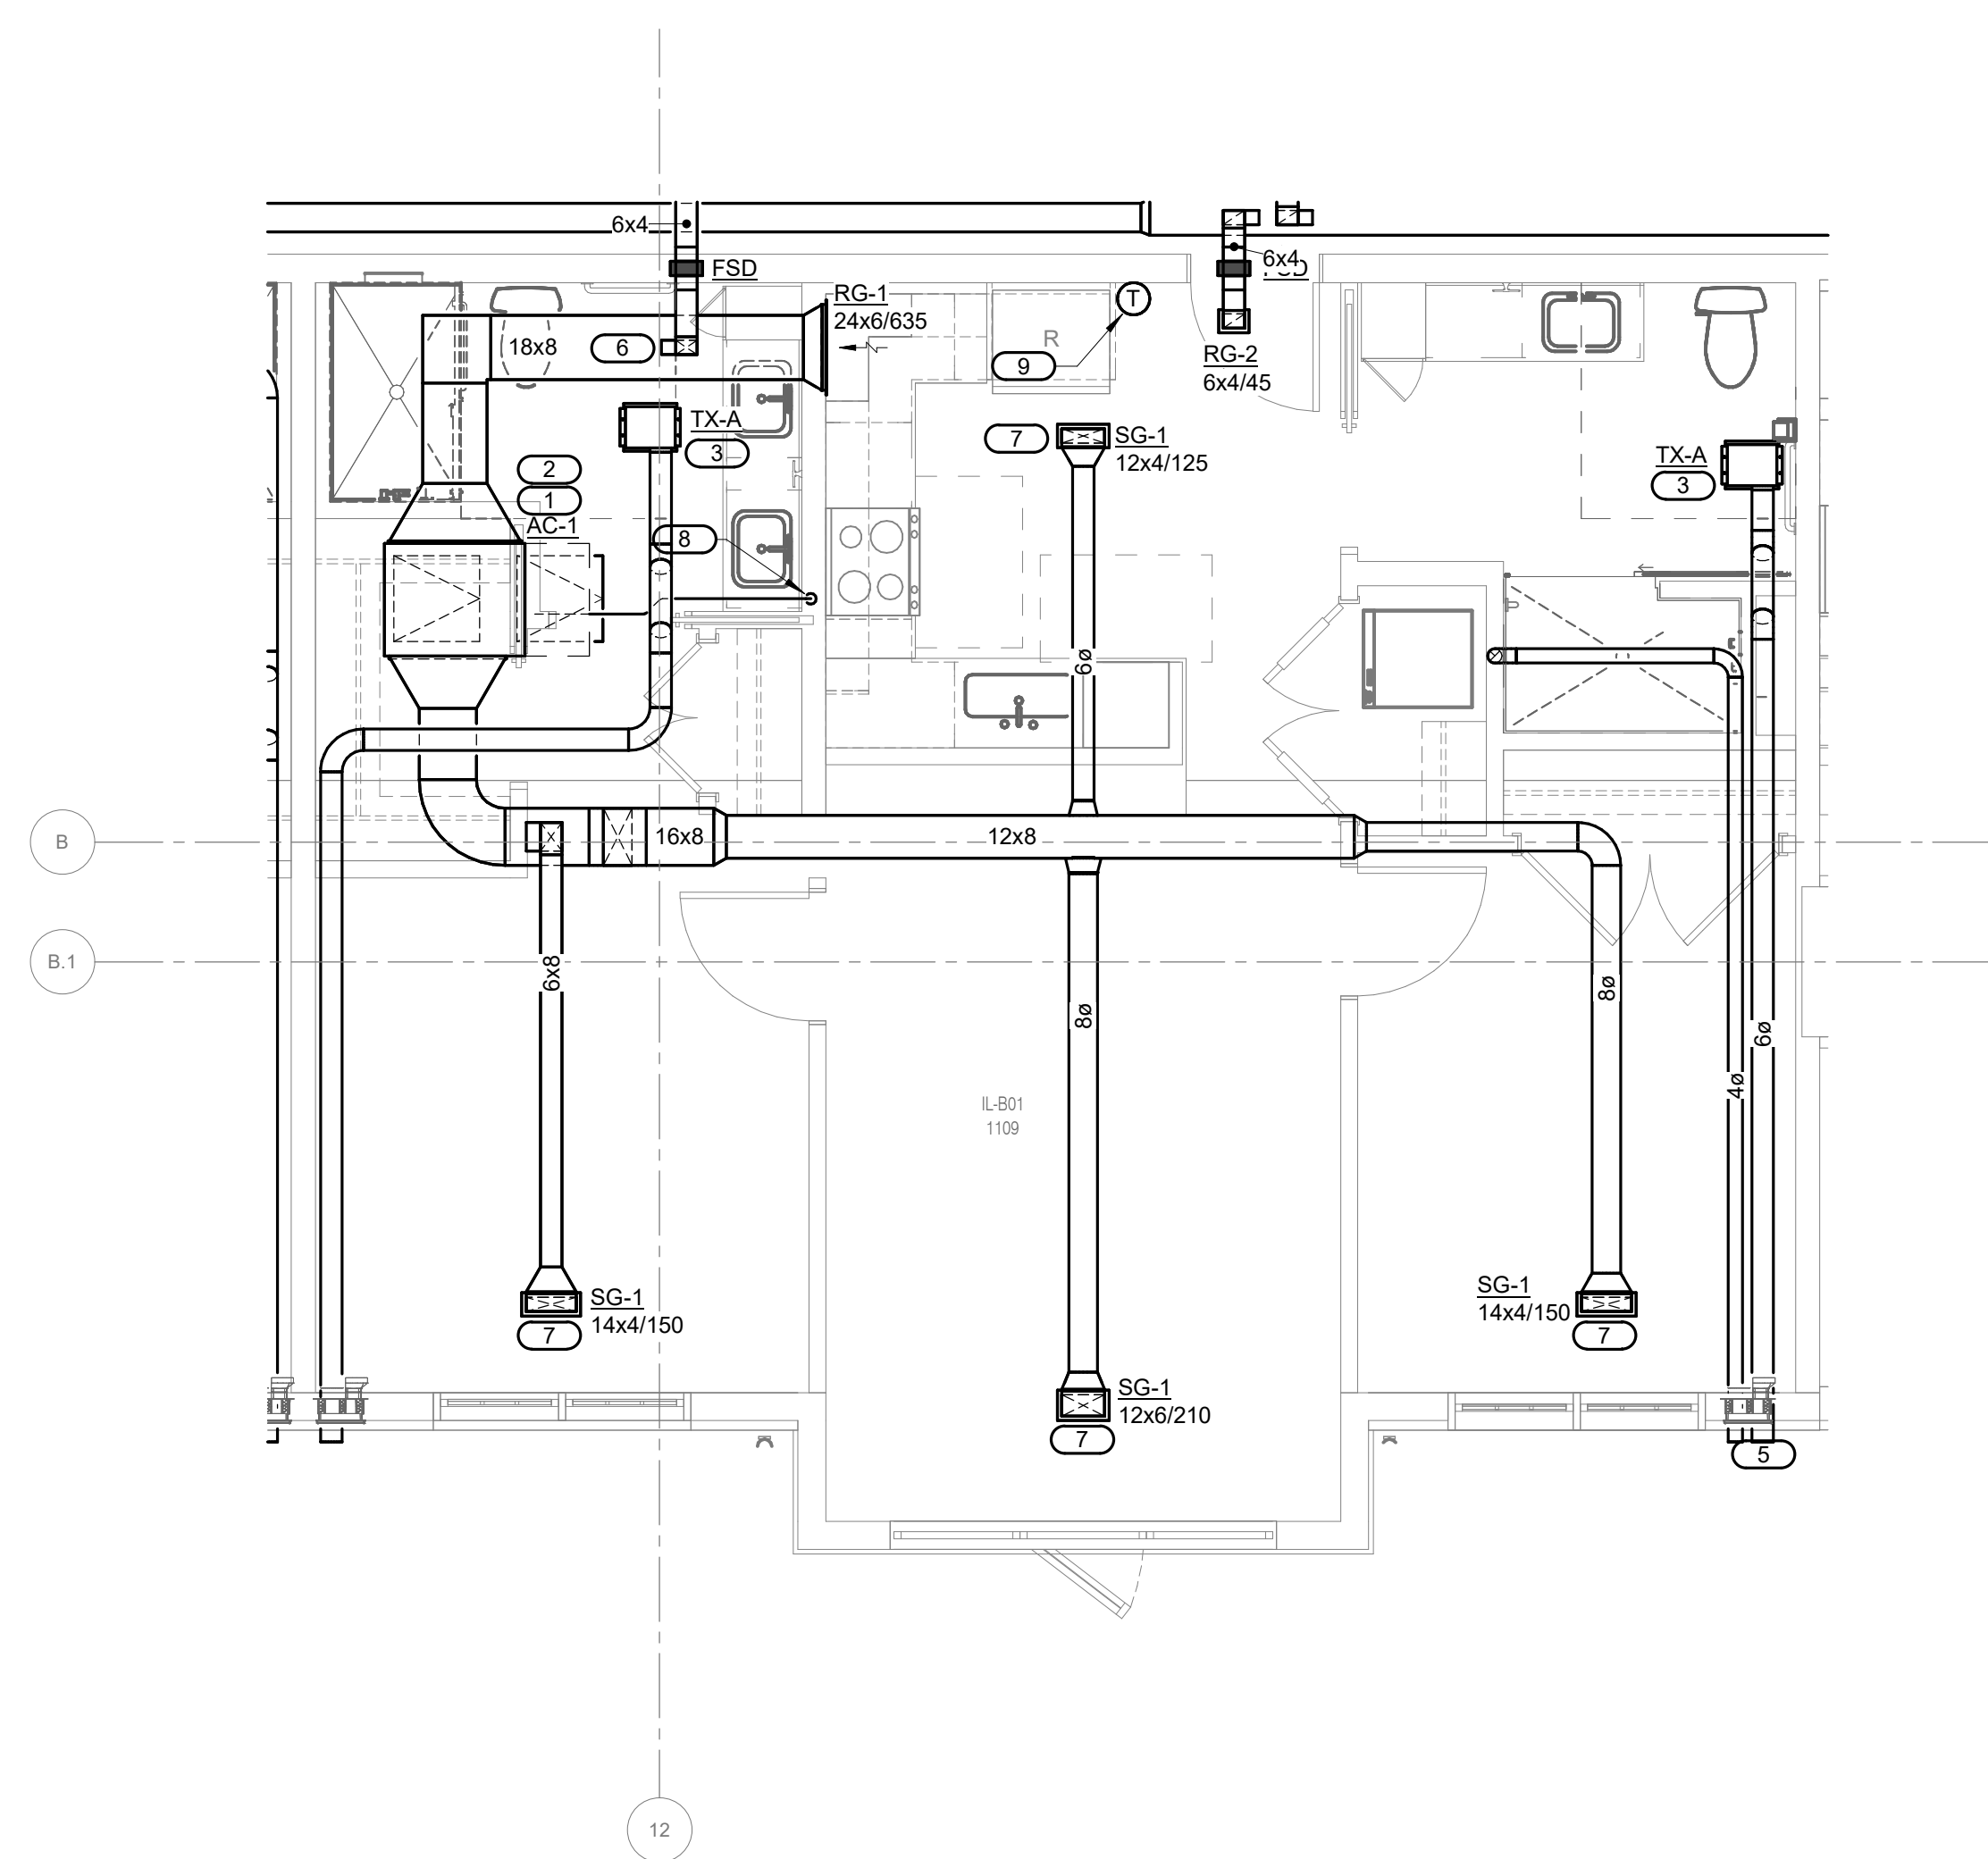

2 MECH. UNIT B01 - 2 BED 2 BATH - PLAN - AC-1 - FIRST FLOOR
1/4" = 1'-0"

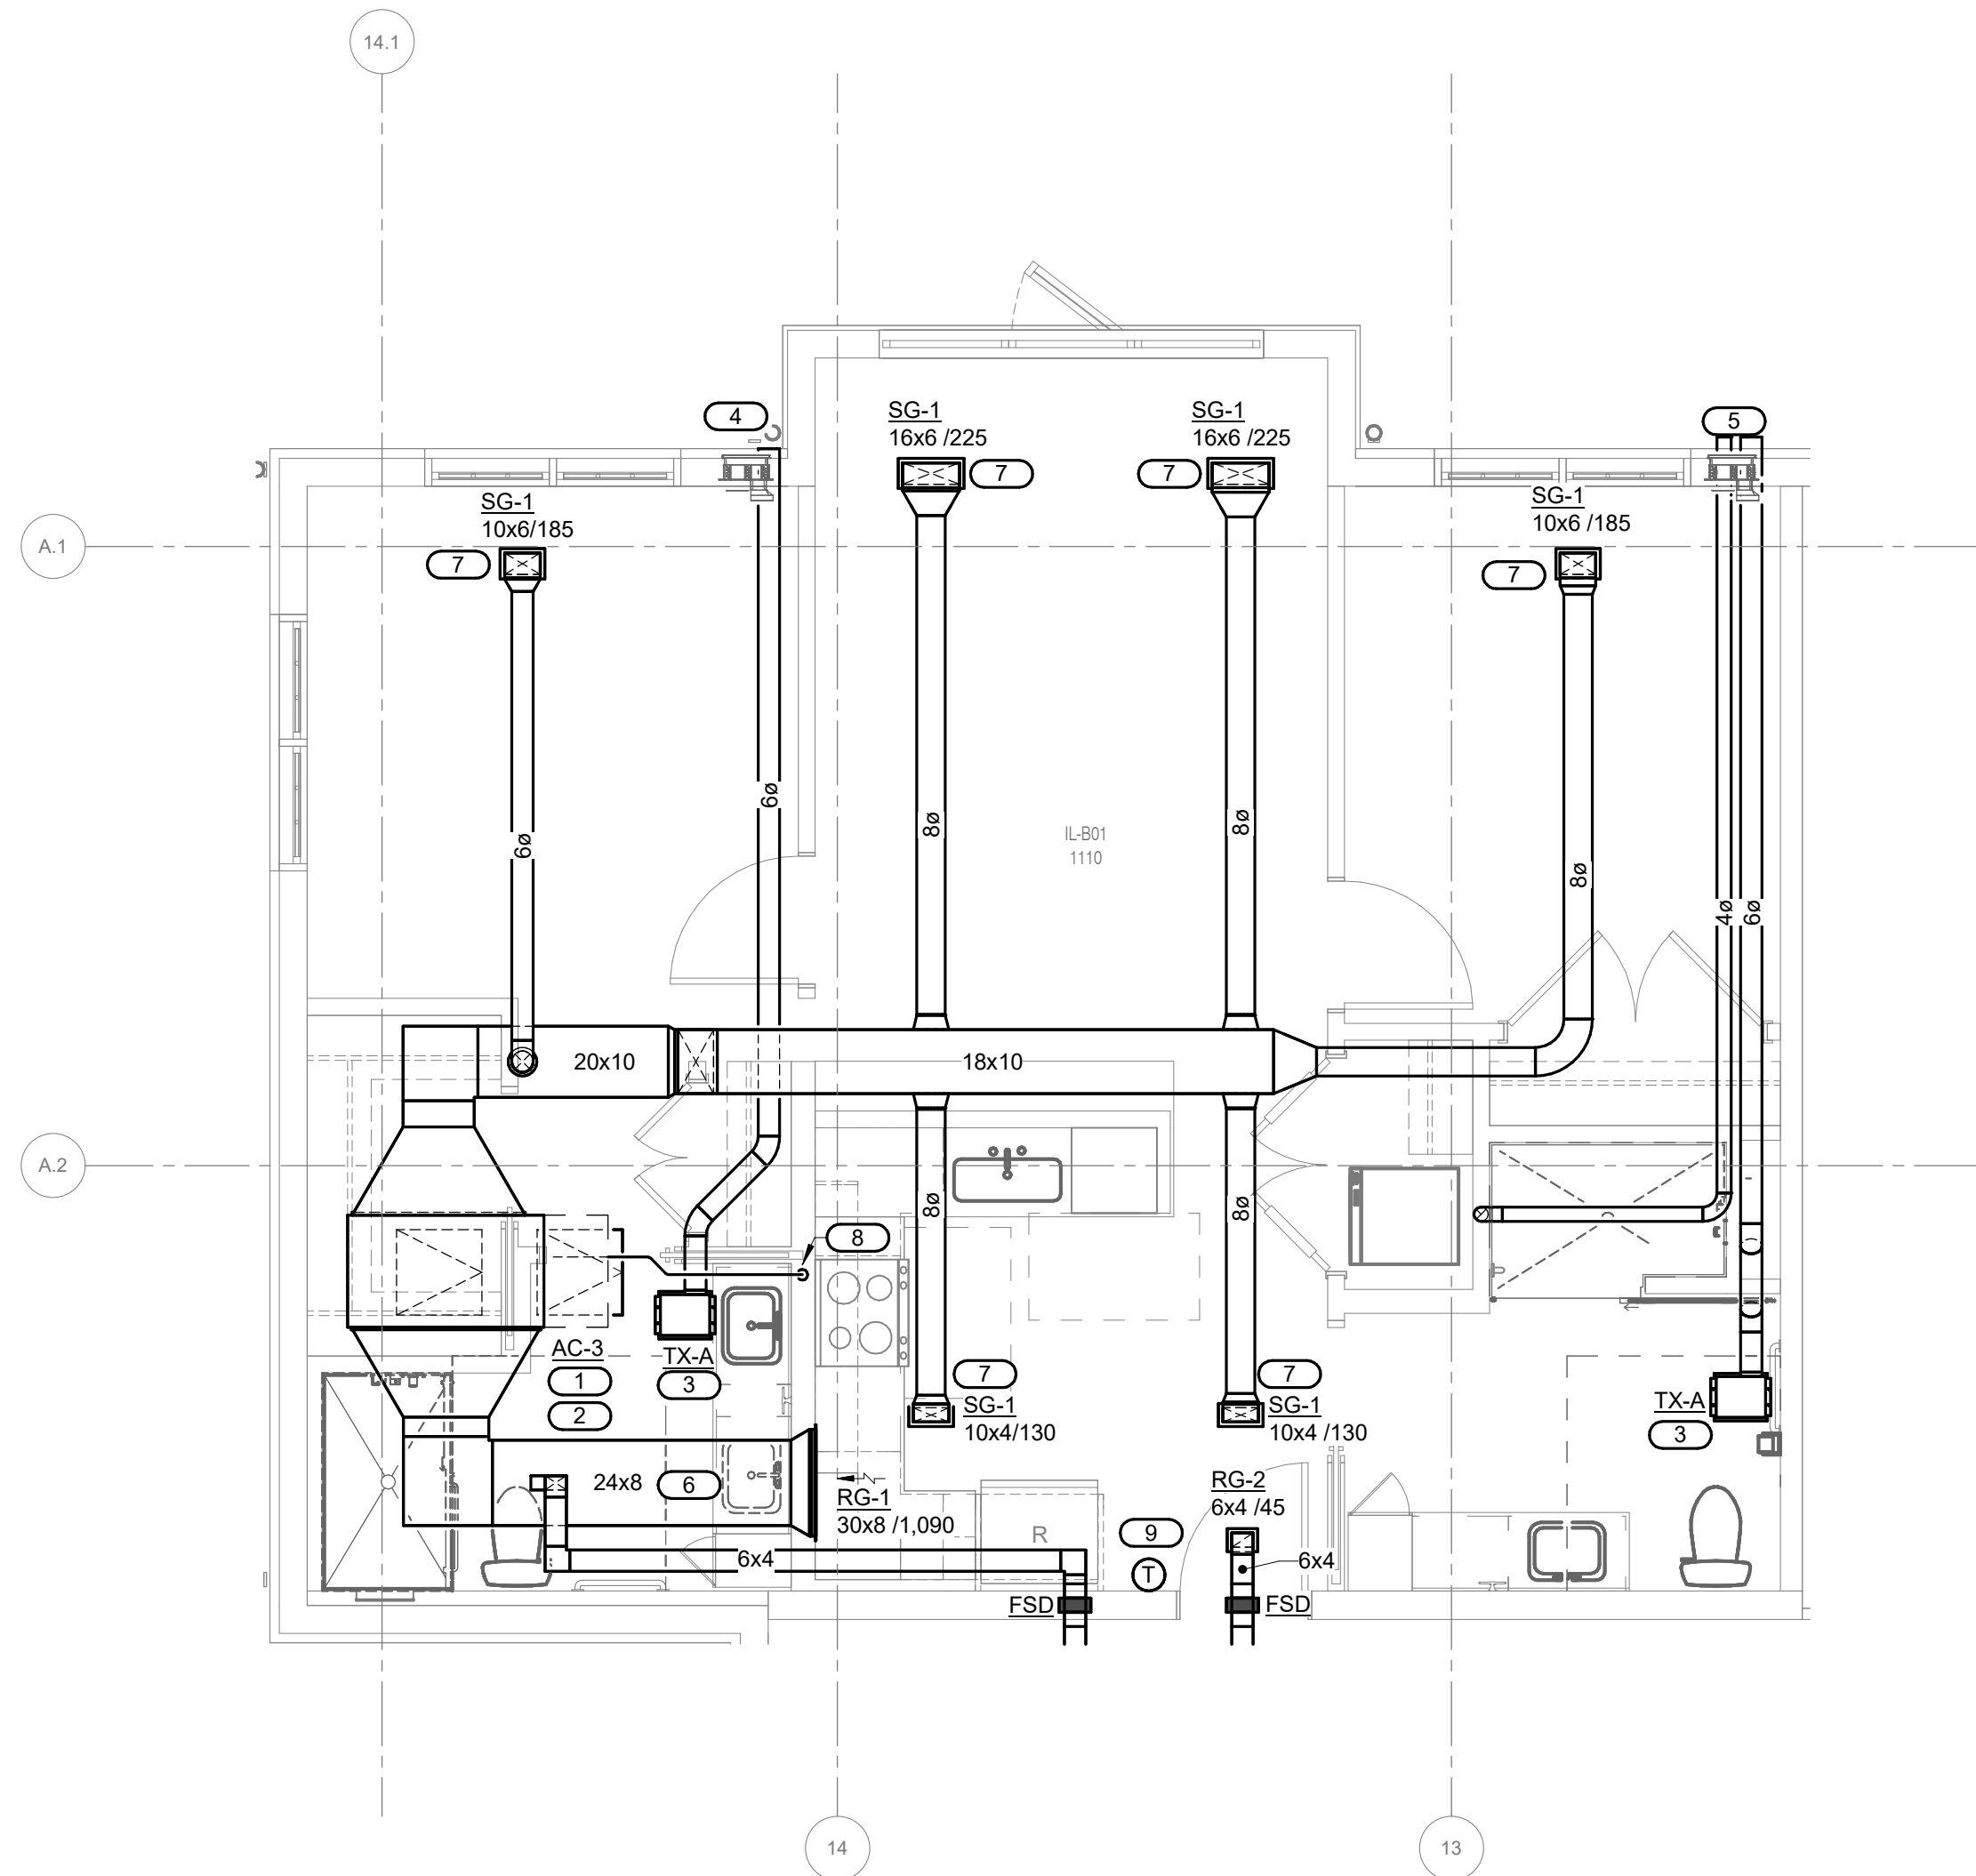

3 MECH. UNIT B01 - 2 BED 2 BATH - PLAN - AC-3 - FIRST FLOOR
1/4" = 1'-0"

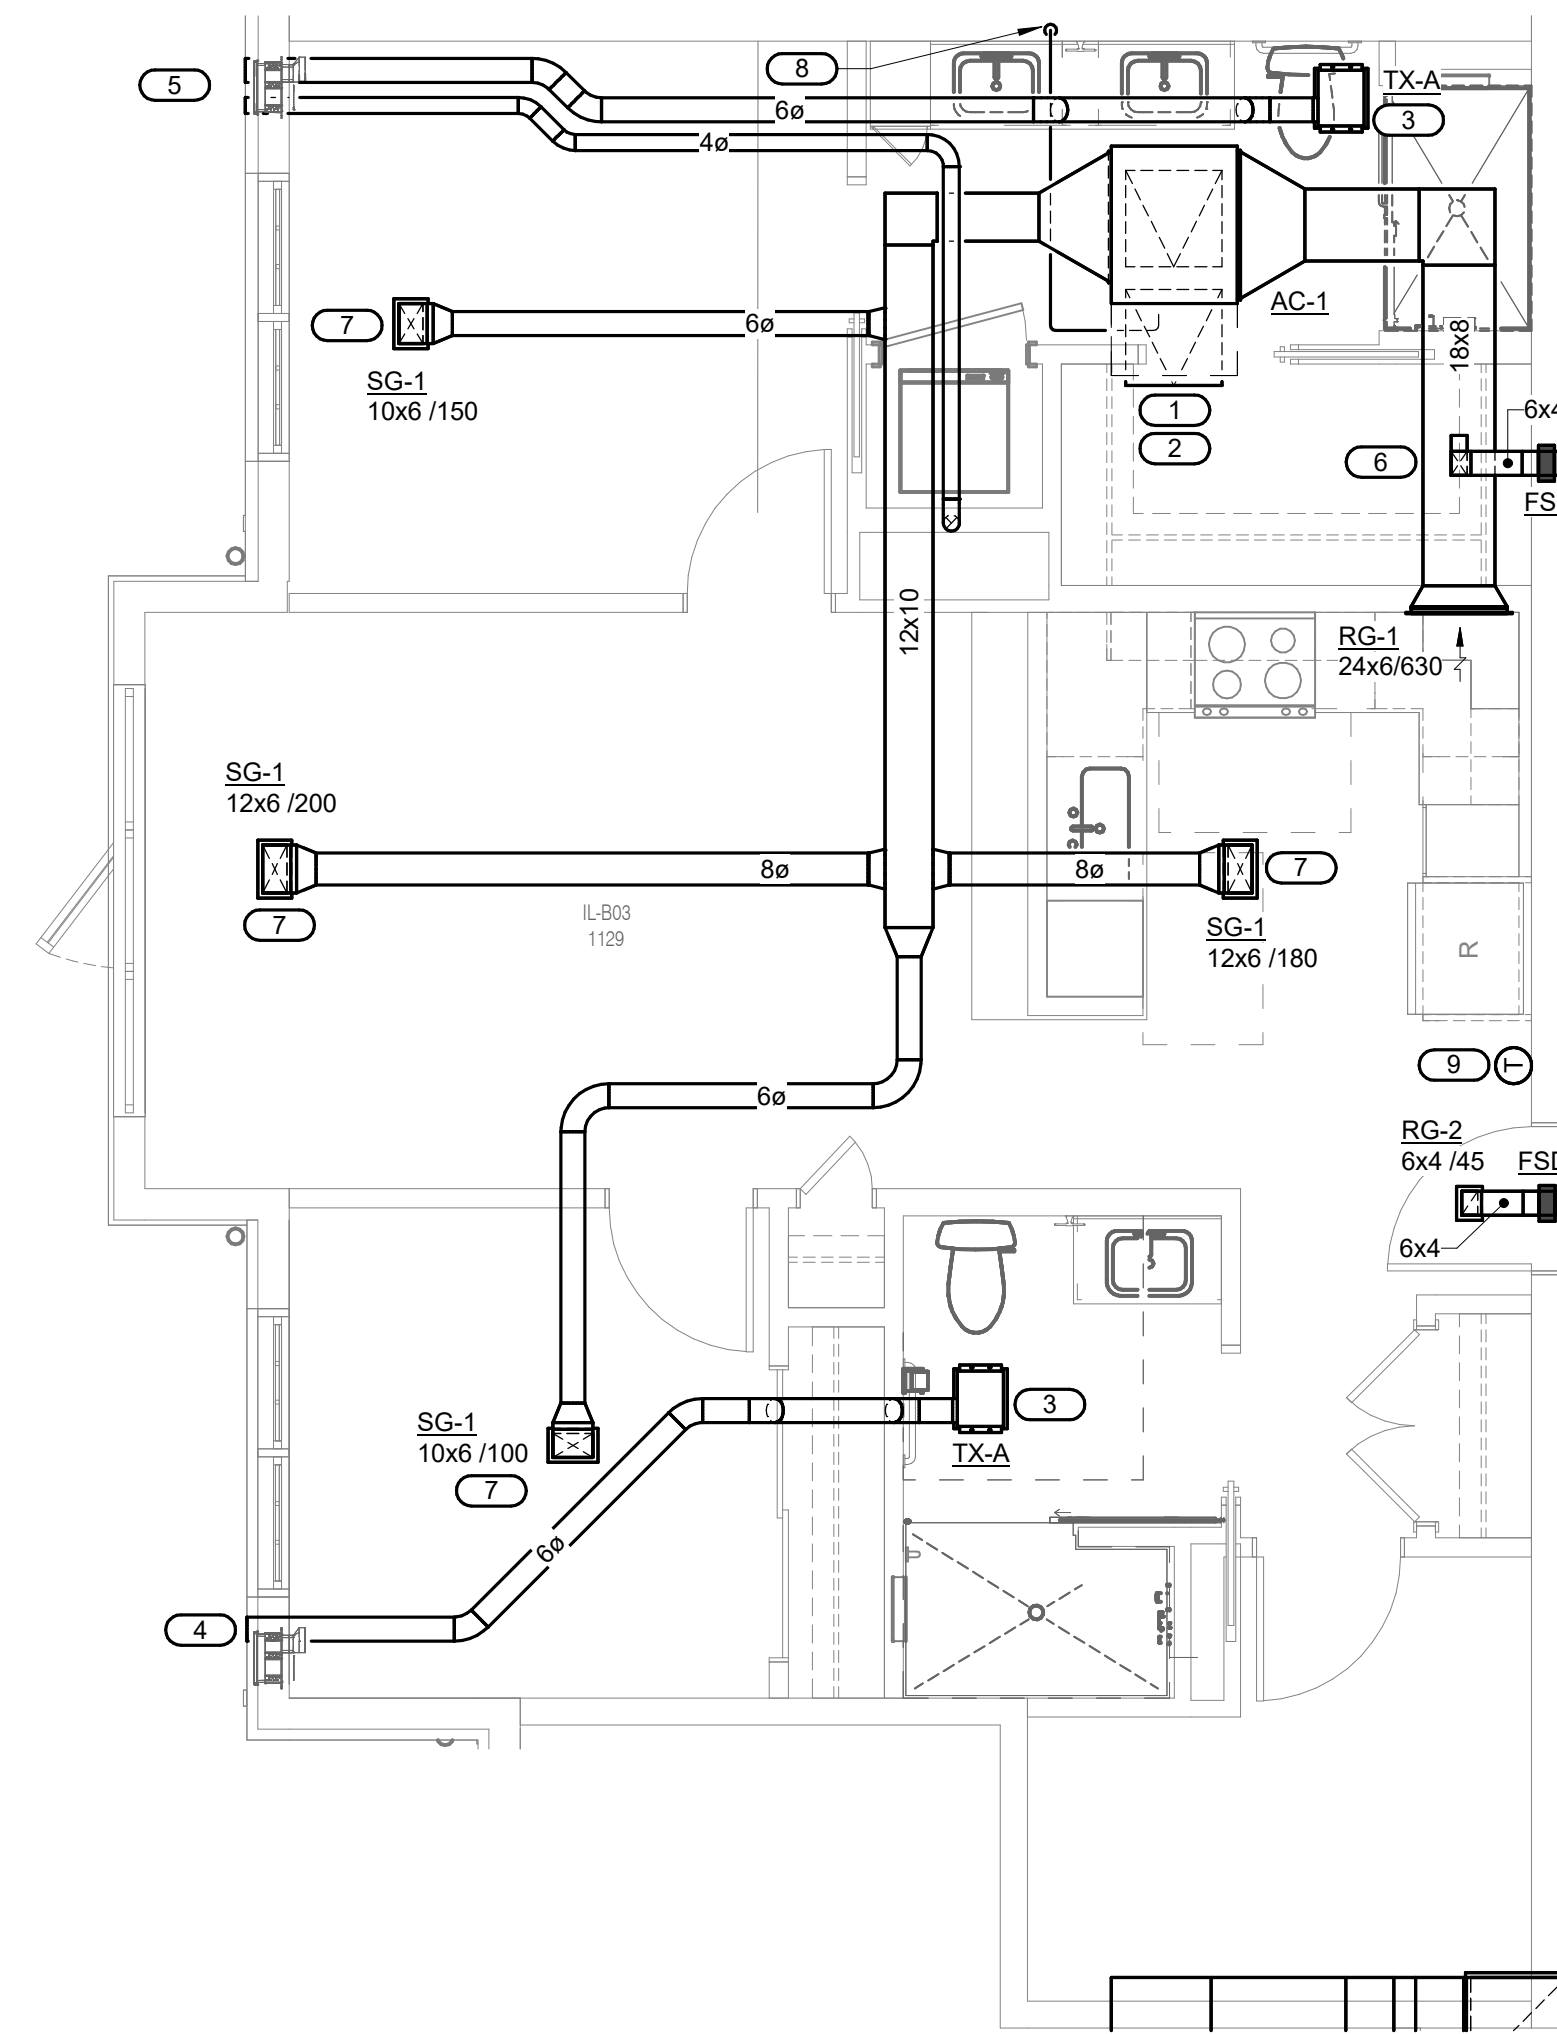

4 MECH. UNIT B03 - 2 BED 2 BATH - PLAN - AC-1 - FIRST FLOOR
1/4" = 1'-0"

KEYNOTES:

1. NEW FAN COIL UNIT MOUNTED ABOVE CEILING PER MANUFACTURER RECOMMENDATIONS. PROVIDE ACCESS PANEL AS REQUIRED FOR UNIT MAINTENANCE.
2. ROUTE REFRIGERANT LINES FROM FAN COIL UNIT TO ASSOCIATED CONDENSING UNIT ON ROOF AS REQUIRED. SIZE REFRIGERANT LINES PER MANUFACTURER RECOMMENDATIONS. DO NOT EXCEED MAXIMUM EQUIVALENT REFRIGERANT LENGTHS.
3. NEW EXHAUST FAN INSTALLED IN BATHROOM CEILING PER MANUFACTURER RECOMMENDATIONS.
4. ROUTE EXHAUST DUCTWORK TO EXTERIOR WALL AS REQUIRED. PROVIDE X-VENT MODEL "XSEB-P" AT DUCTWORK TERMINATION POINT. MAINTAIN MINIMUM 3'-0" FROM WINDOW OPENINGS AND 10'-0" FROM ANY OUTDOOR AIR INTAKES.
5. ROUTE EXHAUST DUCTWORK TO EXTERIOR WALL AS REQUIRED. PROVIDE X-VENT MODEL "XVEB-46-P" FOR BOTH DUCTWORK LINES AT TERMINATION POINT. MAINTAIN MINIMUM 3'-0" FROM WINDOW OPENINGS AND 10'-0" FROM ANY OUTDOOR AIR INTAKES.
6. PROVIDE 30" LONG RETURN AIR PLENUM. MATCH SIZE OF UNIT RETURN AIR OPENING. EXHAUST OUTLET AS REQUIRED.
7. PROVIDE SOUTHWARK MODEL 59FLD, UL APPROVED, RADIATION DAMPER BOOT ABOVE GRILLE.
8. PROVIDE A 1-1/4" DRAIN PIPE CONNECTION FROM THE INDOOR UNIT TO THE LAVATORY SANITARY LINE. REFER TO DETAIL 11MS02 FOR THE CONNECTION REQUIREMENTS.
9. MOUNT THE THERMOSTAT ON THE WALL AT 48" ABOVE FINISHED FLOOR (A.F.F.).

HKS

ARCHITECT
HKS ARCHITECTS, P.C.
30 WEST 26th STREET, 12th FLOOR
NEW YORK, NY 10010

STRUCTURAL
IMEG
1411 BROADWAY, SUITE 600
NEW YORK, NY 10018

MEP ENGINEER
IMEG
177 CROSWAYS PARK DRIVE
WOODBURY, NY 11797

LV ENGINEER
TATEROY
765 HICKORY FLAT HWY, SUITE 200
WOODSTOCK, GA 30188

LANDSCAPE ARCHITECT
MFPF
120 BROADWAY, 20TH FLOOR
NEW YORK, NY 10271

POOL DESIGNER
COUNSLMANHUNSAKER & ASSOCIATES, INC.
12851 MANCHESTER ROAD, SUITE 120
ST. LOUIS, MO 63131

FOOD SERVICE & LAUNDRY
CLARK
2551 HORSESHOE RD.
LANCASTER, PA 17601


SUNRISE[®]
SENIOR LIVING
RYE BROOK

DOB BSCAN | DOB STAMP & SIGNATURES

SEAL & SIGNATURE

CON NO.: 111AAA

KEY PLAN

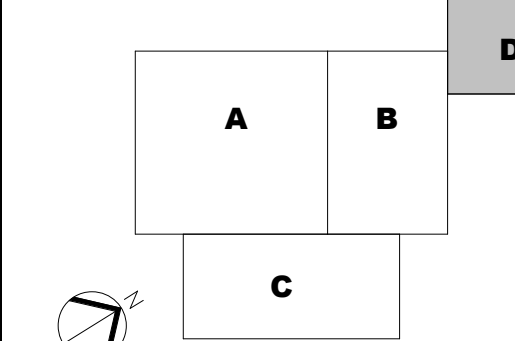

NO.	DESCRIPTION	DATE
1	DD Program Print	08/26/25
2	DESIGN DEVELOPMENT	11/05/25
3	EXTERIOR BUILDING PERMIT	12/03/25
4	100% DESIGN DEVELOPMENT	01/08/26
5	ISSUED FOR PERMIT	06/05/26

IMEG
177 CROSWAYS PARK DRIVE
WOODBURY, NY 11797
P: 516-927-6900

IMEG RESERVES PROPRIETARY RIGHTS, INCLUDING COPYRIGHTS, TO THIS DRAWING AND THE DATA SHOWN THEREON. NO PART OF THIS DRAWING OR DATA ARE THE EXCLUSIVE PROPERTY OF IMEG AND SHALL NOT BE USED OR REPRODUCED FOR ANY OTHER PROJECT WITHOUT THE EXPRESS WRITTEN APPROVAL AND PARTICIPATION OF IMEG. ©2025 IMEG CONSULTANTS CORP.

REF. SCALE IN INCHES
PROJECT #20240404.01

HKS PROJECT NUMBER
25004064.00


DATE
07/15/26

ISSUE
ISSUED FOR GMP

SHEET TITLE
UNIT PLANS IL - FIRST FLOOR - MECHANICAL

SHEET NO.

M2100
DOB FILE # DOB PAGE #

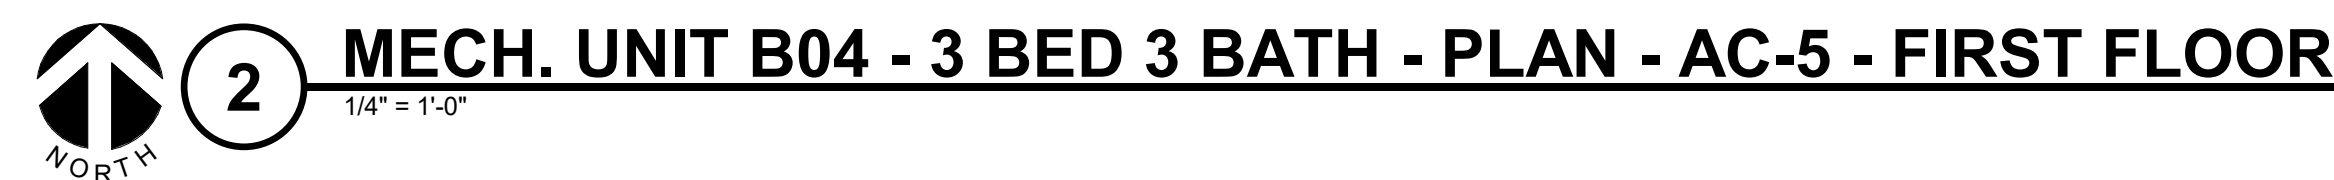

- 
- SUNRISE[®]**
SENIOR LIVING
RYE BROOK

SEAL & SIGNATURE_____

CON NO.: 111AAA
KEY PLAN_____

A diagram showing a 2x2 grid of cells labeled A, B, C, and D. Cell D is shaded gray. A compass is shown in the bottom left corner.

REVISION		
NO.	DESCRIPTION	DATE
1	DD Progress Print	08/28/25
2	DESIGN DEVELOPMENT	11/25/25
3	EXTERIOR BUILDING PERMIT	12/23/25
4	100% DESIGN DEVELOPMENT	01/30/26
5	ISSUED FOR PERMIT	06/05/26

HKS PROJECT NUMBER
85004864.00


DATE
07/15/26ISSUE
ISSUED BY

SHEET TITLE


SHEET TITLE
**UNIT PLANS IL - FIRST
FLOOR - MECHANICAL**

SHEET NO.


M2101

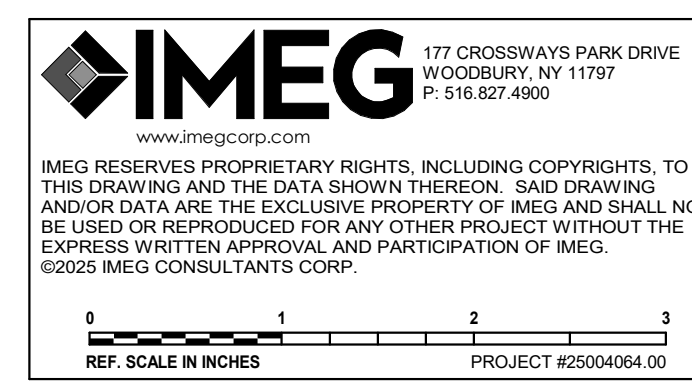


TITLE BLOCK VERSION: 2019030
MODEL: A:\projects\25004064\03 - Sunrise Rye Brook NY - Senior L.A.M.C. 2020\MEP25 - 2020\04\03 - L.A.E. 2019\03\01 - C.d
PRINT DATE: 11/02/2020 12:44:25 PM - TEMPLATE VERSION: 23.0.1

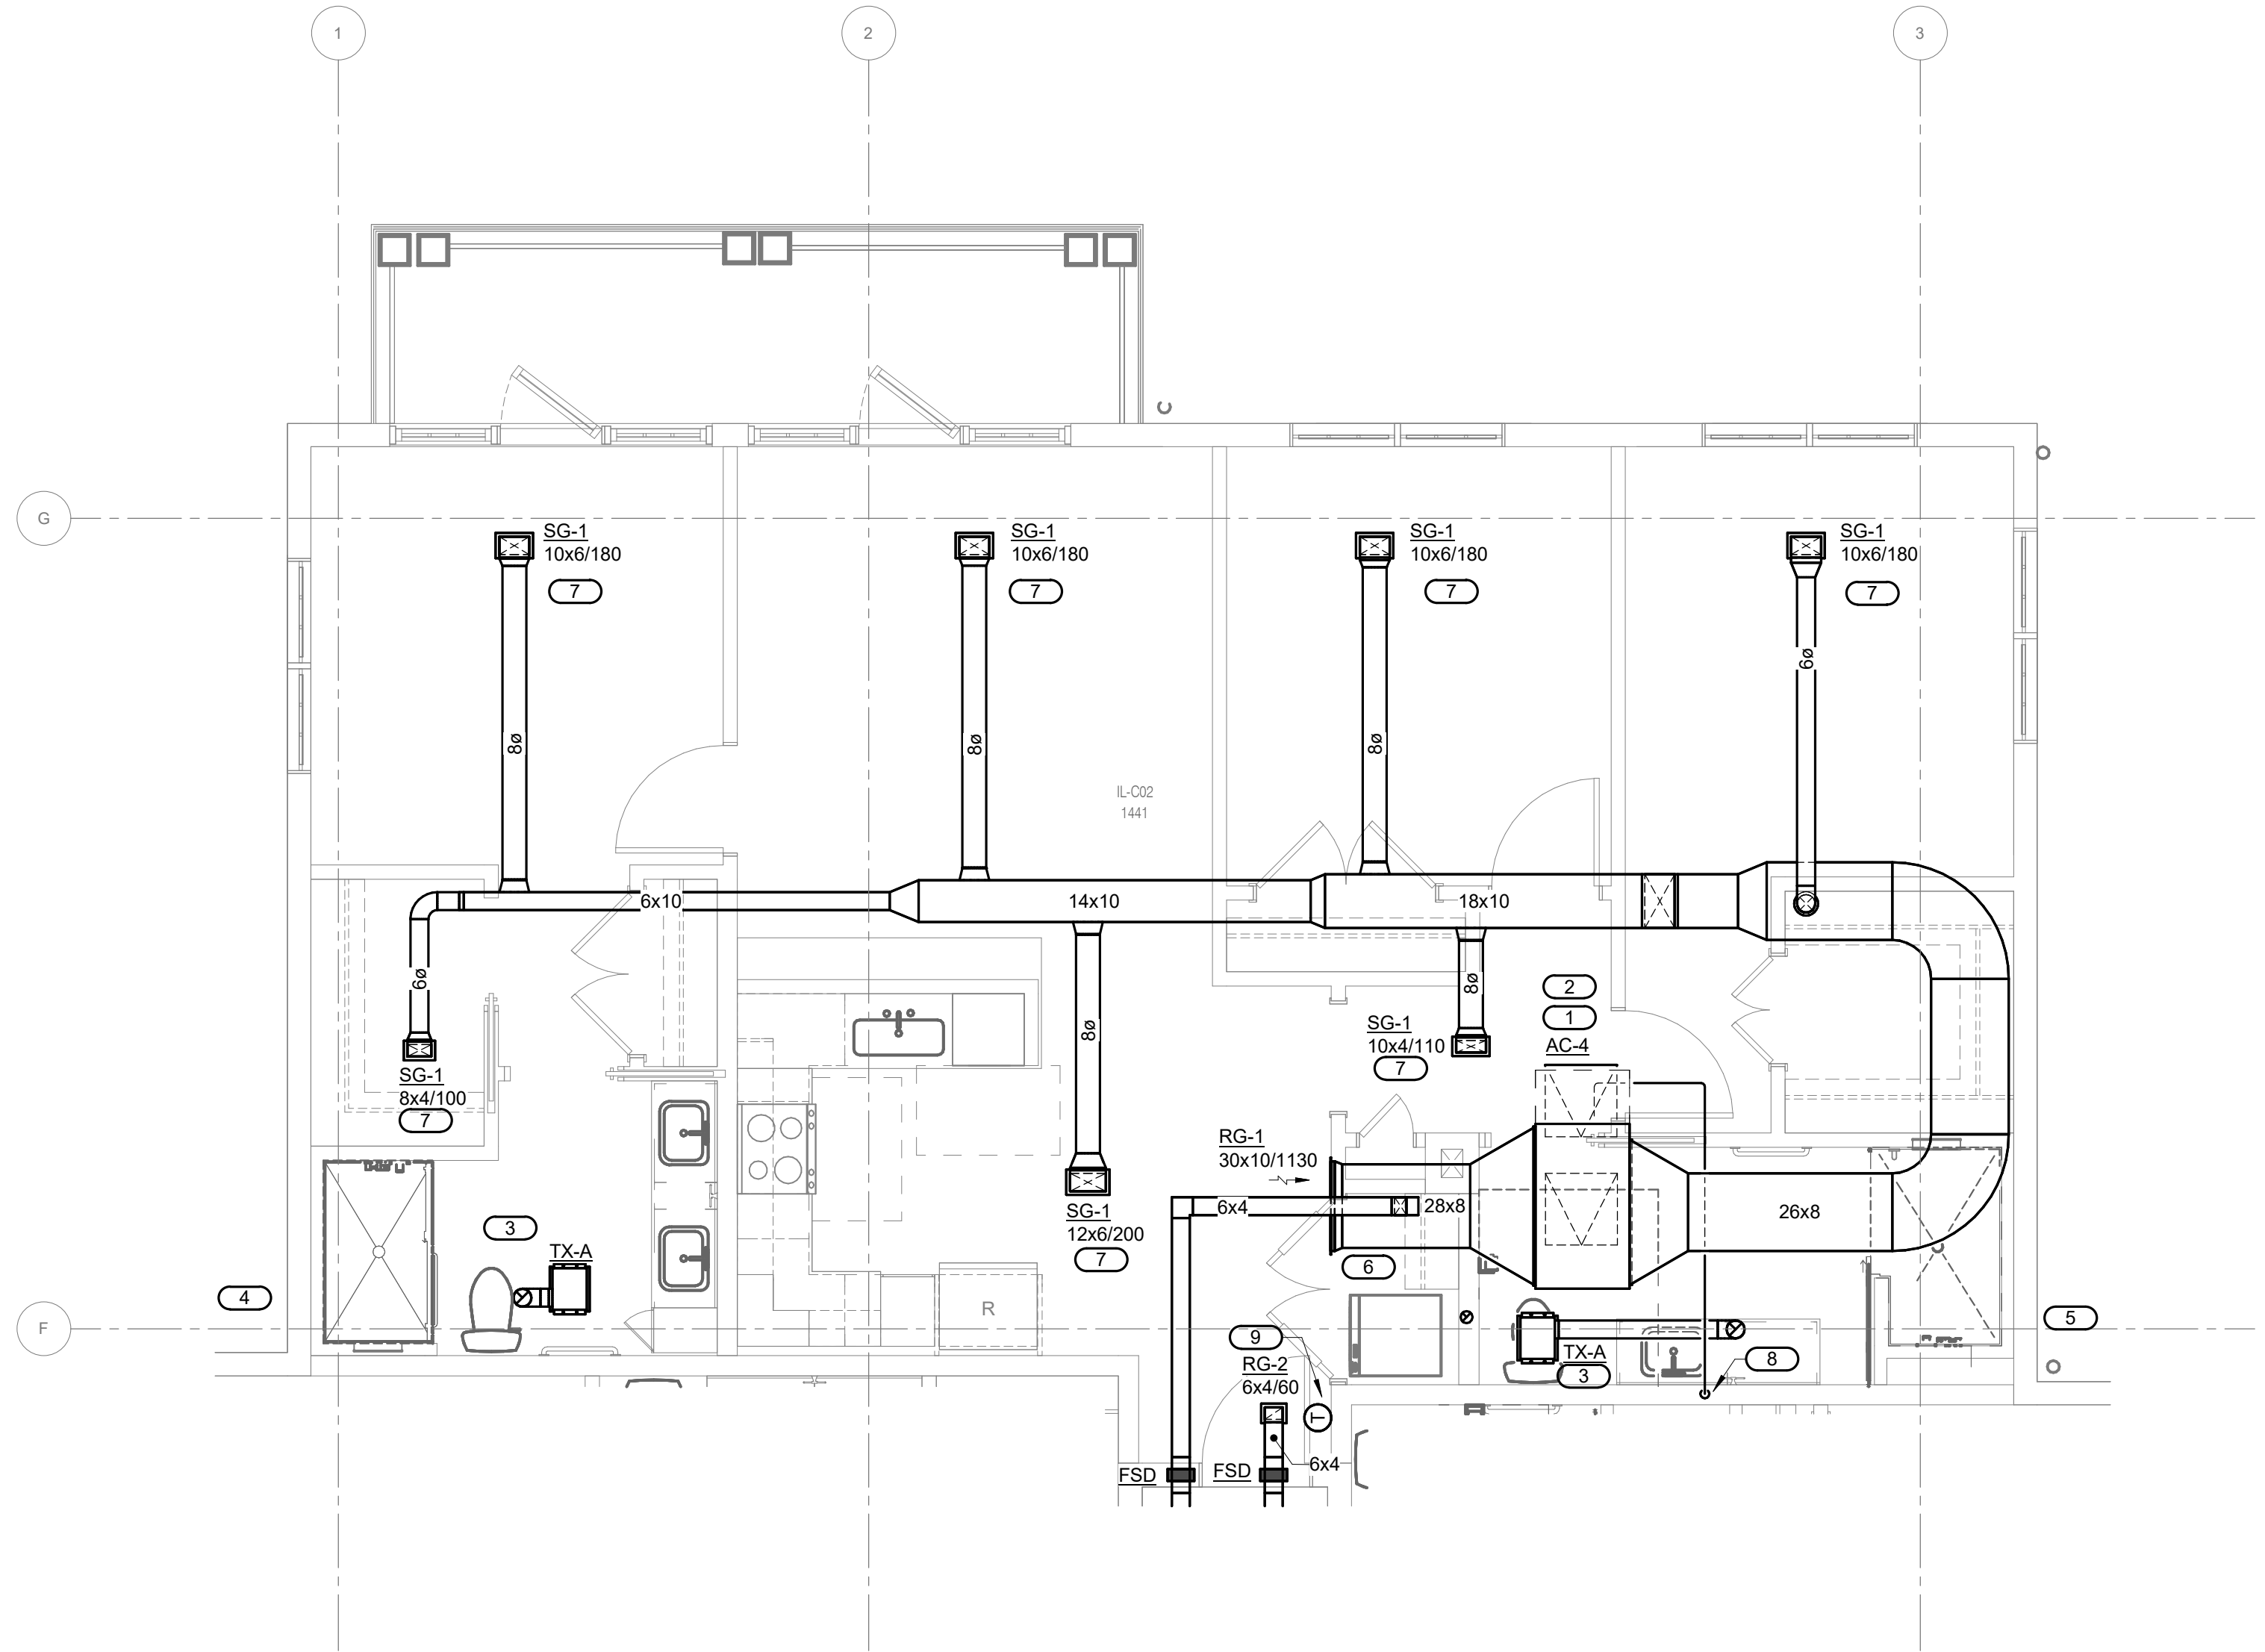


1 MECH. UNIT C02 - 3 BED 2 BATH - PLAN - AC-4
1/4" = 1'-0"

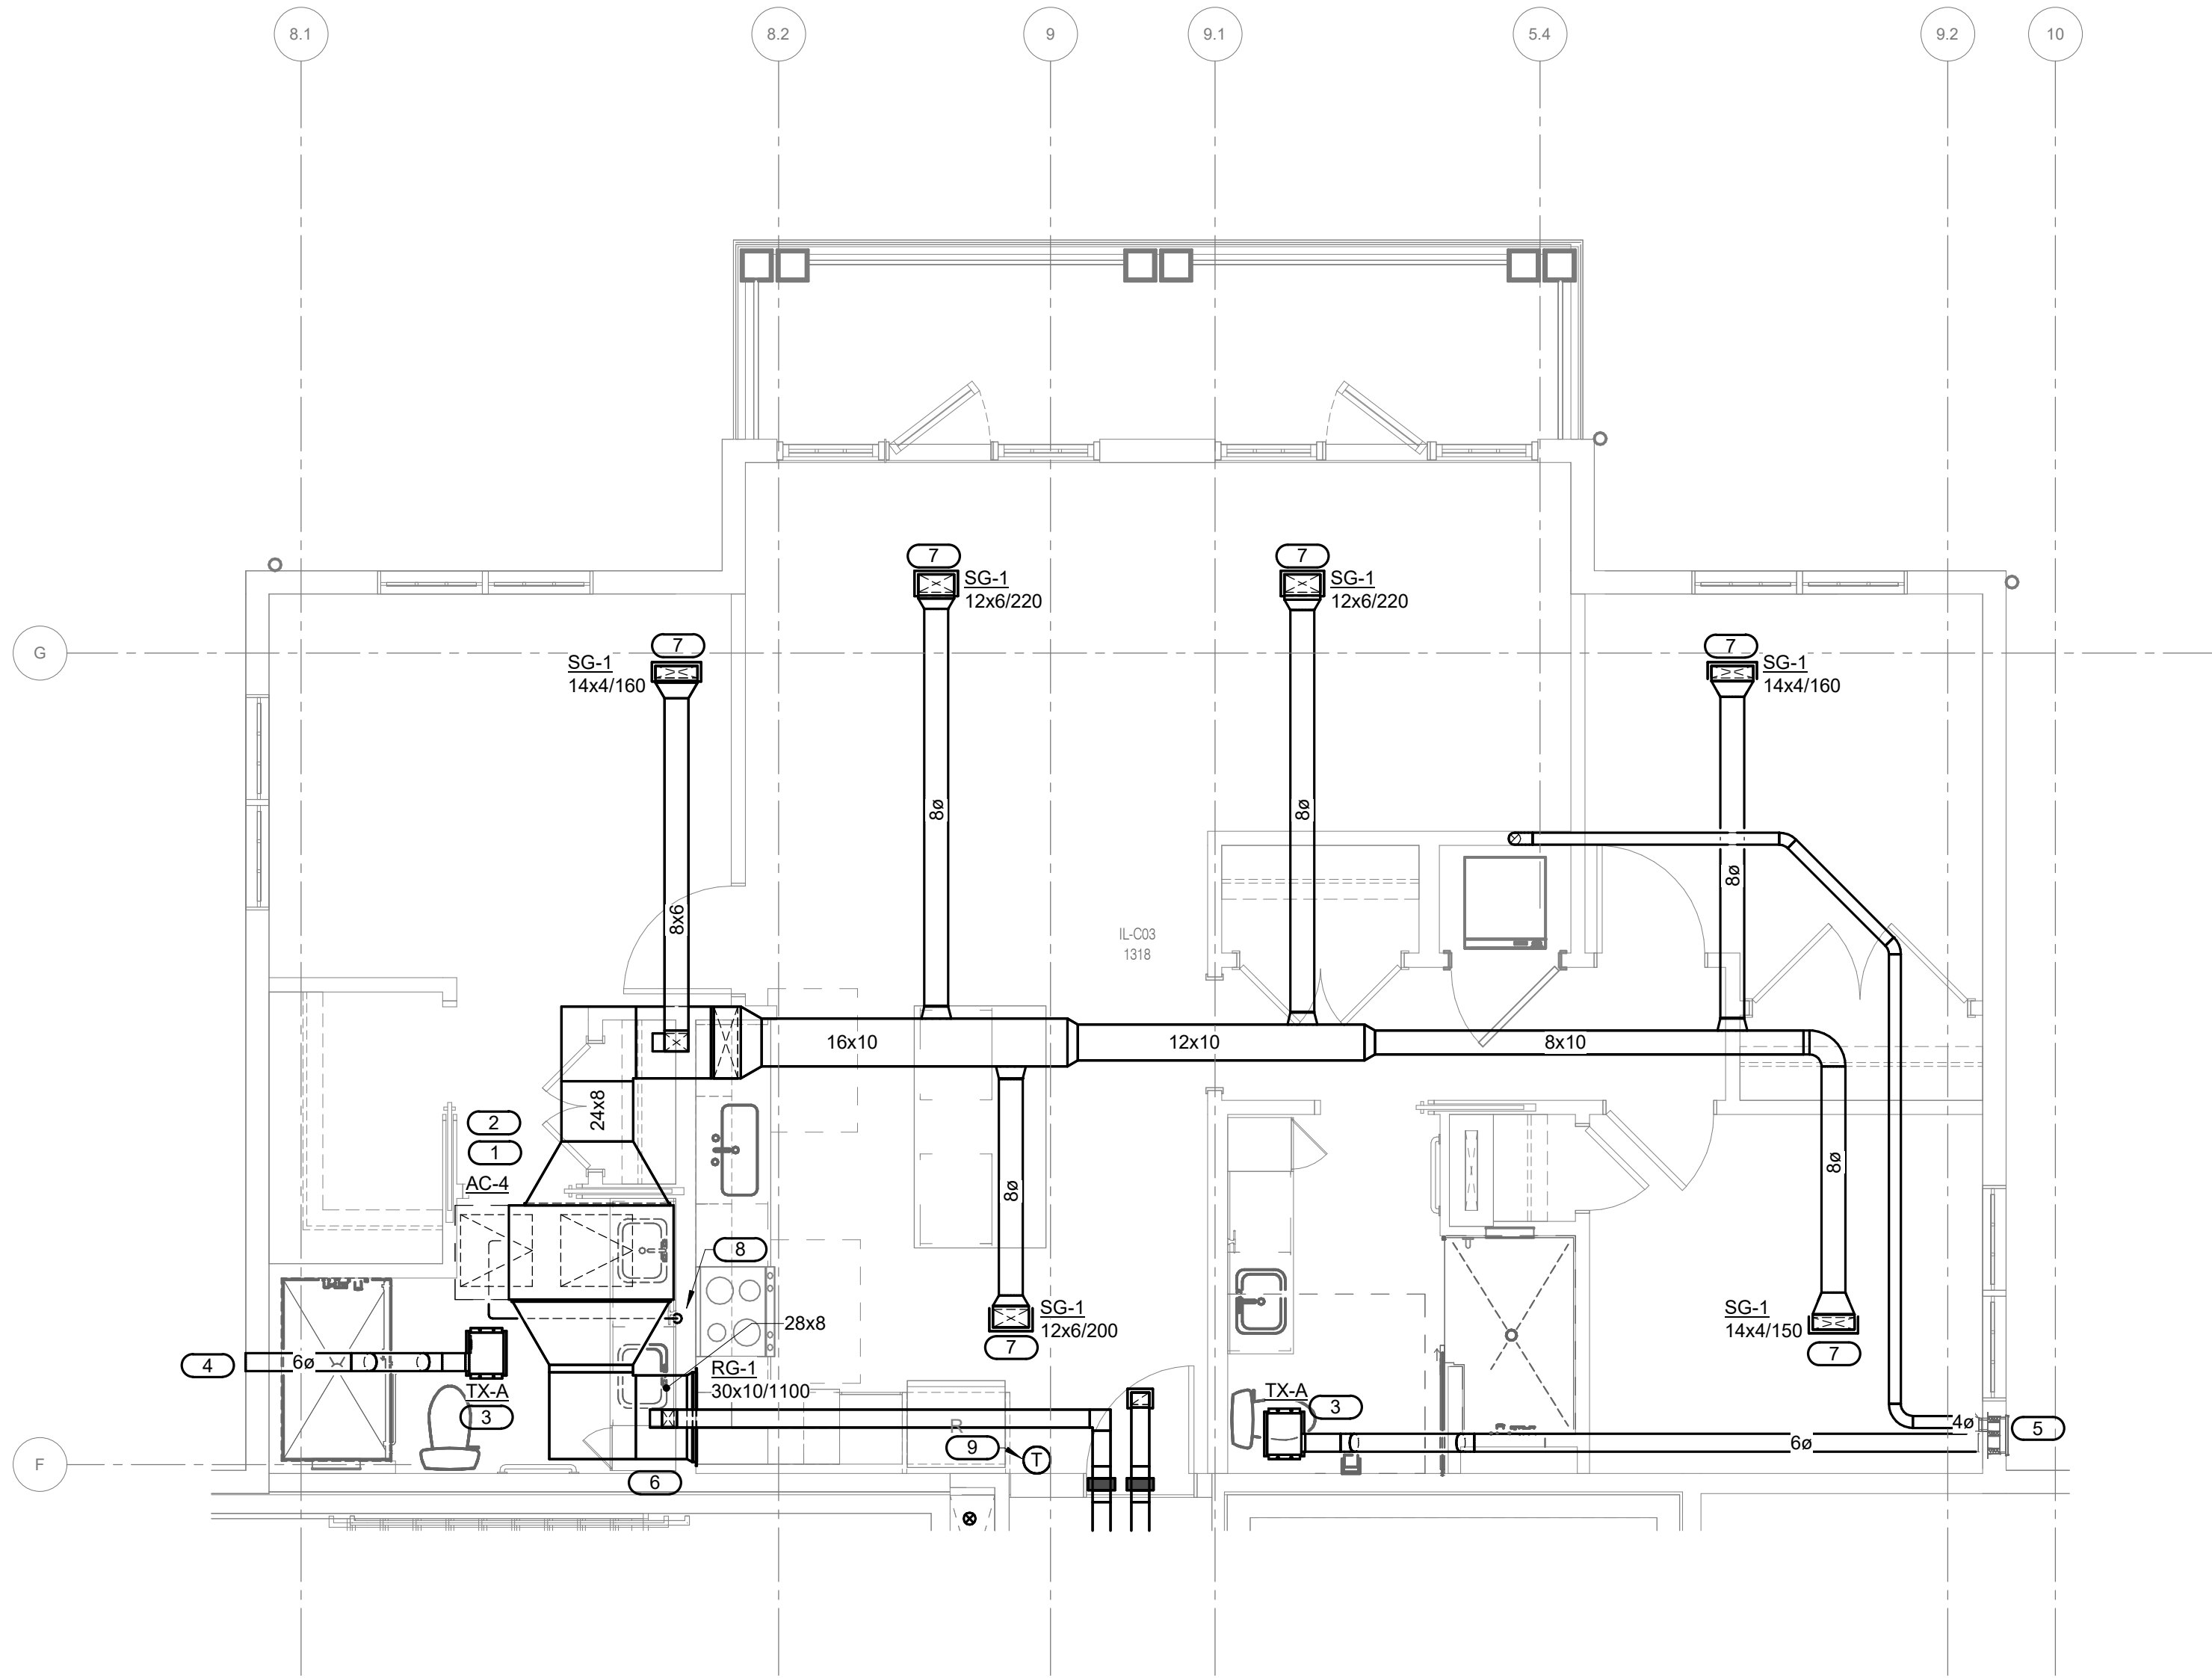

2 MECH. UNIT C03 - 3 BED 2 BATH - PLAN - AC-4
1/4" = 1'-0"

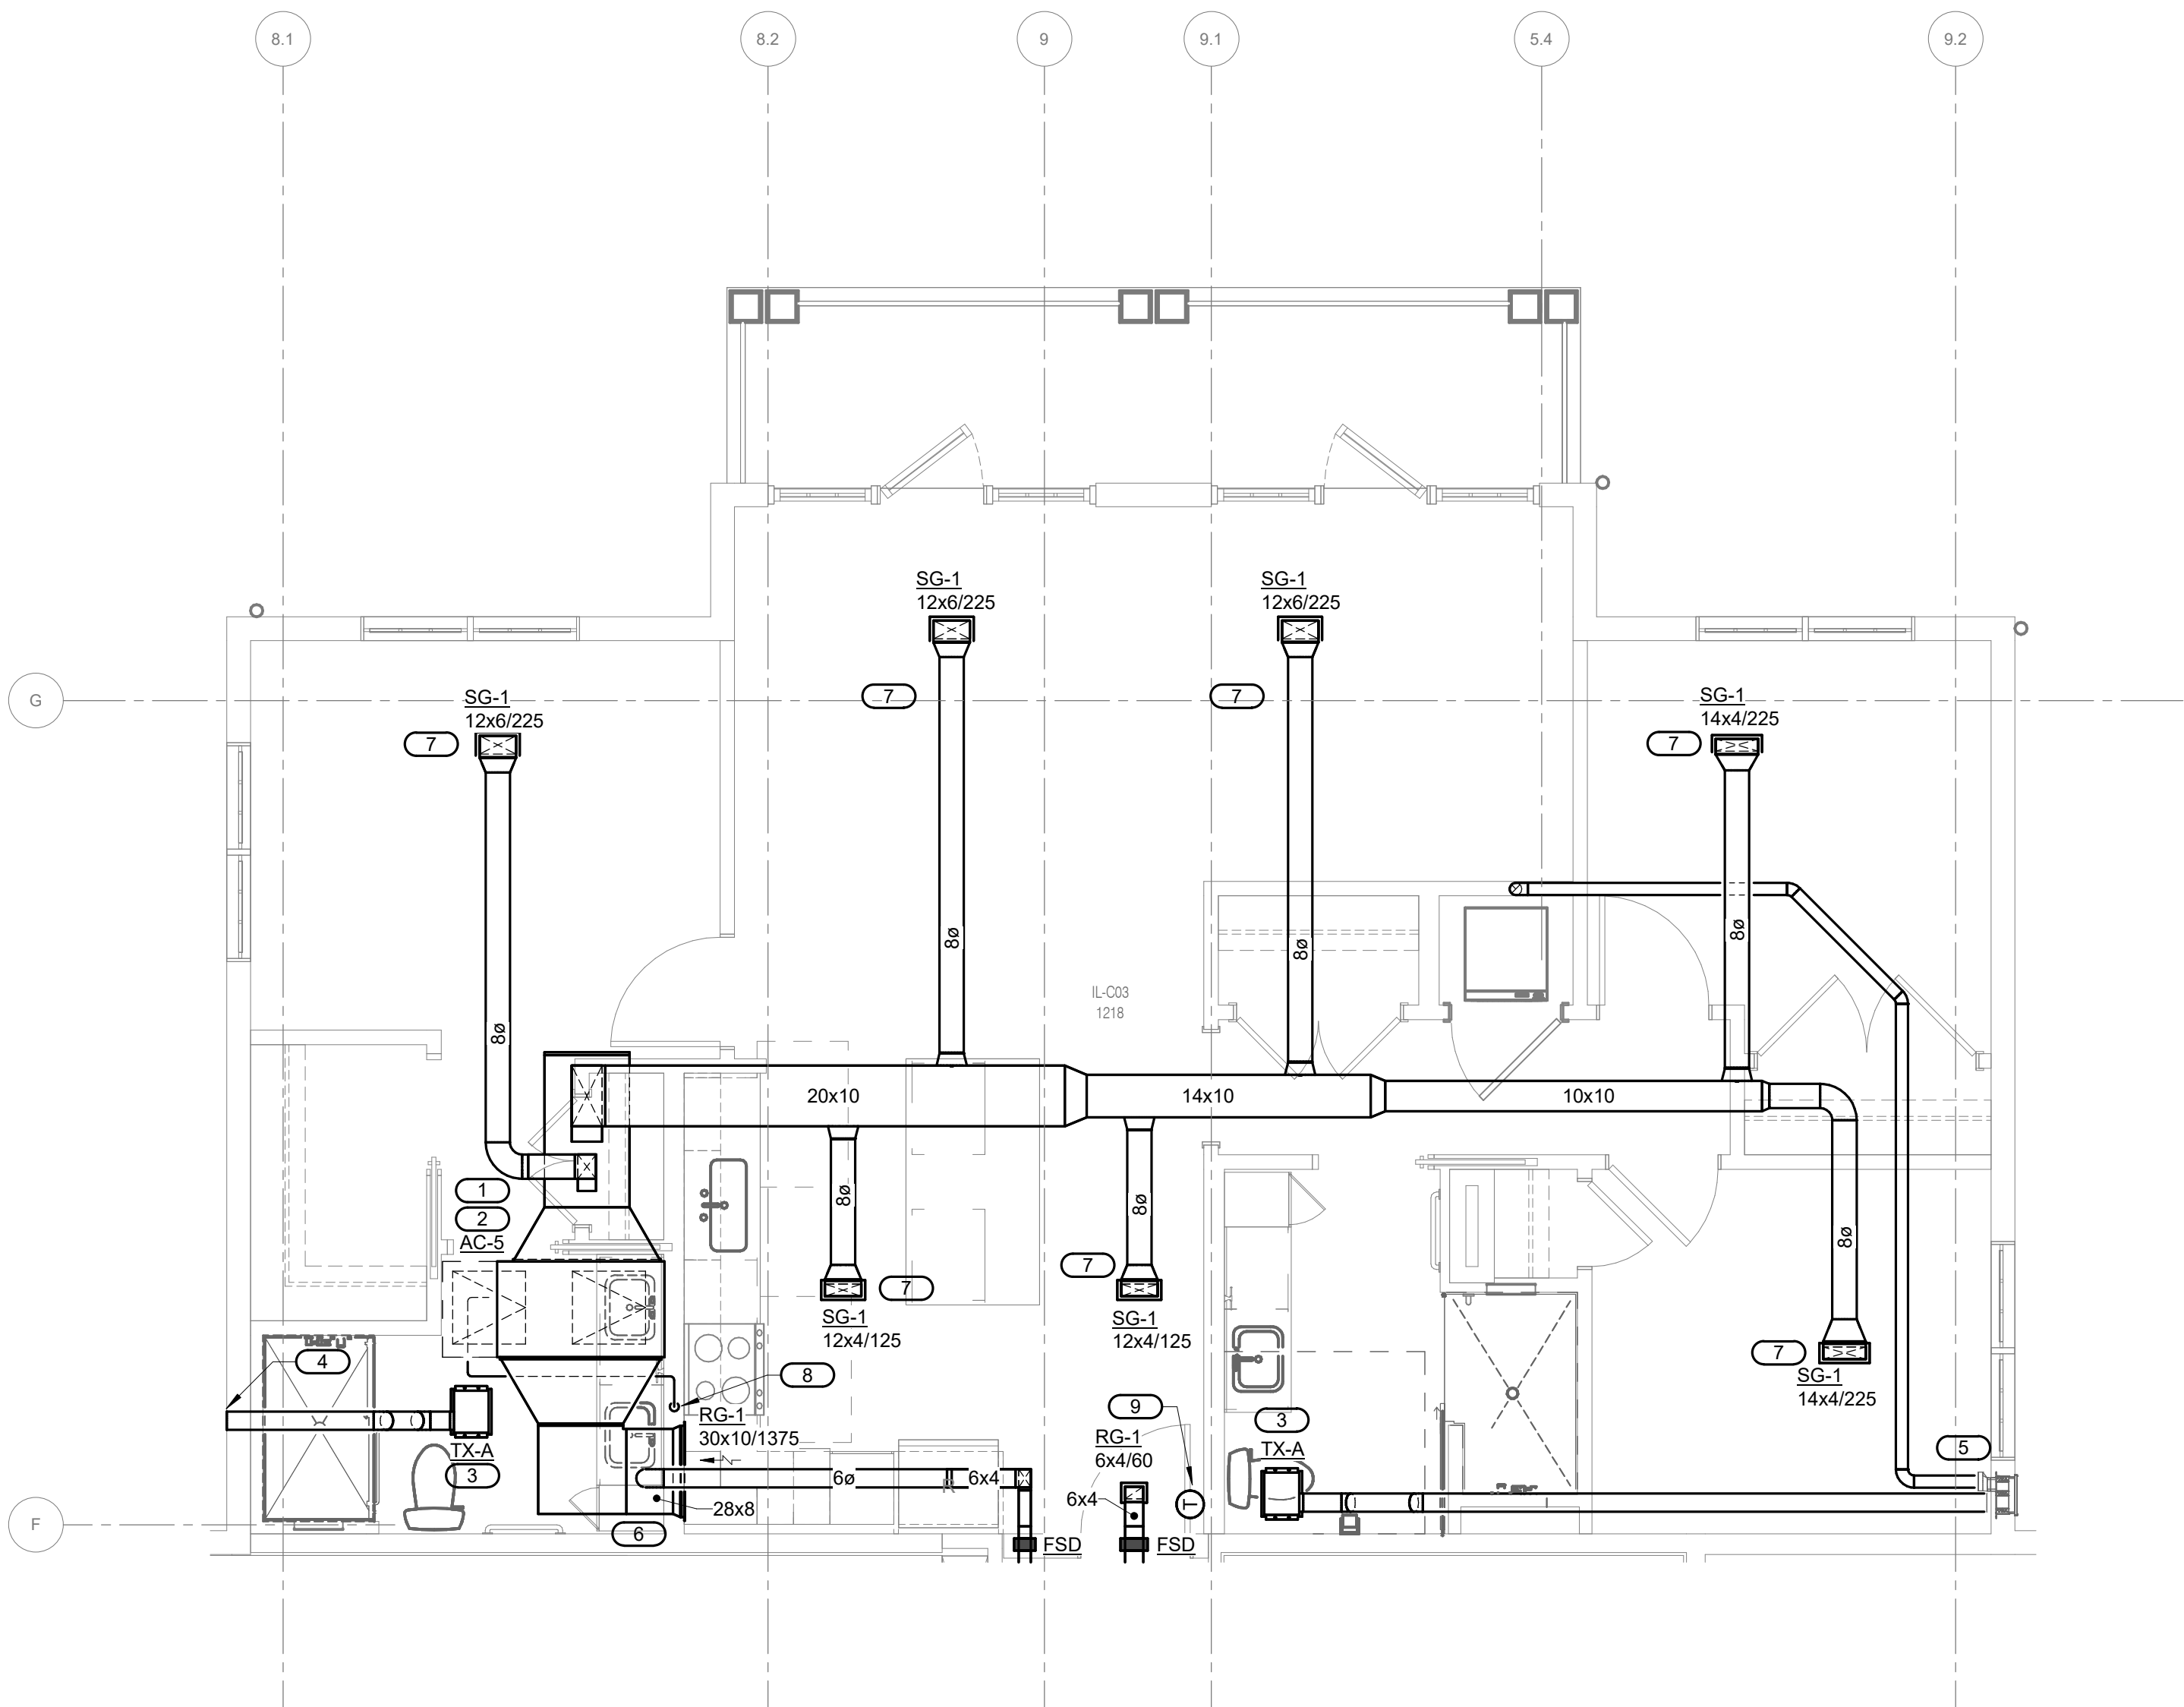

3 MECH. UNIT C03 - 3 BED 2 BATH - PLAN - AC-5
1/4" = 1'-0"

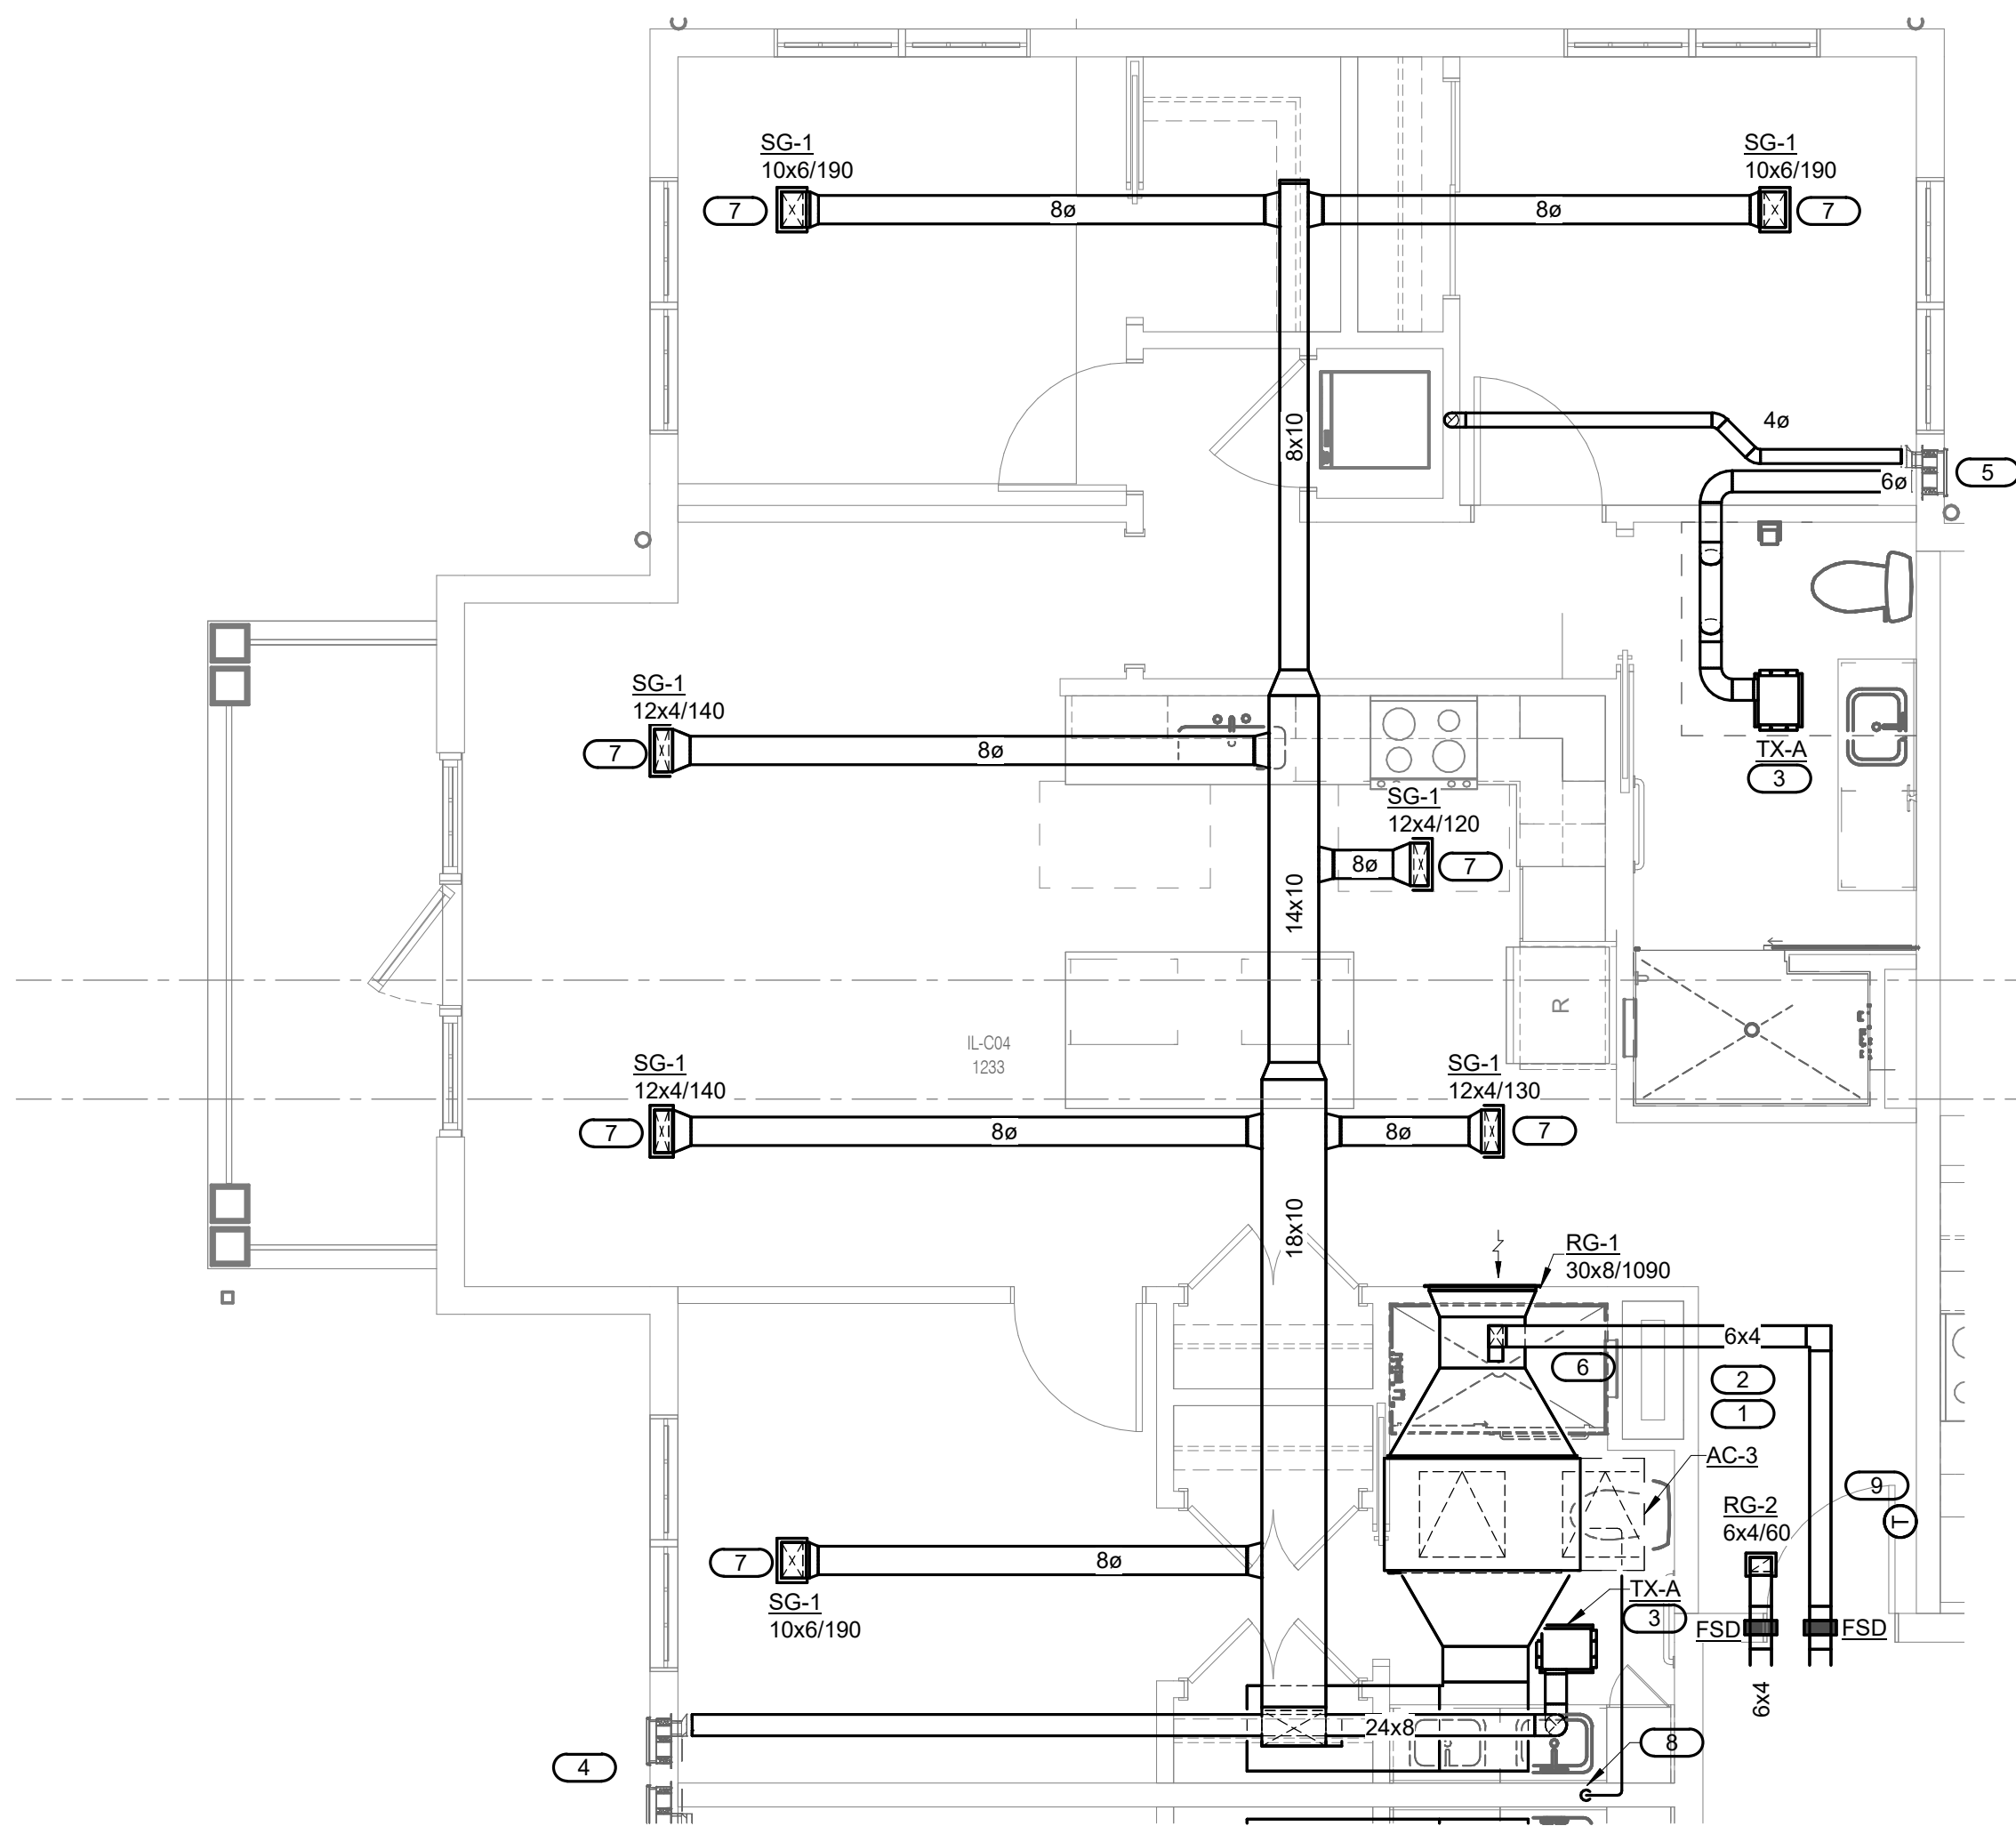

4 MECH. UNIT C04 - 3 BED 2 BATH - PLAN - AC-3
1/4" = 1'-0"

- KEYNOTES:**
1. NEW FAN COIL UNIT MOUNTED ABOVE CEILING PER MANUFACTURER RECOMMENDATIONS. PROVIDE ACCESS PANEL AS REQUIRED FOR UNIT MAINTENANCE.
 2. ROUTE REFRIGERANT LINES FROM FAN COIL UNIT TO ASSOCIATED CONDENSING UNIT ON ROOF AS REQUIRED. SIZE REFRIGERANT LINES PER MANUFACTURER RECOMMENDATIONS. DO NOT EXCEED MAXIMUM EQUIVALENT REFRIGERANT LENGTHS.
 3. NEW EXHAUST FAN INSTALLED IN BATHROOM CEILING PER MANUFACTURER RECOMMENDATIONS.
 4. ROUTE EXHAUST DUCTWORK TO EXTERIOR WALL AS REQUIRED. PROVIDE VENT MODEL: "VEB-66-F" FOR BOTH DUCTWORK LINES AT TERMINATION POINT. MAINTAIN MINIMUM 3'-0" FROM WINDOW OPENINGS AND 10'-0" FROM ANY OUTDOOR AIR INTAKES.
 5. ROUTE EXHAUST DUCTWORK TO EXTERIOR WALL AS REQUIRED. PROVIDE VENT MODEL: "VEB-66-F" FOR BOTH DUCTWORK LINES AT TERMINATION POINT. MAINTAIN MINIMUM 3'-0" FROM WINDOW OPENINGS AND 10'-0" FROM ANY OUTDOOR AIR INTAKES.
 6. PROVIDE 30" LONG RETURN AIR PLENUM. MATCH SIZE OF UNIT RETURN AIR OPENING. PROVIDE SOUTH-WARK MODEL: 99FULD, UL APPROVED. RADIATION DAMPER BOOT ABOVE GRILLE.
 7. PROVIDE A 1-1/4" DRAIN PIPE CONNECTION FROM THE INDOOR UNIT TO THE LAVATORY SANITARY LINE. REFER TO DETAIL 1M5002 FOR THE CONNECTION REQUIREMENTS.
 8. MOUNT THE THERMOSTAT ON THE WALL AT 48" ABOVE FINISHED FLOOR (A.F.F.).

HKS

ARCHITECT
HKS ARCHITECTS, P.C.
30 WEST 26th STREET, 12th FLOOR
NEW YORK, NY 10010

STRUCTURAL
IMEG
1411 BROADWAY, SUITE 600
NEW YORK, NY 10018

MEP ENGINEER
IMEG
177 CROSSWAYS PARK DRIVE
WOODBURY, NY 11797

LV ENGINEER
TATEROY
765 HICKORY FLAT HWY, SUITE 200
WOODSTOCK, GA 30188

LANDSCAPE ARCHITECT
MPFP
120 BROADWAY, 20TH FLOOR
NEW YORK, NY 10271

POOL DESIGNER
COUNSILMANHUNSAKER & ASSOCIATES, INC.
12851 MANCHESTER ROAD, SUITE 120
ST. LOUIS, MO 63131


FOOD SERVICE & LAUNDRY
CLARK
2551 HORSEHOE RD.
LANCASTER, PA 17601

SUNRISE SENIOR LIVING
RYE BROOK


DOB BSCAN | DOB STAMP & SIGNATURES

SEAL & SIGNATURE

CON NO.: 111AAA
KEY PLAN

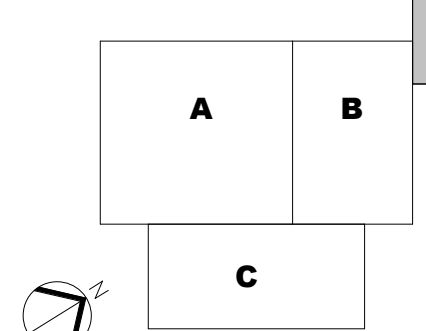

REVISION	NO.	DESCRIPTION	DATE
1	DD Program Print		08/26/25
2	DESIGN DEVELOPMENT		11/02/25
3	EXTERIOR BUILDING PERMIT		12/03/25
4	100% DESIGN DEVELOPMENT		01/02/26
5	ISSUED FOR PERMIT		06/26/26

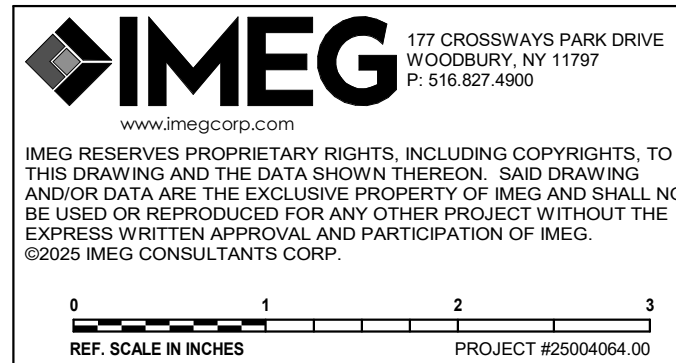


HKS PROJECT NUMBER
25004064.00
DATE
07/15/26
ISSUE
ISSUED FOR GMP

SHEET TITLE
UNIT PLANS IL - MECHANICAL


SHEET NO.
M2105

DOB FILE # DOB PAGE #


TITLE BLOCK VERSION: 2019030
MODEL: Autodesk Docs/27292.000 - Sunrise E.L.A.M.C. 2024MEP25 20240404.00 - LAL Building, C-4
PRINT DATE: 11/02/2025 12:45:24 PM - TEMPLATE VERSION: 23.0.1

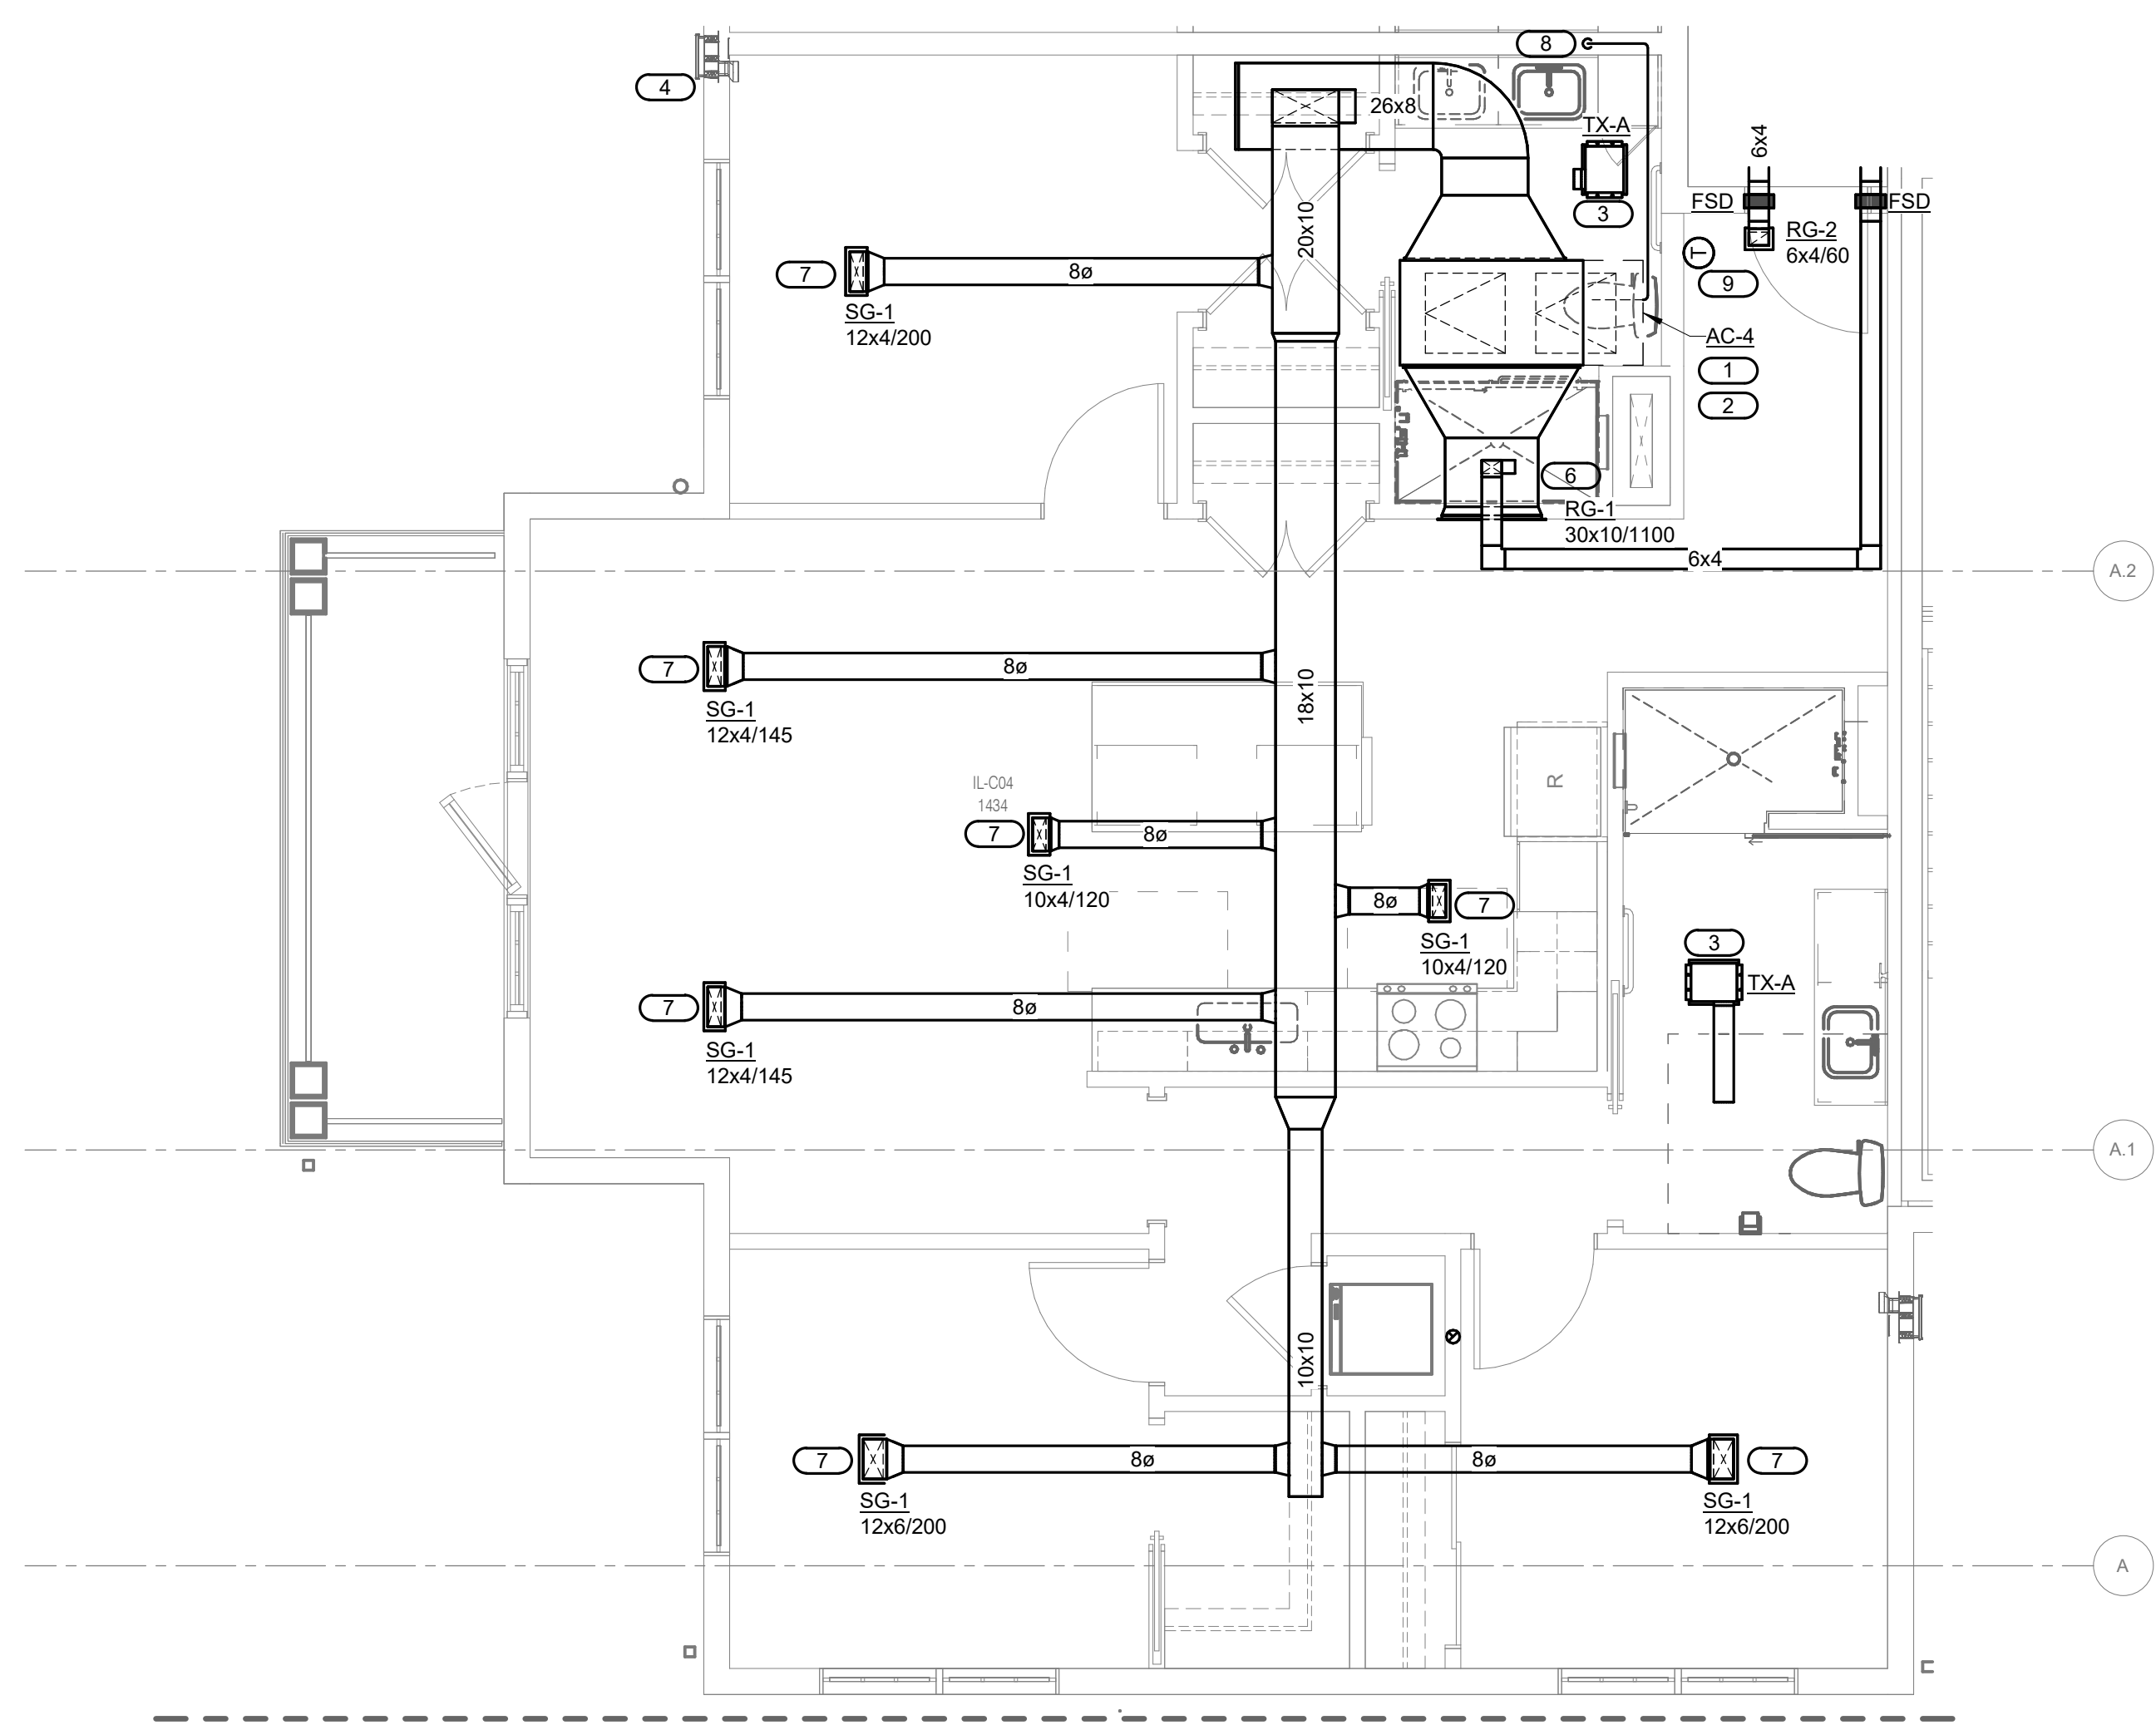

1 MECH. UNIT C04 - 3 BED 2 BATH - PLAN - AC-4
1/4" = 1'-0"

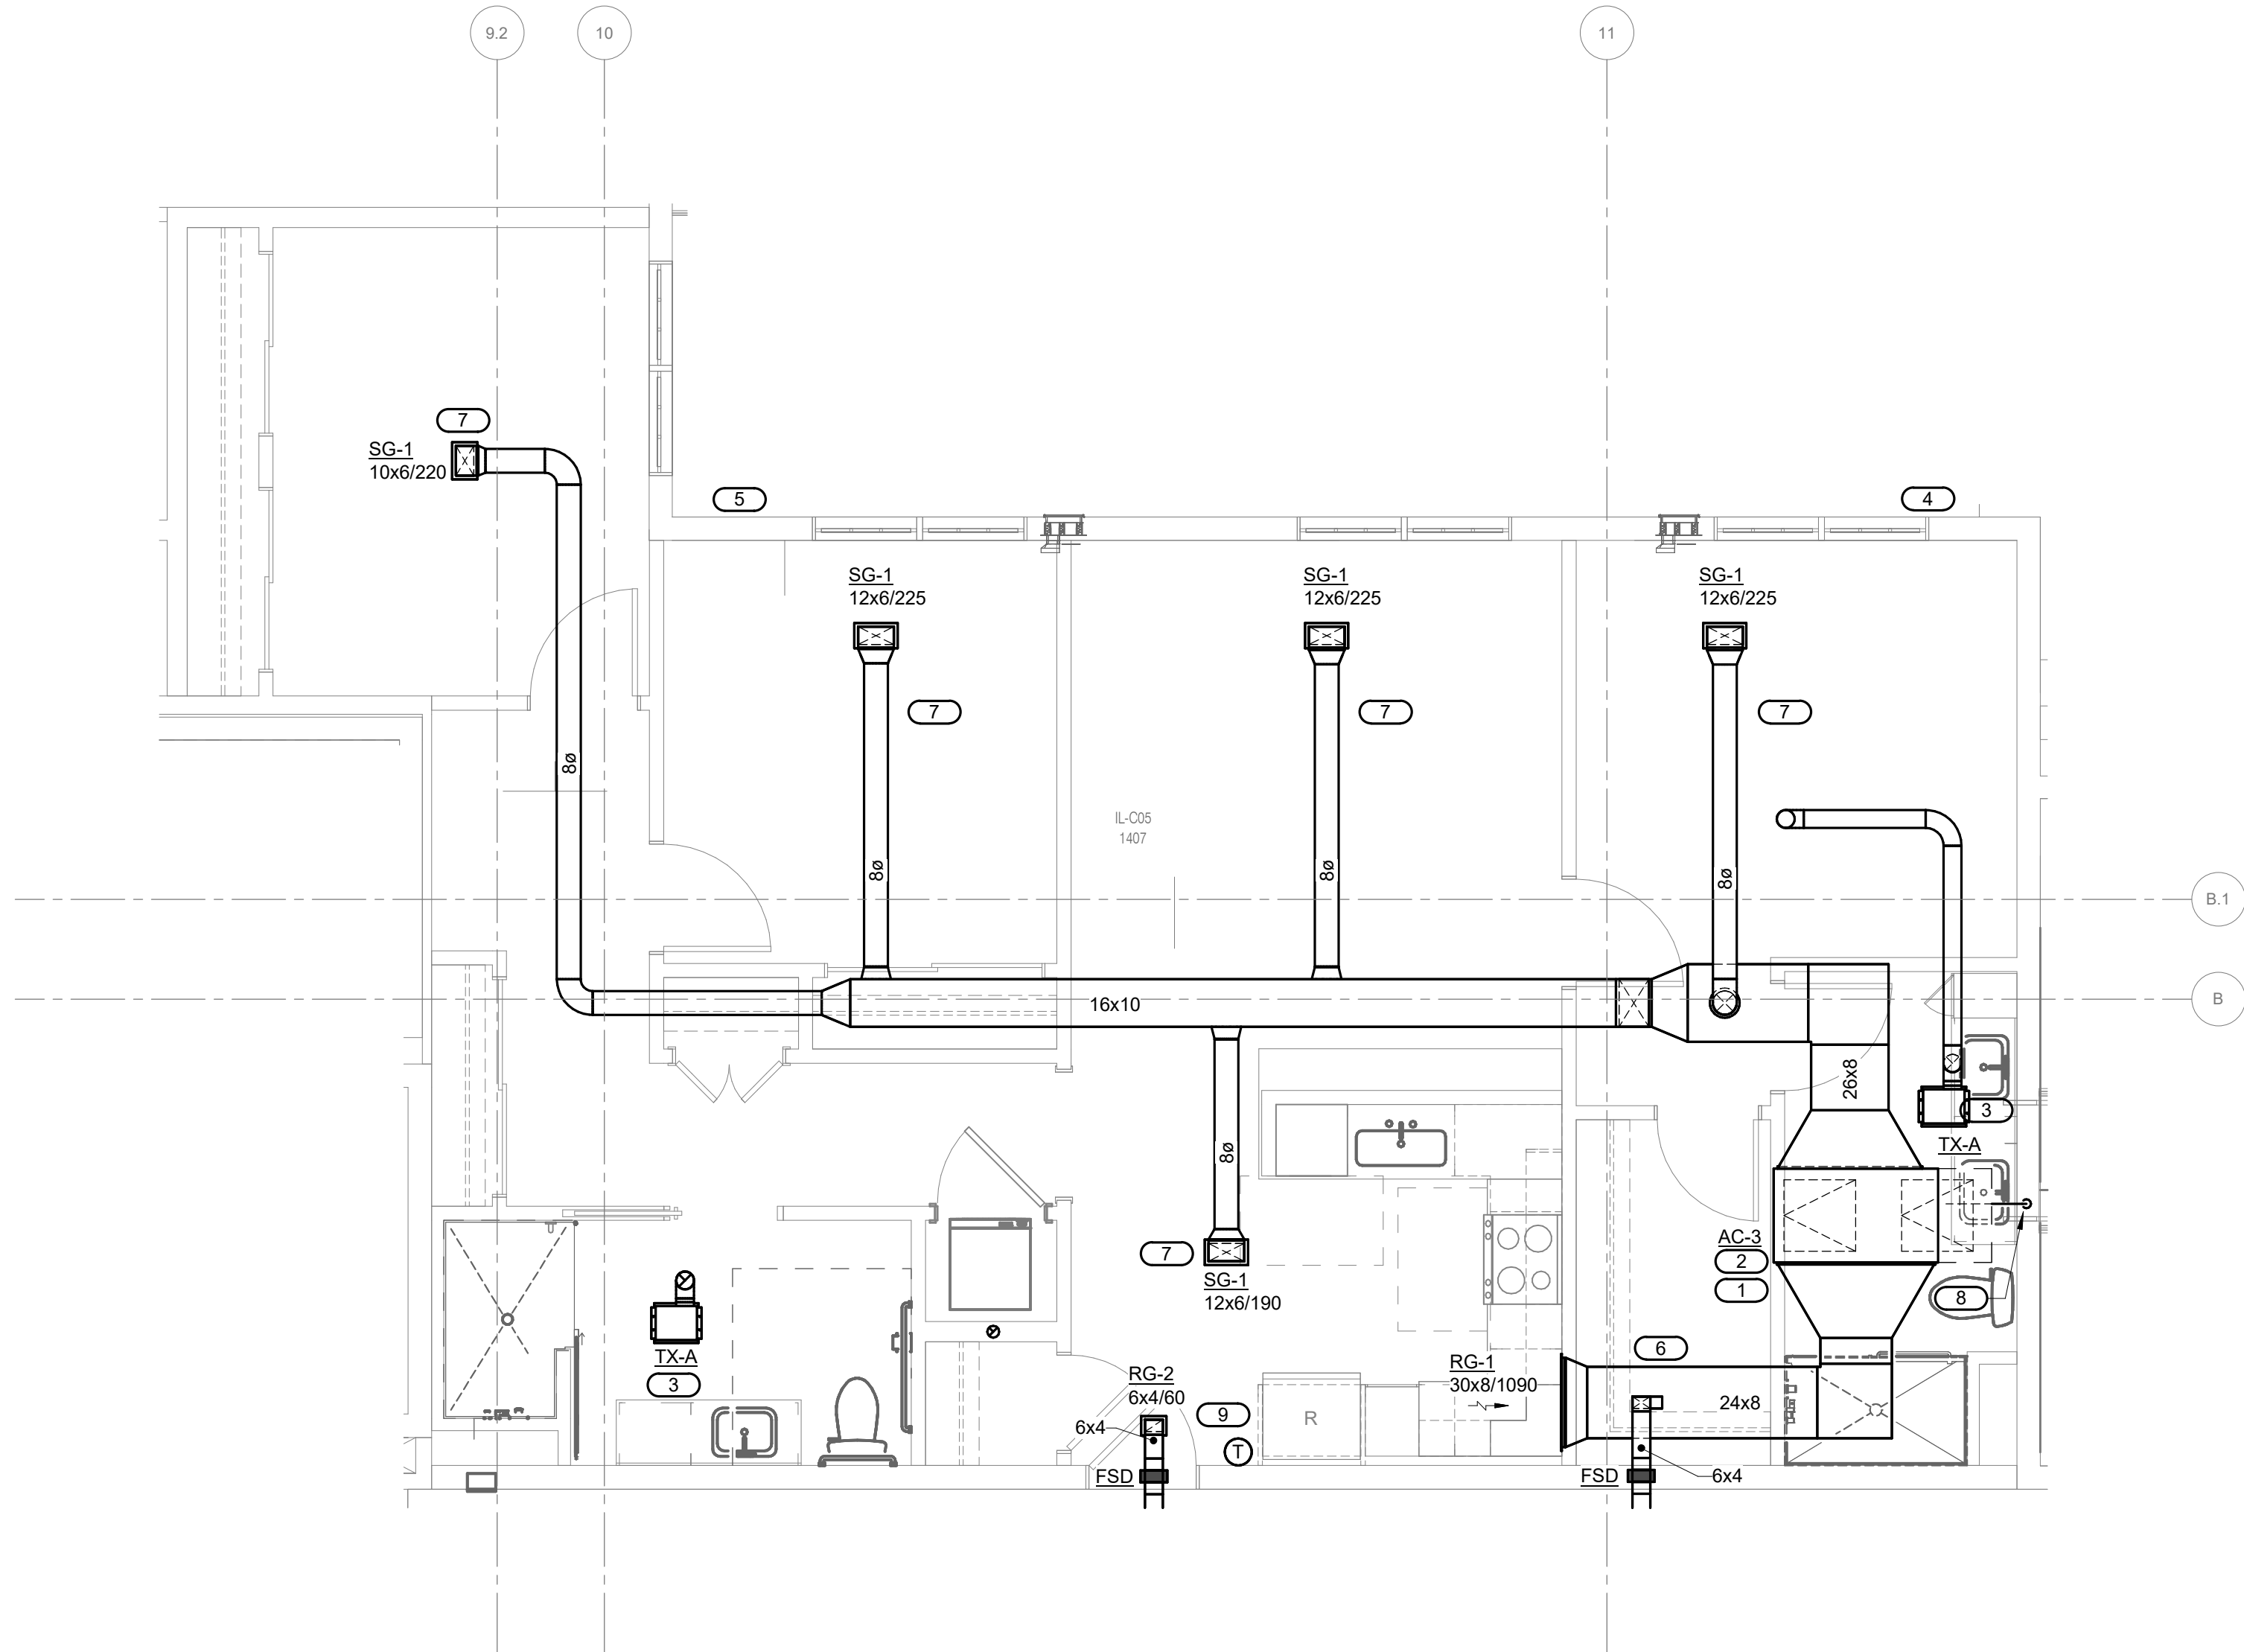

2 MECH. UNIT C05 - 3 BED 2 BATH - PLAN
1/4" = 1'-0"

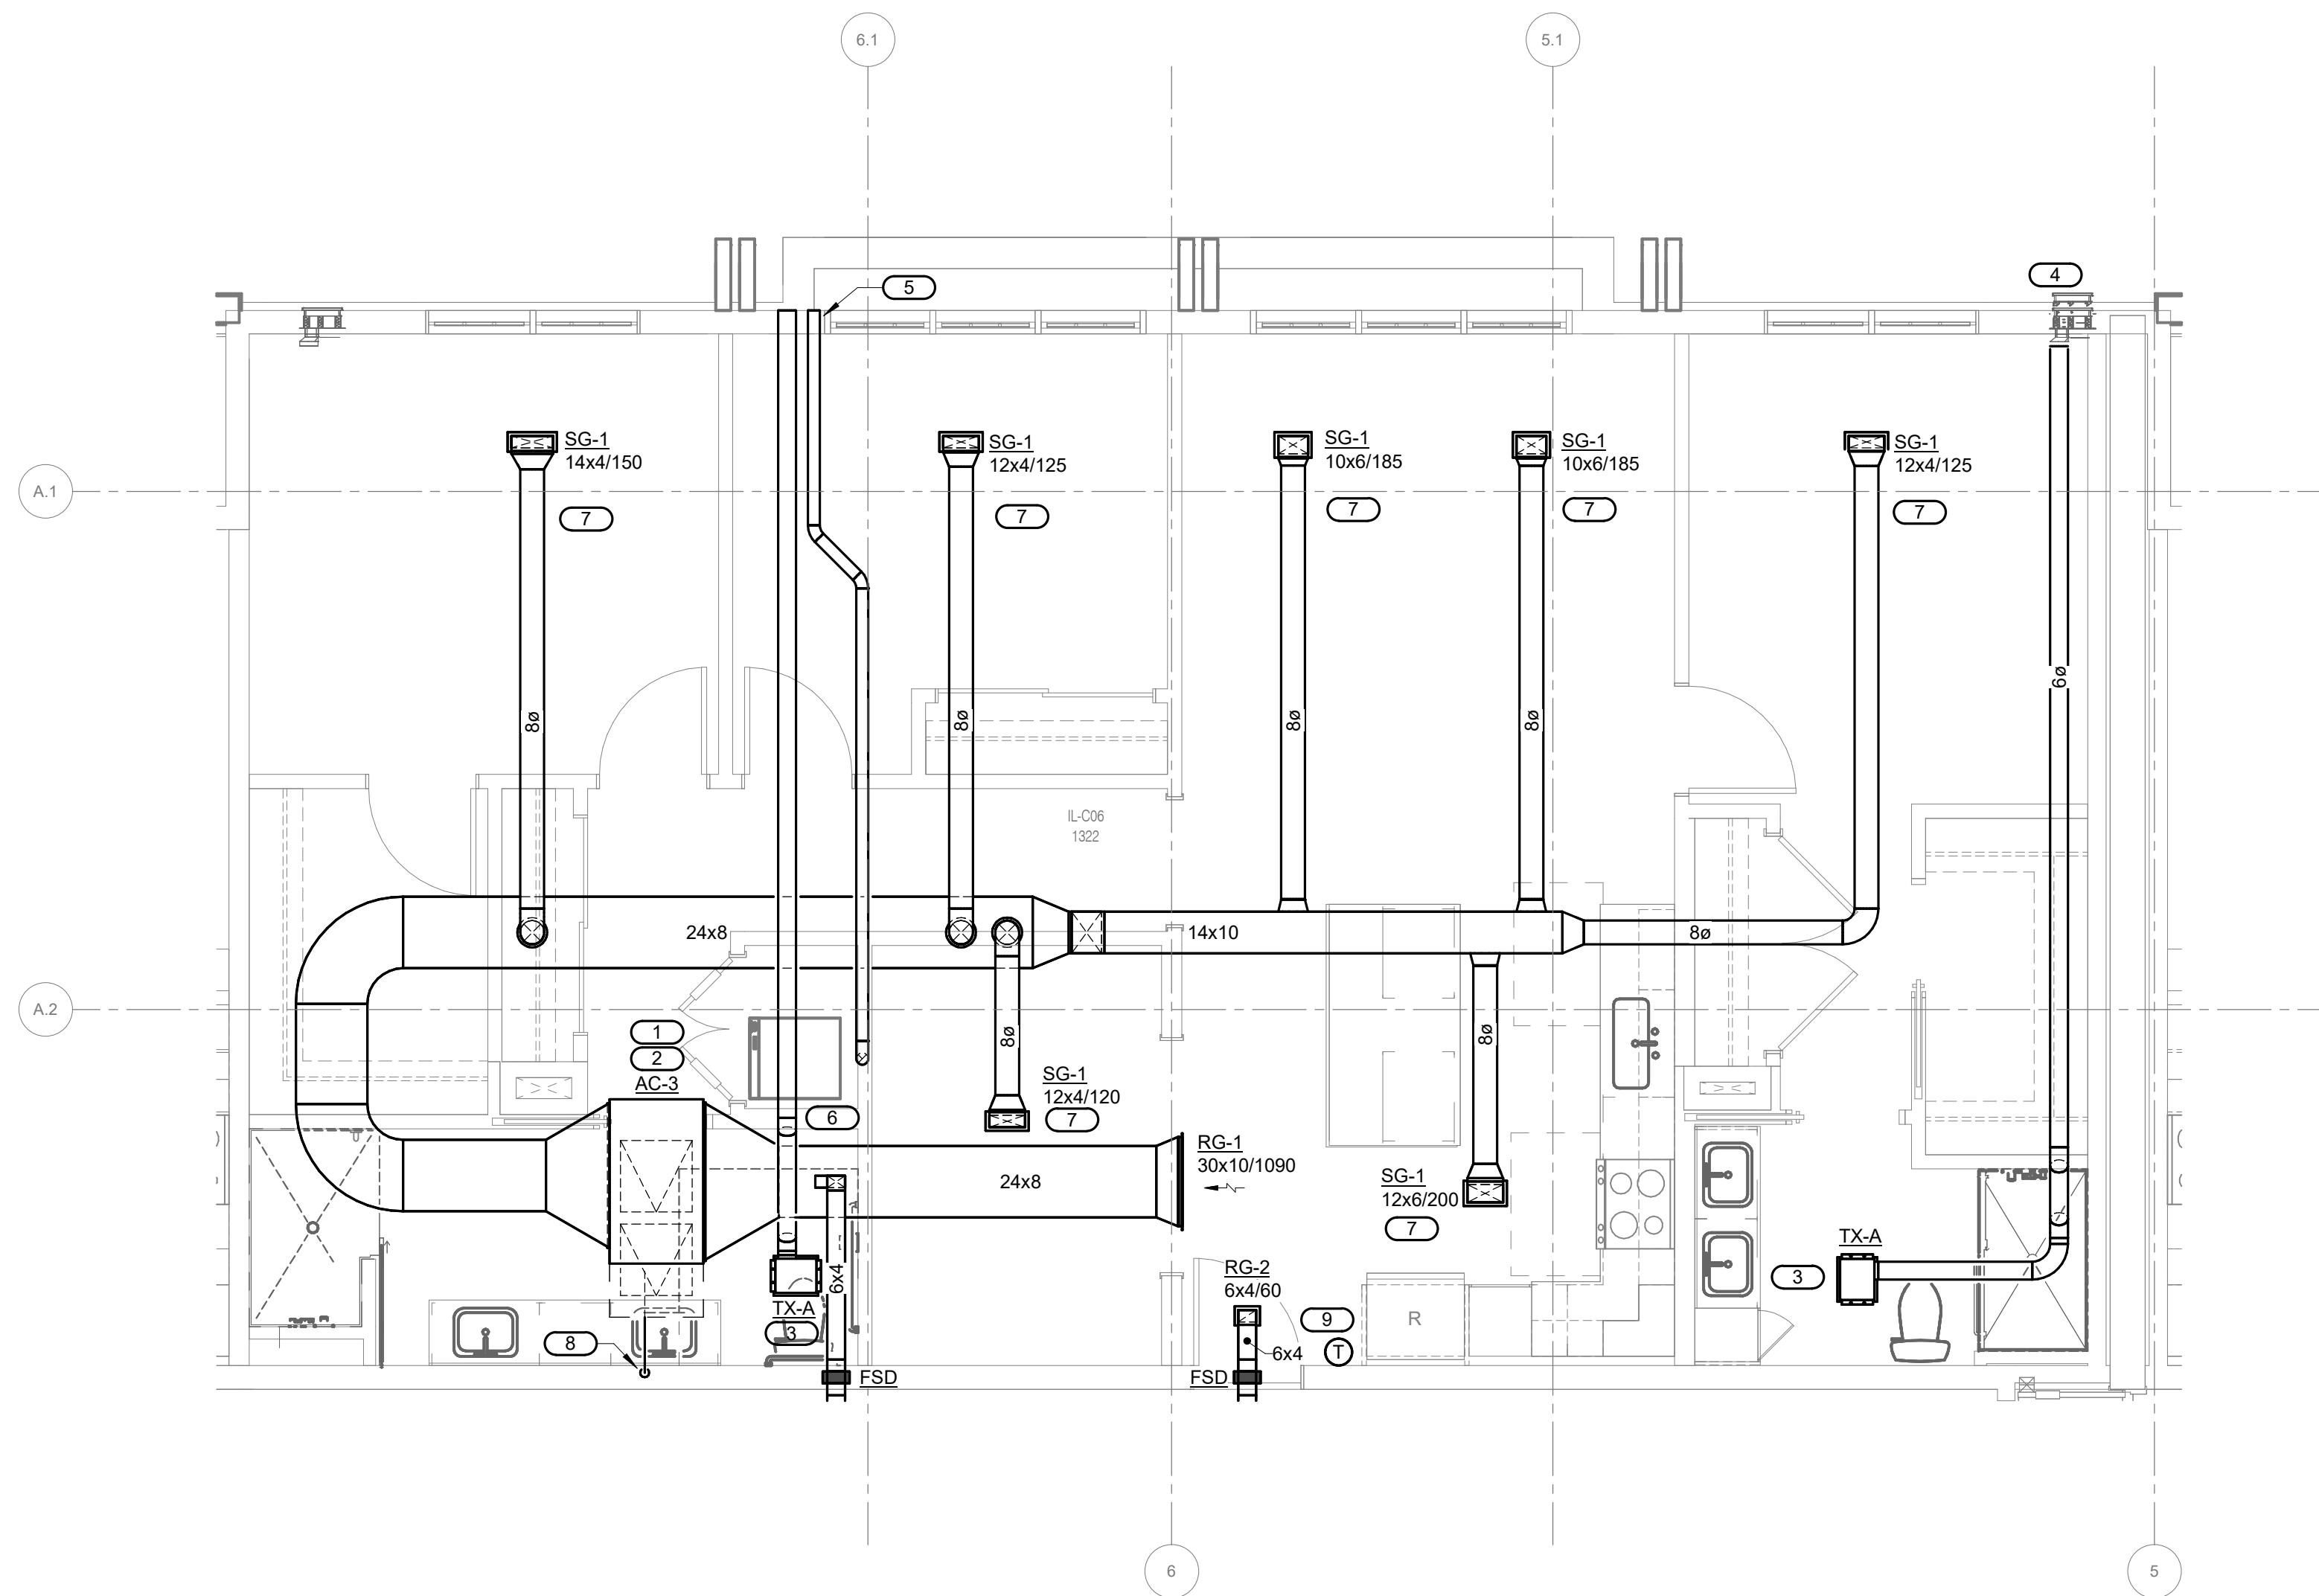

3 MECH. UNIT C06 - 3 BED 2 BATH + DEN - PLAN
1/4" = 1'-0"

- KEYNOTES:**
1. NEW FAN COIL UNIT MOUNTED ABOVE CEILING PER MANUFACTURER RECOMMENDATIONS. PROVIDE ACCESS PANEL AS REQUIRED FOR UNIT MAINTENANCE.
 2. ROUTE REFRIGERANT LINES FROM FAN COIL UNIT TO ASSOCIATED CONDENSING UNIT ON ROOF AS REQUIRED. SIZE REFRIGERANT LINES PER MANUFACTURER RECOMMENDATIONS. DO NOT EXCEED MAXIMUM EQUIVALENT REFRIGERANT LENGTHS.
 3. NEW EXHAUST FAN INSTALLED IN BATHROOM RECOMMENDATIONS.
 4. ROUTE EXHAUST DUCTWORK TO EXTERIOR WALL AS REQUIRED. PROVIDE X-VENT MODEL "XSEB-P" AT DUCTWORK TERMINATION POINT. MAINTAIN MINIMUM 3'-0" FROM WINDOW OPENINGS AND 10'-0" FROM ANY OUTDOOR AIR INTAKES.
 5. ROUTE EXHAUST DUCTWORK TO EXTERIOR WALL AS REQUIRED. PROVIDE X-VENT MODEL "XVEB-46-P" FOR BOTH DUCTWORK LINES AT TERMINATION POINT. MAINTAIN MINIMUM 3'-0" FROM WINDOW OPENINGS AND 10'-0" FROM ANY OUTDOOR AIR INTAKES. EXHAUST OUTLET AS REQUIRED.
 6. PROVIDE 30" LONG RETURN AIR PLENUM MATCH SIZE OF UNIT RETURN AIR OPENING.
 7. PROVIDE SOUTHWARM MODEL: SIFULD, UL APPROVED, RADIATION DAMPER BOOT ABOVE GRILLE.
 8. PROVIDE A 1-1/4" DRAIN PIPE CONNECTION FROM THE INDOOR UNIT TO THE LAVATORY SANITARY LINE. REFER TO DETAIL 11MS602 FOR THE CONNECTION REQUIREMENTS.
 9. MOUNT THE THERMOSTAT ON THE WALL AT 48" ABOVE FINISHED FLOOR (A.F.F.).

HKS

ARCHITECT
HKS ARCHITECTS P.C.
30 WEST 26th STREET, 12th FLOOR
NEW YORK, NY 10010

STRUCTURAL
IMEG
1411 BROADWAY, SUITE 600
NEW YORK, NY 10018

MEP ENGINEER
IMEG
177 CROSSWAYS PARK DRIVE
WOODBURY, NY 11797

LV ENGINEER
TATEROY
765 HICKORY FLAT HWY, SUITE 200
WOODSTOCK, GA 30188

LANDSCAPE ARCHITECT
MPFP
120 BROADWAY, 20TH FLOOR
NEW YORK, NY 10271

POOL DESIGNER
COUNSLMANHUNSAKER & ASSOCIATES, INC.
12851 MANCHESTER ROAD, SUITE 120
ST. LOUIS, MO 63131

FOOD SERVICE & LAUNDRY
CLARK
2551 HORSESHOE RD.
LANCASTER, PA 17601


SUNRISESM
SENIOR LIVING
RYE BROOK

DOB BSCAN | DOB STAMP & SIGNATURES

SEAL & SIGNATURE

CON NO.: 111AAA

KEY PLAN

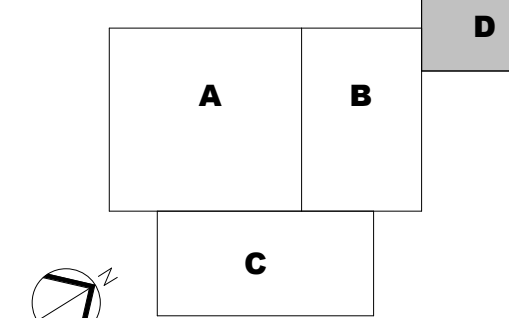

REVISION		
NO.	DESCRIPTION	D.
1	DD Progress Print	08/26/25
2	DESIGN DEVELOPMENT	11/03/25
3	EXTERIOR BUILDING PERMIT	12/03/25
4	100% DESIGN DEVELOPMENT	01/06/26
5	ISSUED FOR PERMIT	06/06/26

IMEG
177 CROSSWAYS PARK DRIVE
WOODBURY, NY 11797
P: 516.927.4900

IMEG RESERVES PROPRIETARY RIGHTS, INCLUDING COPYRIGHTS, TO THIS DRAWING AND THE DATA SHOWN HEREON. NO REPRODUCING AND/OR DATA ARE THE EXCLUSIVE PROPERTY OF IMEG AND SHALL NOT BE USED OR REPRODUCED FOR ANY OTHER PROJECT WITHOUT THE EXPRESS WRITTEN APPROVAL AND PARTICIPATION OF IMEG. ©2025 IMEG CONSULTANTS CORP.

REF. SCALE IN INCHES
PROJECT #20240404.00

HKS PROJECT NUMBER
25004064.00

DATE
07/15/26

ISSUE
ISSUED FOR GMP

SHEET TITLE
UNIT PLANS IL - MECHANICAL

SHEET NO.

M2106
DOB FILE # DOB PAGE #



1. NEW PTAC UNIT MOUNTED ON EXTERIOR WALL PER MANUFACTURER RECOMMENDATIONS. PROVIDE 1" CONDENSATE LINE THROUGH EXTERIOR WALL, DAYLIGHT CONDENSATE PIPE AND PROVIDE SPLASH GUARD. CONDENSATE LINE UNITS ARE STACKED VERTICALLY THE CONDENSATE LINES MAY BE COMBINED, PROVIDE 1" CONDENSATE LINE THROUGH EXTERIOR WALL.
2. NEW EXHAUST FAN INSTALLED IN BATHROOM CEILING PER MANUFACTURER RECOMMENDATIONS.
 - A. ROUTE EXHAUST DUCTWORK TO EXTERIOR WALL AS REQUIRED. PROVIDE X-VENT MODEL: "DVEB-86P" FOR BOTH DUCTWORK LINES AT EXTERIOR. PROVIDE 1" VENT MINIMUM 3'-0" FROM WINDOW OPENINGS AND 10'-0" FROM ANY OUTDOOR AIR INTAKE.
 - B. ROUTE EXHAUST DUCTWORK TO EXTERIOR WALL AS REQUIRED. PROVIDE X-VENT MODEL: "DVEB-86P" FOR BOTH DUCTWORK LINES AT EXTERIOR. PROVIDE 1" VENT MINIMUM 3'-0" FROM WINDOW OPENINGS AND 10'-0" FROM ANY OUTDOOR AIR INTAKES.
 - C. ROUTE EXHAUST DUCTWORK UP THROUGH ROOF AS REQUIRED.

SEAL & SIGNATURE _____





REVISION		
NO	DESCRIPTION	DATE
1	DD Progress Print	09/28/25
2	DESIGN DEVELOPMENT	11/25/25
3	EXTERIOR BUILDING PERMIT	12/23/25
4	100% DESIGN DEVELOPMENT	01/30/26
5	ISSUED FOR PERMIT	06/05/26

ISSUED FOR GMP


SHEET NO.

M2107

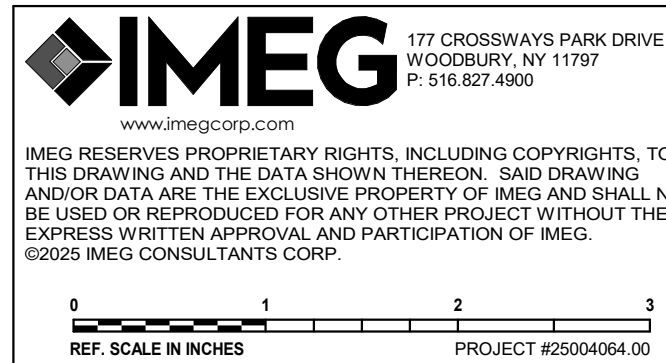


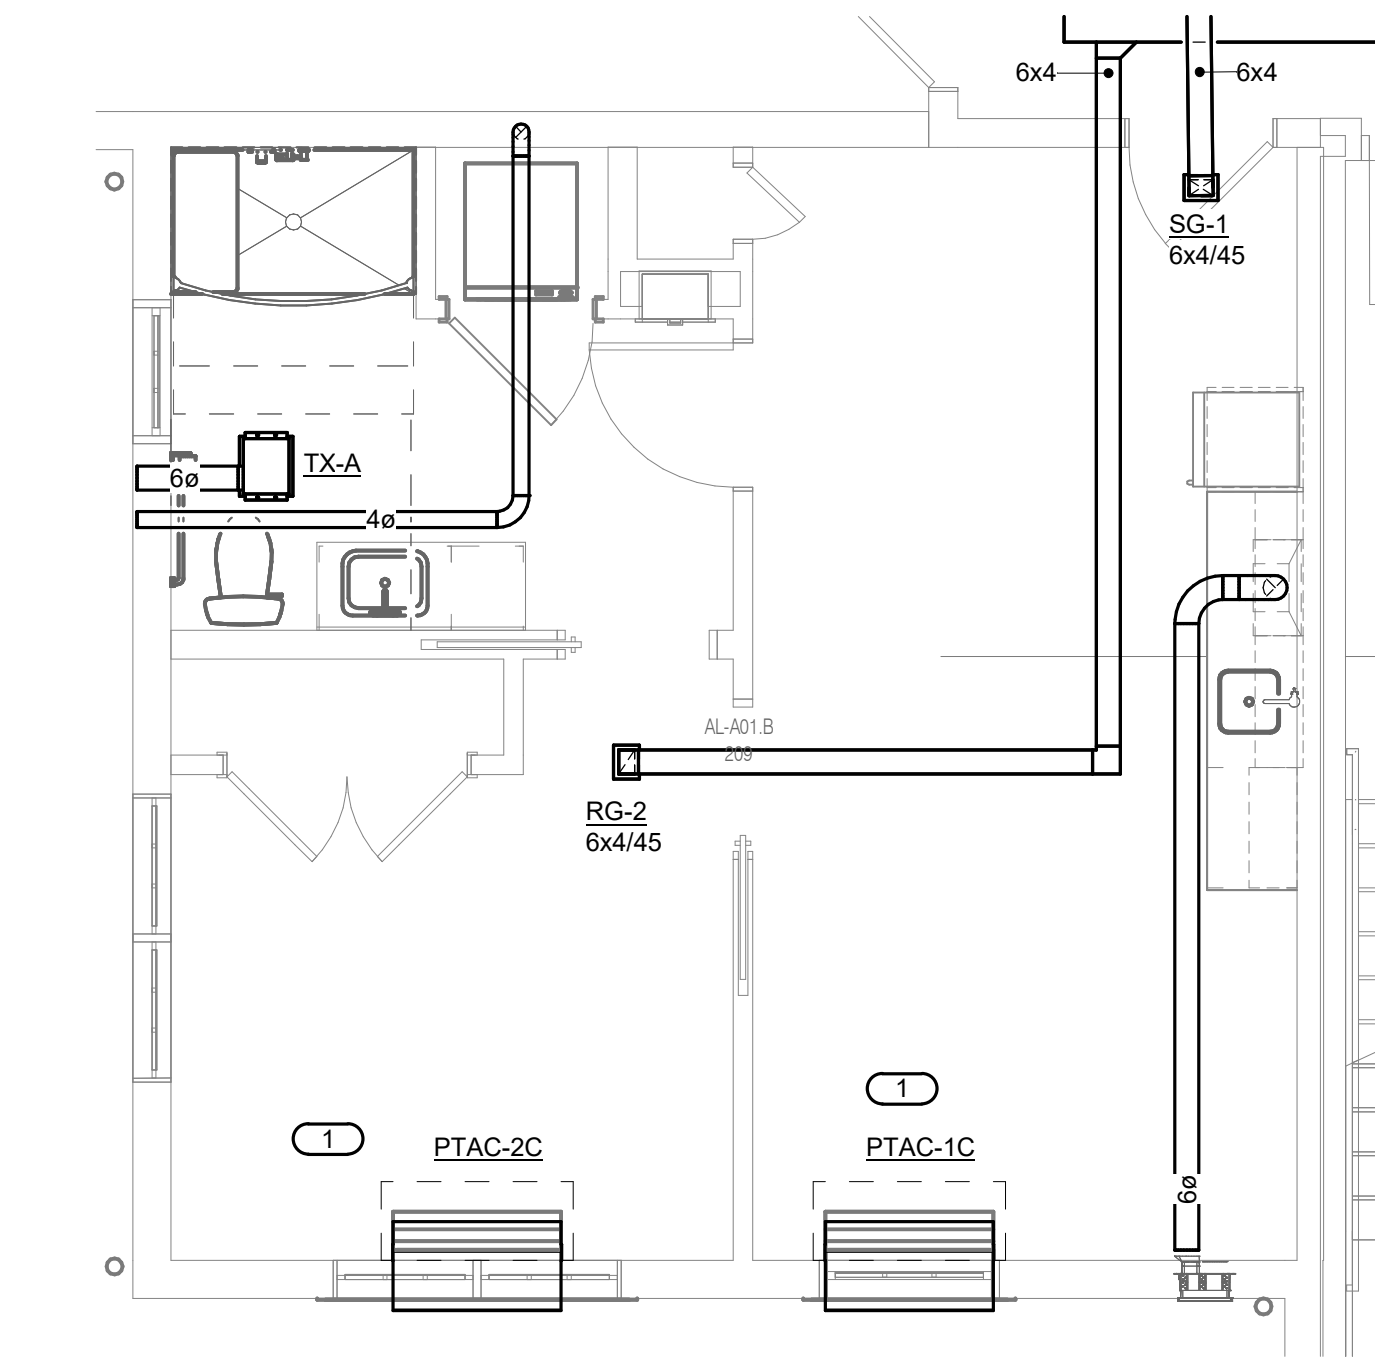


1 MECH. UNIT - AL-A01.C
1/4" = 1'-0"

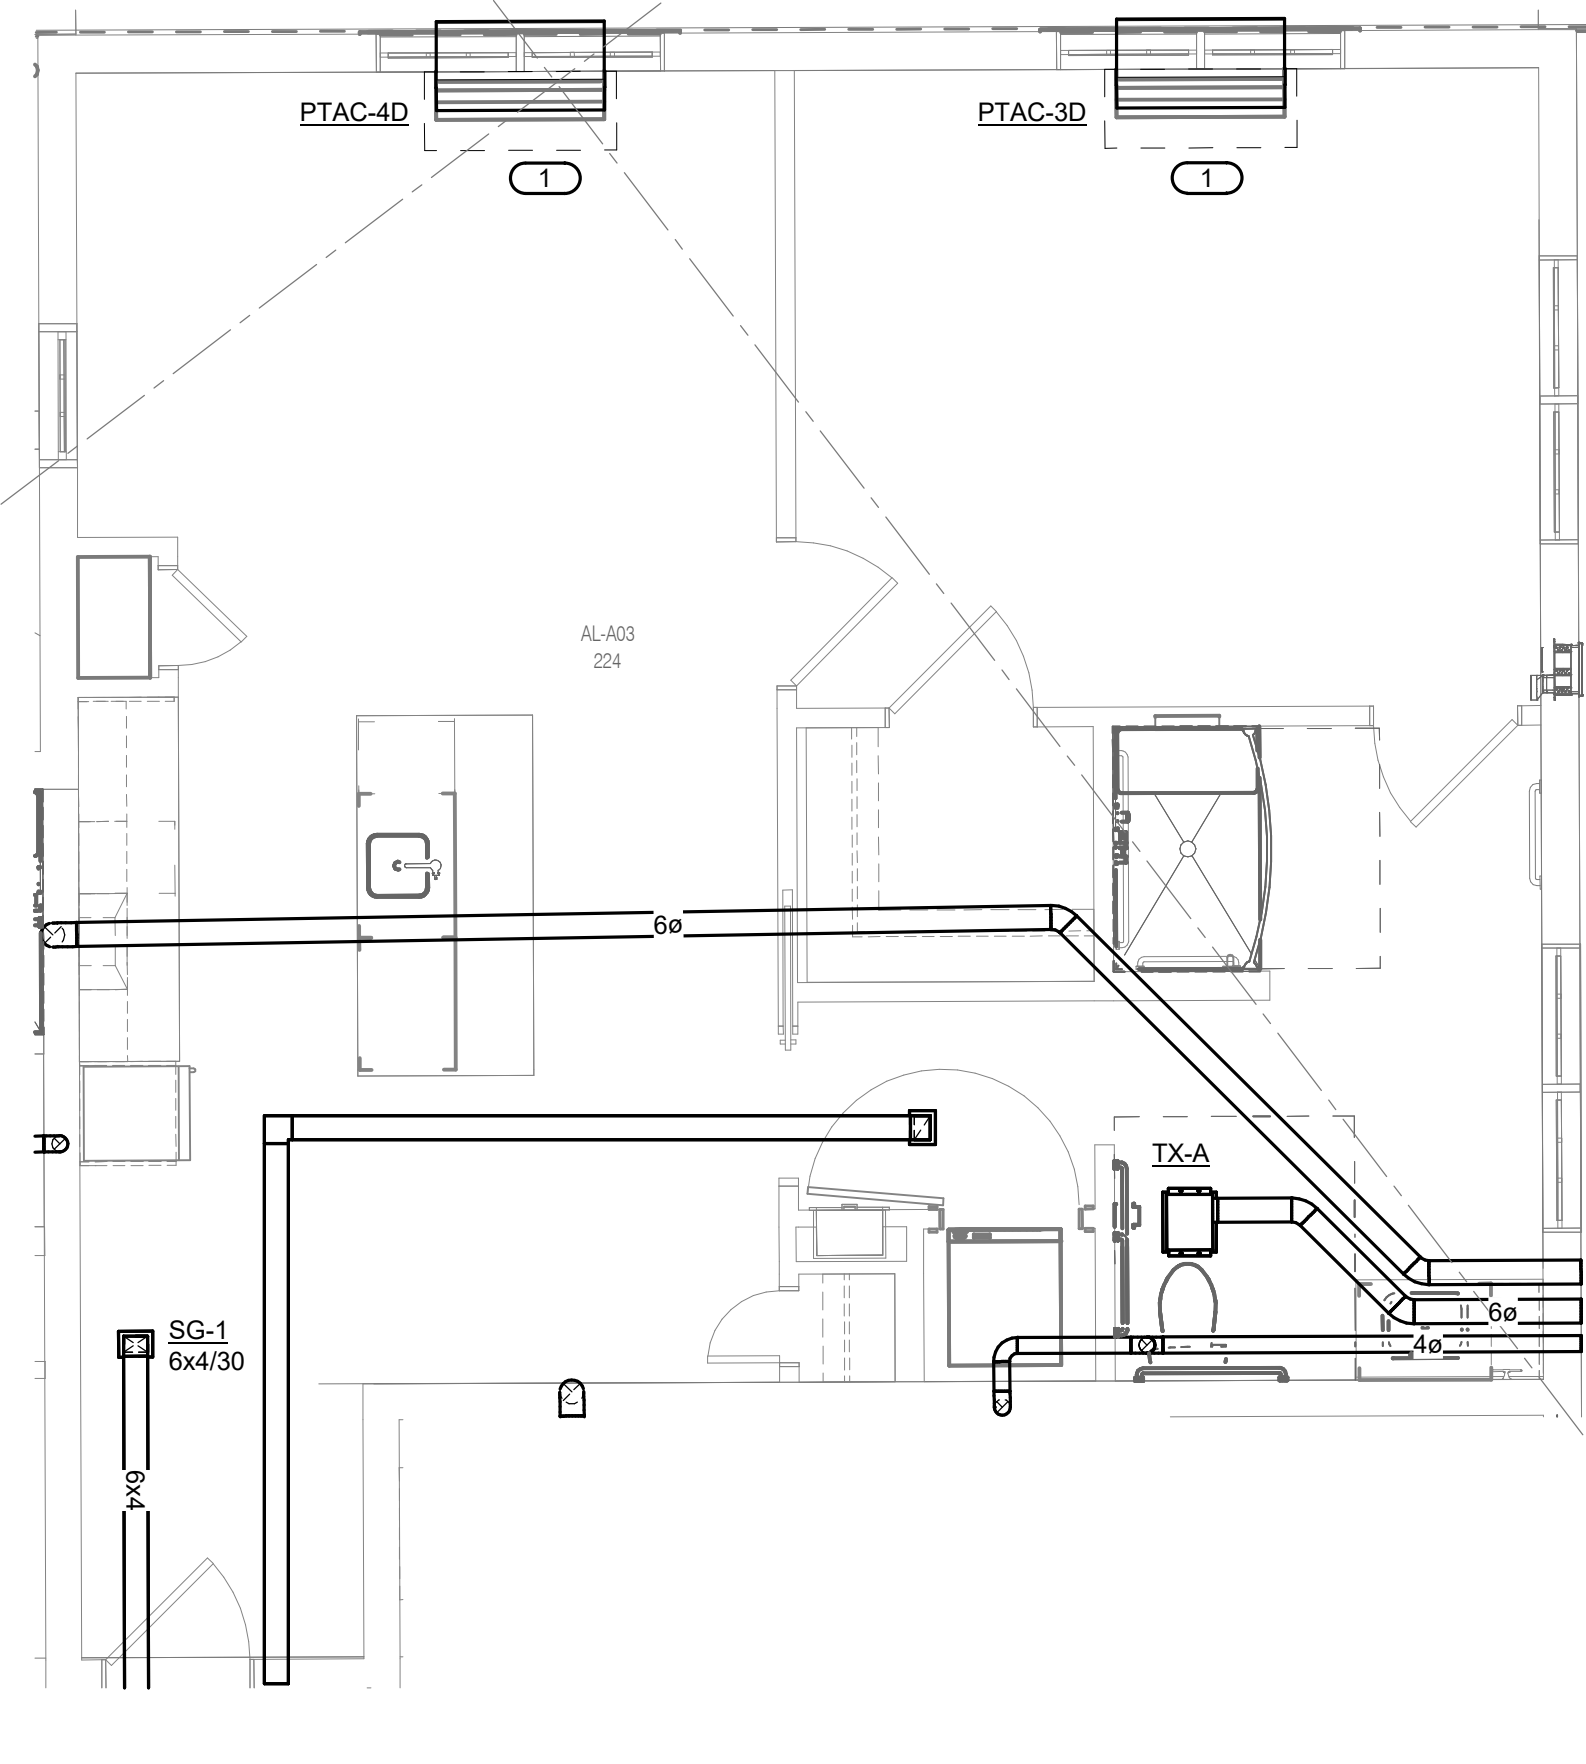


4 MECH. UNIT - 1 BED 1 BATH - AL-A03
1/4" = 1'-0"

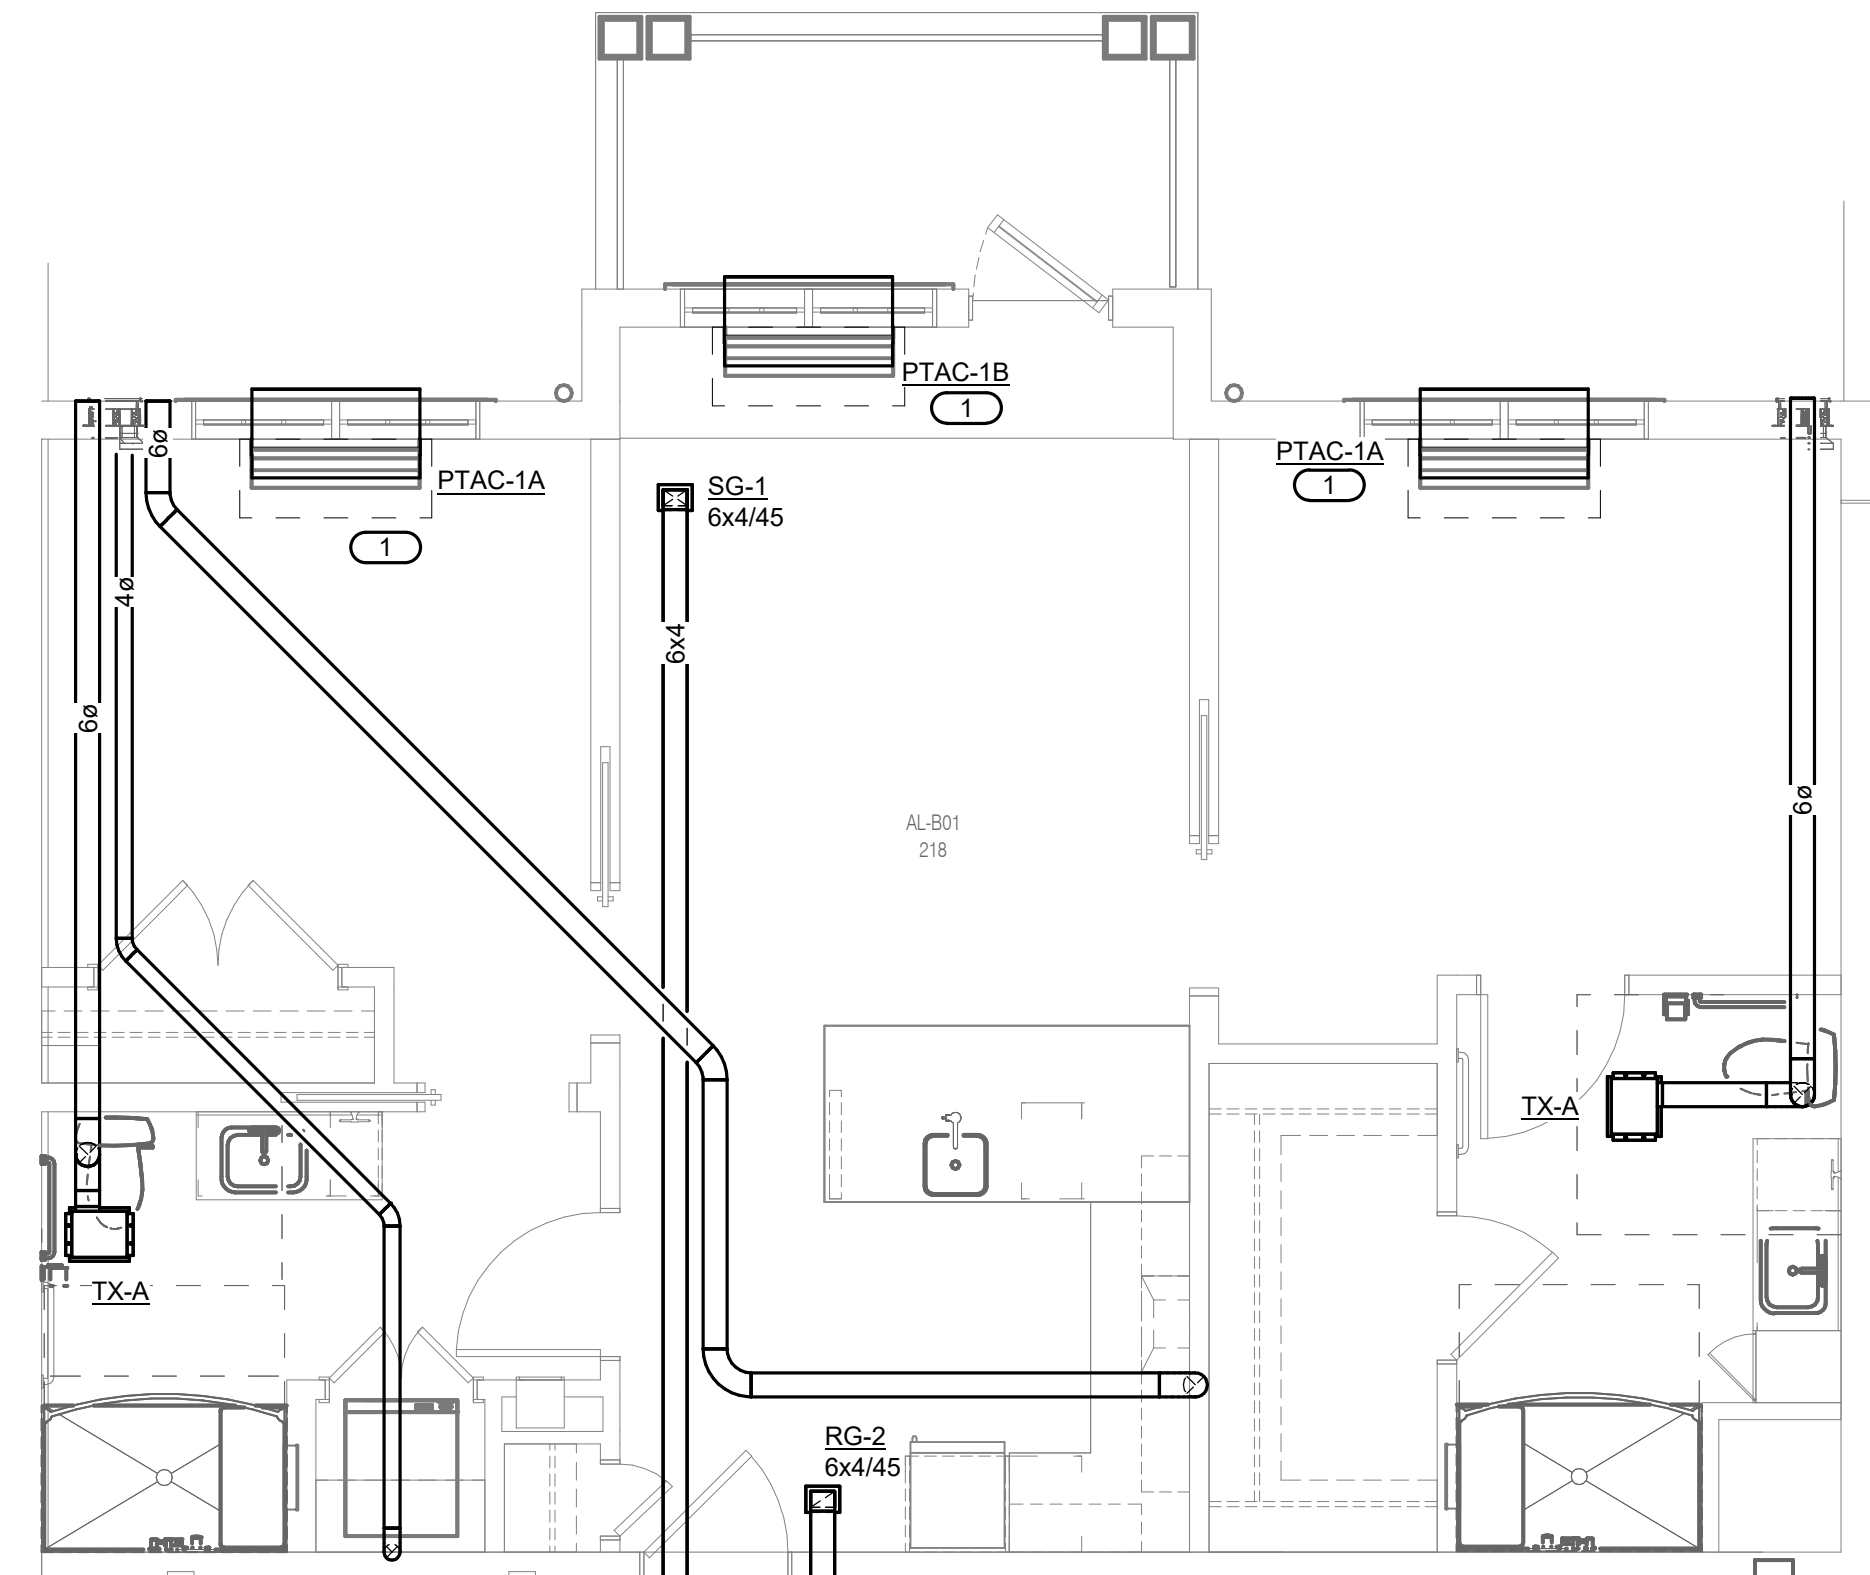


7 MECH. UNIT - 2 BED 2 BATH (TYPICAL) - AL-B01
1/4" = 1'-0"

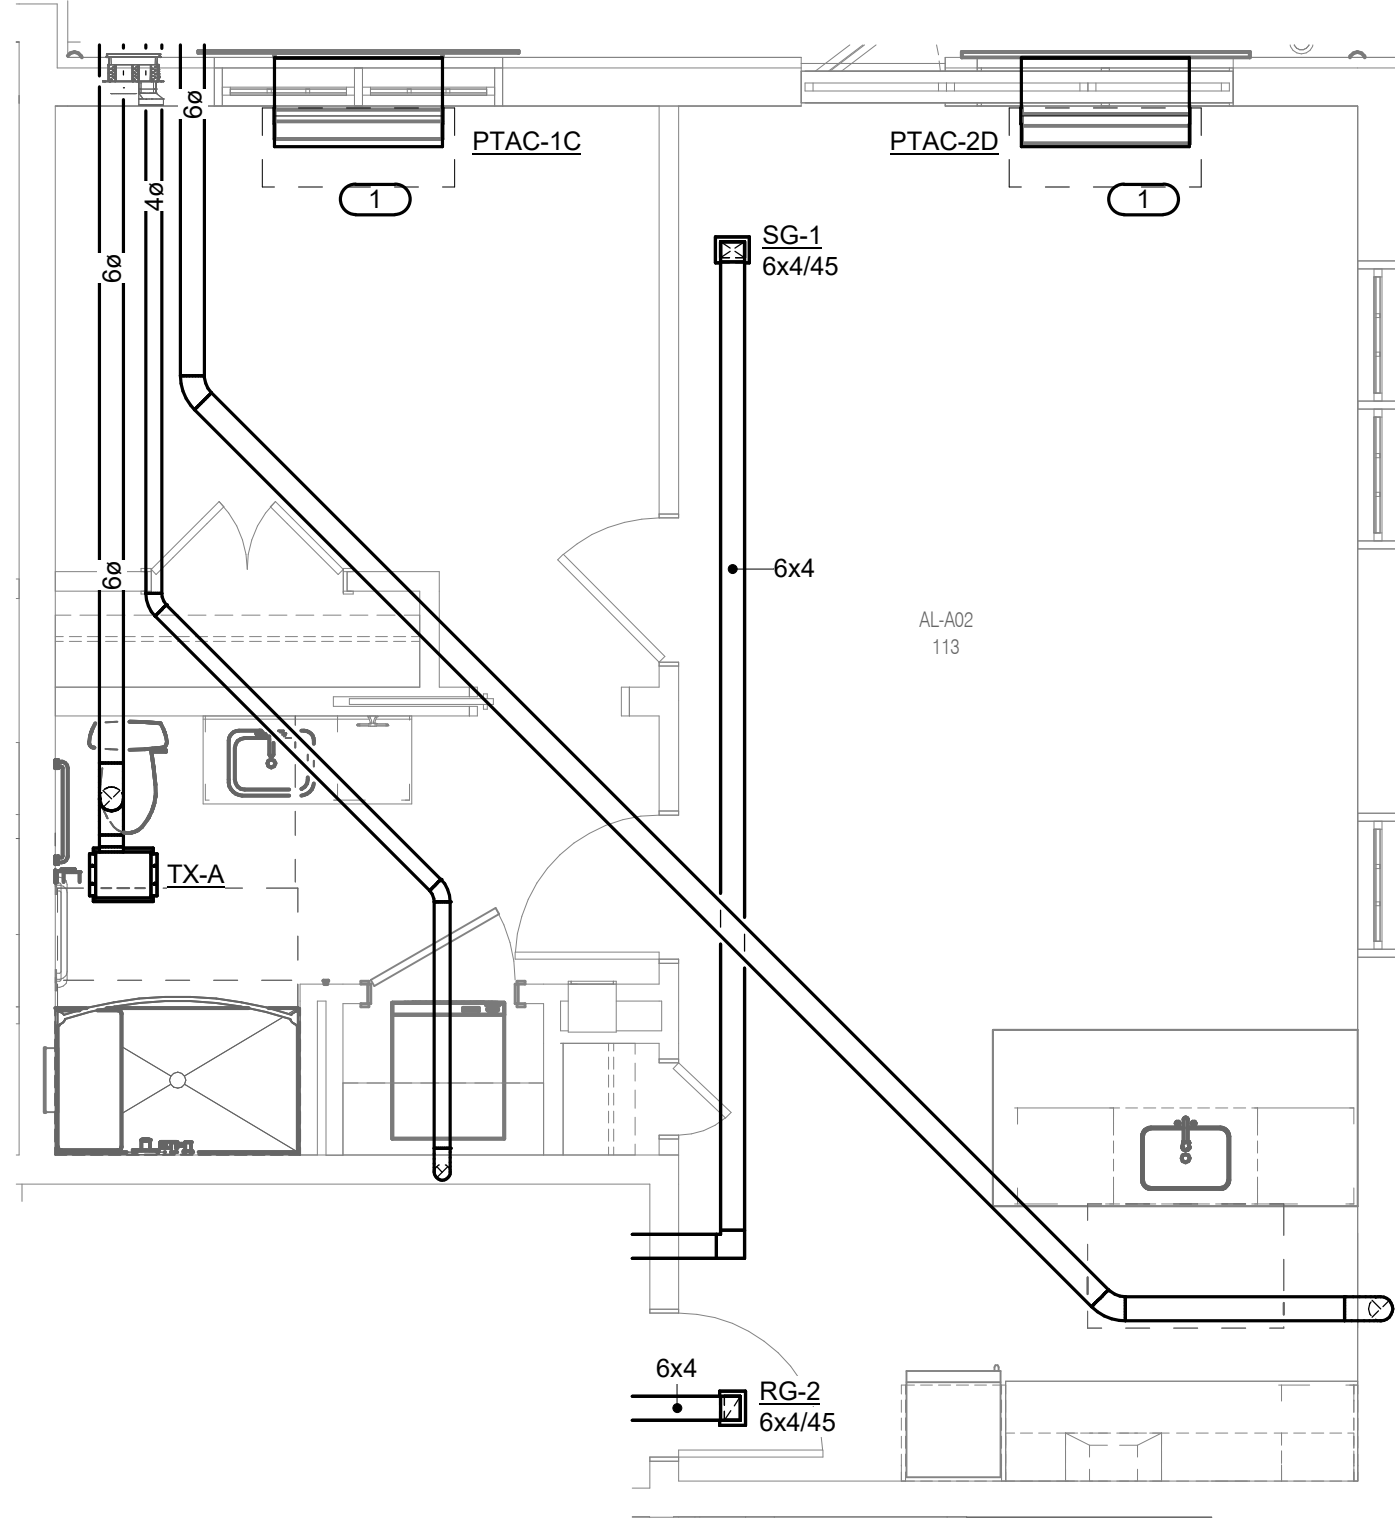


2 MECH. UNIT - 1 BED 2 BATH - AL-A02
1/4" = 1'-0"

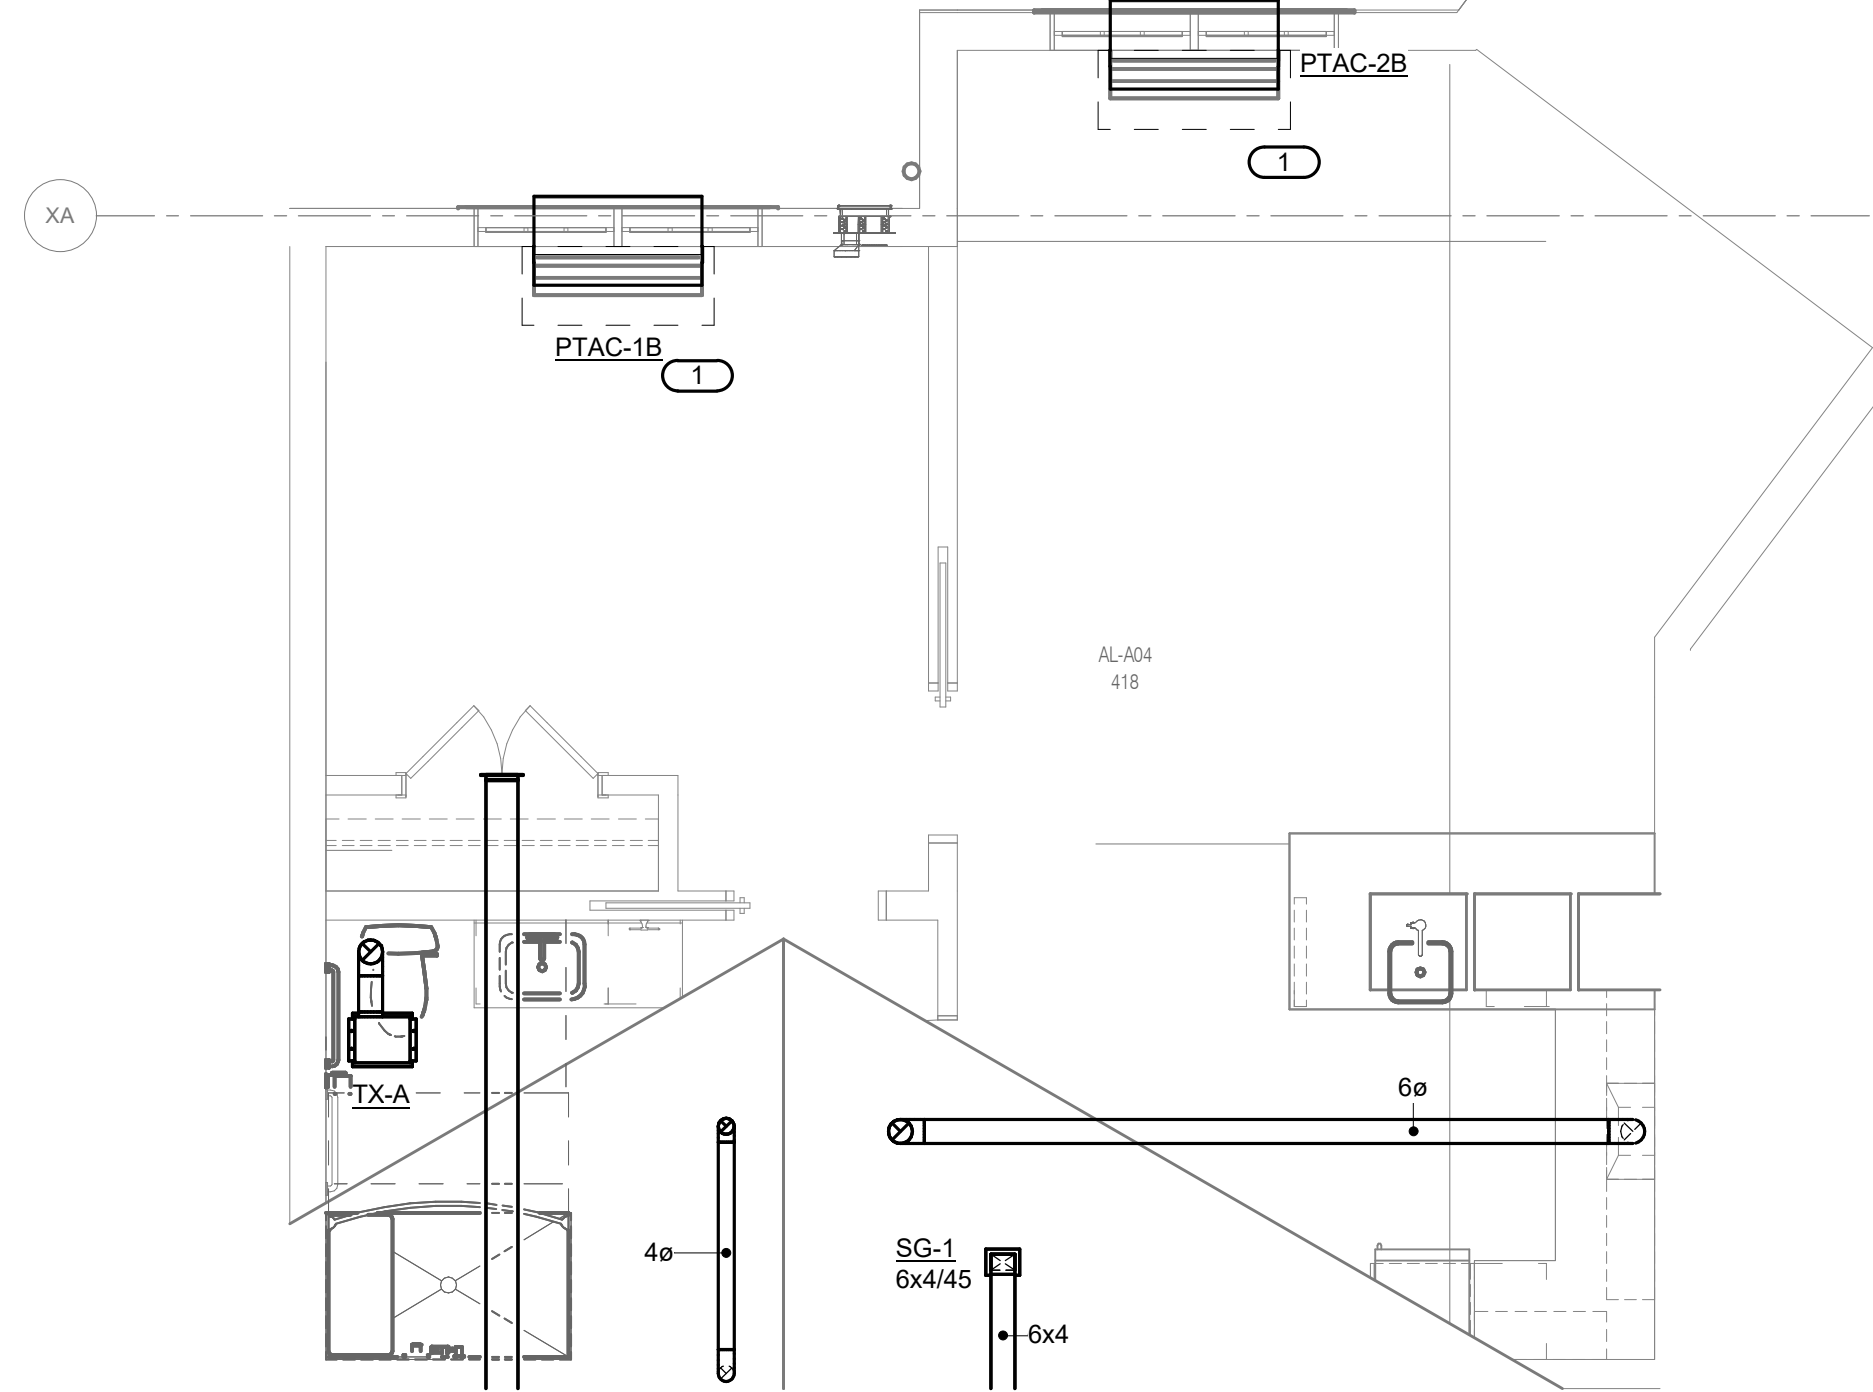

5 MECH. UNIT - 1 BED 1 BATH (LEVEL - 04) AL-A04
1/4" = 1'-0"

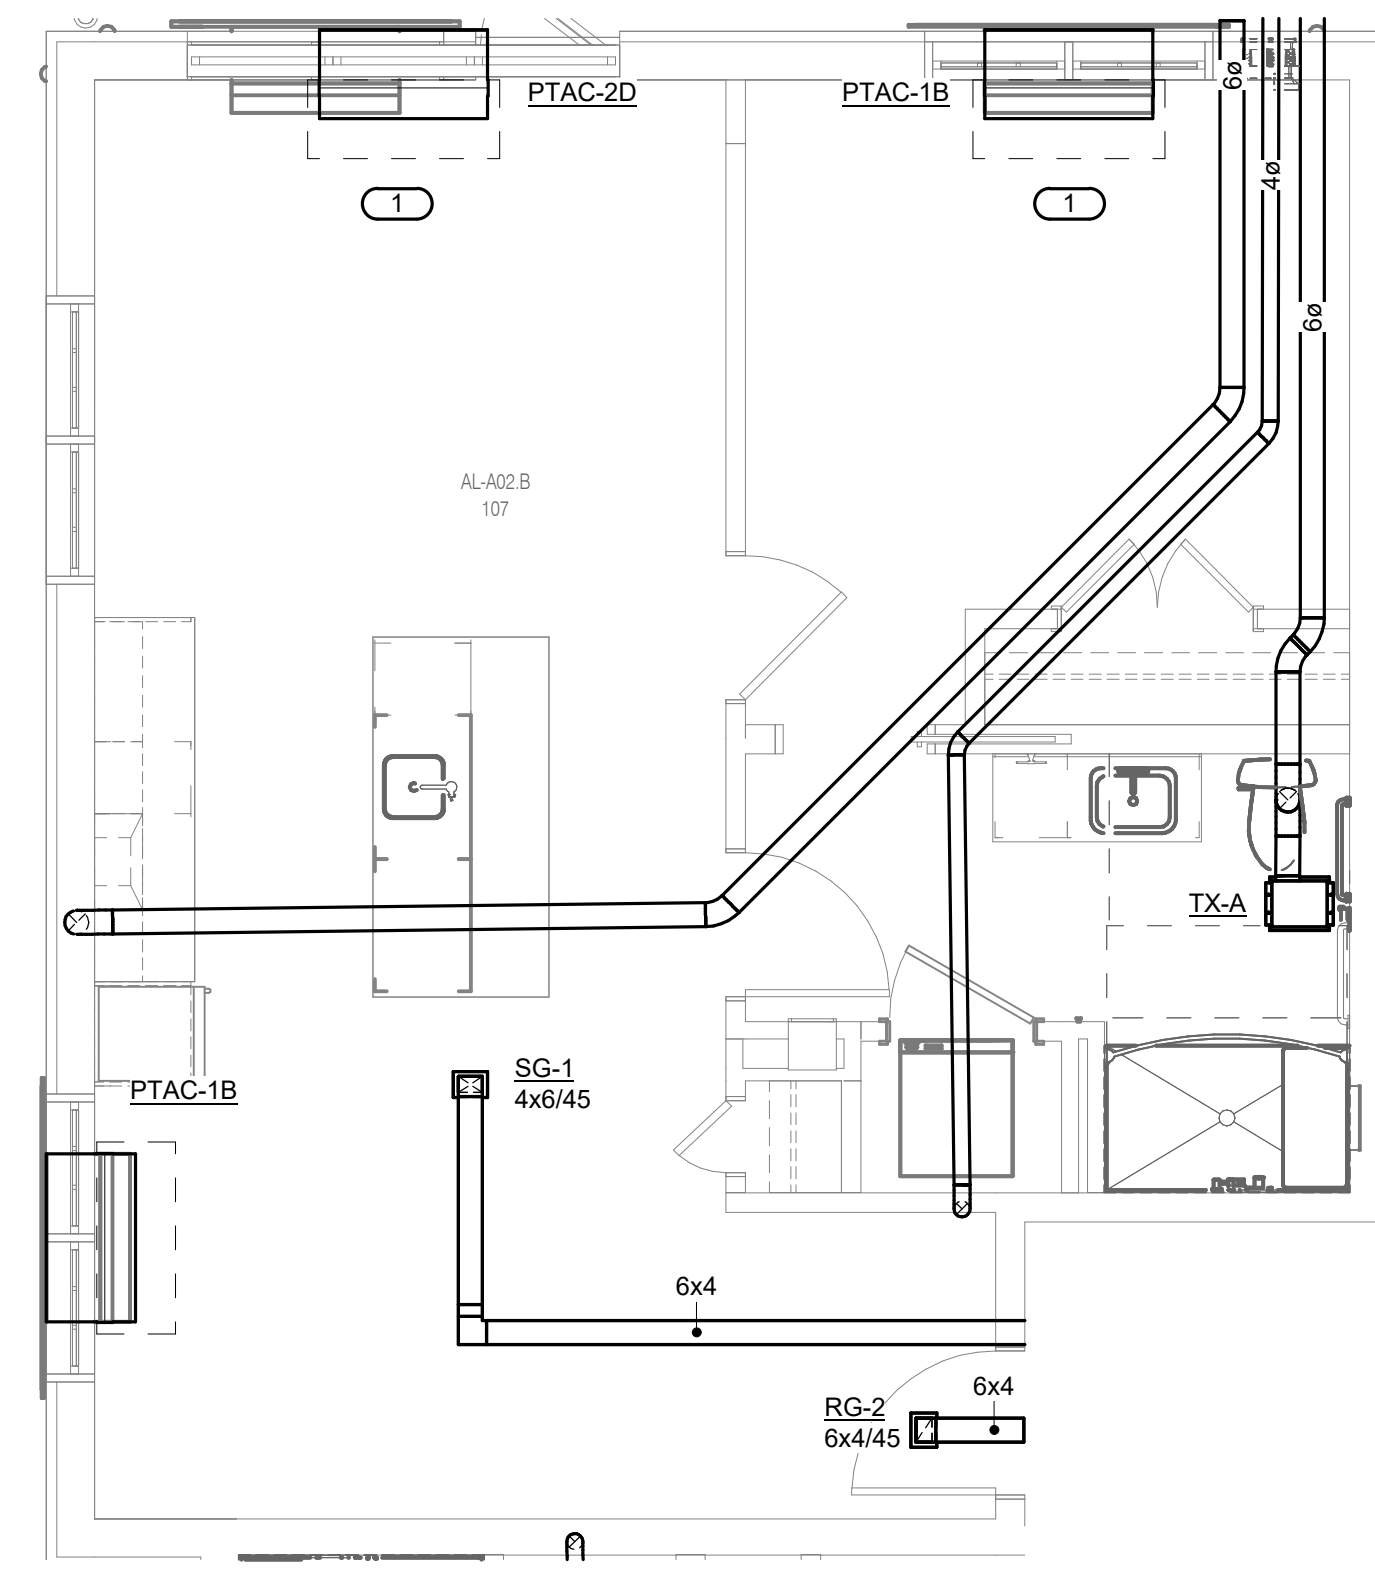



3 MECH. UNIT - (NORTH) CORNER - 1 BED 2 BATH - AL-A02.B
1/4" = 1'-0"

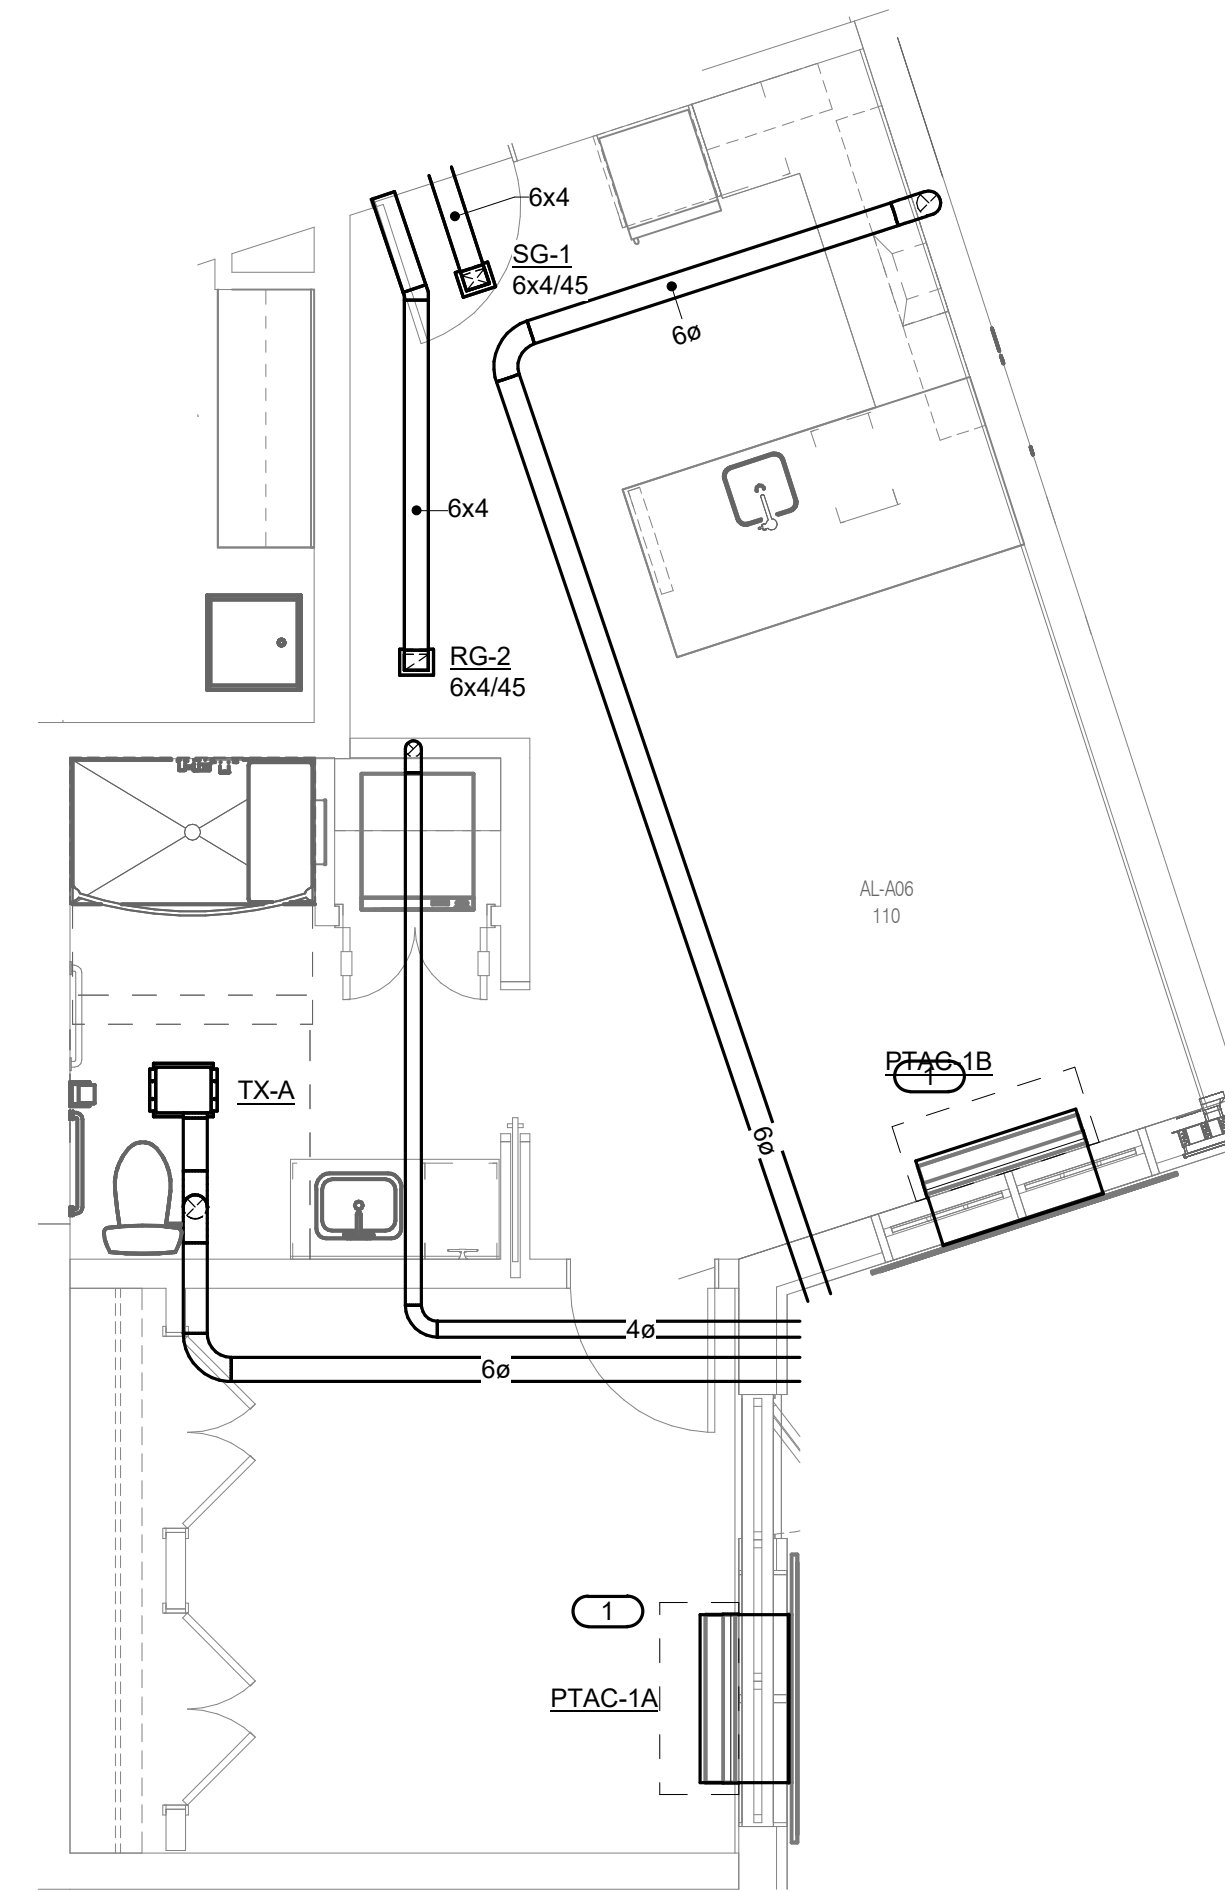

6 MECH. UNIT - 1 BED 1 BATH LVL1 - AL-A06
1/4" = 1'-0"


KEYNOTES:

1. NEW PTAC UNIT MOUNTED ON EXTERIOR WALL PER MANUFACTURER RECOMMENDATIONS. PROVIDE 3/4" CONDENSATE LINE DOWN THROUGH EXTERIOR WALL. DAYLIGHT CONDENSATE PIPE AND PROVIDE SPLASH BLOCK ON GRADE. IF MULTIPLE PTAC UNITS ARE STACKED VERTICALLY THE CONDENSATE LINES MAY BE COMBINED. PROVIDE 1" CONDENSATE LINE WHERE CONDENSATE IS COMBINED.
2. NEW EXHAUST FAN INSTALLED IN BATHROOM CEILING PER MANUFACTURER RECOMMENDATIONS.
3. ROUTE EXHAUST DUCTWORK TO EXTERIOR WALL AS REQUIRED. PROVIDE X-VENT MODEL "DVEB-46-4" AT DUCTWORK TERMINATION POINT. MAINTAIN MINIMUM 3'-0" FROM WINDOW OPENINGS AND 10'-0" FROM ANY OUTDOOR AIR INTAKES.
4. ROUTE EXHAUST DUCTWORK TO EXTERIOR WALL AS REQUIRED. PROVIDE X-VENT MODEL "DVEB-46-4" FOR BOTH DUCTWORK LINES AT TERMINATION POINT. MAINTAIN MINIMUM 3'-0" FROM WINDOW OPENINGS AND 10'-0" FROM ANY OUTDOOR AIR INTAKES.
5. ROUTE EXHAUST DUCTWORK UP THROUGH ROOF AS REQUIRED.

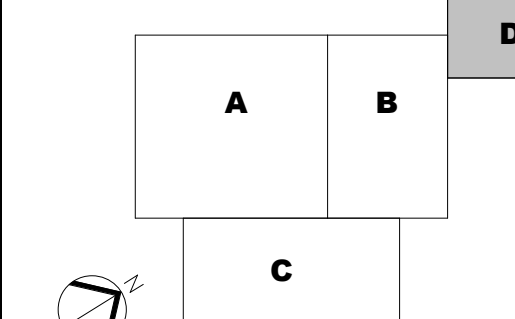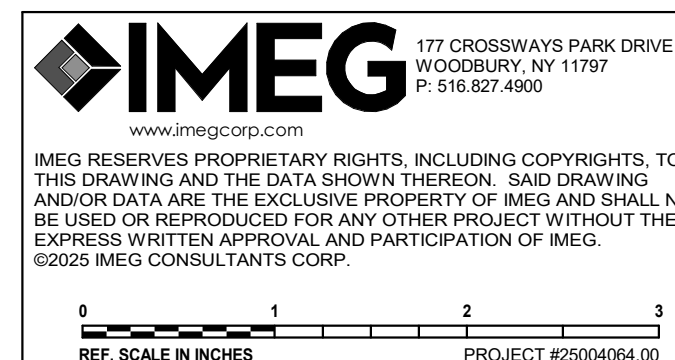


REVISION		
NO.	DESCRIPTION	DATE
1	DD Progress Print	08/26/2
2	DESIGN DEVELOPMENT	11/25/2
3	EXTERIOR BUILDING PERMIT	12/23/2
4	100% DESIGN DEVELOPMENT	01/30/2
5	ISSUED FOR PERMIT	06/05/2


TITLE BLOCK VERSION: 20160303
MODEL: A:\0000\Draw\25027292-000_Sunrise_Rye Brook NY_Senior Living\A\MEP\25004064-00_CAD\MEP.dwg
PROJECT ADDRESS: 300 Kings Rd, Rye Brook, NY 10573
PRINT DATE: 11/05/2016 12:45:24 PM
TEMPORARY VERSION: 23.0.1

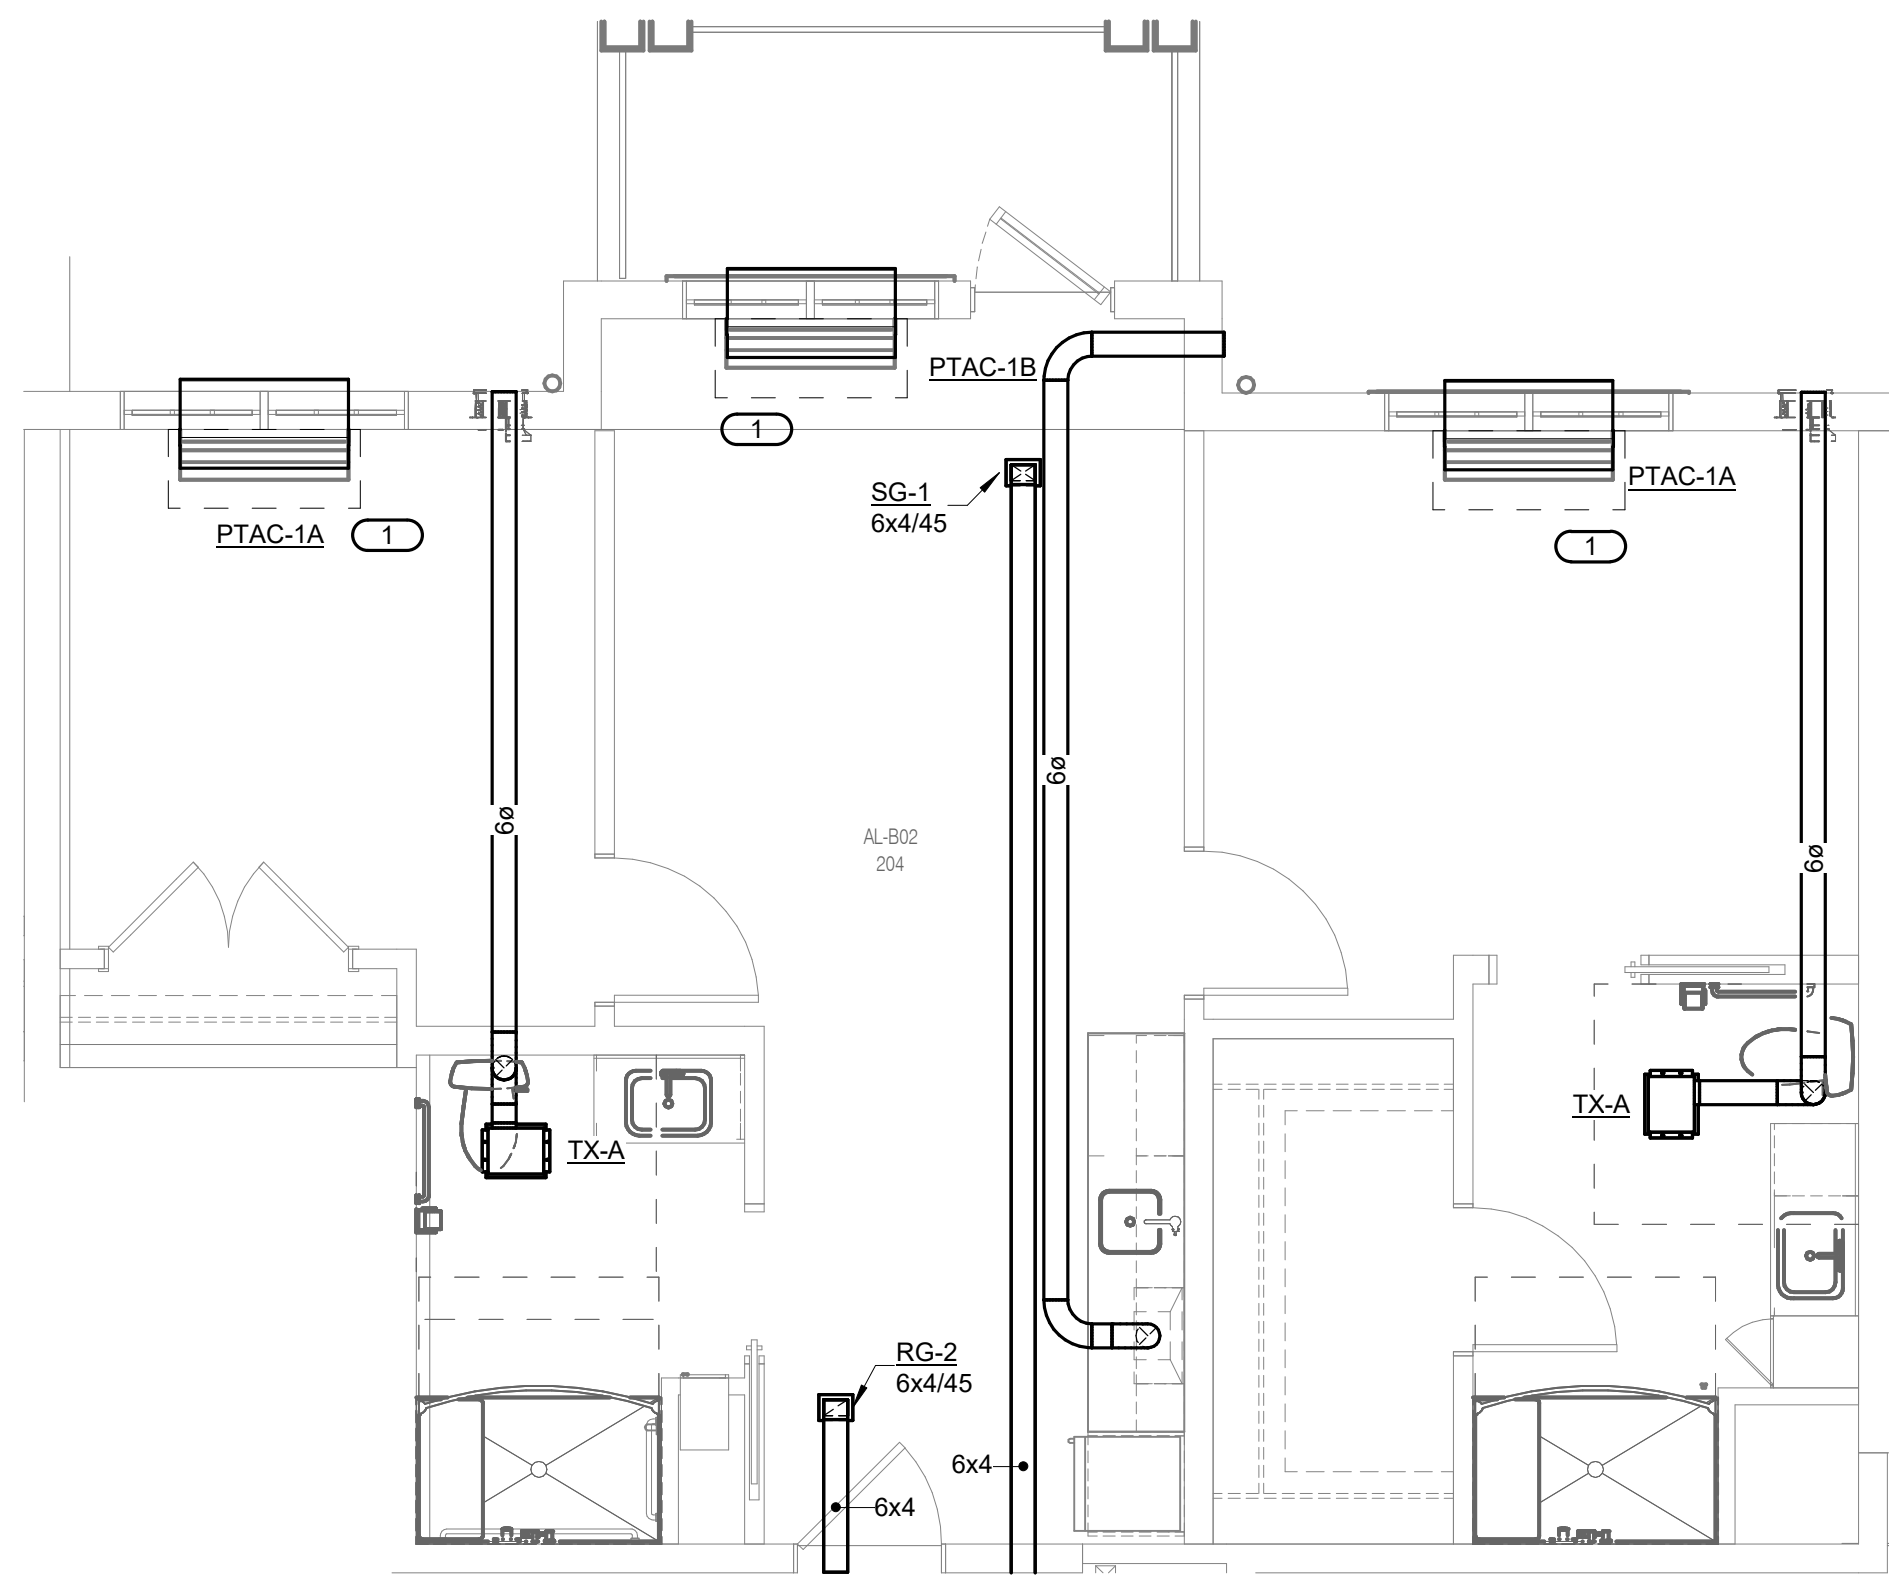


1 MECH. UNIT - 2 BED 2 BATH - AL-B02
1/4" = 1'-0"

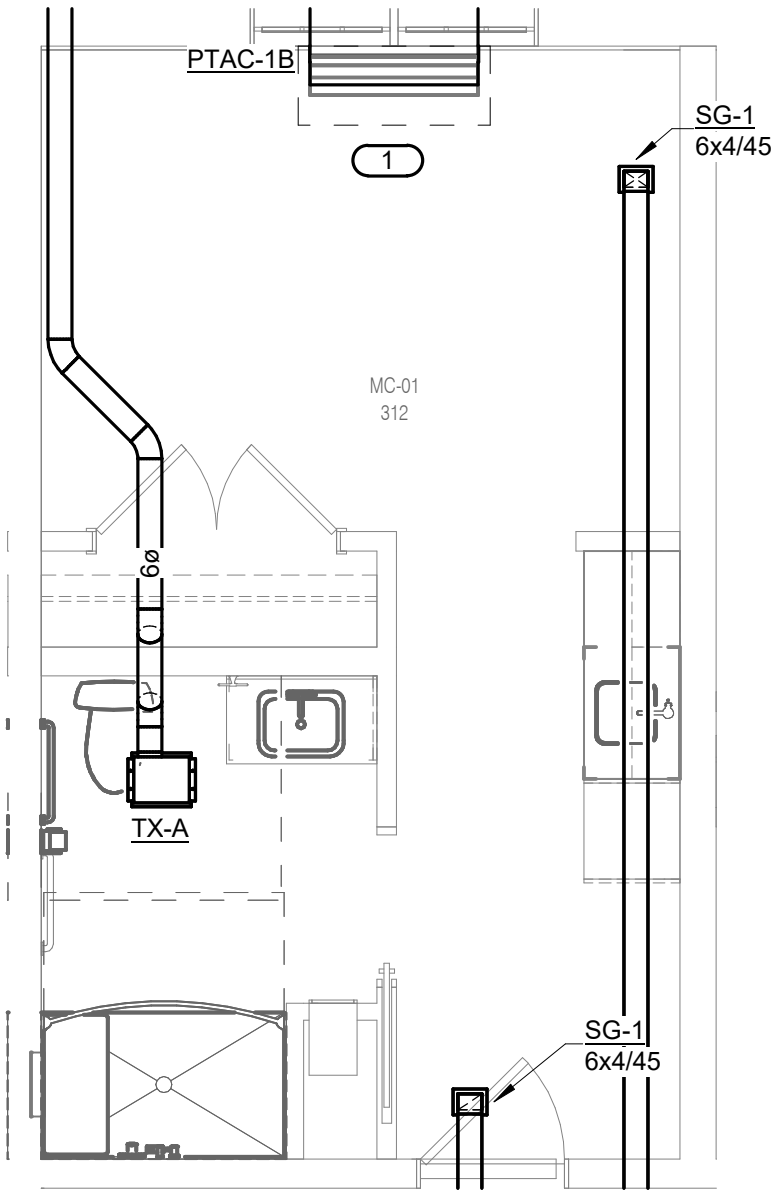


2 MECH. REM - PRIVATE (TYPICAL) - MC-01
1/4" = 1'-0"

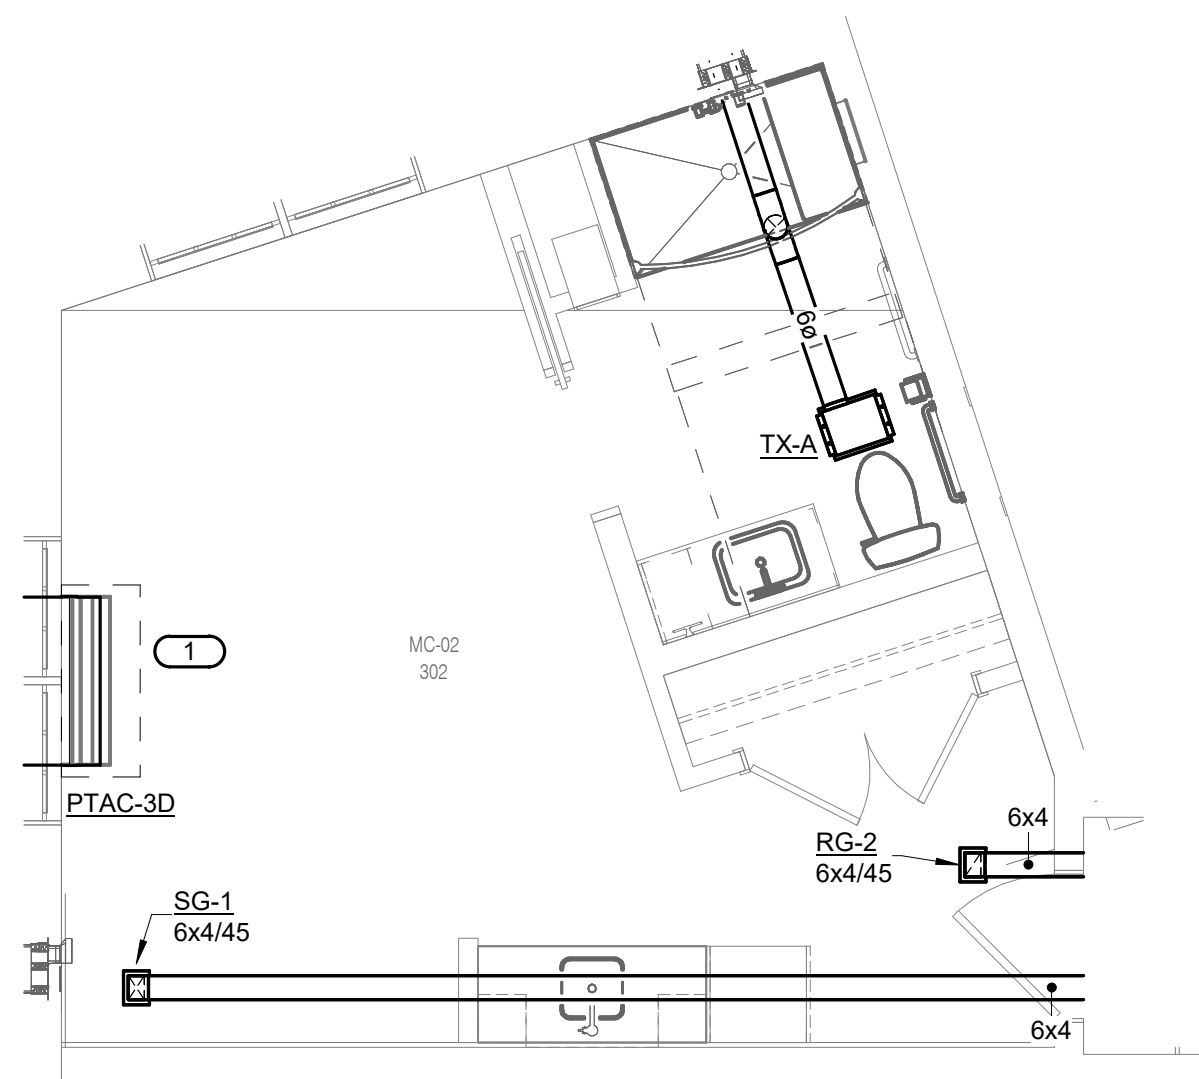


3 MECH. REM - PRIVATE - CORNER UNIT - MC-02
1/4" = 1'-0"

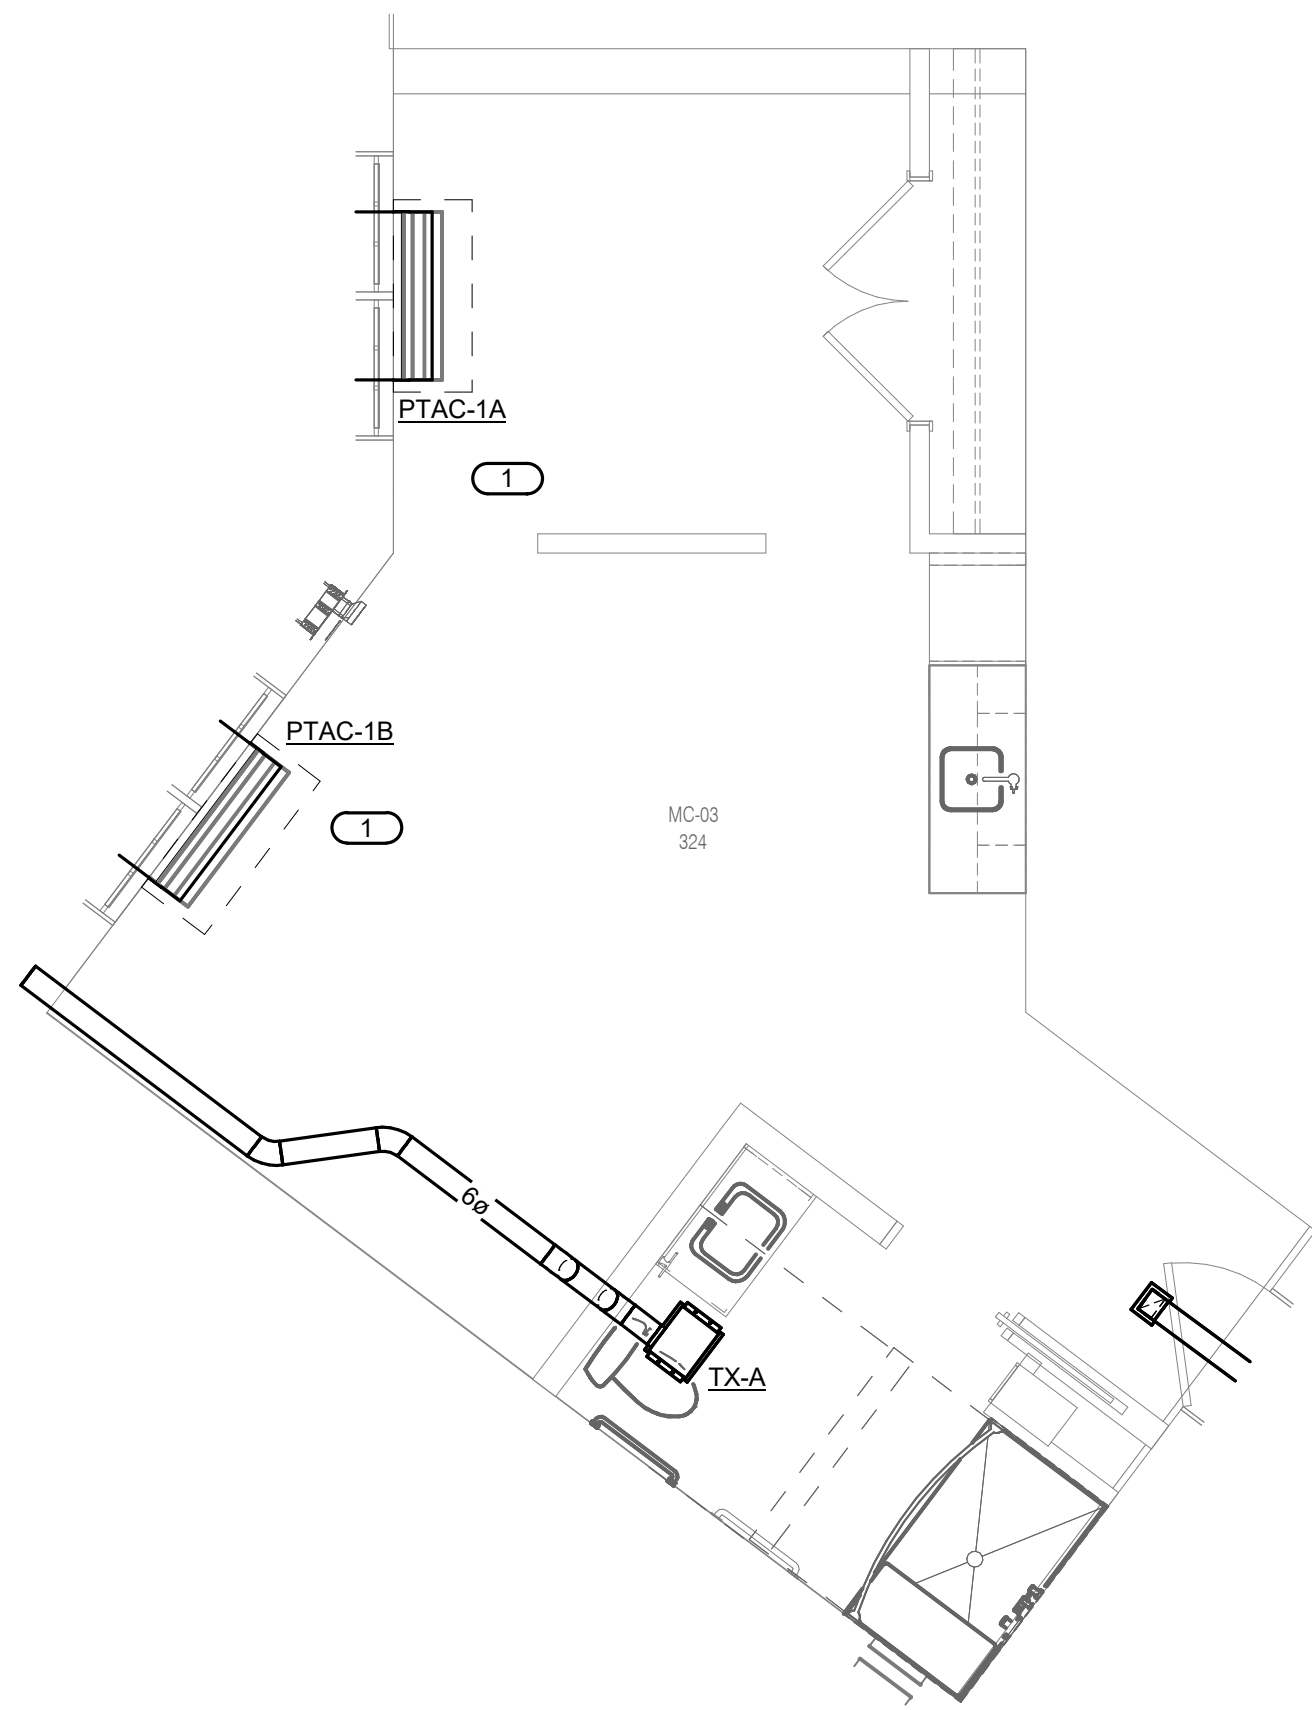

4 MECH. REM - PRIVATE - CORNER UNIT - MC-03
1/4" = 1'-0"

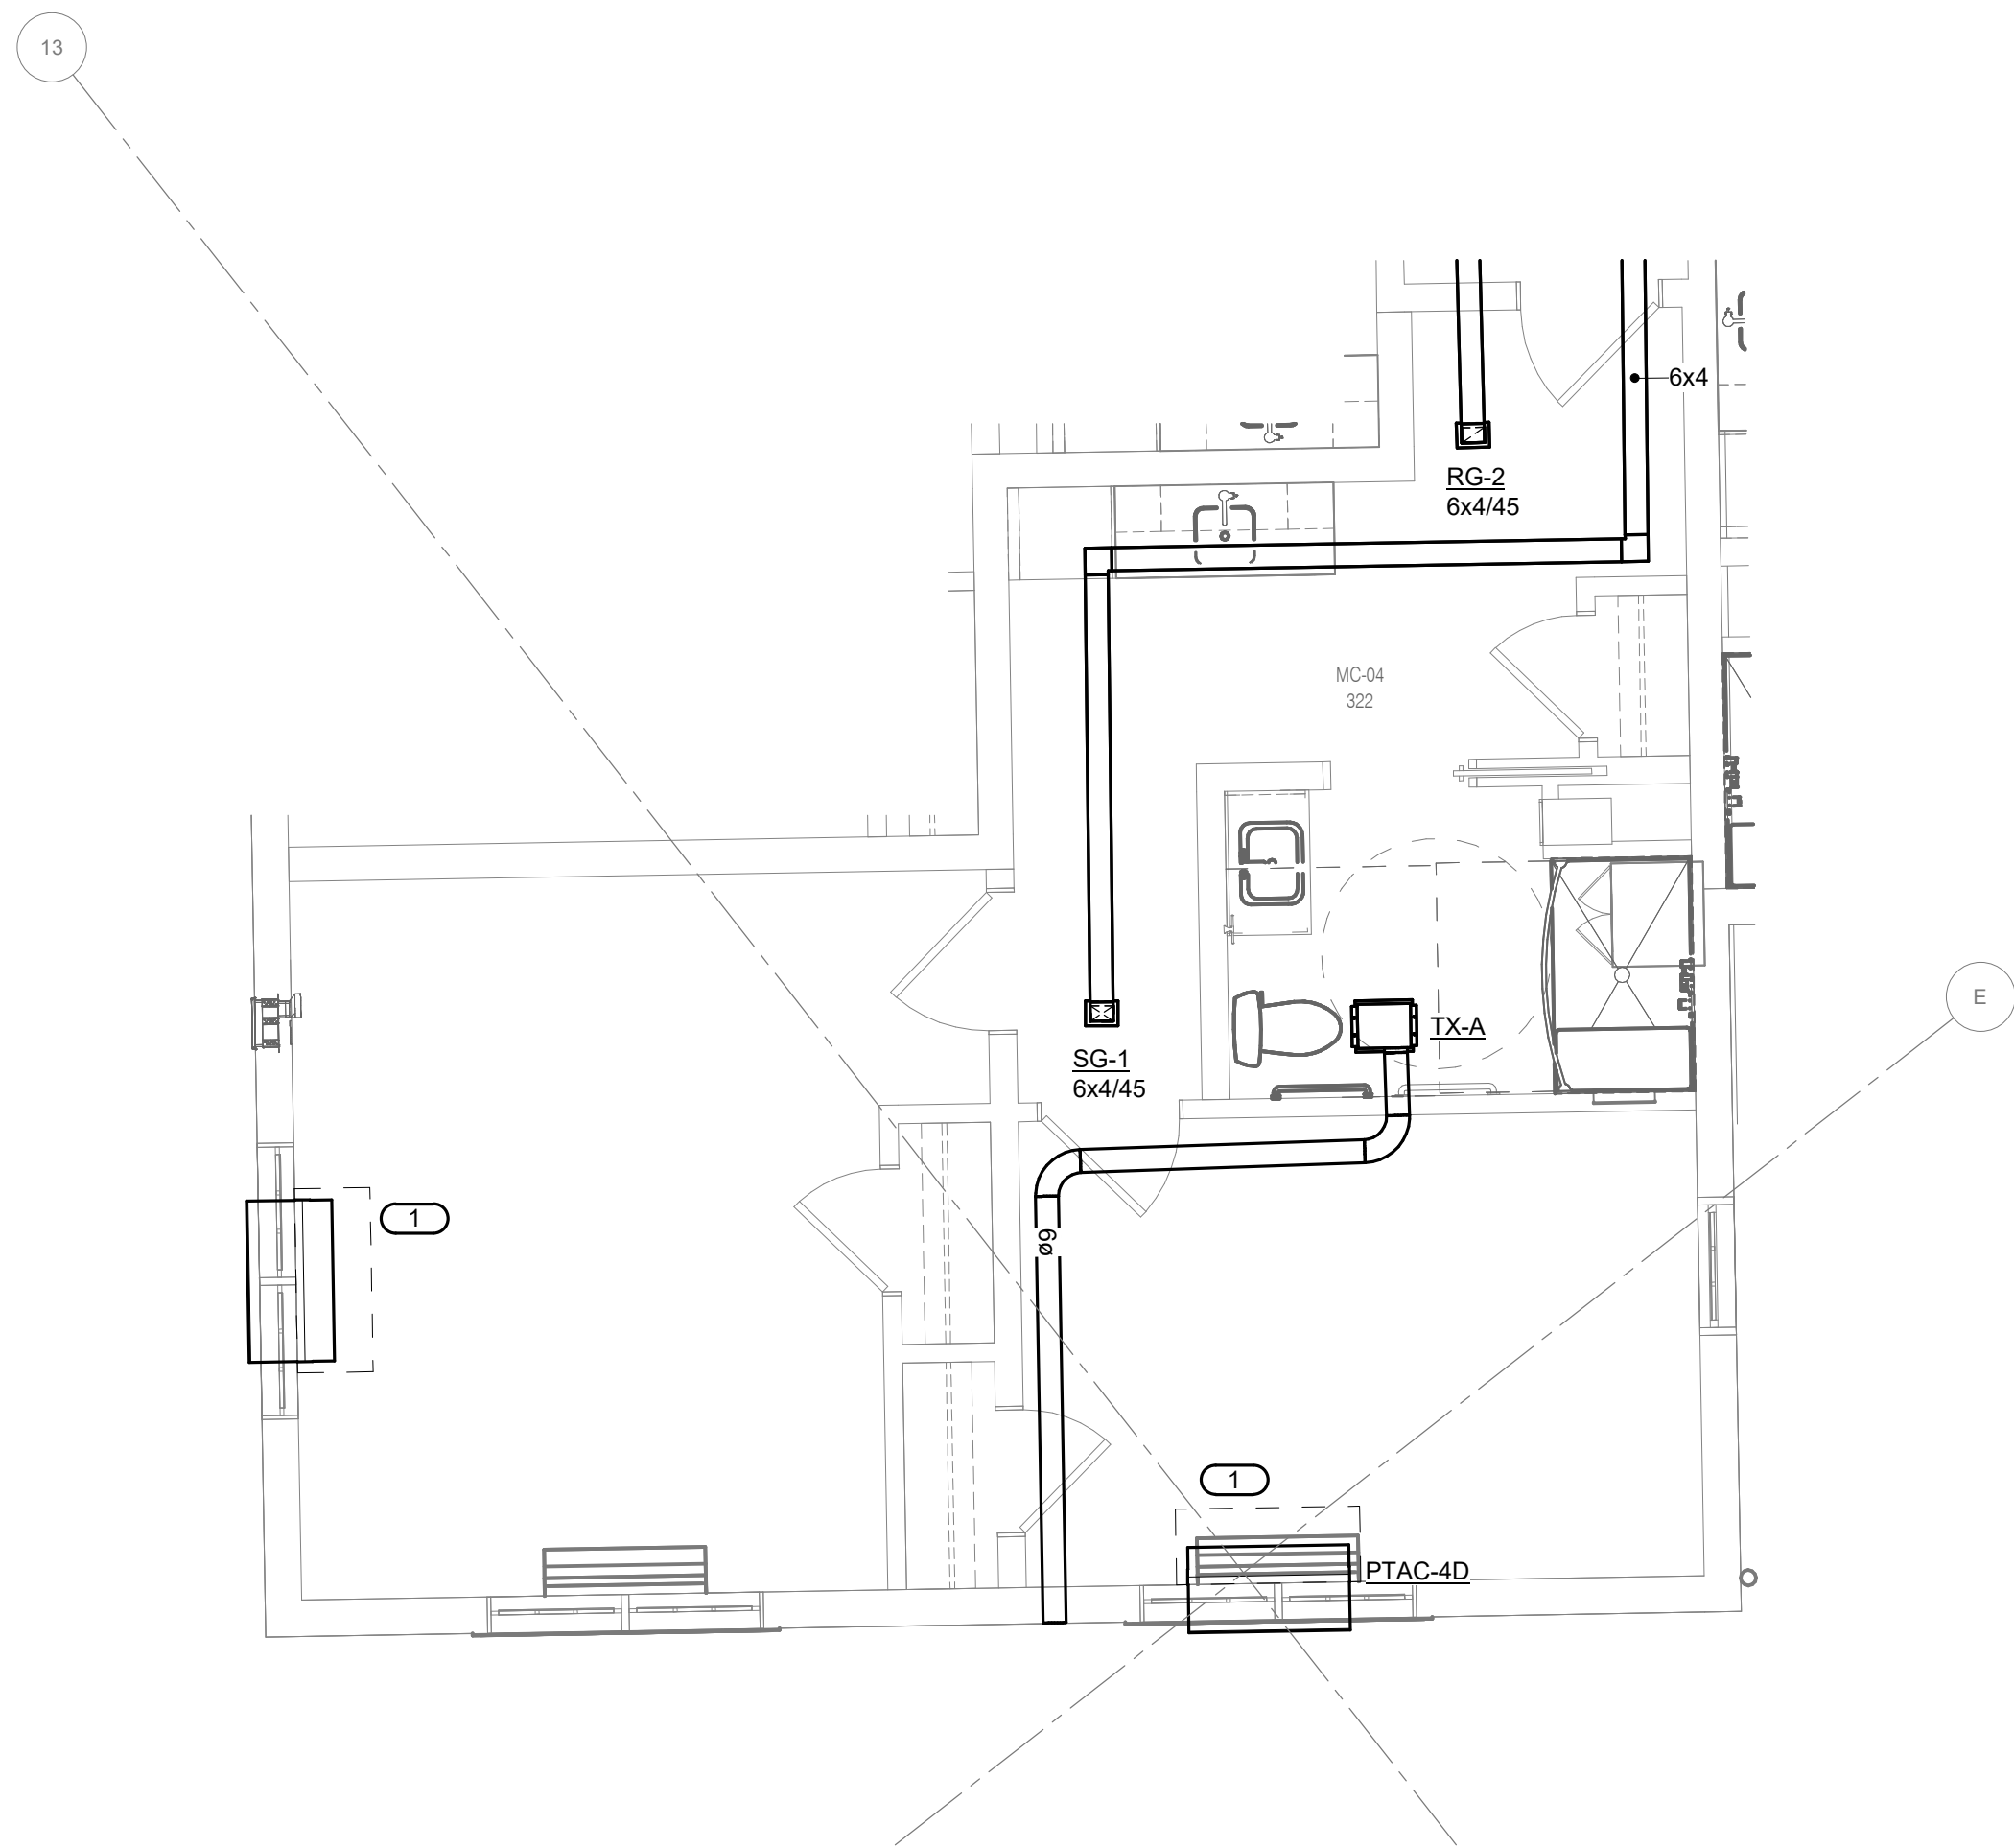


5 MECH. REM - SHARED (TYPICAL) - MC-04
1/4" = 1'-0"

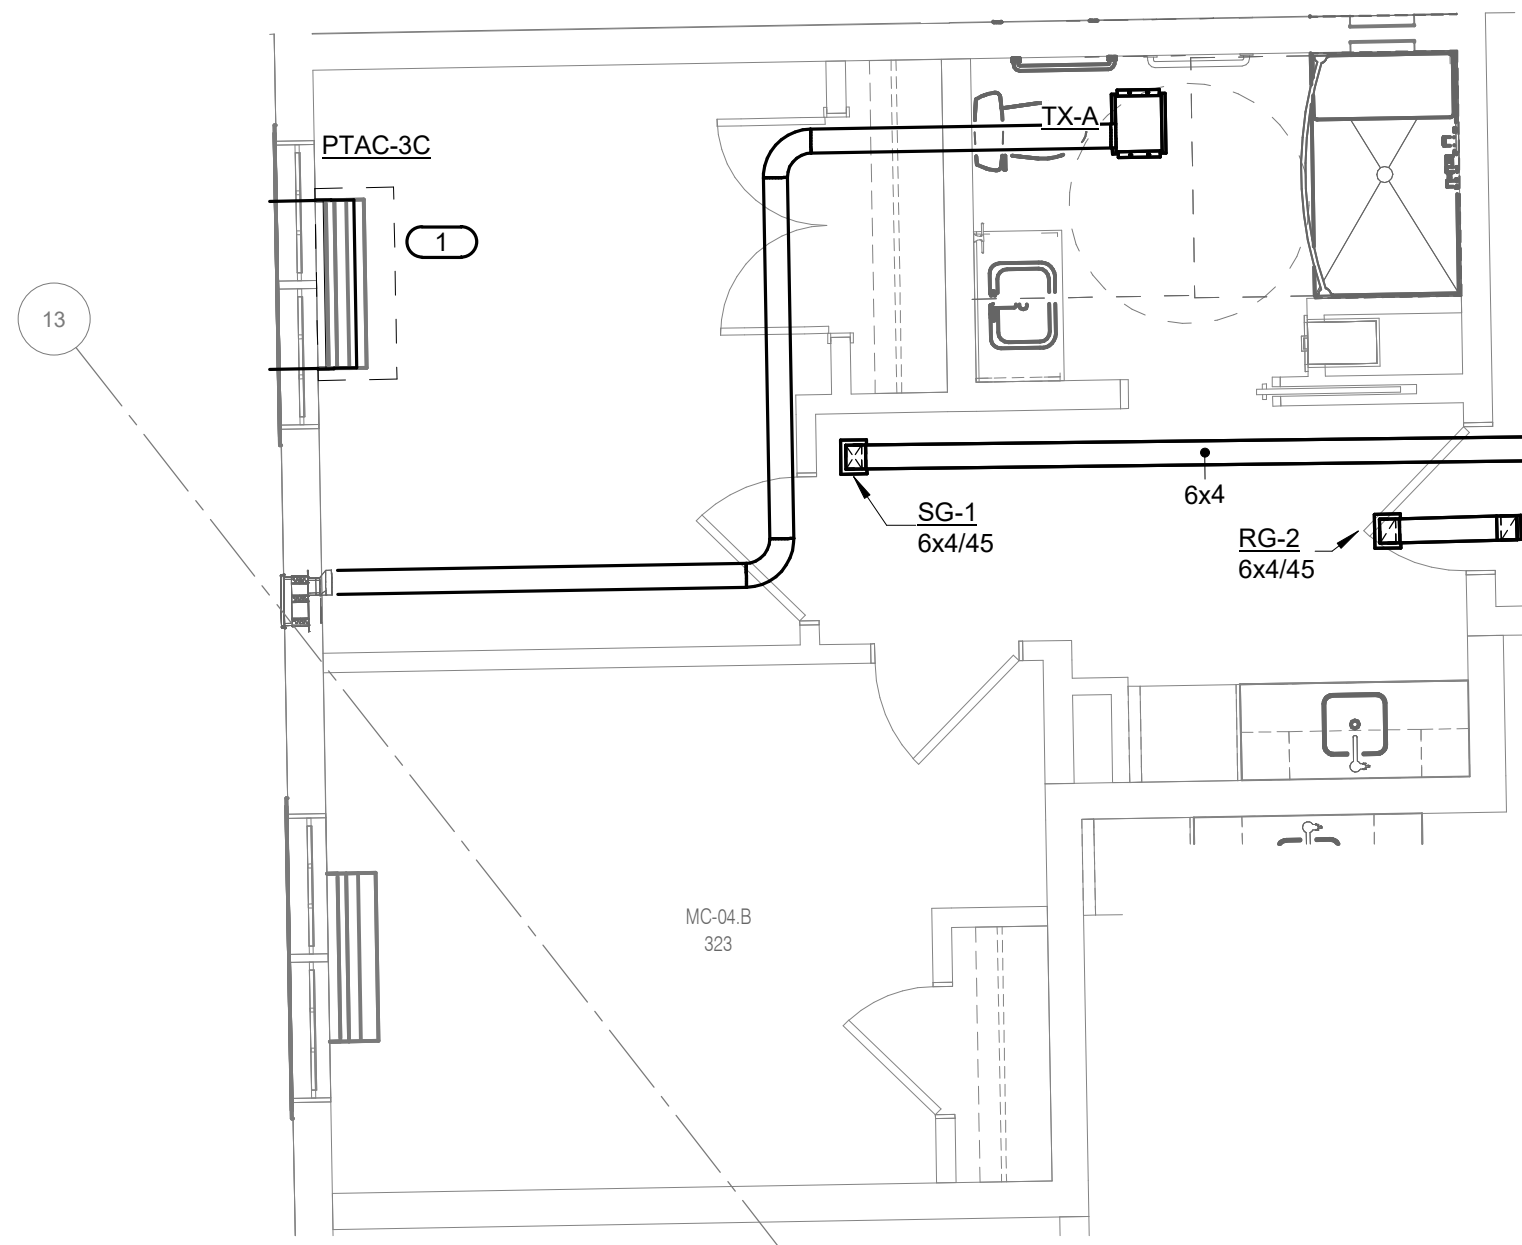

6 MECH. MC-04.B
1/4" = 1'-0"

- KEYNOTES:**
1. NEW PTAC UNIT MOUNTED ON EXTERIOR WALL PER MANUFACTURER RECOMMENDATIONS. PROVIDE 3/4" CONDENSATE LINE DOWN THROUGH EXTERIOR WALL. DAYLIGHT CONDENSATE PIPE AND PROVIDE SPLASH BLOCK ON GRADE. IF MULTIPLE PTAC UNITS ARE STACKED VERTICALLY THE CONDENSATE LINES MAY BE COMBINED. PROVIDE 1" CONDENSATE LINE WHERE CONDENSATE IS COMBINED.
 2. NEW EXHAUST FAN INSTALLED IN BATHROOM CEILING PER MANUFACTURER RECOMMENDATIONS.
 3. ROUTE EXHAUST DUCTWORK TO EXTERIOR WALL AS REQUIRED. PROVIDE XVENT MODEL: '6SEB-P' AT DUCTWORK TERMINATION POINT. MAINTAIN MINIMUM 3'-0" FROM WINDOW OPENINGS AND 10'-0" FROM ANY OUTDOOR AIR INTAKES.
 4. ROUTE EXHAUST DUCTWORK TO EXTERIOR WALL AS REQUIRED. PROVIDE XVENT MODEL: 'OVES-66-P' FOR BOTH DUCTWORK LINES AT TERMINATION POINT. MAINTAIN MINIMUM 3'-0" FROM WINDOW OPENINGS AND 10'-0" FROM ANY OUTDOOR AIR INTAKES.
 5. ROUTE EXHAUST DUCTWORK UP THROUGH ROOF AS REQUIRED.

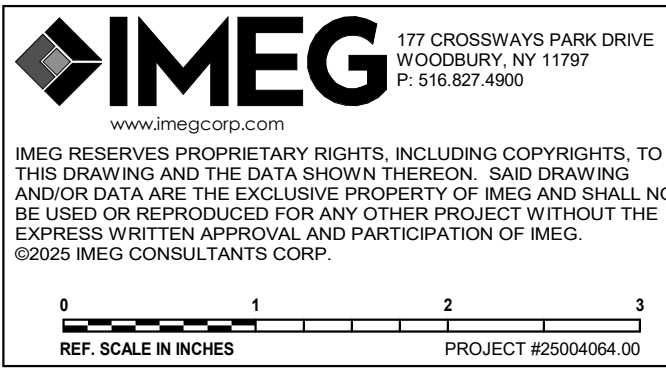

HKS

ARCHITECT
HKS ARCHITECTS, P.C.
30 WEST 26th STREET, 12th FLOOR
NEW YORK, NY 10010

STRUCTURAL
MEG
1411 BROADWAY, SUITE 600
NEW YORK, NY 10018

MEP ENGINEER
MEG
177 CROSSWAYS PARK DRIVE
WOODBURY, NY 11797

LV ENGINEER
TATEROY
765 HICKORY FLAT HWY, SUITE 200
WOODSTOCK, GA 30188

LANDSCAPE ARCHITECT
MFP
120 BROADWAY, 20TH FLOOR
NEW YORK, NY 10071

POOL DESIGNER
COUNSLMAN HUNSAKER & ASSOCIATES, INC.
12851 MANCHESTER ROAD, SUITE 120
ST. LOUIS, MO 63131

FOOD SERVICE & LAUNDRY
CLARK
2551 HORSESHOE RD.
LANCASTER, PA 17601


SUNRISESM
SENIOR LIVING
RYE BROOK

DOB BSCAN | DOB STAMP & SIGNATURES

SEAL & SIGNATURE

CON NO.: 111AAA

KEY PLAN

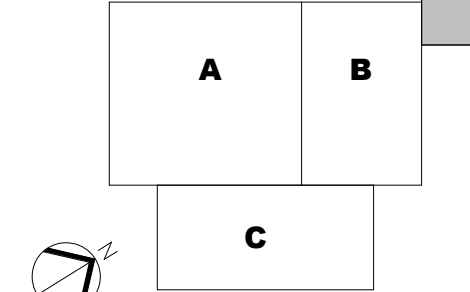

REVISION		
NO.	DESCRIPTION	DATE
1	DD Progress Print	08/26/25
2	DESIGN DEVELOPMENT	11/25/25
3	EXTERIOR BUILDING PERMIT	12/23/25
4	100% DESIGN DEVELOPMENT	01/30/26
5	ISSUED FOR PERMIT	06/05/26

HKS PROJECT NUMBER

25004064.00

DATE

07/15/26

ISSUE


ISSUED FOR GMP

SHEET TITLE
UNIT PLANS AL - MECHANICAL


SHEET NO.

M2109


DOB FILE # DOB PAGE #

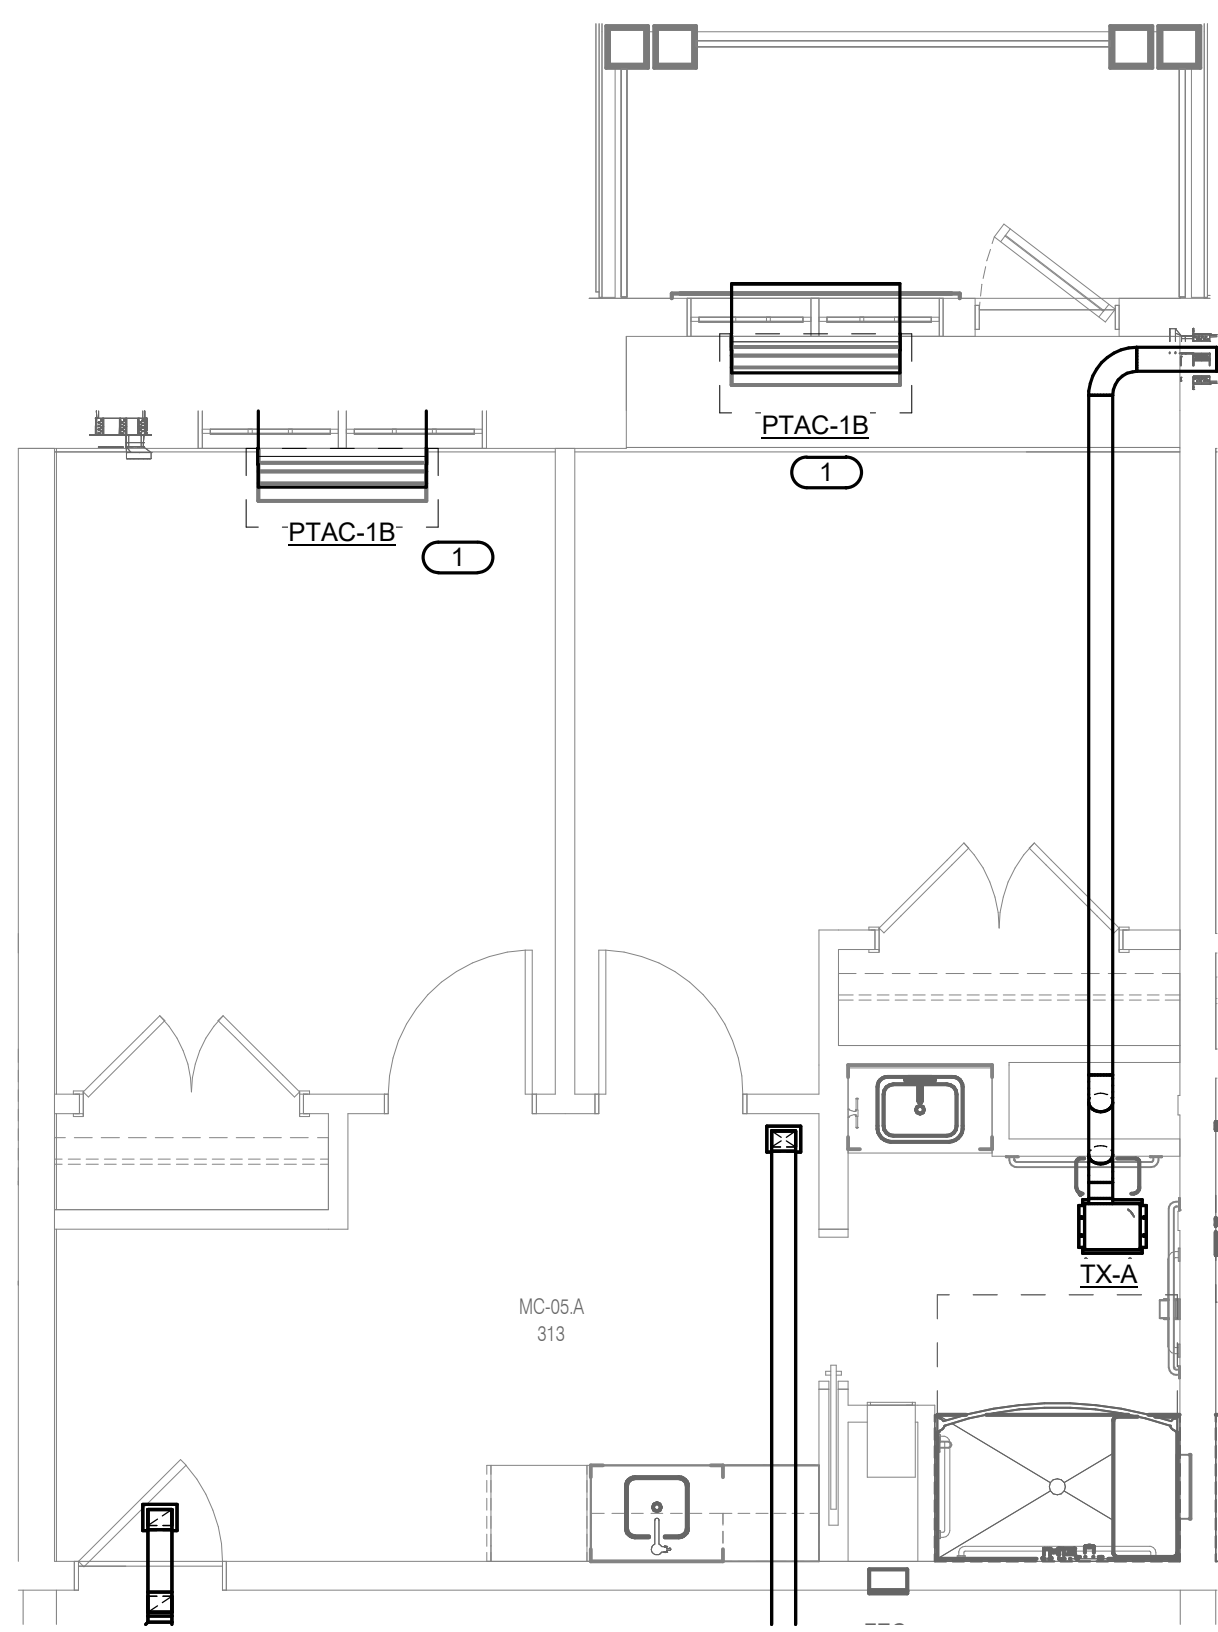


1 MECH. REM SEMI-PRIVATE (TYPICAL) - MC-05
1/4" = 1'-0"

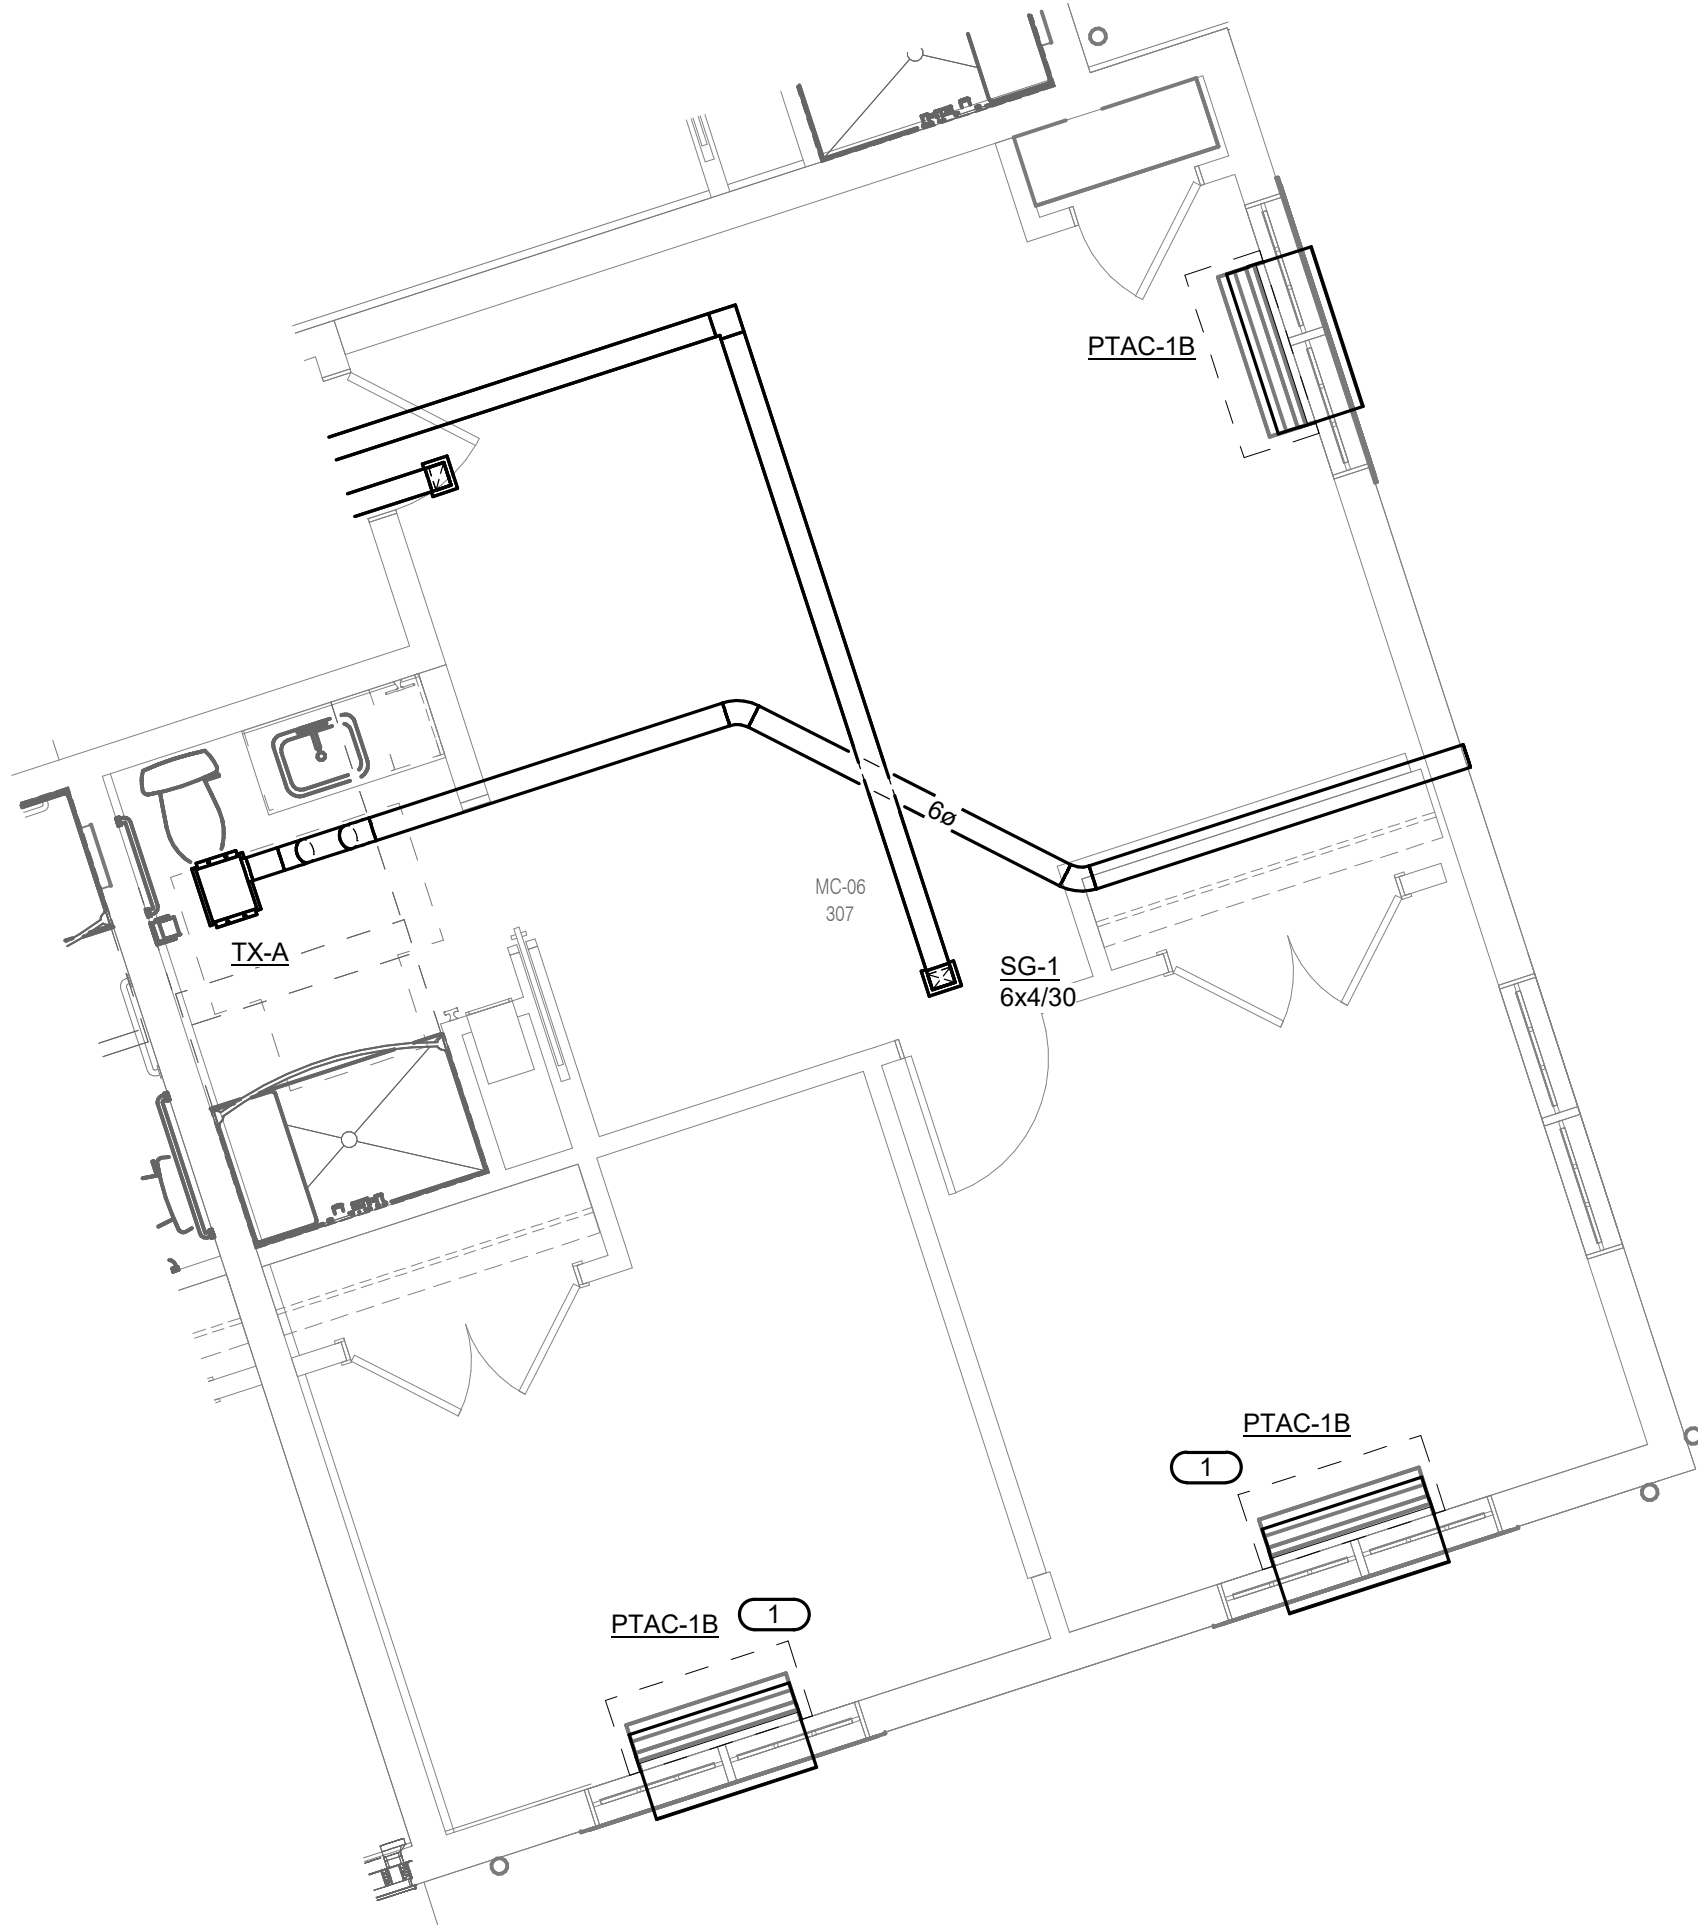

2 MECH. REM SEMI-PRIVATE - (NORTH-EAST) CORNER UNIT - MC-06
1/4" = 1'-0"

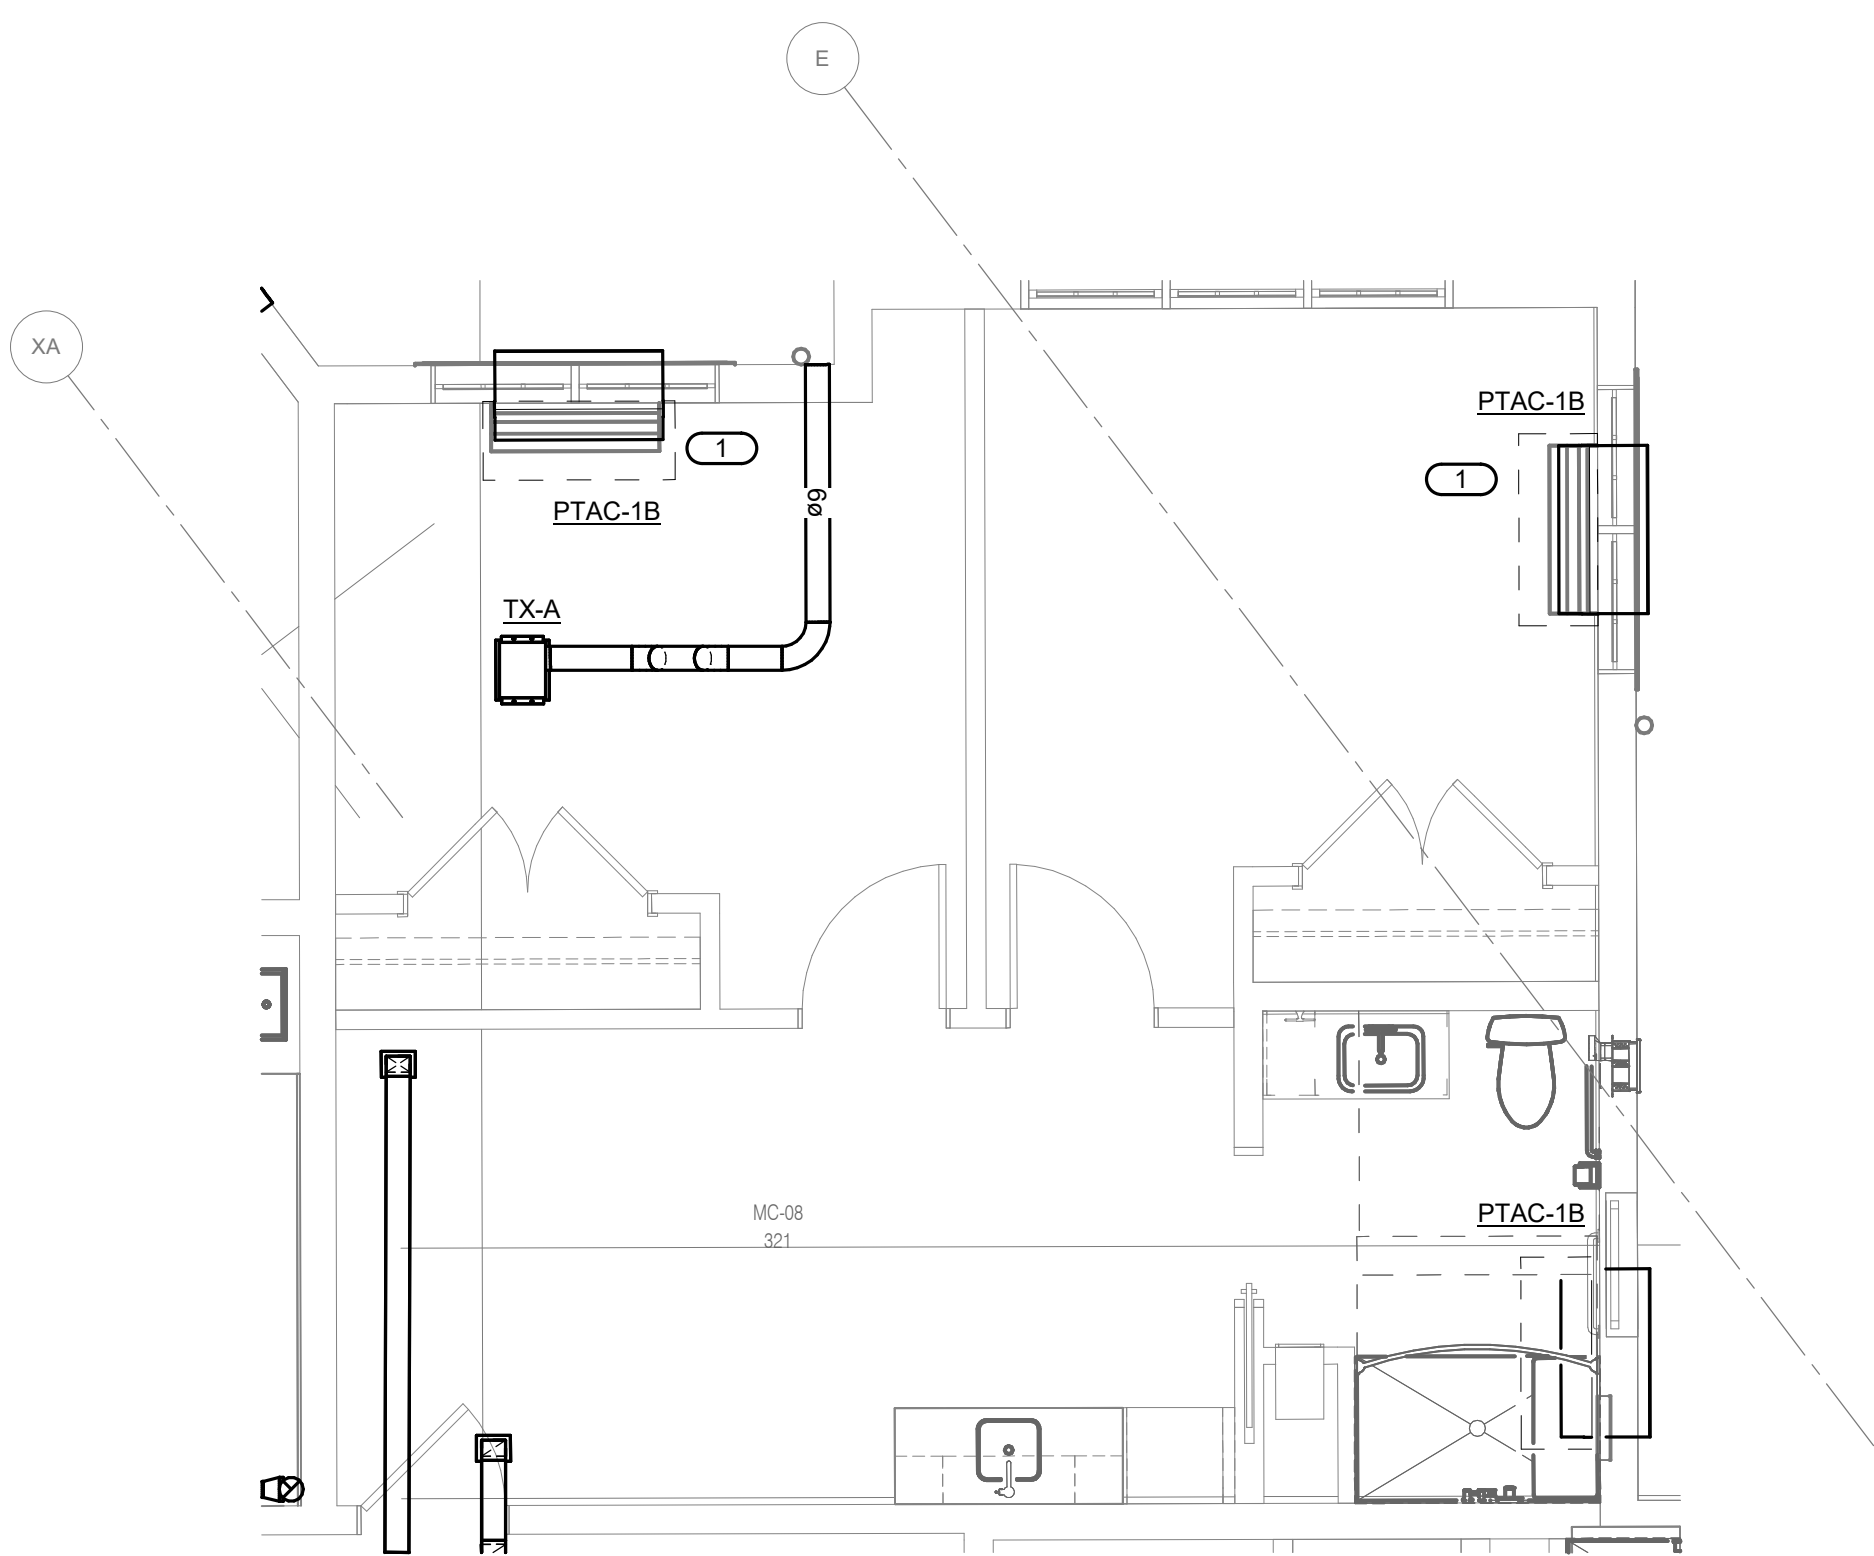

3 MECH. REM SEMI-PRIVATE - MC-08
1/4" = 1'-0"

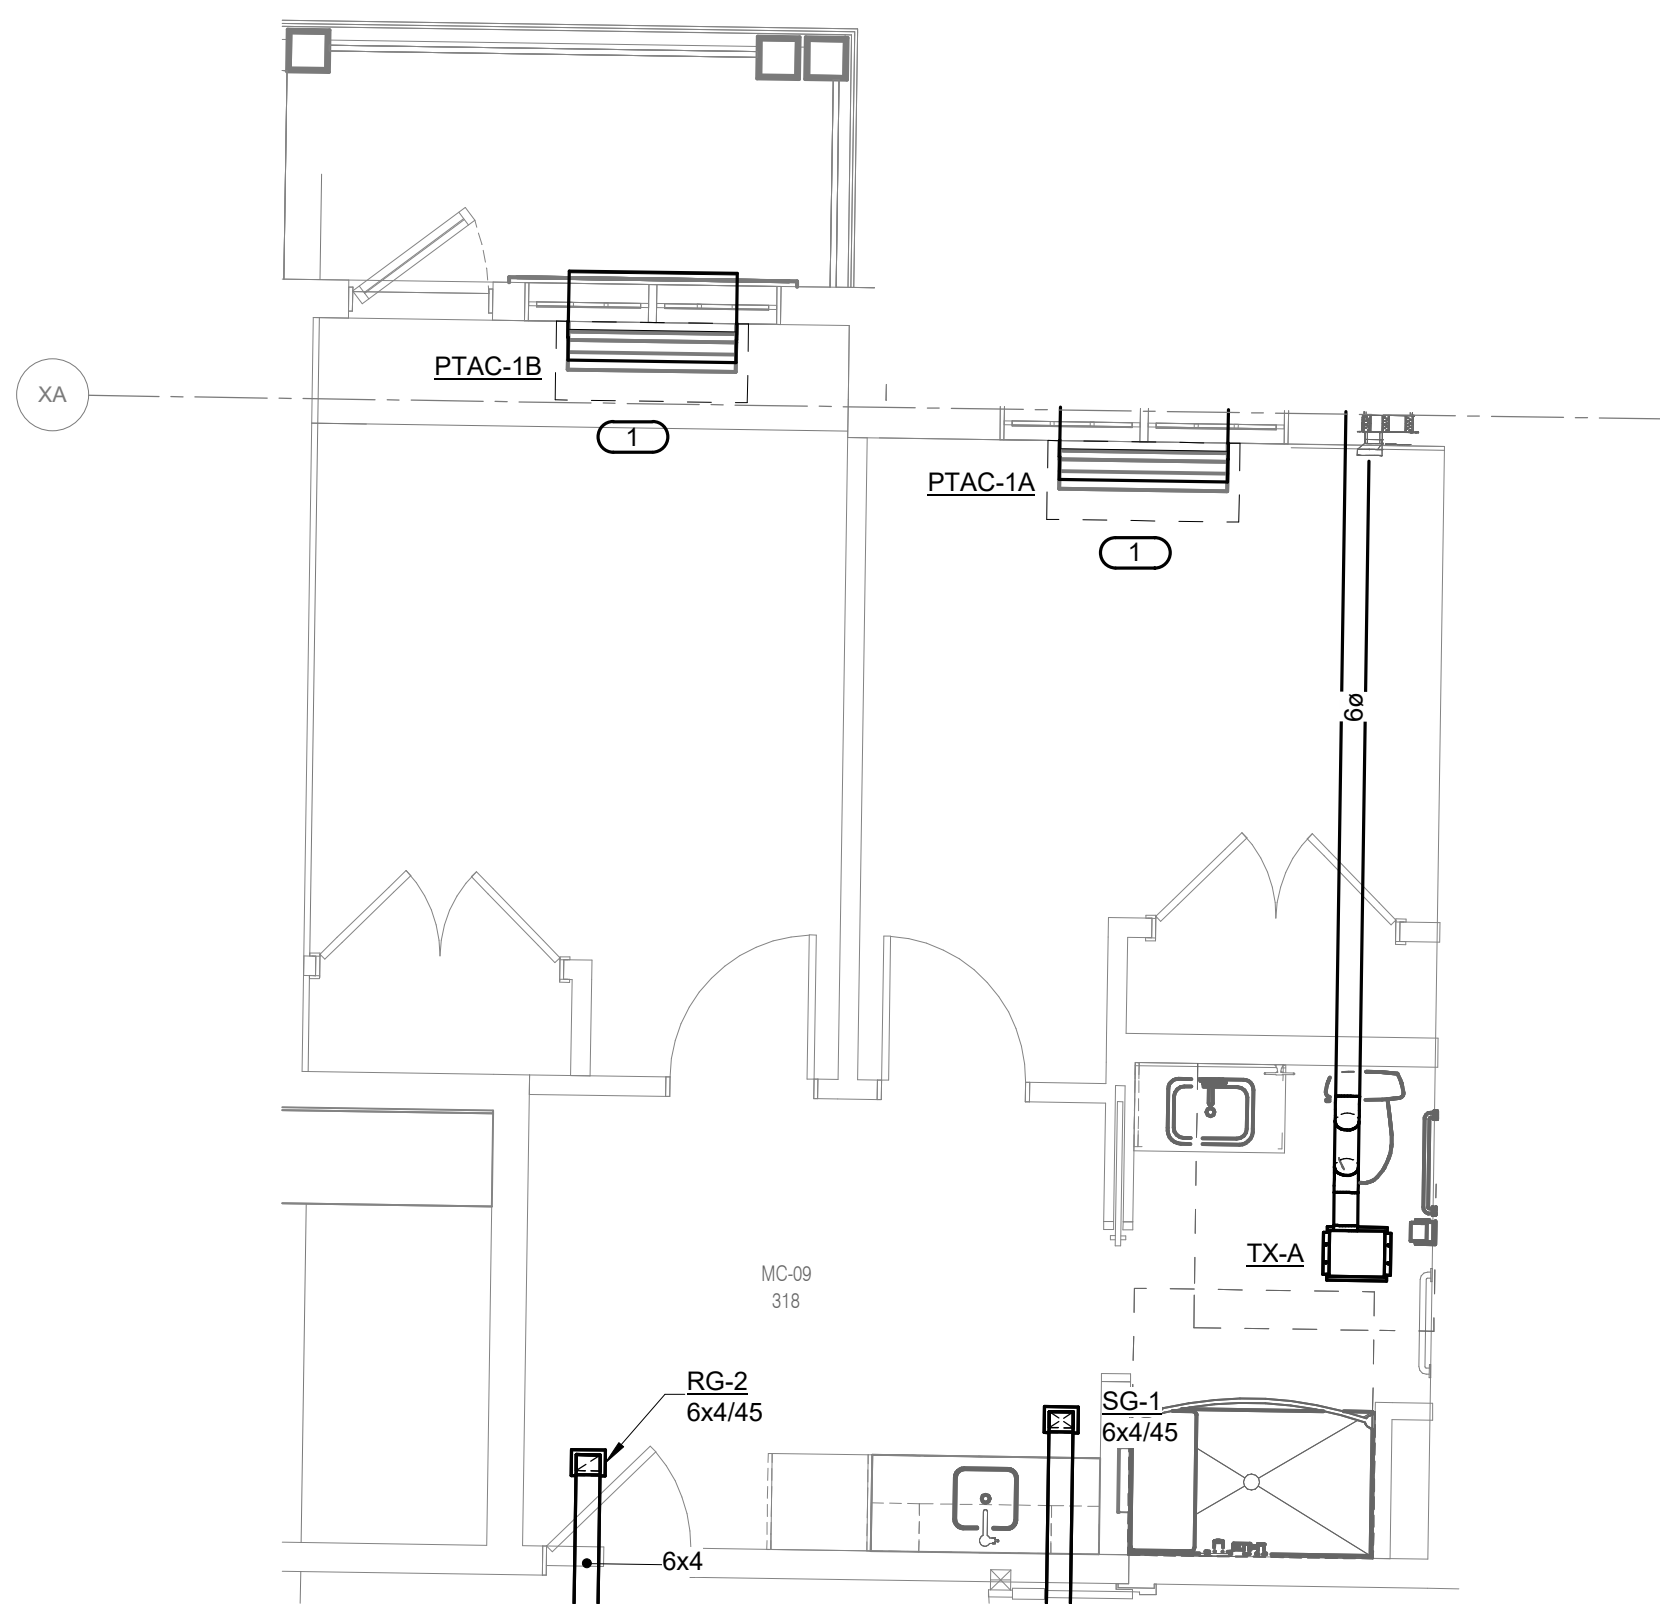

4 MECH. REM SEMI-PRIVATE - MC-09
1/4" = 1'-0"

KEYNOTES:

1. NEW PTAC UNIT MOUNTED ON EXTERIOR WALL. PER MANUFACTURER RECOMMENDATIONS. PROVIDE 3/4" CONDENSATE LINE DOWN THROUGH EXTERIOR WALL. DAYLIGHT CONDENSATE PIPE AND PROVIDE SPLASH BLOCK ON GRADE. IF MULTIPLE PTAC UNITS ARE STACKED VERTICALLY THE CONDENSATE LINES MAY BE COMBINED. PROVIDE 1" CONDENSATE LINE WHERE CONDENSATE IS COMBINED.
2. NEW EXHAUST FAN INSTALLED IN BATHROOM CEILING PER MANUFACTURER RECOMMENDATIONS.
3. ROUTE EXHAUST DUCTWORK TO EXTERIOR WALL AS REQUIRED. PROVIDE X-VENT MODEL. "SSEB-4" AT DUCTWORK TERMINATION POINT. MAINTAIN MINIMUM 3'-0" FROM WINDOW OPENINGS AND 10'-0" FROM ANY OUTDOOR AIR INTAKES.
4. ROUTE EXHAUST DUCTWORK TO EXTERIOR WALL AS REQUIRED. PROVIDE X-VENT MODEL. "DVEB-46-4" FOR BOTH DUCTWORK LINES AT TERMINATION POINT. MAINTAIN MINIMUM 3'-0" FROM WINDOW OPENINGS AND 10'-0" FROM ANY OUTDOOR AIR INTAKES.
5. ROUTE EXHAUST DUCTWORK UP THROUGH ROOF AS REQUIRED.

HKS

ARCHITECT

HKS ARCHITECTS, P.C.
30 WEST 26th STREET, 12th FLOOR
NEW YORK, NY 10010

STRUCTURAL

IMEG
1411 BROADWAY, SUITE 600
NEW YORK, NY 10018

MEP ENGINEER

IMEG
177 CROSWAYS PARK DRIVE
WOODBURY, NY 11797

LV ENGINEER

TASERCO
765 HICKORY FLAT HWY, SUITE 200
WOODSTOCK, GA 30188

LANDSCAPE ARCHITECT

MPFP
120 BROADWAY, 20TH FLOOR
NEW YORK, NY 10271

POOL DESIGNER

COUNSLMAN HUNSAKER & ASSOCIATES, INC.
12851 MANCHESTER ROAD, SUITE 120
ST. LOUIS, MO 63131

FOOD SERVICE & LAUNDRY


CLARK
2551 HORSESHOE RD.
LANCASTER, PA 17601SUNRISESM
SENIOR LIVING
RYE BROOK

DOB BSCAN | DOB STAMP & SIGNATURES

SEAL & SIGNATURE

CON NO.: 111AAA

KEY PLAN

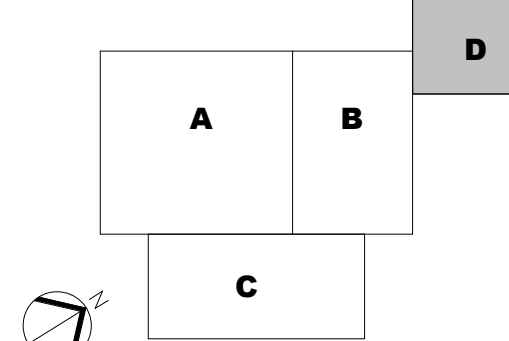

REVISION		
NO	DESCRIPTION	DATE
1	DD Progress Print	08/28/25
2	DESIGN DEVELOPMENT	11/25/25
3	EXTERIOR BUILDING PERMIT	12/23/25
4	100% DESIGN DEVELOPMENT	01/30/26
5	ISSUED FOR PERMIT	06/05/26

HKS PROJECT NUMBER

25004064.00

DATE

07/15/26

ISSUE

ISSUED FOR GMP

SHEET TITLE

UNIT PLANS AL -
MECHANICAL

SHEET NO.

M2110

DOB FILE # DOB PAGE #


IMEG

IMEG RESERVES PROPRIETARY RIGHTS, INCLUDING COPYRIGHTS, TO THIS DRAWING AND THE DATA SHOWN THEREON. NO REPRODUCTION AND/OR DATA ARE THE EXCLUSIVE PROPERTY OF IMEG AND SHALL NOT BE USED OR REPRODUCED FOR ANY OTHER PROJECT WITHOUT THE EXPRESS WRITTEN APPROVAL AND PARTICIPATION OF IMEG. ©2025 IMEG CONSULTANTS CORP.

177 CROSWAYS PARK DRIVE
WOODBURY, NY 11797
P: 516.927.6900

REF. SCALE IN INCHES PROJECT #25004064.00

© HKS, INC.

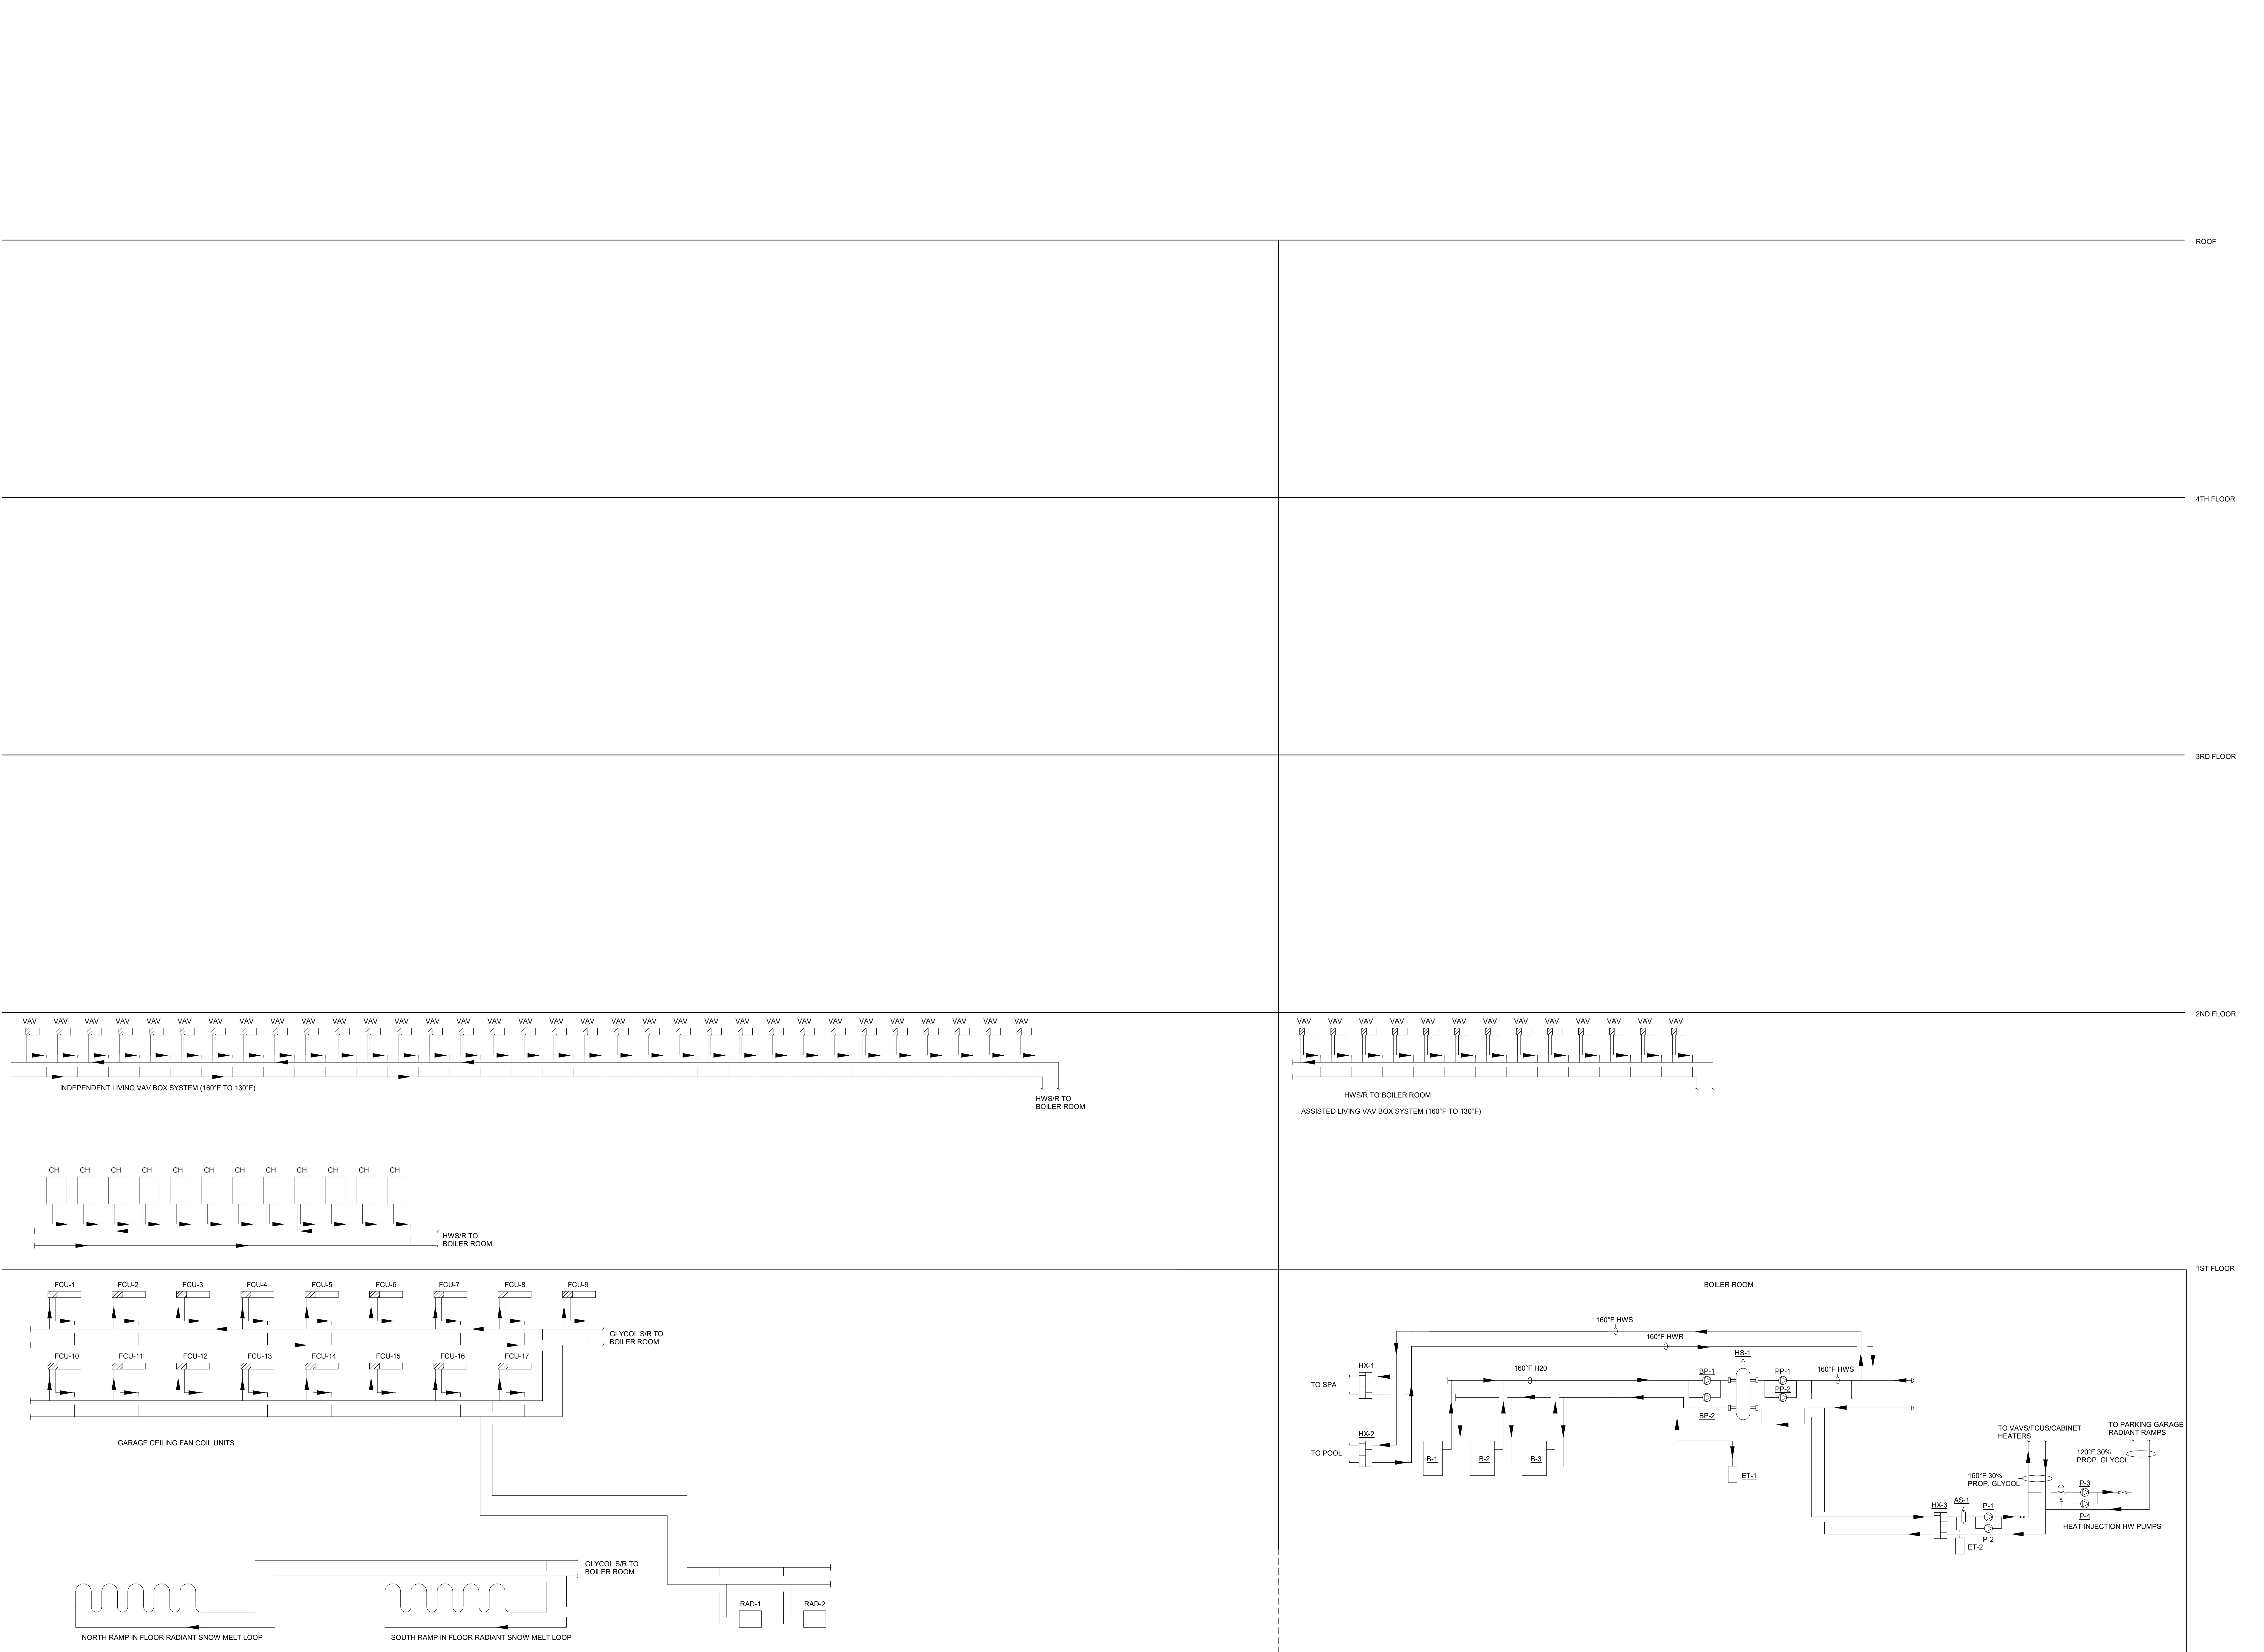

1 HYDRONIC FLOW DIAGRAM

NO SCALE



177 CROSWAYS PARK DRIVE
WOODBURY, NY 11797
P: 516-927-6900

IMEG RESERVES PROPRIETARY RIGHTS, INCLUDING COPYRIGHTS, TO THIS DRAWING AND THE DATA SHOWN THEREON. NO REPRODUCTION AND/OR DATA ARE THE EXCLUSIVE PROPERTY OF IMEG AND SHALL NOT BE USED OR REPRODUCED FOR ANY OTHER PROJECT WITHOUT THE EXPRESS WRITTEN APPROVAL AND PARTICIPATION OF IMEG. ©2016 IMEG CONSULTANTS CORP.

01'0"

02'0"

03'0"

04'0"

05'0"

REF. SCALE IN INCHES

PROJECT #25004064.00

ARCHITECT
HKS ARCHITECTS, P.C.
30 WEST 26th STREET, 12th FLOOR
NEW YORK, NY 10010

STRUCTURAL
IMEG
1411 BROADWAY, SUITE 600
NEW YORK, NY 10018

MEP ENGINEER
IMEG
177 CROSWAYS PARK DRIVE
WOODBURY, NY 11797

LV ENGINEER
TASERCO
7853 HICKORY FLAT HWY, SUITE 200
WOODSTOCK, GA 30188

LANDSCAPE ARCHITECT
MFPF
120 BROADWAY, 20TH FLOOR
NEW YORK, NY 10271

POOL DESIGNER
COUNSLMAN-HUNSAKER & ASSOCIATES, INC.
12851 MANCHESTER ROAD, SUITE 120
ST. LOUIS, MO 63131

FOOD SERVICE & LAUNDRY
CLARK
2551 HORSESHOE RD.
LANCASTER, PA 17601




DOB BSCAN | DOB STAMP & SIGNATURES

SEAL & SIGNATURE

CON NO. 111AAA

KEY PLAN

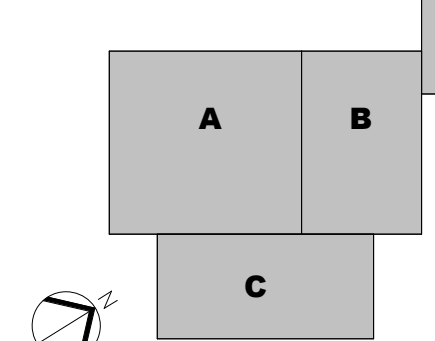


REVISION	
NO.	DESCRIPTION
1	DD Progress Print
2	DESIGN DEVELOPMENT
3	EXTERIOR BUILDING PERMIT
4	100% DESIGN DEVELOPMENT
5	ISSUED FOR PERMIT

HKS PROJECT NUMBER
25004064.00
DATE
07/15/26
ISSUE
ISSUED FOR GMP


SHEET TITLE
**MECHANICAL
DIAGRAMS**

SHEET NO.

TITLE BLOCK VERSION: 2501000
MODEL: A:\0000\Draw\07292\000_Sunrise Brook NY_Senior Living\MEP\25004064-00_LAL.dwg
PRINT DATE: 11/05/2016 12:46:07 PM
TEMPORARY VERSION: 23.0.1

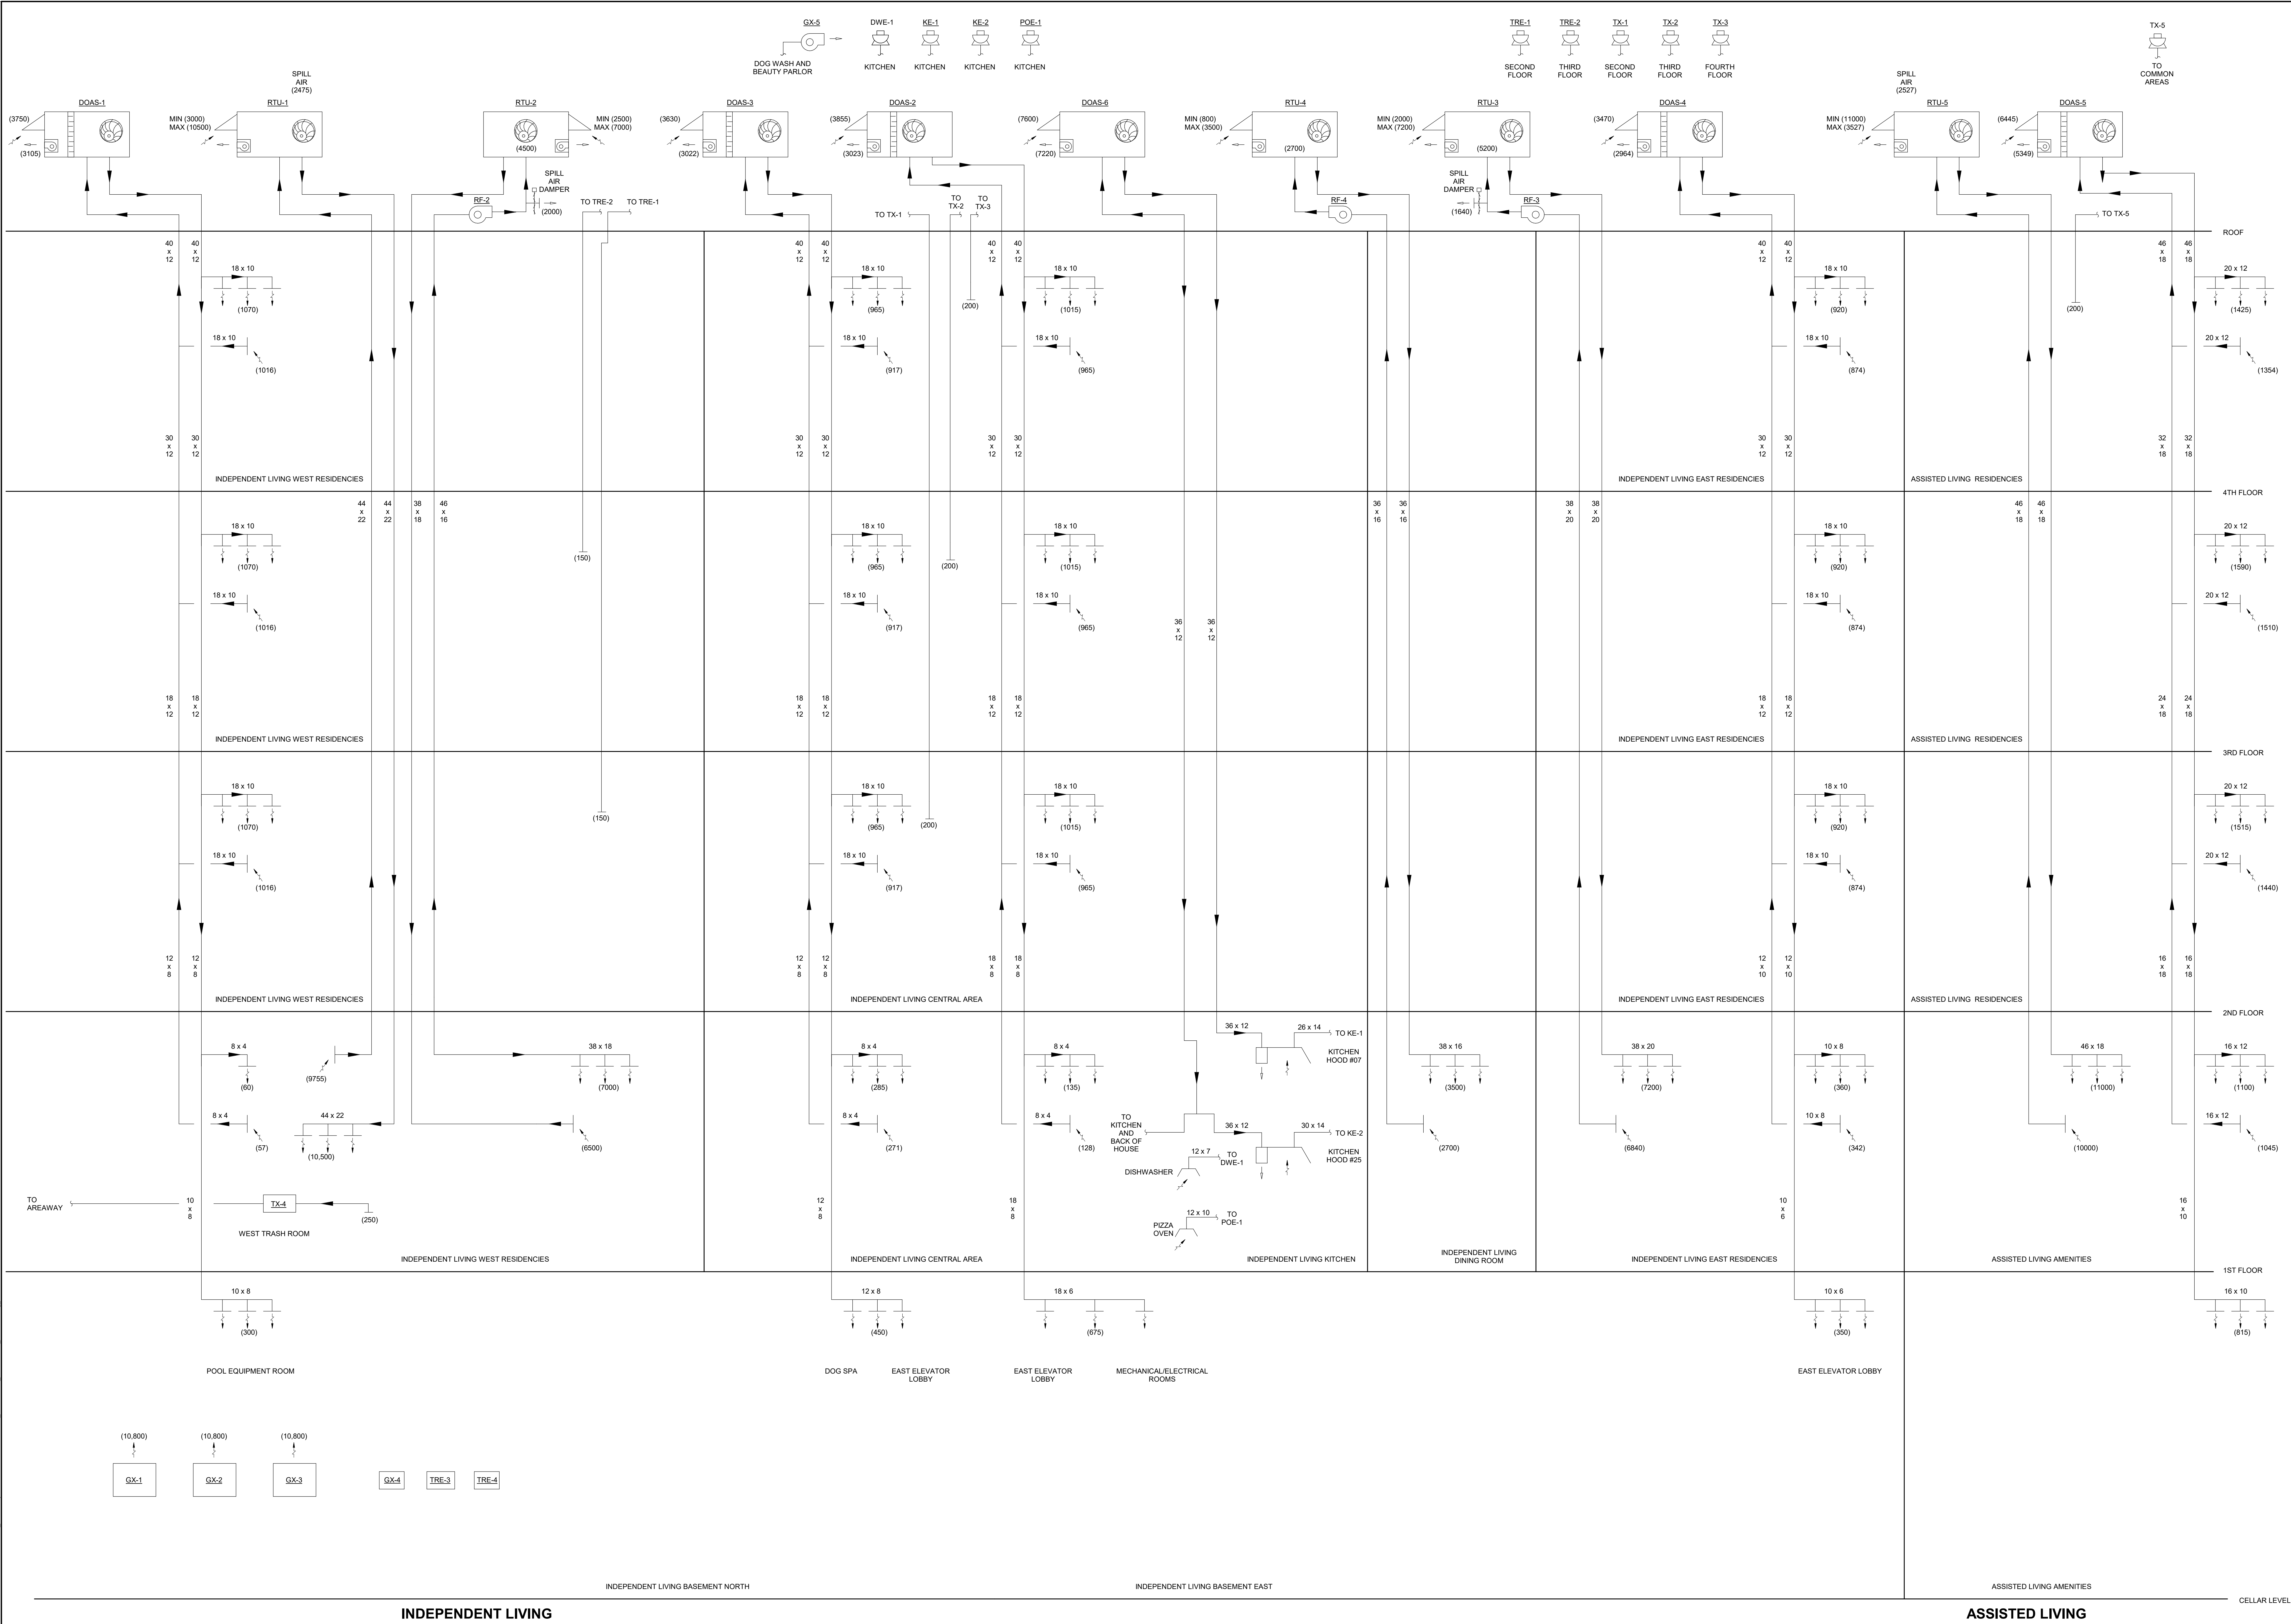

1 AIRFLOW DIAGRAM
NO SCALE

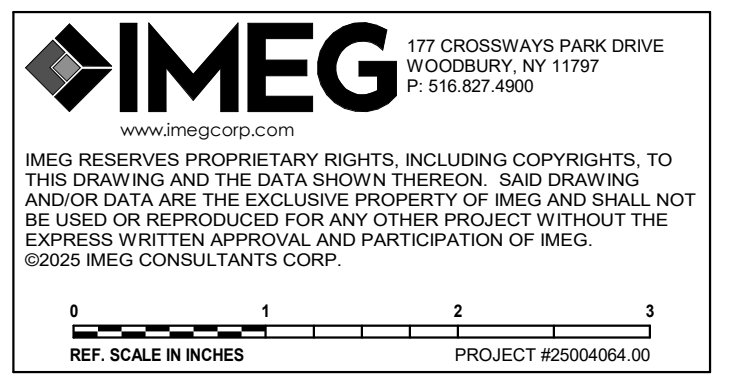

HKS

ARCHITECT
HKS ARCHITECTS, P.C.
30 WEST 26th STREET, 12th FLOOR
NEW YORK, NY 10018

STRUCTURAL
IMEG
1411 BROADWAY, SUITE 600
NEW YORK, NY 10018

MEP ENGINEER
IMEG
177 CROSWAYS PARK DRIVE
WOODBURY, NY 11797

LV ENGINEER
TATEROY
765 HICKORY FLAT HWY, SUITE 200
WOODSTOCK, GA 30188

LANDSCAPE ARCHITECT
MFPF
120 BROADWAY, 20TH FLOOR
NEW YORK, NY 10271

POOL DESIGNER
COUNSLMANHUNSAKER & ASSOCIATES, INC.
12851 MANCHESTER ROAD, SUITE 120
ST. LOUIS, MO 63131

FOOD SERVICE & LAUNDRY
CLARK
2551 HORSESHOE RD.
LANCASTER, PA 17601

PROJECT ADDRESS: 300 King St, Rye Brook, NY 10573

SUNRISESM
SENIOR LIVING
RYE BROOK

DOB SCAN | DOB STAMP & SIGNATURES _____

SEAL & SIGNATURE _____

CON NO.: 111AAA
KEY PLAN:

REVISION	NO.	DESCRIPTION	DATE
1	DD Program Print	08/26/25	
2	DESIGN DEVELOPMENT	11/05/25	
3	EXTERIOR BUILDING PERMIT	12/03/25	
4	100% DESIGN DEVELOPMENT	01/28/26	
5	ISSUED FOR PERMIT	06/26/26	

HKS PROJECT NUMBER
25004064.00

DATE
07/15/26

ISSUE
ISSUED FOR GMP

SHEET TITLE
MECHANICAL AIR FLOW DIAGRAMS

SHEET NO.
M5001

DOB FILE # _____ DOB PAGE # _____



TITLE BLOCK VERSION: 20190301
PROJECT: ALBANY DASH/27292-000 - Sunrise E&M, 2024MEP25-2000404-00 - LAL Building, LLC
PRINT DATE: 11/05/2025 1:46:25 PM - TEMPLATE VERSION: 23.0.1

DEDICATED OUTDOOR AIR UNIT SCHEDULE (DOAS)

REFER TO "DEDICATED OUTDOOR AIR UNIT COMPONENT SCHEDULES" FOR ADDITIONAL INFORMATION

NOTES:
1.

TAG NAME	LOCATION	SERVICE	SUPPLY FAN CFM	SUPPLY FAN E.S.P.	SUPPLY FAN HP	EXHAUST FAN CFM	EXHAUST FAN E.S.P.	EXHAUST FAN HP	SENSIBLE MBH	COOLING COIL TOTAL MBH	COOLING COIL EAT DB	COOLING COIL EAT WB	COOLING COIL LAT DB	COOLING COIL LAT WB	HEAT PUMP TOTAL MBH	HEAT PUMP EAT	HEAT PUMP LAT	ENERGY WHEEL PERFORMANCE DATA				EER	FILTER TYPE	REFRIGERANT TYPE	ELECTRICAL				MAXIMUM DIMENSIONS			WEIGHT LBS	MANUFACTURER	MODEL					
																		RECOVERED CAPACITY		WINTER TOTAL MBH	WINTER SENS. MBH				ENTHALPY RECOVERY RATIO														
																		SUMMER TOTAL MBH	SUMMER SENS. MBH						213.24	154.65	62.9	14.7	MERV-8	R-454B	460				3	46.5	49.6	60	7'-11"
DOAS-1	IL ROOF	NORTHWEST RESIDENCE	3,500	2.25	3.27	0	0.75	1.83	113.1	175.8	80.7	67.8	50.6	50.6	124.5	53	84.6	96.6	53.65	213.24	154.65	62.9	14.7	MERV-8	R-454B	460	3	46.5	49.6	60	7'-11"	5'-8"	15'-3"	4,143	TRANE	HORIZON			
DOAS-2	IL ROOF	NORTHEAST RESIDENCE	3,500	2.25	3.27	0	0.75	1.83	113.1	175.8	80.7	67.8	50.6	50.6	124.5	53	84.6	96.6	53.65	213.24	154.65	62.9	14.7	MERV-8	R-454B	460	3	46.5	49.6	60	7'-11"	5'-8"	15'-3"	4,143	TRANE	HORIZON			
DOAS-3	IL ROOF	SOUTHWEST RESIDENCE	3,500	2.25	3.27	0	0.75	1.83	113.1	175.8	80.7	67.8	50.6	50.6	124.5	53	84.6	96.6	53.65	213.24	154.65	62.9	14.7	MERV-8	R-454B	460	3	46.5	49.6	60	7'-11"	5'-8"	15'-3"	4,143	TRANE	HORIZON			
DOAS-4	IL ROOF	SOUTHEAST RESIDENCE	3,900	2.25	3.86	0	0.75	2.26	123.1	196.3	80.8	67.9	51.4	50.8	136.3	52.7	82.4	105.97	59.39	234.75	171.3	61.9	14.1	MERV-8	R-454B	460	3	46.5	52.6	60	7'-11"	5'-8"	15'-3"	4,392	TRANE	HORIZON			
DOAS-5	AL ROOF	AL RESIDENCE	6,500	2.25	7.92	0	0.75	3.84	220.3	329	80.7	67.8	49.1	49.1	239.6	53	83.7	177.71	99.24	393.13	286.17	62.6	12.3	MERV-8	R-454B	460	3	81.9	88.7	110	7'-11"	5'-8"	15'-3"	5,536	TRANE	HORIZON			
DOAS-6	IL ROOF	SOUTHEAST RESIDENCE	3,500	2.25	3.27	0	0.75	1.83	113.1	175.8	80.7	67.8	50.6	50.6	124.5	53	84.6	96.6	53.65	213.24	154.65	62.9	14.7	MERV-8	R-454B	460	3	46.5	49.6	60	7'-11"	5'-8"	15'-3"	4,143	TRANE	HORIZON			
DOAS-7	IL ROOF	SOUTHEAST RESIDENCE	3,500	2.25	3.27	0	0.75	1.83	113.1	175.8	80.7	67.8	50.6	50.6	124.5	53	84.6	96.6	53.65	213.24	154.65	62.9	14.7	MERV-8	R-454B	460	3	46.5	49.6	60	7'-11"	5'-8"	15'-3"	4,143	TRANE	HORIZON			

PACKAGED ROOFTOP UNIT SCHEDULE (RTU)

REFER TO "PACKAGED ROOFTOP UNIT COMPONENT SCHEDULES" FOR ADDITIONAL INFORMATION

NOTES:
1. OPERATING WEIGHT INCLUDES UNIT, CURB, ACCESSORIES AND UNIT MOUNTED POWER EXHAUST, DUCT MOUNTED ACCESSORIES AND EQUIPMENT ARE NOT INCLUDED. CONTRACTOR IS RESPONSIBLE FOR ALL CHANGES REQUIRED DUE TO ROOFTOP UNIT HEAVIER THAN THE BASIS OF DESIGN AT NO ADDITIONAL COST.

TAG NAME	LOCATION	SERVICE	SUPPLY FAN			EXHAUST FAN			COOLING COIL				NATURAL GAS HEATING				EER	REFRIGERAN T TYPE	TONS	ELECTRICAL				DIMENSIONS			WEIGHT	MANUFACTURER	MODEL			
			CFM	ESP	HP	CFM	ESP	HP	TOTAL MBH	SENSIBLE MBH	EAT		LAT		HEATING INPUT (MBH)	HEATING OUTPUT MBH				HEATING EAT COIL	HEATING COIL LAT	VOLTS	P H	HZ	MCA	MOCP	WIDTH			HEIGHT	DEPTH	OPERATING
											DB	WB	DB	WB																		
RTU-1	IL ROOF	WEST WING	10,500	2.5"	15	7500	1"	1	359.78	277.2	75	62.5	50.4	50.3	600	486	75	118.1	10.7	R-454B	30	460	3	60	90	100	7'-6"	5'-10"	17'-4"	5,417	TRANE	VOYAGER
RTU-2	IL ROOF	CENTER WING	7,000	1.25"	2.9	4500	0.5"	2	249.37	146.38	75	0	56.1	56.1	400	324	75	108.6	9.3	R-454B	20	460	3	60	55	70	7'-3"	5'-6"	10'-3"	2,699	TRANE	PRECEDENT
RTU-3	IL ROOF	EAST WING	7,200	1.75"	2.9	5200	0.5"	2	251.85	148.64	75	0	56.3	56.5	400	324	75	116.1	9.3	R-454B	20	460	3	60	55	70	7'-3"	5'-6"	10'-3"	2,699	TRANE	PRECEDENT
RTU-4	IL ROOF	KITCHEN	3,500	1.4"	4.1	2700	0.5"	1	122.56	72.54	75	0	55.5	55.5	240	194.4	75	125.8	10.8	R-454B	10	460	3	60	35	45	5'-3"	4'-4"	8'-3"	1,803	TRANE	PRECEDENT
RTU-5	AL ROOF	ASSISTED LIVING	11,000	2.5"	51	10000	1"	1	390	297.58	75	62.6	49.9	49.8	600	864	75	116	10.3	R-454B	35	460	3	60	94	110	7'-6"	5'-10"	17'-4"	5,489	TRANE	VOYAGER

PACKAGED TERMINAL AIR CONDITIONER SCHEDULE (PTAC)

NOTES:
1.

AMBIENT TEMP °F			FAN CFM		OA CFM		REFRIGERATION			EFFICIENCY		COOLING		HEATING (HEAT PUMP W AUX. ELECTRIC HEAT)										ELECTRICAL		CONTROL		MAXIMUM DIMENSIONS			WEIGHT LBS			
TAG NAME	SUMMER DRY BULB	WINTER DRY BULB	SERVICE	TYPE	DESIGN	DESIGN	TYPE	CHARGE LBS	CLG EER	HTG COP	BTUH	HEAT PUMP BTUH (SE/F)	NO. OF STAGES	TOTAL KW (QTY * KW)		VOLTS PH	FLA	MCA	MOPC	BY (A)	TYPE (B)	BY (A)	TYPE (C)	SCCR	EM PWR	TYPE (H)	WIDTH	HEIGHT	DEPTH	OPERATING	MANUFACTURER	IR	MODEL	NOTES
														ELECTRIC ELEMENT	DISCONNECT																			
PTAC-1A	95	27	ASSISTED LIVING	WALL-MOUNTED	330	0	R32	0	12.8	3.7	7000	6100	1	1	1.3	208	1	6.2	8.5	15	MFR	MFR	0	No	3'-6"	1'-7"	1'-10"	106	AMANA	PTH073J				
PTAC-1B	95	27	ASSISTED LIVING	WALL-MOUNTED	330	0	R32	0	12.8	3.7	7000	6100	1	1	2.1	208	1	10.1	14.1	15	MFR	MFR	0	No	3'-6"	1'-7"	1'-10"	106	AMANA	PTH073J				
PTAC-1C	95	27	ASSISTED LIVING	WALL-MOUNTED	330	0	R32	0	12.8	3.7	7000	6100	1	1	3	208	1	14.1	19.5	20	MFR	MFR	0	No	3'-6"	1'-7"	1'-10"	106	AMANA	PTH073J				
PTAC-2B	95	27	ASSISTED LIVING	WALL-MOUNTED	330	0	R32	0	12.5	3.6	9000	8000	1	1	2.1	208	1	10.1	14.1	15	MFR	MFR	0	No	3'-6"	1'-7"	1'-10"	102	AMANA	PTH093J				
PTAC-2C	95	27	ASSISTED LIVING	WALL-MOUNTED	330	0	R32	0	12.5	3.6	9000	8000	1	1	3	208	1	14	19.5	20	MFR	MFR	0	No	3'-6"	1'-7"	1'-10"	102	AMANA	PTH093J				
PTAC-2D	95	27	ASSISTED LIVING	WALL-MOUNTED	330	0	R32	0	12.5	3.6	9000	8000	1	1	4.1	208	1	20	27.6	30	MFR	MFR	0	No	3'-6"	1'-7"	1'-10"	102	AMANA	PTH093J				
PTAC-3B	95	27	ASSISTED LIVING	WALL-MOUNTED	330	0	R32	0	11.5	3.3	11600	10800	1	1	2.1	208	1	10.1	14.1	15	MFR	MFR	0	No	3'-6"	1'-7"	1'-10"	108	AMANA	PTH123J				
PTAC-3C	95	27	ASSISTED LIVING	WALL-MOUNTED	330	0	R32	0	11.5	3.3	11600	10800	1	1	3	208	1	14.1	19.5	20	MFR	MFR	0	No	3'-6"	1'-7"	1'-10"	108	AMANA	PTH123J				
PTAC-3D	95	27	ASSISTED LIVING	WALL-MOUNTED	330	0	R32	0	11.5	3.3	11600	10800	1	1	4.1	208	1	20	27.6	30	MFR	MFR	0	No	3'-6"	1'-7"	1'-10"	108	AMANA	PTH123J				
PTAC-4D	95	27	ASSISTED LIVING	WALL-MOUNTED	330	0	R32	0	10.6	3.1	14000	14000	1	1	4.1	208	1	20	27.6	30	MFR	MFR	0	No	3'-6"	1'-7"	1'-10"	113	AMANA	PTH153J				

FAN COIL UNIT SCHEDULE - HYDRONIC (FCU)

NOTES:
1.

TAG NAME	QUANTITY	SERVICE	TYPE	FAN		HEATING COIL										ELECTRICAL		CONTROL		MAXIMUM DIMENSIONS			WEIGHT LBS	MANUFACTURER	MODEL	NOTES							
				CFM DESIGN	EXT S.P. IN. WC	MOTOR MHP [E]	MBH	EAT DB °F	LAT DB °F	GPM DESIGN	W.P.D. FT. HD.	EWT °F	LWT °F	VOLTS	PH	TYPE [H]	DIAGRAM	WIDTH	HEIGHT	DEPTH	DRY												
FCU-A	20	BASEMENT HEATING	HORIZONTAL	0	0	0	0	0	0	0	0	0	0	0	0	0	1			0"	0"	0"	0										

VAV SCHEDULE - HYDRONIC REHEAT

TAG	AHU	ROOM	MODEL	SIZE		CFM		STATIC PRESSURE			NC LEVELS		HOT WATER HEATING COIL										UNIT INFO	
				UNIT	OUTLET	MAX	MIN	INLET	DOWN	MIN	RAD	DIS	CFM	MBH	EAT	EWT	LAT	APU	GPM	LWT	WPI	ROWS	FPI	HAND
VAV-01			DESV	12	16x15	1200	825	1	0.25	0.24	20	24	825	26.9	60	160	90	0.23	1.5	122.5	0.24	2-RH	10	RH
VAV-02			DESV	14	20x17.5	1450	1350	1	0.25	0.19	20	19	1350	44	60	160	90	0.17	2.4	122.6	0.3	2-RH	10	RH
VAV-03			DESV	14	20x17.5	2250	1150	1	0.25	0.39	23	22	1150	37.5	60	160	90	0.35	1.9	120	0.22	2-RH	10	RH
VAV-04			DESV	08	12x10	700	375	1	0.25	0.32	22	28	375	12.2	60	160	90	0.3	0.8	127.1	0.15	2-RH	10	RH
VAV-05			DESV	08	12x10	400	400	1	0.25	0.13	17	25	400	13	60	160	90	0.12	0.8	127.8	0.17	2-RH	10	RH
VAV-06			DESV	08	12x10	400	400	1	0.25	0.13	17	25	400	13	60	160	90	0.12	0.8	127.8	0.17	2-RH	10	RH
VAV-07			DESV	10	14x12.5	700	250	1	0.25	0.09	23	27	250	8.1	60	160	90	0.08	1	143.9	0.15	1-RH	10	RH
VAV-08			DESV	04	12x8	200	100	1	0.25	0.11	27	34	100	3.3	60	160	90.7	0.03	0.4	140.8	0.1	1-RH	10	RH
VAV-09			DESV	08	12x10	350	150	1	0.25	0.06	17	25	150	4.9	60	160	90	0.05	0.5	137.8	0.19	1-RH	10	RH
VAV-10			DESV	06	12x8	425	250	1	0.25	0.36	23	24	250	8.9	60	160	92.8	0.21	0.7	134.3	0.1	2-RH	10	RH
VAV-11			DESV	10	14x12.5	550	500	1	0.25	0.12	20	24	500	16.8	60	160	90.9	0.11	1.1	127.8	0.14	2-RH	10	RH
VAV-12			DESV	14	20x17.5	1300	1300	1	0.25	0.15	18	19	1300	42.3	60	160	90	0.14	2.3	122.3	0.28	2-RH	10	RH
VAV-13			DESV	10	14x12.5	600	600	1	0.25	0.14	20	24	600	19.5	60	160	90	0.13	1.3	128.7	0.18	2-RH	10	RH
VAV-14			DESV	10	14x12.5	600	600	1	0.25	0.14	20	24	600	19.5	60	160	90	0.13	1.3	128.7	0.18	2-RH	10	RH
VAV-15			DESV	06	12x8	200	200	1	0.25	0.09	14	22	200	8.1	60	160	97.4	0.06	0.7	136.6	0.1	2-RH	10	RH
VAV-16			DESV	06	12x8	300	250	1	0.25	0.19	18	22	250	8.9	60	160	92.8	0.12	0.7	134.3	0.1	2-RH	10	RH
VAV-17			DESV	08	12x10	450	450	1	0.25	0.16	18	25	450	14.7	60	160	90	0.15	1	129.4	0.21	2-RH	10	RH
VAV-18			DESV	08	12x10	500	500	1	0.25	0.19	19	27	500	16.3	60	160	90	0.18	1.1	130.8	0.25	2-RH	10	RH
VAV-19			DESV	06	12x8	200	50	1	0.25	0.06	14	22	50	2.4	60	160	103.6	0.03	0.4	146.4	0.1	1-RH	10	RH
VAV-20			DESV	08	12x10	350	150	1	0.25	0.06	17	25	150	4.9	60	160	90	0.05	0.5	137.8	0.19	1-RH	10	RH
VAV-21			DESV	08	12x10	300	150	1	0.25	0.05	14	24	150	4.9	60	160	90	0.04	0.5	137.8	0.19	1-RH	10	RH
VAV-22			DESV	12	16x15	900	250	1	0.25	0.08	19	23	250	8.4	60	160	90.8	0.07	0.7	135.9	0.11	1-RH	10	RH
VAV-23			DESV	06	12x8	300	100	1	0.25	0.13	20	22	100	3.3	60	160	90.7	0.06	0.4	140.8	0.1	1-RH	10	RH
VAV-24			DESV	10	14x12.5	550	200	1	0.25	0.07	22	24	200	6.6	60	160	90.3	0.06	0.7	141	0.09	1-RH	10	RH
VAV-25			DESV	14	20x17.5	3000	1100	1	0.25	0.64	25	23	1100	35.8	60	160	90	0.56	1.8	119.3	0.2	2-RH	10	RH
VAV-26			DESV	06	12x8	400	200	1	0.25	0.32	22	24	200	8.1	60	160	97.4	0.19	0.7	136.6	0.1	2-RH	10	RH
VAV-27			DESV	14	20x17.5	1850	425	1	0.25	0.16	22	22	425	13.8	60	160	90	0.13	1.3	137.6	0.12	1-RH	10	RH
VAV-28			DESV	10	14x12.5	800	525	1	0.25	0.21	22	24	525	17.1	60	160	90	0.2	1.1	127.2	0.14	2-RH	10	RH
VAV-29			DESV	16	24x18	1800	600	1	0.25	0.1	17	18	600	19.5	60	160	90	0.19	1.39	139	0.23	1-RH	10	RH
VAV-30			DESV	06	12x8	350	200	1	0.25	0.26	21	23	200	8.1	60	160	97.4	0.16	0.7	136.6	0.1	2-RH	10	RH
VAV-31			DESV	14	20x17.5	1200	400	1	0.25	0.07	19	19	400	13	60	160	90	0.06	1.1	136.6	0.1	1-RH	10	RH
VAV-32			DESV	06	12x8	150	50	1	0.25	0.04	11	18	50	2.4	60	160	103.6	0.02	0.4	146.4	0.1	1-RH	10	RH
VAV-33			DESV	16	24x18	2500	1000	1	0.25	0.33	18	20	1000	36.3	60	160	93.5	0.31	2.1	125.1	0.1	2-RH	10	RH
VAV-34			DESV	14	20x17.5	1200	450	1	0.25	0.07	19	19	450	14.7	60	160	90	0.06	1.4	138.7	0.14	1-RH	10	RH
VAV-35			DESV	06	12x8	200	200	1	0.25	0.09	14	22	200	8.1	60	160	97.4	0.06	0.7	136.6	0.1	2-RH	10	RH
VAV-36			DESV	08	12x10	350	150	1	0.25	0.06	17	25	150	4.9	60	160	90	0.05	0.5	137.8	0.19	1-RH	10	RH
VAV-37			DESV	08	12x10	250	150	1	0.25	0.04	13	27	150	4.9	60	160	90	0.03	0.5	137.8	0.19	1-RH	10	RH
VAV-38			DESV	08	12x10	450	300	1	0.25	0.16	18	25	300	10.9	60	160	93.4	0.15	0.7	128.6	0.14	2-RH	10	RH
VAV-39			DESV	06	12x8	400	250	1	0.25	0.32	22	24	250	8.9	60	160	92.8	0.19	0.7	134.3	0.1	2-RH	10	RH
VAV-40			DESV	06	12x8	200	100	1	0.25	0.06	14	22	100	3.3	60	160	90.7	0.03	0.4	140.8	0.1	1-RH	10	RH
VAV-41			DESV	08	12x10	400	150	1	0.25	0.07	18	25	150	4.9	60	160	90	0.06	0.5	137.8	0.19	1-RH	10	RH
VAV-42			DESV	12	16x15	600	200	1	0.25	0.05	16	23	200	7.6	60	160	94.9	0.04	0.7	138.2	0.11	1-RH	10	RH
VAV-43			DESV	14	20x17.5	1000	400	1	0.25	0.06	18	18	400	13	60	160	90	0.05	1.1	136.6	0.1	1-RH	10	RH
VAV-44			DESV	16	24x18	1100	500	1	0.25	0.05	12	11	500	16.3	60	160	90	0.04	1.3	134.7	0.14	1-RH	10	RH
VAV-45			DESV	08	12x10	450	350	1	0.25	0.16	18	25	350	11.5	60	160	90.3	0.15	0.7	128.8	0.14	2-RH	10	RH
VAV-46			DESV	06	12x8	400	200	1	0.25	0.32	22	24	200	8.1	60	160	97.4	0.19	0.7	136.6	0.1	2-RH	10	RH
VAV-47			DESV	06	12x8	450	300	1	0.25	0.4	23	24	300	9.8	60	160	90	0.24	0.7	133.2	0.11	2-RH	10	RH

MINI-SPLIT SYSTEM - INDOOR UNIT (HEAT PUMP HEATING)

NOTES:
1. INDOOR UNITS SELECTED FOR SPACE PEAK LOADS.
2. PROVIDE 30% FILTERS FOR EACH UNIT. FILTER MAY BE INTEGRAL OR SUITABLE FOR FIELD INSTALLATION IN FABRICATED FILTER ANGLES. FILTER ANGLES PROVIDED BY U.M.C.
3. UNIT SHALL BE PROVIDED WITH CONDENSATE PUMP FOR FINAL AIR BALANCING UP OR DOWN THROUGH FIELD ADJUSTMENT.
4. INDOOR UNIT CFM SELECTED AT HIGH CFM. INDOOR UNIT SHALL HAVE CAPABILITY TO ADJUST CFM FOR FINAL AIR BALANCING UP OR DOWN THROUGH FIELD ADJUSTMENT.
5. DUCTED CONCEALED UNITS SHALL BE PROVIDED WITH SUPPLY AND RETURN DUCT FLANGES.
6. UNIT SHALL BE PROVIDED WITH INTEGRAL LIFT PUMP FOR CONDENSATE REMOVAL. IF NOT PROVIDED INTEGRAL WITH UNIT, CONTRACTOR SHALL PROVIDE SEPARATE CONDENSATE PUMP. CONDENSATE PUMP SHALL BE POWERED BY UNIT. IF NOT, MECHANICAL CONTRACTOR IS RESPONSIBLE TO PROVIDE POWER FOR CONDENSATE PUMP.

TAG NAME	SERVICE	ASSOC. OUTDOOR UNIT	CFM		REFRIGERATION		COOLING		HEATING		COND. PUMP		ELECTRICAL DISCONNECT		MAXIMUM DIMENSIONS		WEIGHT LBS		MANUFACTURER	MODEL	NOTES
			DESIGN	EXT S.P. IN. WC	TYPE	CHARGE LBS	TOTAL MBH	TOTAL MBH	REQ'D	VOLTS	PH	MCA	MOC	BY [A]	TYPE [B]	HEIGHT	WIDTH	DEPTH			
AC-1	<varies>	<varies>	<varies>	<varies>	<varies>	<varies>	<varies>	<varies>	<varies>	208	<varies>	<varies>	<varies>	<varies>	<varies>	<varies>	<varies>	<varies>	<varies>	<varies>	<varies>
AC-2	<varies>	<varies>	<varies>	<varies>	<varies>	<varies>	<varies>	<varies>	<varies>	208	<varies>	<varies>	<varies>	<varies>	<varies>	<varies>	<varies>	<varies>	<varies>	<varies>	<varies>
AC-3	SEE DWGS.	HP-3	1,090	0.8	R-32	7.5	30	34	Yes	208	1	3.1	15	EC	F	MFR	10,000	Yes	10"	4'-8"	2'-8"
AC-4	SEE DWGS.	HP-4	1,130	0.8	R-32	7.5	36	40	Yes	208	1	3.1	15	EC	F	MFR	10,000	Yes	10"	4'-8"	2'-8"
AC-5	SEE DWGS.	HP-5	1,370	0.8	R-32	7.5	40.5	47	Yes	208	1	3.6	15	EC	F	MFR	10,000	Yes	10"	4'-8"	2'-8"

MINI-SPLIT SYSTEM - OUTDOOR UNIT (HEAT PUMP)

NOTES:
1. UNITS SHALL BE SELECTED FOR DESIGN COOLING LOAD.
2. COORDINATE ELECTRICAL CONNECTIONS WITH MANUFACTURER UNIT IS SUPPLIED AS MULTIPLE MODULES. EACH MODULE REQUIRES A SEPARATE ELECTRICAL CONNECTION AND DISCONNECT.
3. DESIGN COOLING CAPACITY SHALL BE RATED AT INDOOR TEMP = 74°F DB/61°F WB, OUTDOOR TEMP = 89°F DB. EFFECTS OF ESTIMATED REFRIGERANT LINE LENGTH SHALL BE INCLUDED IN COMPUTING DESIGN CAPACITY.
4. DESIGN HEATING CAPACITY SHALL BE RATED AT INDOOR TEMP = 70°F DB, OUTDOOR TEMP = 14°F DB. EFFECTS OF ESTIMATED REFRIGERANT LINE LENGTHS AND DEPOSITING SHALL BE INCLUDED IN COMPUTING DESIGN CAPACITY.

TAG NAME	AMBIENT TEMP °F		NO. OF INDOOR UNITS	REFRIGERATION		COOLING		HEATING		ELECTRICAL (SAME EACH MODULE)				ELECTRICAL MODULE 1		MAXIMUM DIMENSIONS		WEIGHT LBS		MANUFACTURER	MODEL	NOTES		
	COOLING RANGE	HEATING RANGE		SERVICE	CHARGE	MBH (NOTE 3)	MBH (NOTE 4)	VOLTS	PH	BY [A]	TYPE [B]	BY [A]	EM	PWR	MACA	MCCP	SCCR	WIDTH	HEIGHT				DEPTH	OPERATING
HP-1	95	47	INDEPENDENT LIVING UNITS	1	R-32	7.5	18	20	208	1	MFR	F	MFR	Yes	19.8	20	10,000	3'-7 5/16"	2'-10 1/4"	1'-6 1/8"	234	Daikin	RZ418AAVJU	
HP-2	95	47	INDEPENDENT LIVING UNITS	1	R-32	7.5	24	27	208	1	MFR	F	MFR	Yes	19.8	20	10,000	3'-7 5/16"	2'-10 1/4"	1'-6 1/8"	234	Daikin	RZ424AAVJU	
HP-3	95	47	INDEPENDENT LIVING UNITS	1	R-32	7.5	36	40	208	1	MFR	F	MFR	Yes	34.6	35	10,000	3'-7 5/16"	2'-10 1/4"	1'-6 1/8"	234	Daikin	RZ430AAVJU	
HP-4	95	47	INDEPENDENT LIVING UNITS	1	R-32	7.5	36	40	208	1	MFR	F	MFR	Yes	34.6	35	10,000	3'-7 5/16"	2'-10 1/4"	1'-6 1/8"	234	Daikin	RZ430AAVJU	
HP-5	95	47	INDEPENDENT LIVING UNITS	1	R-32	7.5	48	54	208	1	MFR	F	MFR	Yes	34.6	35	10,000	3'-7 5/16"	2'-10 1/4"	1'-6 1/8"	234	Daikin	RZ448AAVJU	

HEAT EXCHANGER SCHEDULE

NOTES:

1.

TAG NAME	LOCATION	BTUH	SERVICE	FLUID TYPE	HOT SIDE				COLD SIDE				PLATES				CURB / PAD		MAXIMUM DIMENSIONS				WEIGHT LBS		MANUFACTURER	MODEL	
					DESIGN	GPM	W.P.D. FT. HD.	EWT °F	LWT °F	DESIGN	GPM	W.P.D. FT. HD.	EWT °F	LWT °F	APPROACH TEMP °F	QTY	WIDTH	HEIGHT	TYPE / BY [G]	HEIGHT	WIDTH	HEIGHT	DEPTH	DRY			OPERATING
HX-1	AL BASEMENT	500,000	POOL		0	0	103	83	0	0	0	0	2	0	0'-0"	0"			0"	0"	0"	0	0	0			
HX-2	AL BASEMENT	245,000	SPA		0	0	124	104	0	0	0	0	2	0	0'-0"	0"			0"	0"	0"	0	0	0			
HX-3	AL BASEMENT	826,000	RAMP RADIANT	30% PROP. GL.Y.	0	0	120	90	0	0	0	0	2	0	0'-0"	0"			0"	0"	0"	0	0	0			

AIR TERMINAL SCHEDULE (EG, RG, SD, etc.)

NOTES:
1. REFER TO DRAWINGS FOR NECK SIZE. ALL BRANCH OUTWORK TO AIR TERMINALS SHALL BE NECK SIZE UNLESS NOTED OTHERWISE.
2. REFER TO DRAWINGS FOR FACE SIZES NOTED AS <varies>.
3. CONTRACTOR SHALL DETERMINE PROPER BORDER TYPE TO MATCH CEILING CONSTRUCTION.
4. DIFFUSERS WITH MULTIPLE SLOTS SHALL HAVE THE INNER MOST SLOT DIRECTED TOWARDS THE INTERIOR OF THE BUILDING. THE REMAINING SHALL BE DIRECTED TOWARDS THE EXTERIOR UNLESS NOTED OTHERWISE.

TAG NAME	TYPE	MATERIAL	FACE SIZE (NOTE 1,2)		BORDER (NOTE 3)	SLOTS (NOTE 4)		PATTERN	VOLUME DAMPER	WEIGHT LBS		MANUFACTURER	MODEL	NOTES
			WIDTH	HEIGHT		WIDTH	QTY			DRY	OPERATING			
AP-#	BLANK ACCESS PANEL	[ALUMINUM] [STAINLESS STEEL]	WHITE	2'-0"	2'-0"	LAY-IN	0"	0"	No	0	0	TITUS	PAR	
EG-2	PERFORATED FACE	STEEL	WHITE	<varies>	<varies>	LAY-IN	0"	0"	No	0	0	TITUS	PAR	
EG-4	35 DEGREE DEFLECTION	[ALUMINUM] [STEEL]	WHITE	8"	6"	SURFACE MOUNT			No	0	0	TITUS	350	LONG BLADES
EG-5	35 DEGREE DEFLECTION	[ALUMINUM] [STEEL]	WHITE	8"	6"	SURFACE MOUNT			No	0	0	TITUS	350	LONG BLADES
LD-1		ALUMINUM	WHITE	<varies>	<varies>		0	Yes	0	0	0	TITUS	FL	
LD-#		ALUMINUM	WHITE	4 3/4"	<varies>		2"	0	Yes	0	0	TITUS	FL	
RT-#	[USER DEFINED]	[ALUMINUM] [STEEL]	[USER DEFINED]	8"	<varies>	[USER DEFINED]			No	0	0	TITUS	[USER DEFINED]	[USER DEFINED]
RD-1		ALUMINUM	WHITE	2 3/4"	<varies>		1"	0	Yes	0	0	TITUS	FL	
RG-1	35 DEGREE DEFLECTION	[ALUMINUM] [STEEL]	WHITE	<varies>	<varies>	SURFACE MOUNT			No	0	0	TITUS	350	LONG BLADES
RG-2	<varies>	<varies>	WHITE	<varies>	<varies>	SURFACE MOUNT			No	0	0	TITUS	<varies>	<varies>
RG-4	PERFORATED FACE	STEEL	WHITE	1'-0"	1'-0"	LAY-IN			No	0	0	TITUS	PAR	DUCTED RETURN
RG-#	PERFORATED FACE	STEEL	WHITE	2'-0"	2'-0"	LAY-IN			No	0	0	TITUS	PAR	DUCTED RETURN
SD-1		<varies>	WHITE	<varies>	<varies>				No	0	0			
SD-2			2'-0"	2'-0"					No	0	0			
SD-3			1'-0"	1'-0"					No	0	0			
SD-#			2'-0"	2'-0"					No	0	0			
SG-1	SINGLE DEFLECTION	[ALUMINUM] [STEEL]	WHITE	<varies>	<varies>	SURFACE MOUNT			Yes	0	0	HART AND COOLEY	821	LONG BLADES
SG-2	SINGLE DEFLECTION	[ALUMINUM] [STEEL]	WHITE	<varies>	<varies>	SURFACE MOUNT			No	0	0			
SD-#		ALUMINUM	WHITE	8"	6"	SURFACE MOUNT			No	0	0	TITUS	301	SHORT BLADES
SD-#		ALUMINUM	WHITE	6"	4"	SURFACE MOUNT			Yes	0	0	TITUS	301	SHORT BLADES

DEHUMIDIFICATION UNIT SCHEDULE

NOTES:
1.

TAG NAME	LOCATION	SUPPLY		OUTSIDE AIR		EVAPORATOR COIL		REHEAT COIL HEAT REJECTION (MBH)	ELECTRICAL			DIMENSIONS			WEIGHT LBS	MANUFACTURER	MODEL		
		SUPPLY CFM	SUPPLY ESP	OA CFM	OA ESP	SENSIBLE CAPACITY MBH	TOTAL CAPACITY MBH		MOISTURE REMOVAL CAPACITY (LBS/H)	VOLTS	PH	FLA	MCA	WIDTH	HEIGHT			DEPTH	OPERATING
DH-1 FLOOR MOUNTED	CELLAR	3400	2"	960	0.5"	50.7	84.5	31.3	105.6	208	3	37.4	44	3'-8"	5'-10"	5'-2"	1,400	SERESCO	6 TON COMP. DEHUMIDIFIER

CABINET HEATER SCHEDULE

NOTES:
1. COORDINATE COLOR SELECTION WITH ARCHITECT.

TAG	LOCATION		SERVICE	DIMENSIONS			CFM	FAN	COIL	COIL	ELECTRIC AL	MAXIMUM DIMENSIONS			WEIGHT LBS	MANUFACTURER	MODEL	NOTES		
	NAME			WIDTH	HEIGHT	DEPTH						DESIGN	DRIVE	FLUID TYPE					GPM	MBH
CH-1		BOILER		40"	12"	24"	450	CENTRIFUGAL	HOT WATER	3	18062	120	1	4'-0 3/4"	2'-1"	9 3/4"	105	MODINE	CW00450A	
CH-3		BOILER		40"	12"	24"	450	CENTRIFUGAL	HOT WATER	3	18062	120	1	4'-0 3/4"	2'-1"	9 3/4"	105	MODINE	CW00450A	
CH-4		BOILER		40"	12"	24"	450	CENTRIFUGAL	HOT WATER	3	18062	120	1	4'-0 3/4"	2'-1"	9 3/4"	105	MODINE	CW00450A	
CH-5		BOILER		40"	12"	24"	450	CENTRIFUGAL	HOT WATER	3	18062	120	1	4'-0 3/4"	2'-1"	9 3/4"	105	MODINE	CW00450A	
CH-6		BOILER		40"	12"	24"	450	CENTRIFUGAL	HOT WATER	3	18062	120	1	4'-0 3/4"	2'-1"	9 3/4"	105	MODINE	CW00450A	
CH-7		BOILER		40"	12"	24"	450	CENTRIFUGAL	HOT WATER	3	18062	120	1	4'-0 3/4"	2'-1"	9 3/4"	105	MODINE	CW00450A	
CH-8		BOILER		40"	12"	24"	450	CENTRIFUGAL	HOT WATER	3	18062	120	1	4'-0 3/4"	2'-1"	9 3/4"	105	MODINE	CW00450A	
CH-9		BOILER		40"	12"	24"	1,050	CENTRIFUGAL	HOT WATER	5.8	35582	120	1	5'-11 3/4"	2'-4"	1'-0"	185	MODINE	CW01050A	
CH-10		BOILER		40"	12"	24"	450	CENTRIFUGAL	HOT WATER	3	18062	120	1	4'-0 3/4"	2'-1"	9 3/4"	105	MODINE	CW00450A	
CH-11		BOILER		40"	12"	24"	450	CENTRIFUGAL	HOT WATER	3	18062	120	1	4'-0 3/4"	2'-1"	9 3/4"	105	MODINE	CW00450A	
CH-12		BOILER		40"	12"	24"	450	CENTRIFUGAL	HOT WATER	3	18062	120	1	4'-0 3/4"	2'-1"	9 3/4"	105	MODINE	CW00450A	

FAN SCHEDULE (EF, RF, SF, etc.)

NOTES:																
TAG NAME	LOCATION	SERVICE	CFM	TOTAL P. IN. WC	DRIVE	RPM	WHEEL DIAMETER	ELECTRICAL		DIMENSIONS				WEIGHT LBS	MANUFACTURER	MODEL
			DESIGN	S.P. IN. WC				WHEEL MOTOR	VOLTS	PH	WIDTH	HEIGHT	DEPTH	OPERATING		
DWE-1	IL ROOF	DISHWASHER EXHAUST	0	0	TBD	0	0"	TBD	0	1	0"	0"	0"	0"	TBD	TBD
GK-1	CELLAR	CO EXHAUST	10,800	0.5	BELT	630	2'-6"	3	208	3	4'-6"	7'-6"	4'-6"	1,511	COOK	GMX
GK-2	CELLAR	CO EXHAUST	10,800	0.5	BELT	630	2'-6"	3	208	3	4'-6"	7'-6"	4'-6"	1,511	COOK	GMX
GK-3	CELLAR	CO EXHAUST	10,800	0.5	BELT	267	5'-10"	3	208	3	5'-6"	6'-2"	5'-6"	2,537	COOK	GMX
GK-4	CELLAR	POOL STORAGE EXHAUST	0	0	TBD	0	0"	TBD	0	1	0"	0"	0"	0	COOK	ACE-DVF
GK-5	CELLAR	DOG SPA/SALON	0	0	TBD	0	0"	TBD	0	1	0"	0"	0"	0	COOK	ACE-DVF
GK-6	CELLAR	TRASH ROOM EXHAUST	0	0	TBD	0	0"	TBD	0	1	0"	0"	0"	0	COOK	ACE-DVF
GK-7	CELLAR	POOL STORAGE EXHAUST	300	0.32	DIRECT	1800	0"	TBD	0	115	1	0"	0"	0	GREENHECK	SG-90
GK-8	CELLAR	SPA	450	0.3	DIRECT	1800	0"	TBD	0	115	1	0"	0"	0	GREENHECK	SG-90
KE-1	IL ROOF	KITCHEN HOOD #07 EXHAUST	0	0	TBD	0	0"	TBD	0	1	0"	0"	0"	0	TBD	TBD
KE-2	IL ROOF	KITCHEN HOOD #25 EXHAUST	0	0	TBD	0	0"	TBD	0	1	0"	0"	0"	0	TBD	TBD
ROE-1	IL ROOF	PIZZA OVEN EXHAUST	0	0	TBD	0	0"	TBD	0	1	0"	0"	0"	0	TBD	TBD
RF-2	IL ROOF	RTU-2	6,500	1.25	CENTRIFUGAL	1155	2'-3"	3	460	3	3'-6"	4'-6"	3'-0"	553	COOK	CPS
RF-3	IL ROOF	RTU-3	6,940	1.25	CENTRIFUGAL	1394	2'-3"	3	460	3	3'-6"	4'-1"	3'-0"	529	COOK	CPS
RF-4	IL ROOF	RTU-4	6,700	1.25	CENTRIFUGAL	1453	2'-3"	3	460	3	3'-6"	4'-6"	3'-0"	523	COOK	CPS
TRE-1	IL ROOF	TRASH ROOM EXHAUST	750	0.35	DIRECT	912	1'-1"	14	115	1	1'-7"	3'-0"	1'-7"	59	GREENHECK	G-120-G
TRE-2	IL ROOF	TRASH ROOM EXHAUST	750	0.35	DIRECT	912	1'-1"	14	115	1	1'-7"	3'-0"	1'-7"	59	GREENHECK	G-120-G
TX-1	1ST FLOOR	1ST BATHROOM EXHAUST	150	1.5	CENTRIFUGAL	1394	1'-8"	12	115	1	1'-8"	2'-4"	1'-8"	72	COOK	ACE-DVF
TX-2	1ST FLOOR	1ST EAST BATHROOM EXHAUST	150	1.5	CENTRIFUGAL	1394	1'-8"	12	115	1	1'-8"	2'-4"	1'-8"	72	COOK	ACE-DVF
TX-3	1ST FLOOR	IL GARAGE BATHROOM EXHAUST	250	1	INLINE	1702	1'-8"	8	115	1	1'-8"	2'-4"	1'-8"	78	COOK	ACE-DVF
TX-4	1ST FLOOR	IL DINING ROOM BATHROOM EXHAUST	250	1	INLINE	1725	1'-8"	11	115	1	1'-8"	2'-4"	1'-8"	68	COOK	ACE-DVF
TX-5	1ST FLOOR	AL 1ST FLOOR BATHROOM EXHAUST	250	1	INLINE	1725	1'-8"	14	115	1	1'-8"	2'-4"	1'-8"	63	COOK	ACE-DVF
TX-6	1ST FLOOR	AL 2ND FLOOR BATHROOM EXHAUST	250	1	INLINE	1725	1'-8"	13	115	1	1'-8"	2'-4"	1'-8"	68	COOK	ACE-DVF
TX-7	2ND FLOOR	AL 3RD FLOOR BATHROOM EXHAUST	250	1	INLINE	1725	1'-8"	14	115	1	1'-8"	2'-4"	1'-8"	68	COOK	ACE-DVF
TX-8	2ND FLOOR	AL BASEMENT BATHROOM EXHAUST	75	1	TBD	0	0"	TBD	0	1	0"	0"	0"	0	COOK	ACE-DVF
TX-9	CELLAR		450	0.3	DIRECT	1800	0"	TBD	0	115	1	0"	0"	0	GREENHECK	SG-90-G
TX-10	CELLAR		450	0.3	DIRECT	1800	0"	TBD	0	115	1	0"	0"	0	GREENHECK	SG-90-G
TX-A	IL AL	UNIT RESTROOMS	75	0.25	DIRECT	900	0"	0.04	120	1	1'-3 1/2"	1'-11 1/4"	9"	12	COOK	GC-146